
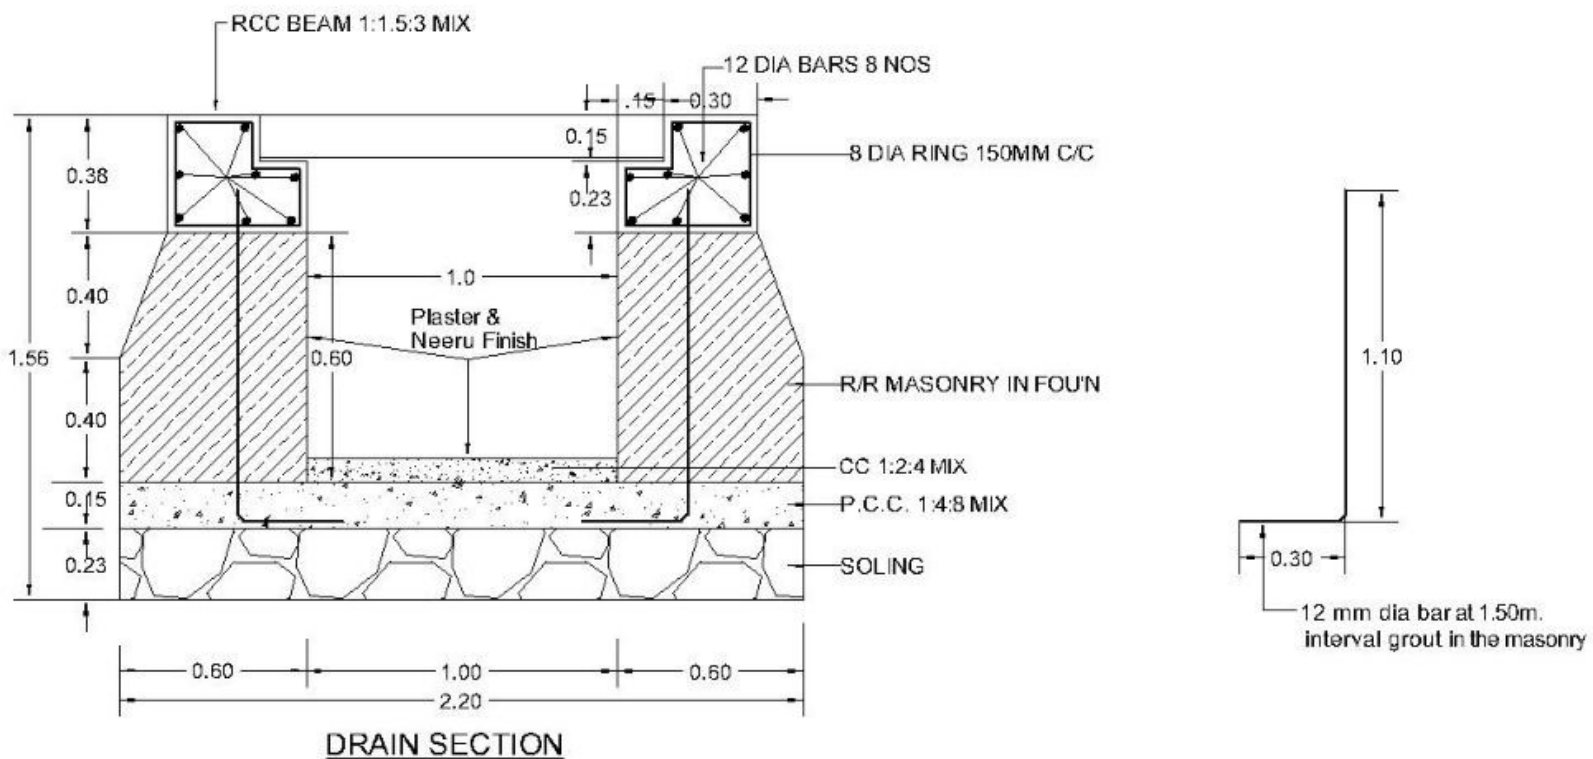


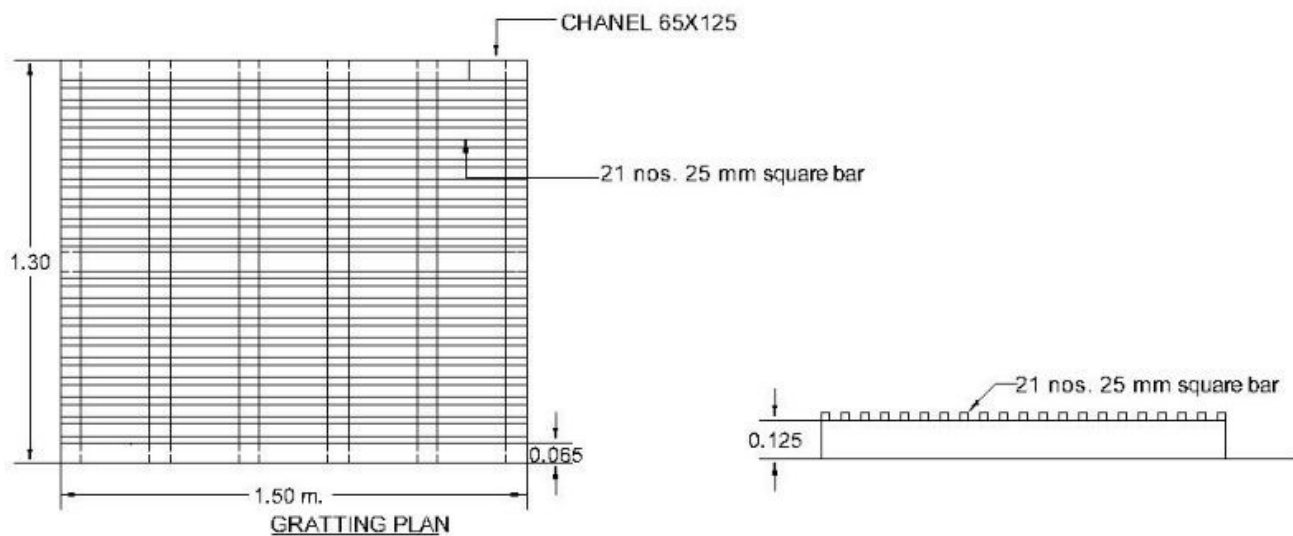

DRAIN SECTION