

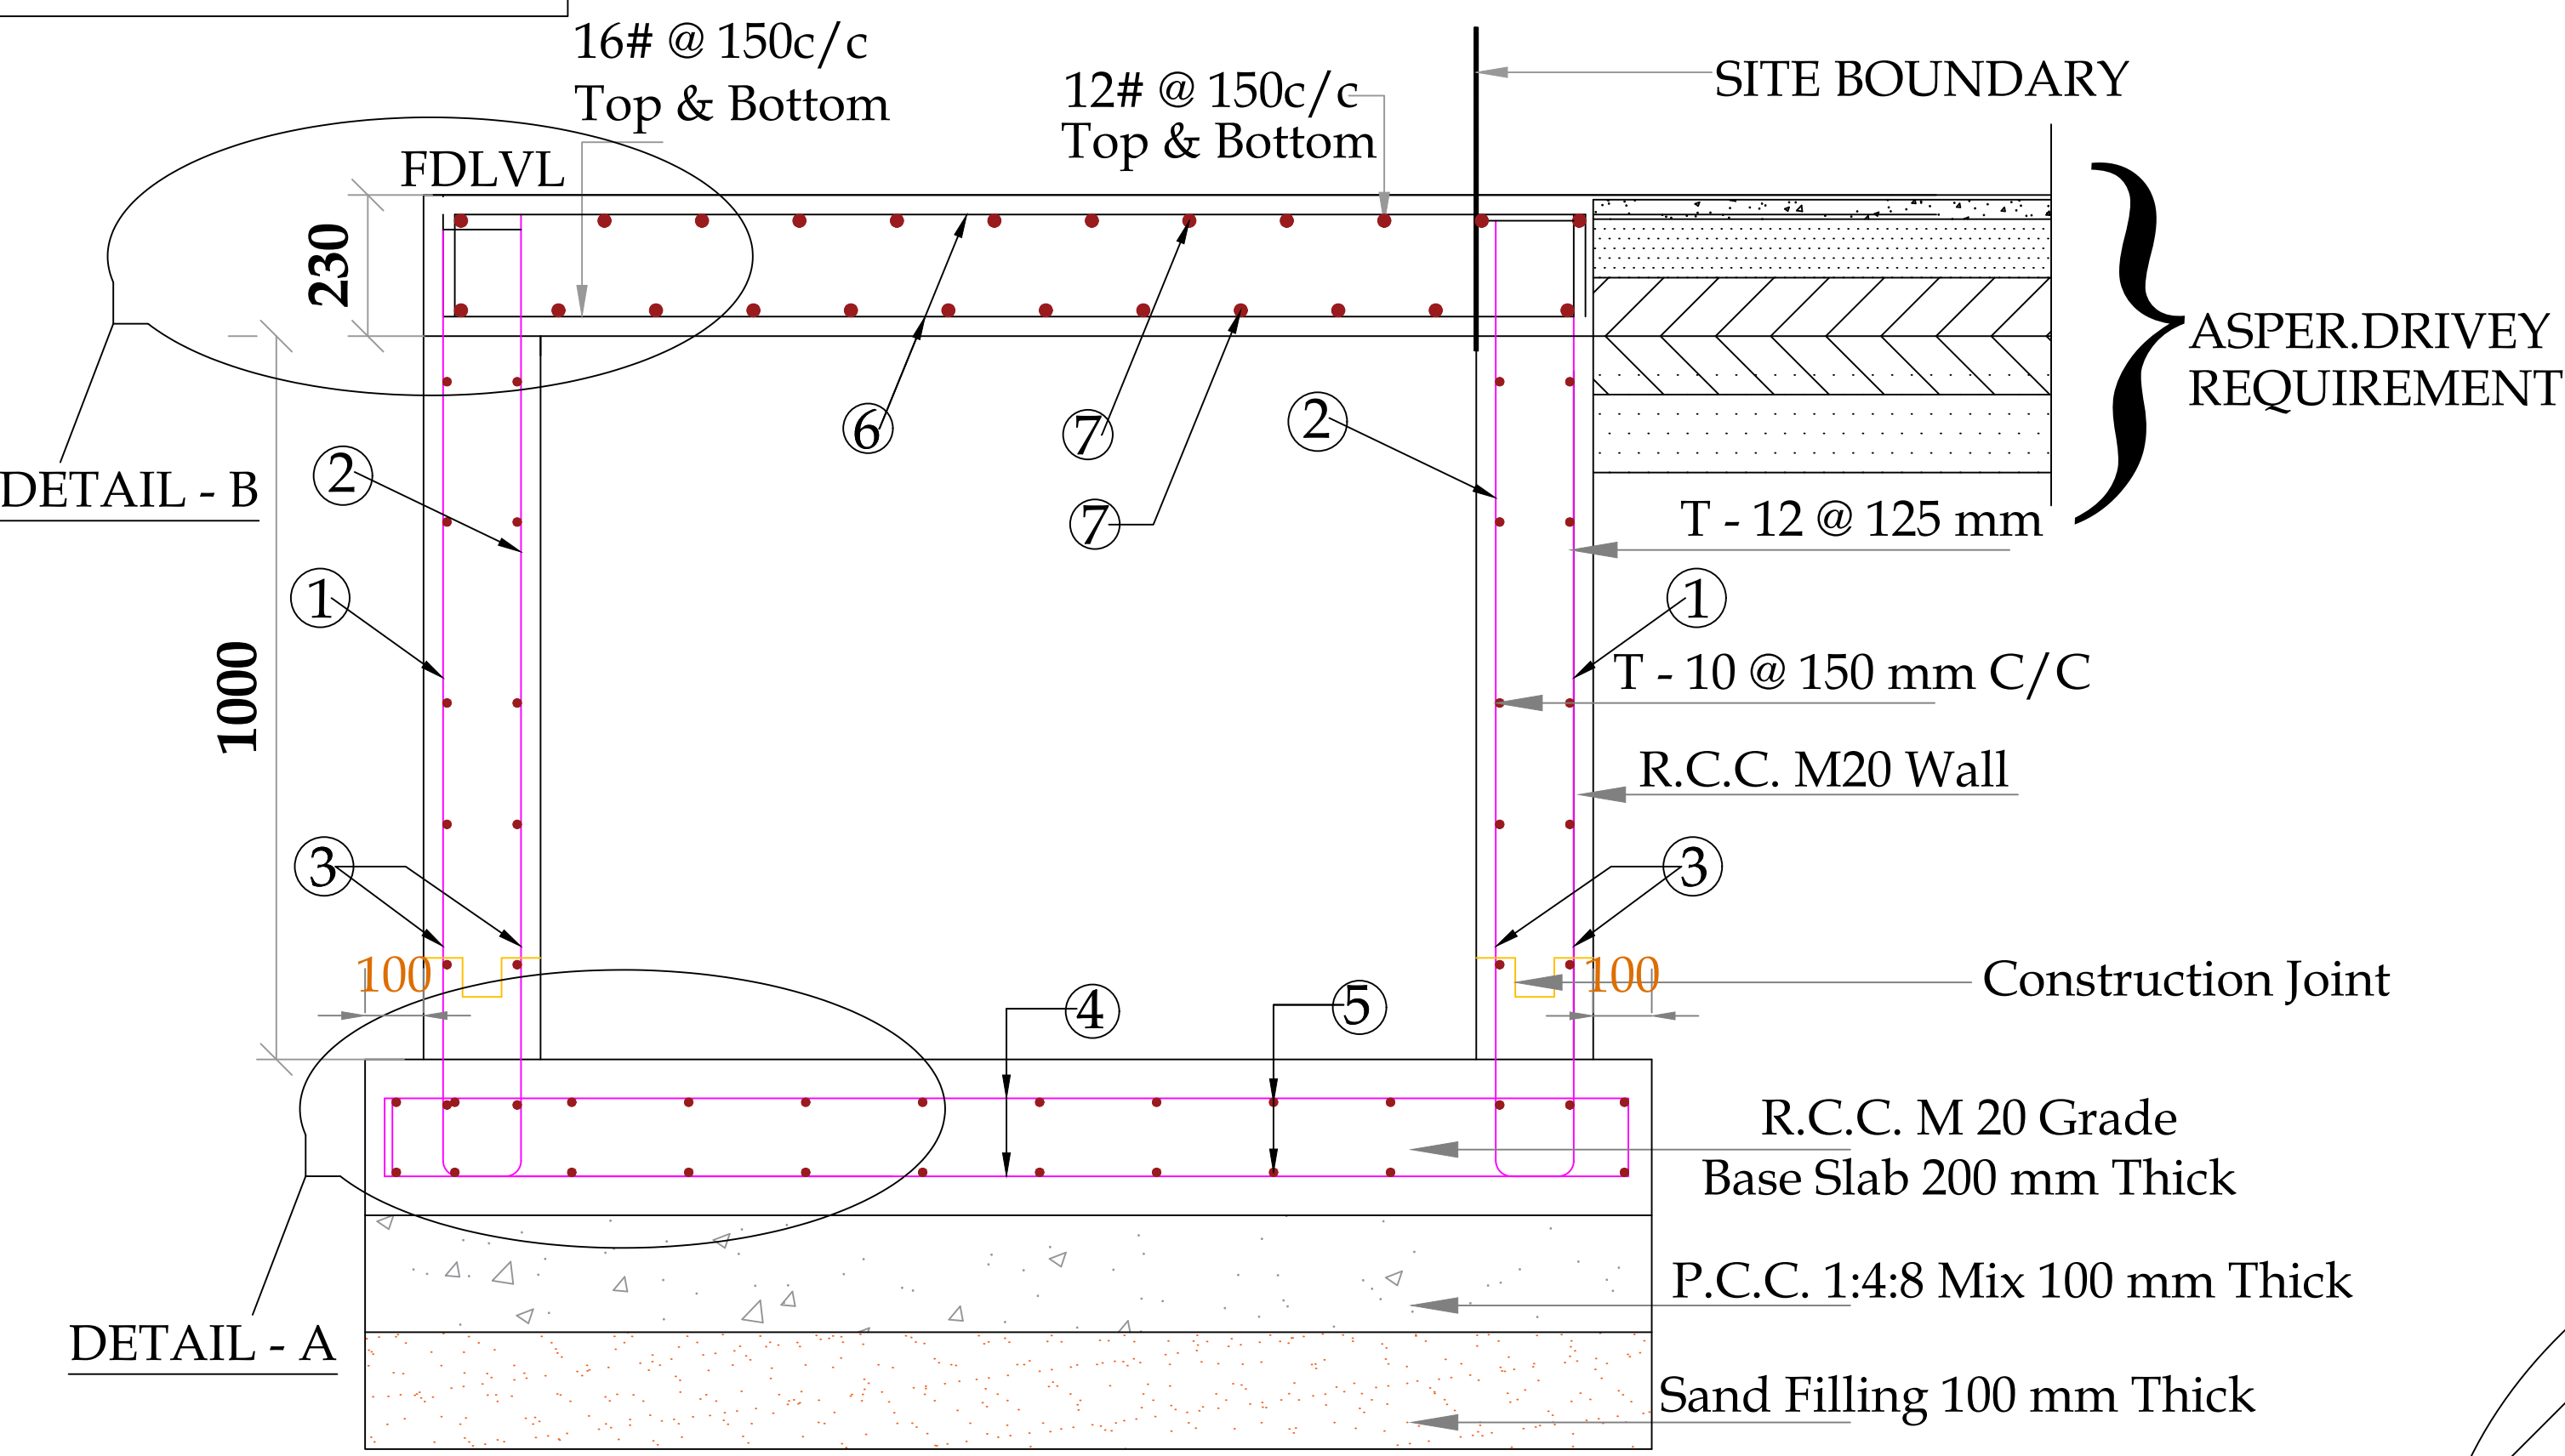


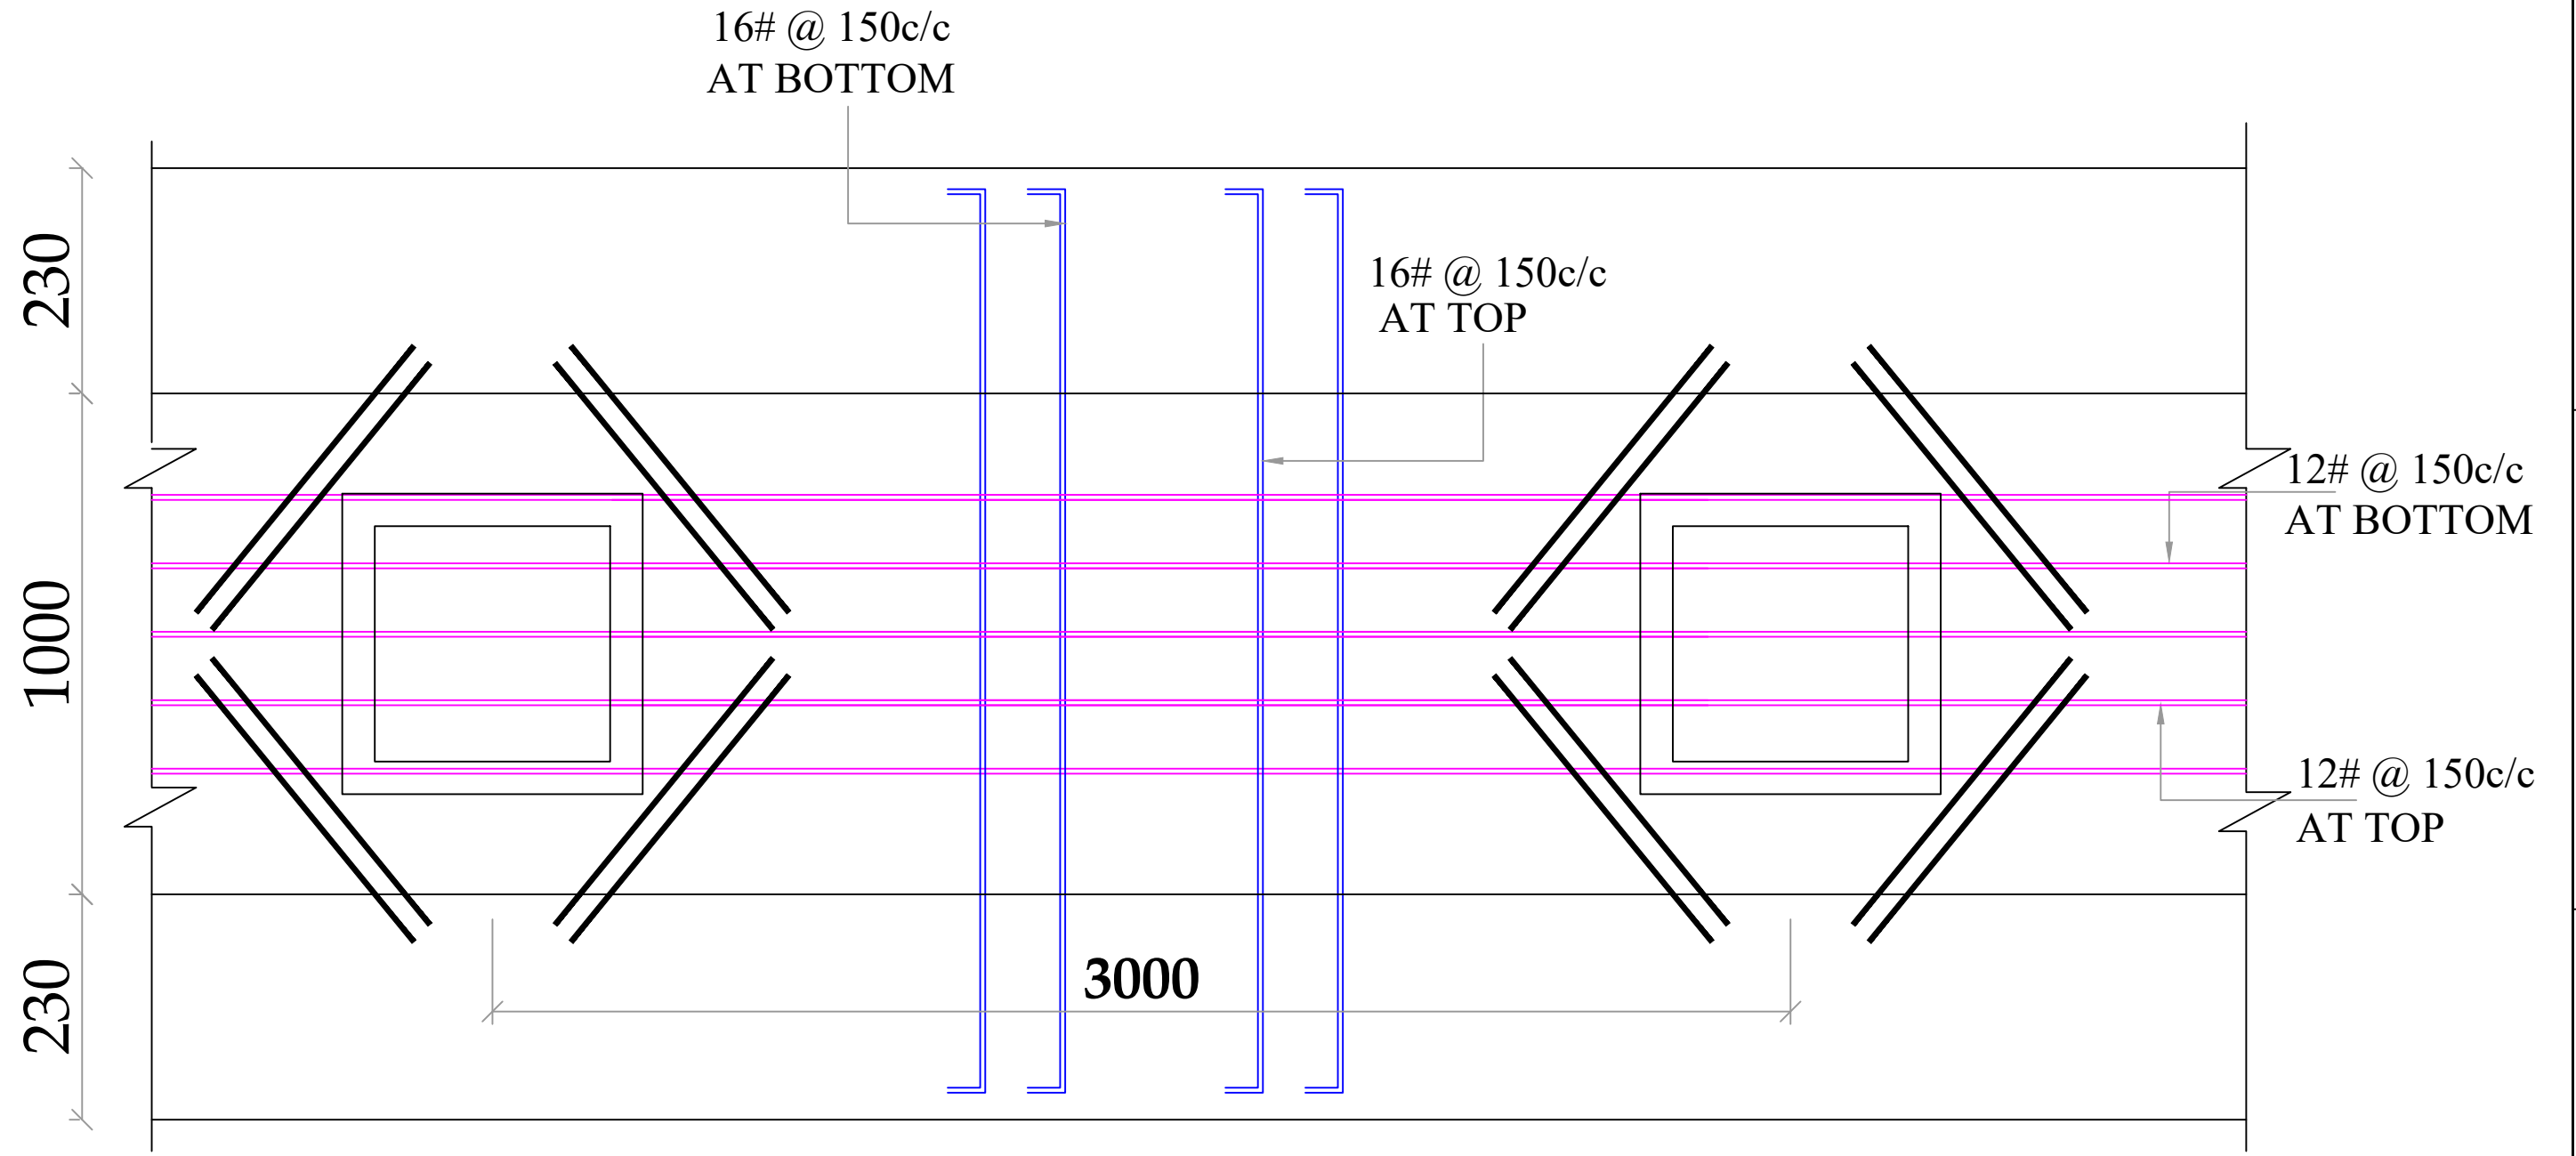



SECTION  
NOT TO SCALE

TABLE SHOWING SALIENT DIMENSIONS:

| S.NO. | SHAPE | a<br>mm | b<br>mm | c<br>mm |
|-------|-------|---------|---------|---------|
| 1     |       | 180     | L       | 500     |
| 2     |       | 150     | L       | 180     |
| 3     |       | L       |         |         |
| 4     |       | 100     | 1150    | 100     |
| 5     |       | Length  |         |         |
| 6     |       | 100     | 1150    | 100     |
| 7     |       | Length  |         |         |

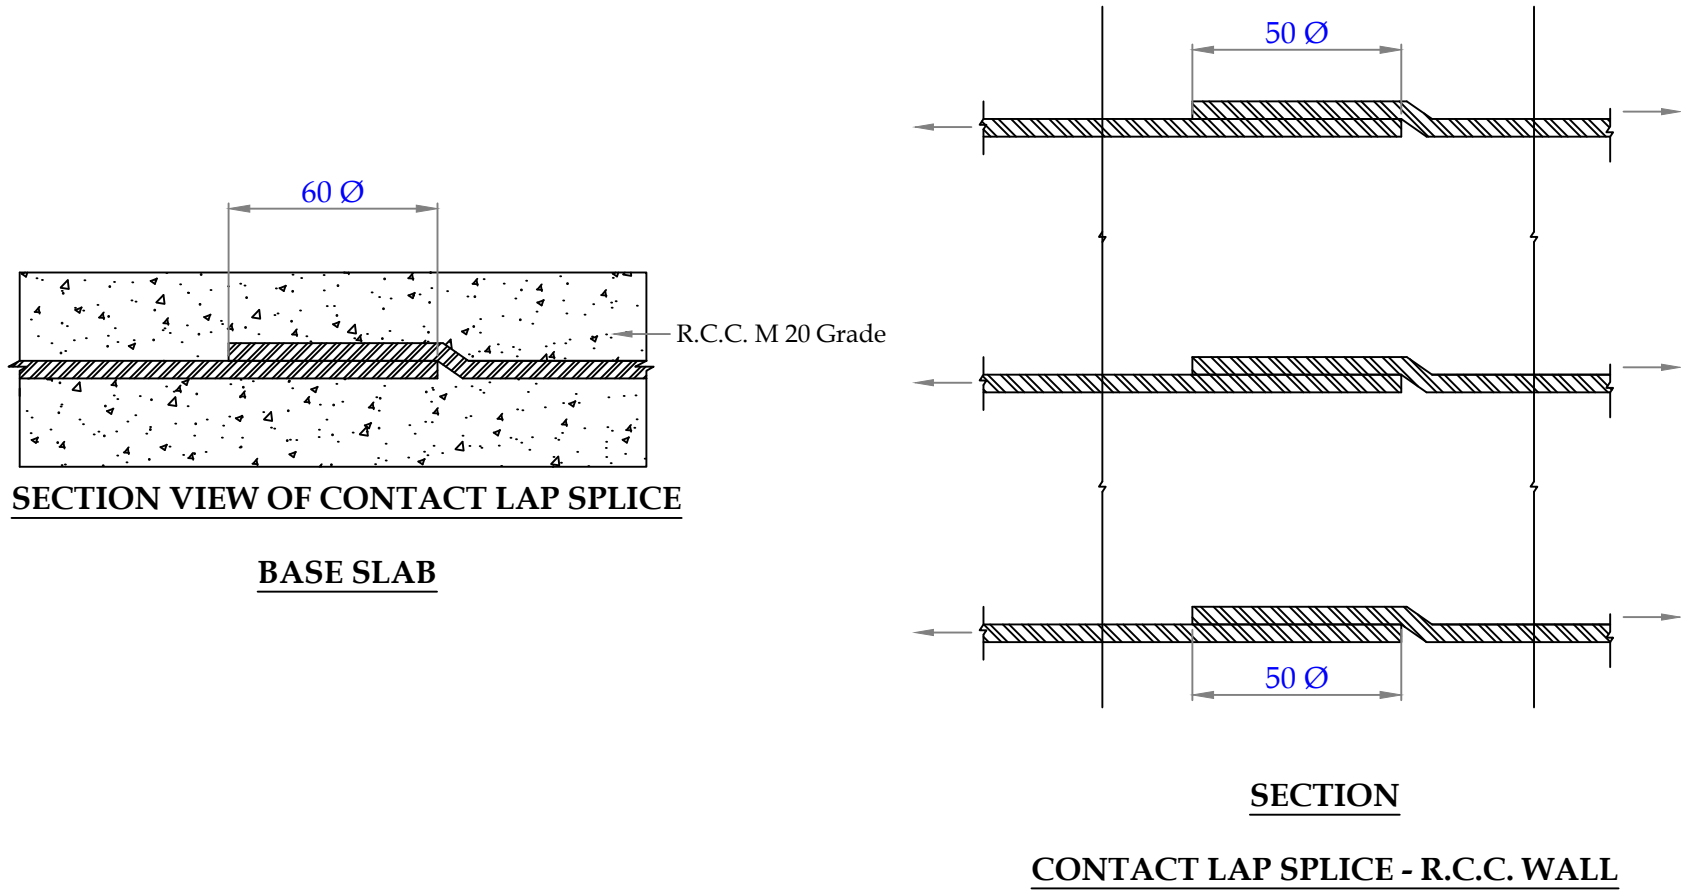

R.C.C CULVERT SLAB DETAIL

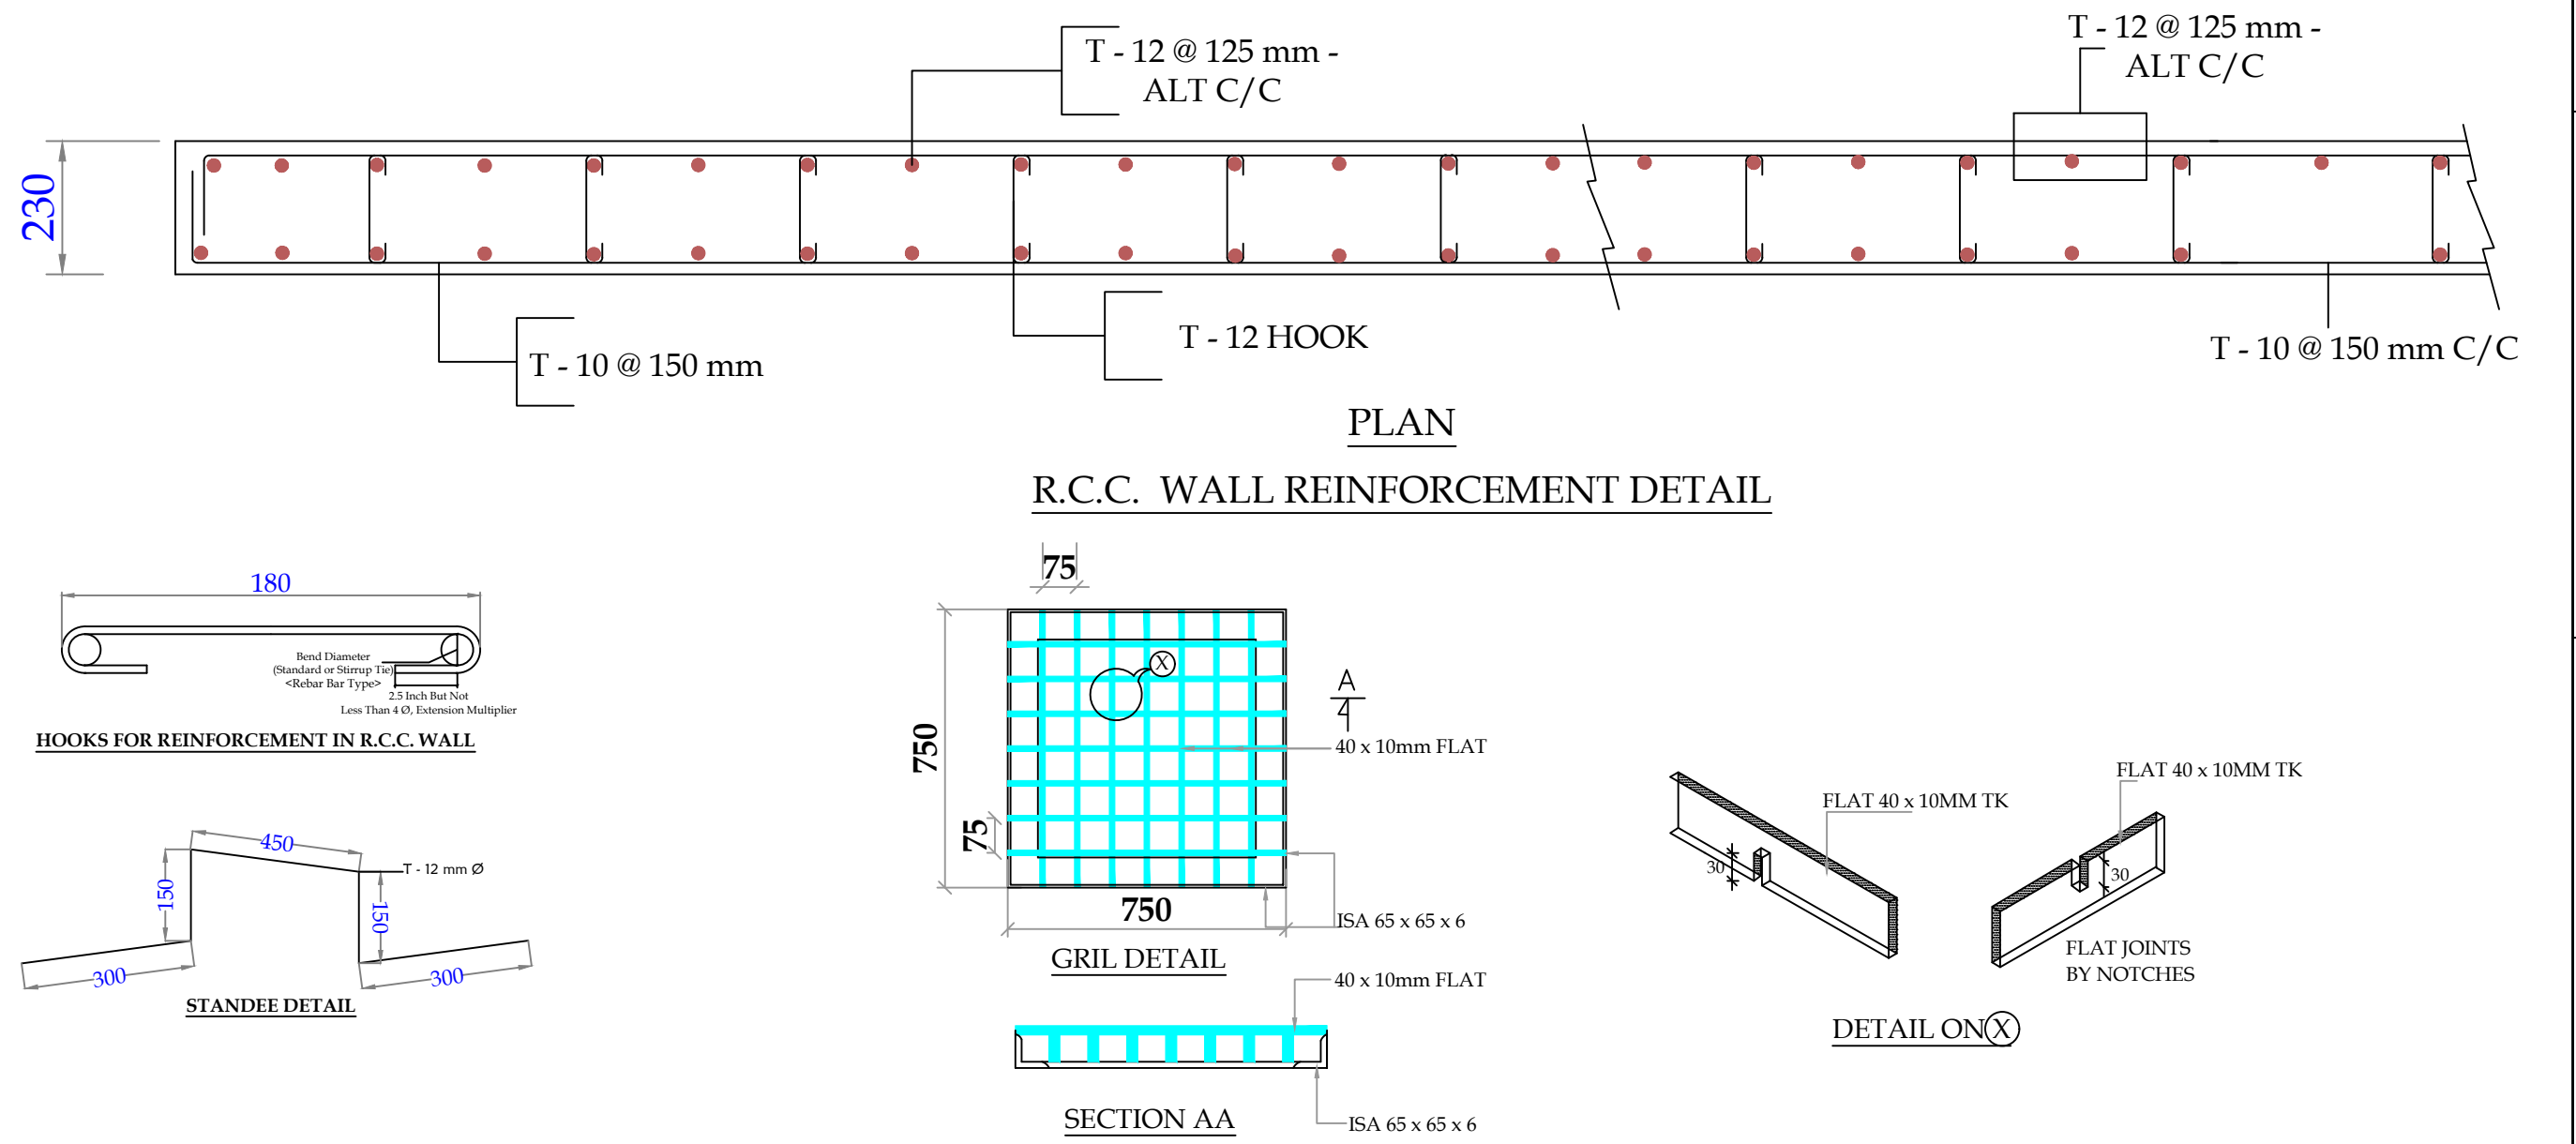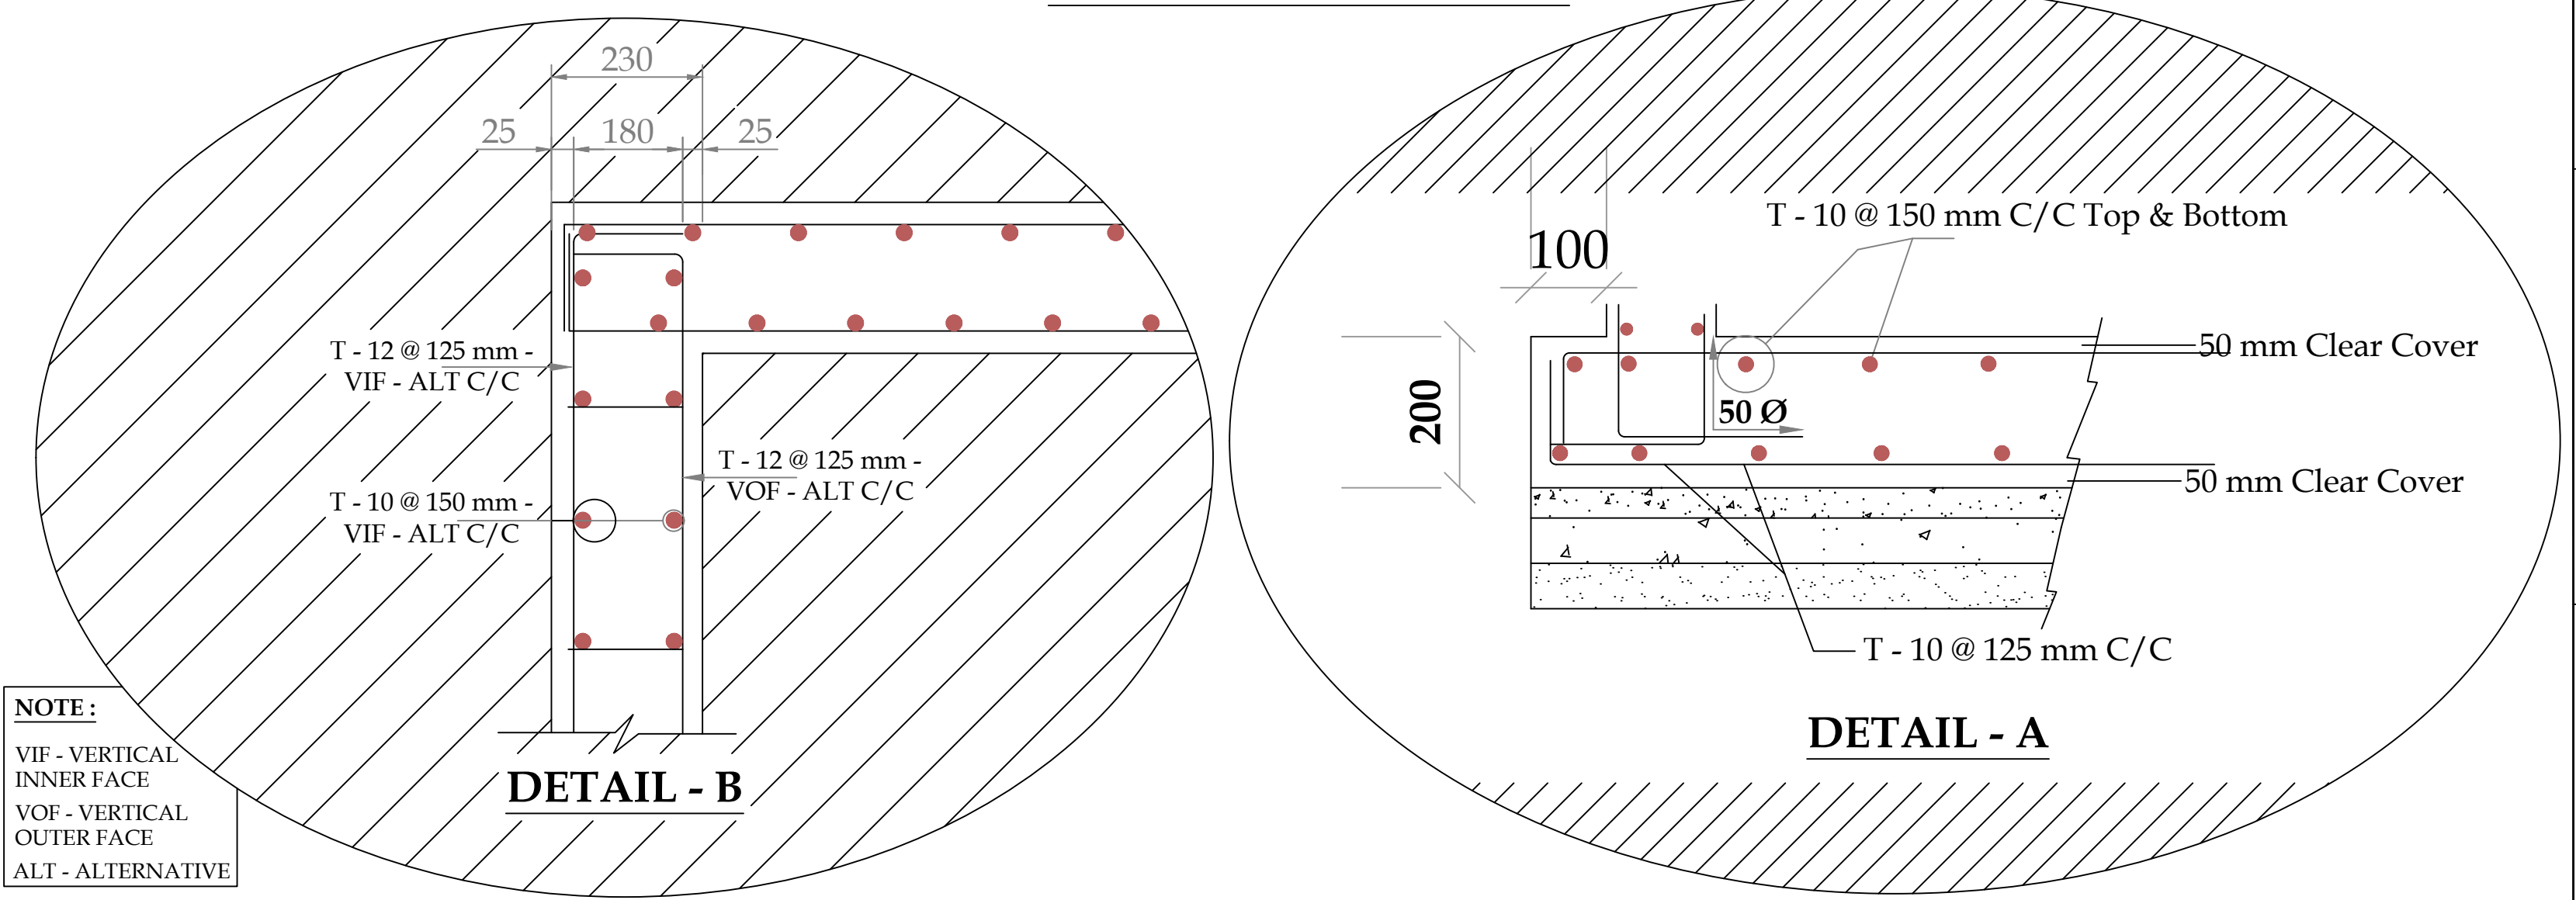

CONSULTANT :-


**Landscape Designer**  
architects,engineers & interior designers  
33, Padhuvai Nagar, Chinthamani,  
Tiruchirappalli - 620 002 , Tamil Nadu.  
phone : 99521 95922 , 0431 - 2705521.  
Email : thresejai@gmail.com, landscapedesignerr@yahoo.com

|                | NAME           | REFERENCE:      |                                     |         |            |                           |            |  |
|----------------|----------------|-----------------|-------------------------------------|---------|------------|---------------------------|------------|--|
| DRAWN          | M.GOPI         | PROPOSED        | <input checked="" type="checkbox"/> |         |            |                           |            |  |
| CHECKED        | JJEYA CHANDRAN | EXISTING        | <input type="checkbox"/>            |         |            |                           |            |  |
| APPROVED       |                | TO BE REMOVED   | <input type="checkbox"/>            | 00      | 20/01/2022 | Released For Construction |            |  |
| PREFER TO PLOT | A3             | FUTURE INCLUDED | <input type="checkbox"/>            | REVISED | DATE       | DESCRIPTION               | REVISED BY |  |



**BHARAT PETROLEUM CORPORATION LIMITED**  
பாரத பெட்ரோலியம் கார்ப்பரேஷன் லிமிடெட்  
भारत पेट्रोनिम कॉर्पोरेशन लिमिटेड  
TRICHY TERRITORY

Caution : The information on this document is the property of Bharat Petroleum Corporation Limited.It must not be used directly or indirectly in anyway detrimental to the interest of the company.

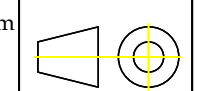

SCALE : 1:100

Project Name :  
**THE PROPOSED NEW RETAIL OUTLET IN S.NO. - 98/3C, 98/4A, 98/4B, 98/5A1, 98/5C, 98/5E, MUNIYANTHANGAL VILLAGE , POLUR TALUK, TIRUVANNAMALAI DISTRICT - 606 903. TAMIL NADU .**

Title : **RCC CULVERT DETAILS**

DRAWING NO :002/LD/JJ/MG/BPCL/20/01/2022 SHEET NO : 01 of 02