


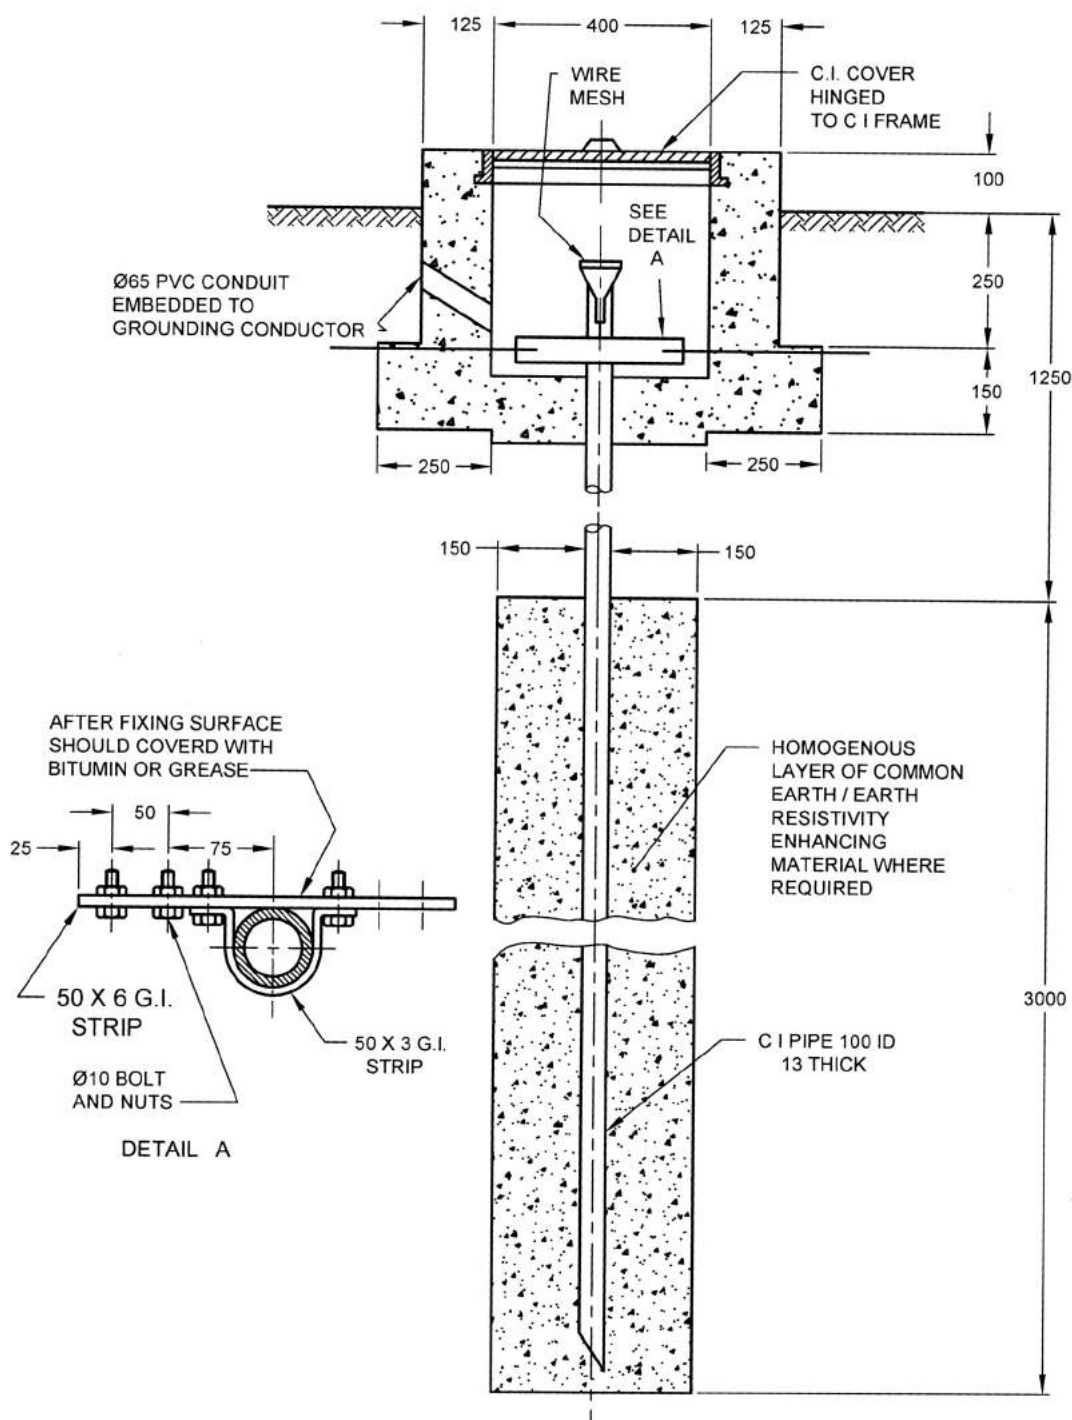

NOTE — After laying the earth from the earth bus to the electrode through the PVC conduits at the pit entry conduits should be sealed with bitumen compound.

All dimensions in millimetres.

FIG. 25 TYPICAL ARRANGEMENT OF PIPE ELECTRODE

