



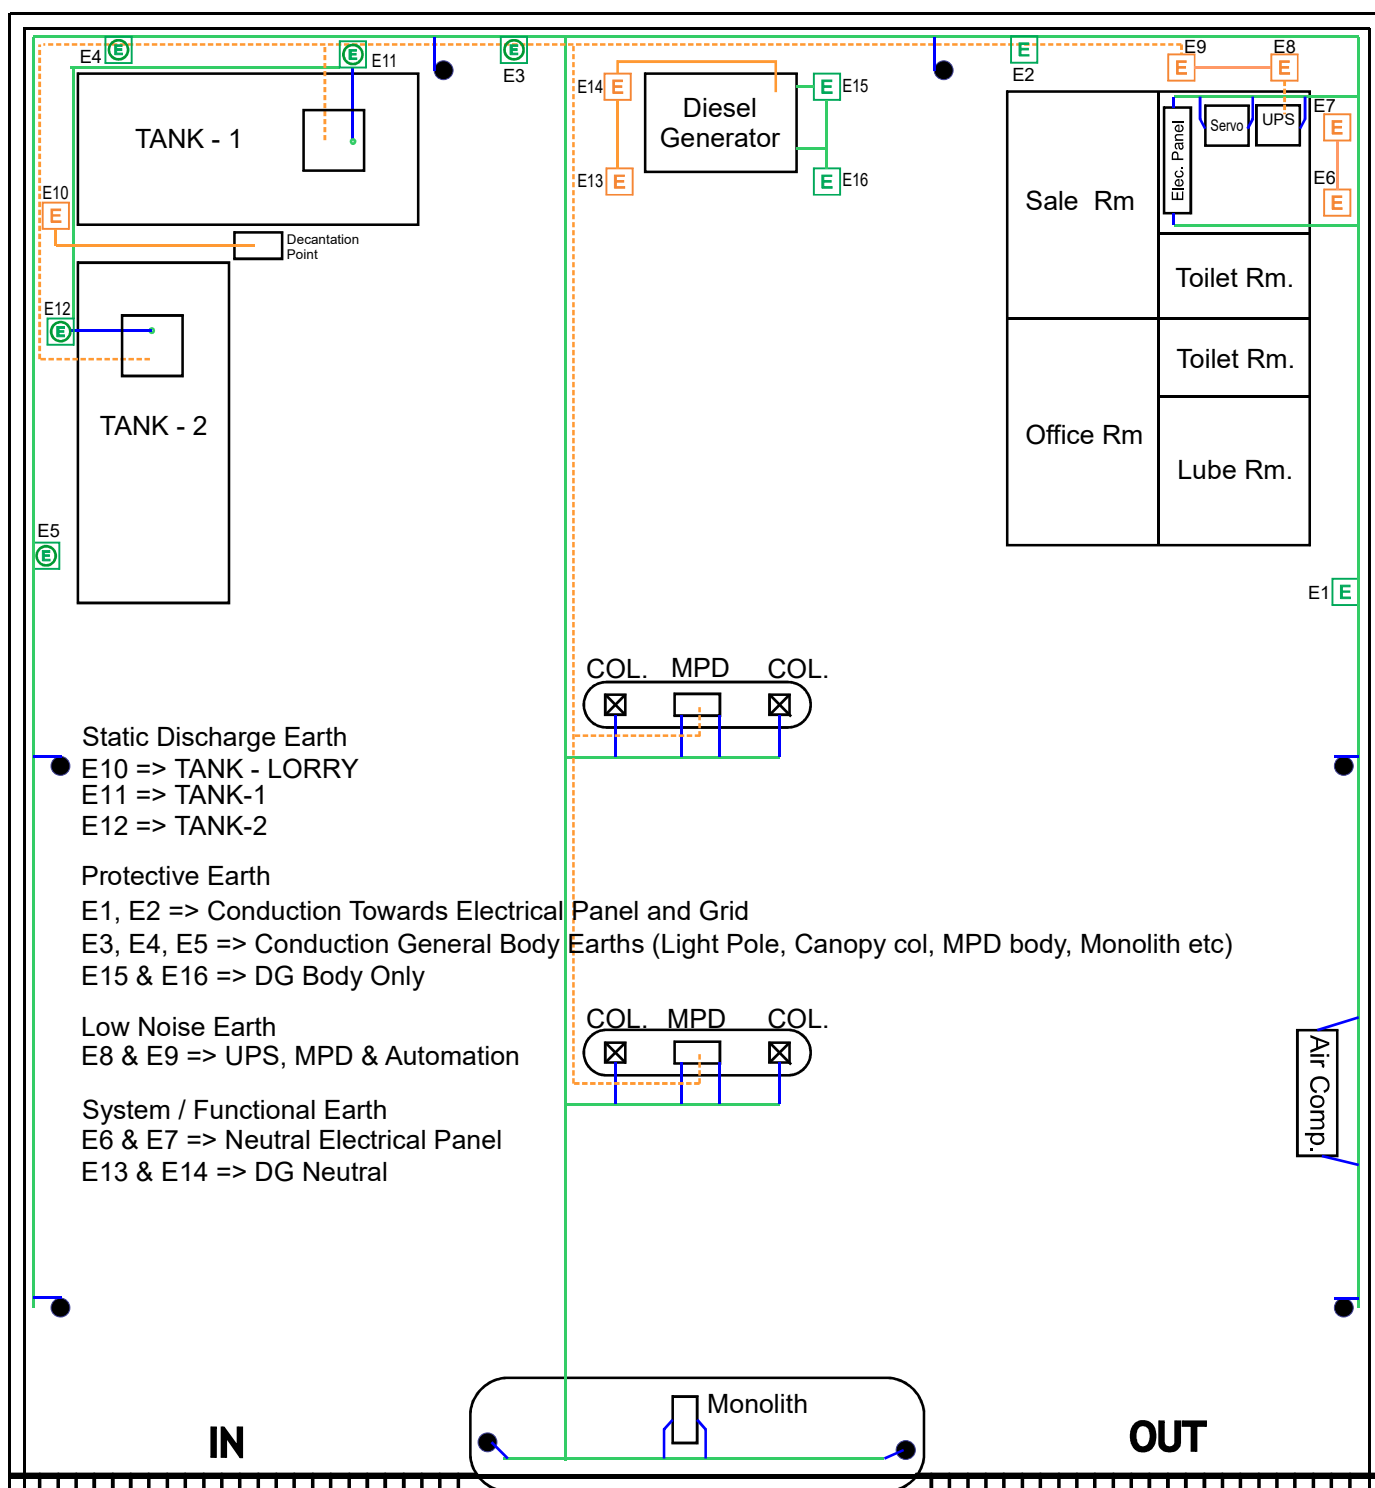

EARTHING LAYOUT PLAN OF A TYPICAL RETAIL OUTLET

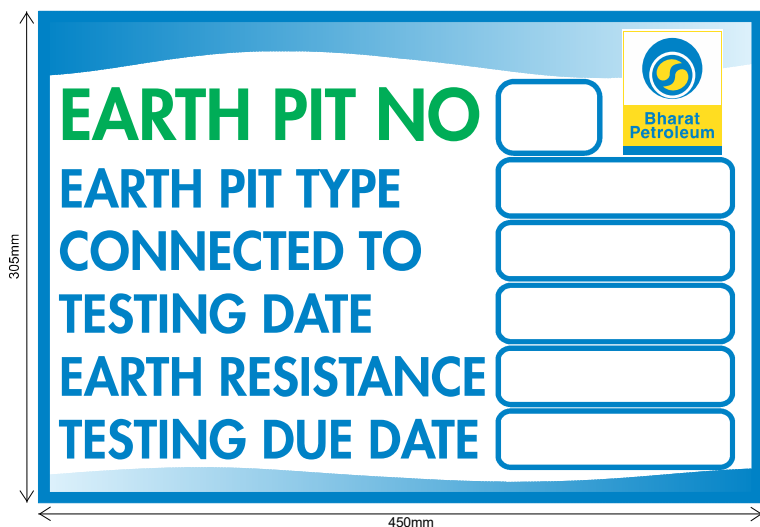


VINYL PASTED SUNBOARD - 305 x 450mm

Dark Green - CMYK combination: C-90 & Y-100
Dark Green - RGB combination: R-0, G-153, B-61

Blue - CMYK combination : C-100 & M-40
Blue - RGB combination: R-0, G-103, B-172

Yellow - CMYK combination : M-10 & Y-100
Yellow - RGB combination: R-252, G-219, B-0

TEXT in BLUE : Font - Futura HV BT; size 89
TEXT in GREEN : Font - Futura HV BT; size 120

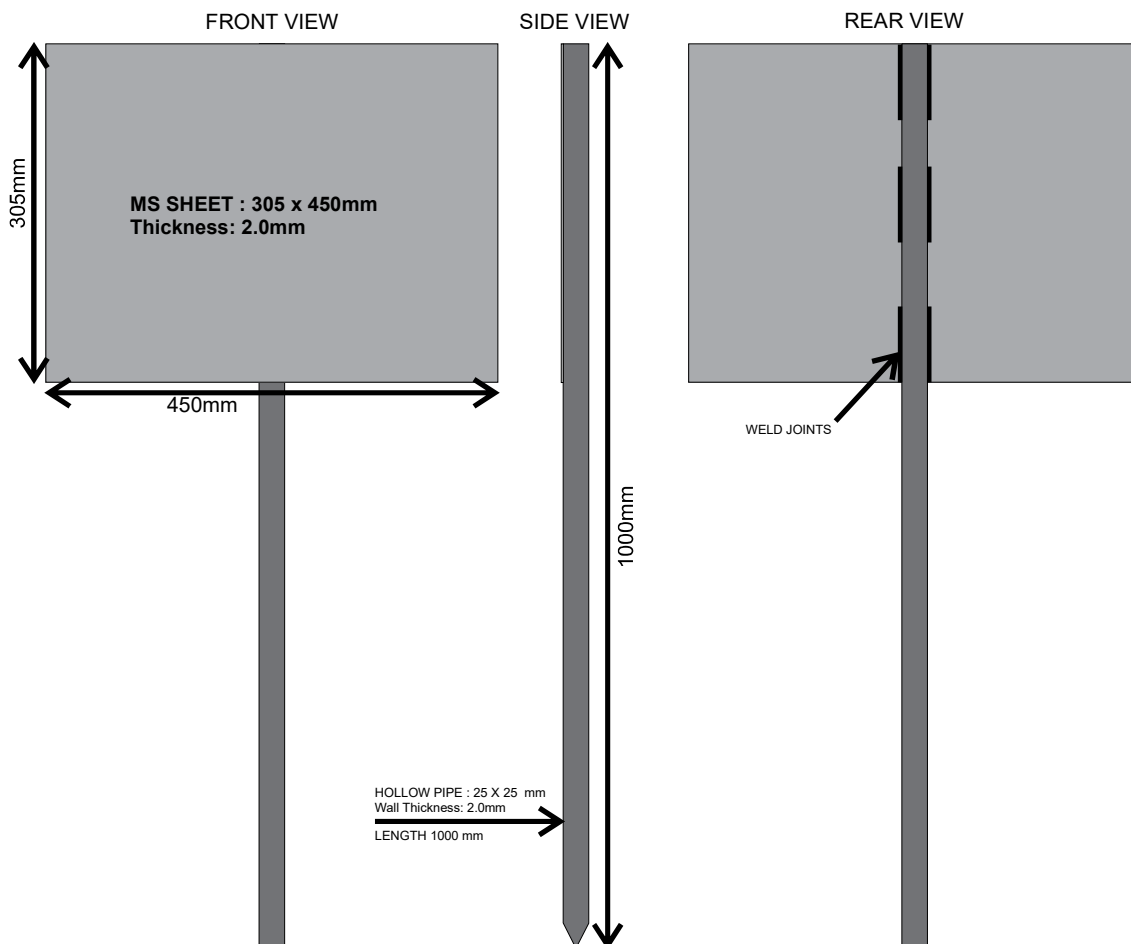

TITLE:	TYPICAL EARTHING LABEL			ALL DIMENSIONS ARE IN MM TOLERANCE +/- 5% ON FAB ITEM		
DRG No:	SES/EP/LABEL					
REV	DATE	DESCRIPTION		SCALE: NTS	DESIGNED	PK
00	10.04.2024			☒ APPROVAL ☐ AS BUILT ☐ CONSTN	APPROVED PROJECTION	RKN 