


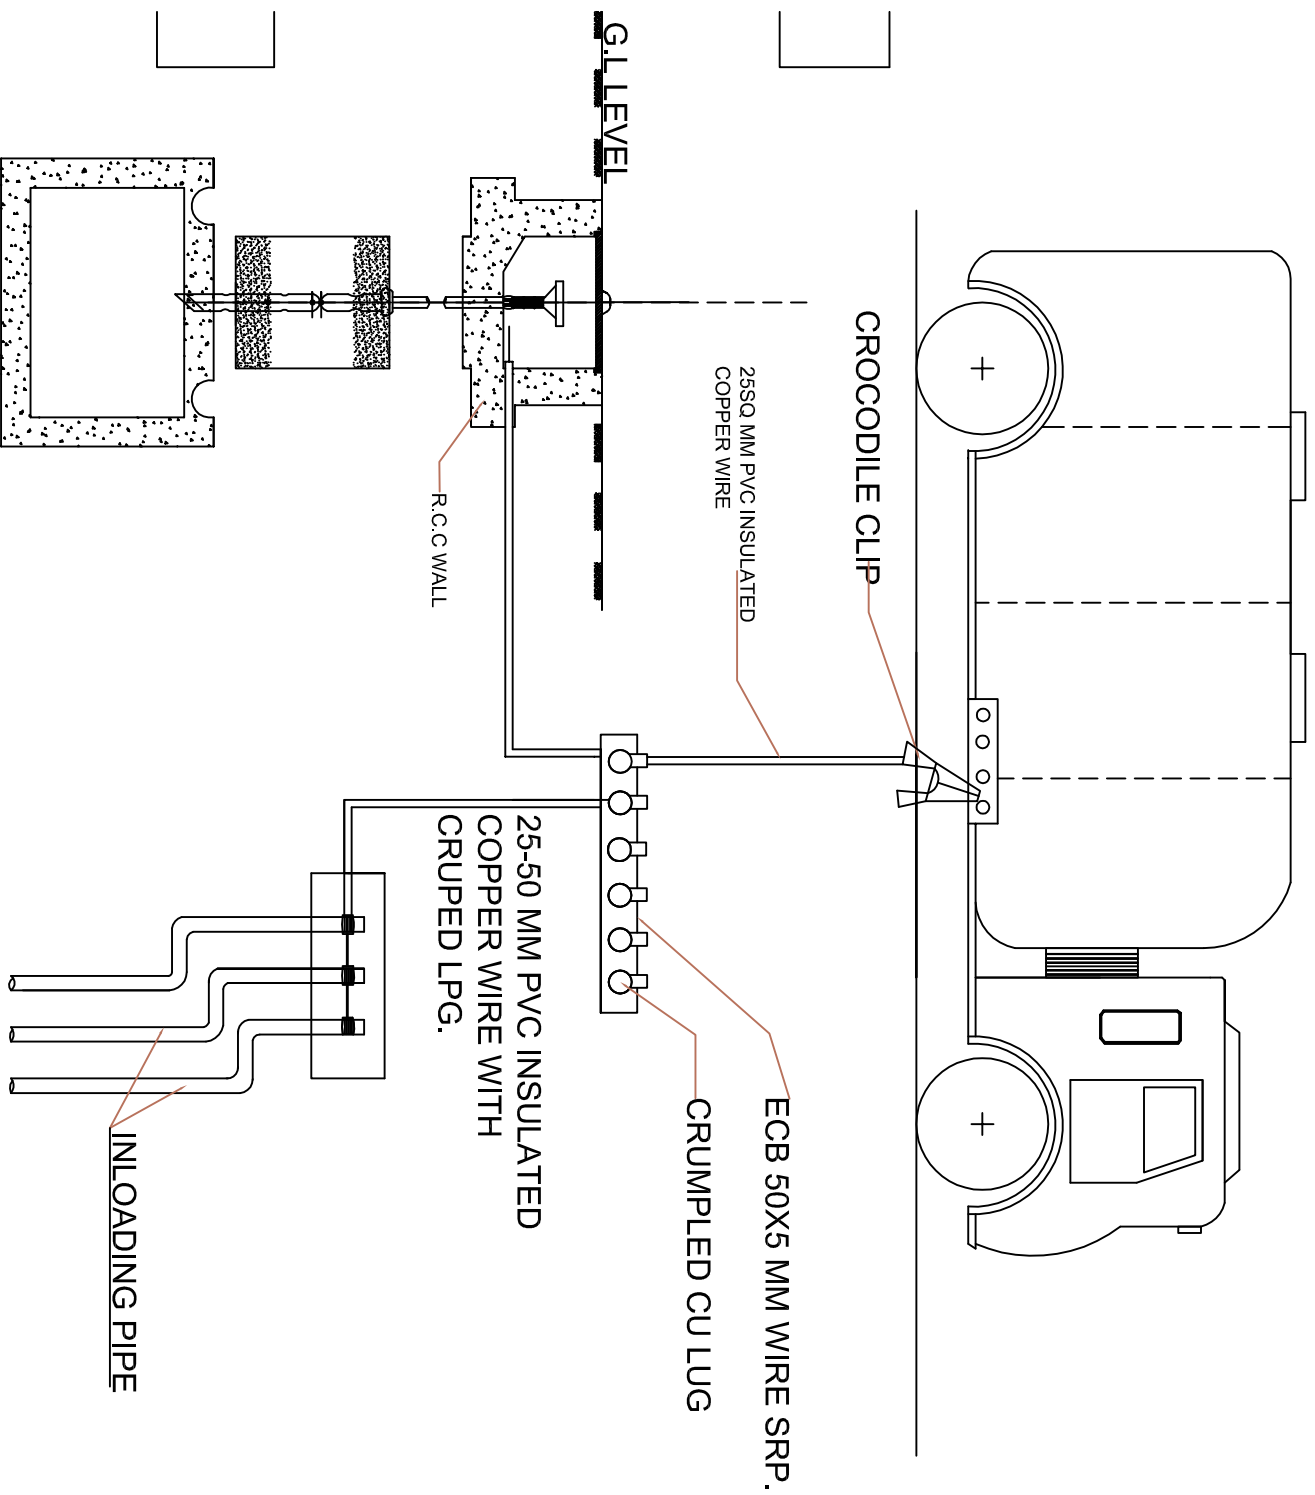

PIPE EARTH PIT -1

DRG NO : BP/RET/TL/1

EARTHING FOR UNLOADING TRUCK