


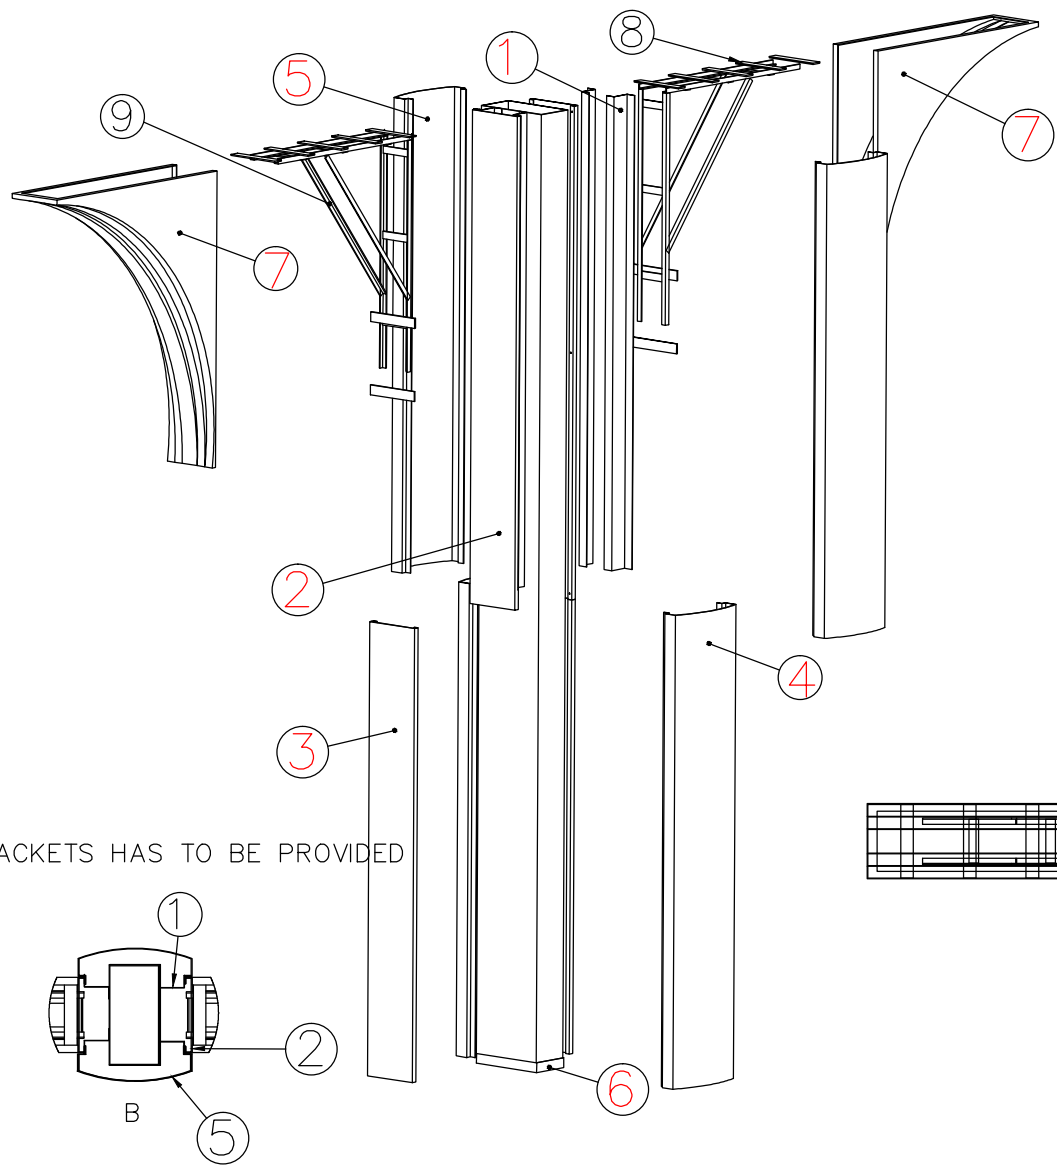

9	STRUCTURE FOR ARCH	2
8	SLIDING CHANNEL FOR ARCH	2
7	ARCH FOR BPCL	2
6	BOTTOM COVER FOR CLADDING	1
5	CLADDING CURVED 2500mm	2
4	CLADDING CURVED 1000mm	2
3	CLADDING STRAIGHT 1000mm	2
2	CLADDING STRAIGHT 2500mm	2
1	Z BRACKET	8
SR.NO	NAME OF COMPONENT	QTY

Z BRACKETS HAS TO BE PROVIDED

ORIENTATION OF THE CLADDING IS CHANGED DEPEND UPON THE SITE

 BHARAT PETROLEUM CORPORATION LTD.					
TITLE :					
COLUMN CLADDING FOR BPCL(5M)				DATE	DRAWING NO.
NUMBERS CROSSED OUT ARE SUPERSEDED DRAWINGS					
SCALE : 1:22	DRAWN:	CHECKED	SHEET NO.	DRAWING NO :	
DATE : 23/5/18	GM.RE		1 of 11	BP.RVI.CA-A01	

REVISIONS
