SR.NO	DESCRIPTION	QTY.
11	PILLER ARCH LIGHT ON SPREADER & SPREADER EXTENSION	2
10	PILLER ARCH LIGHT ON SPREADER	1
9	STRUCTURE FOR ARCH	2
8	SLIDDING CHANNEL FOR ARCH	2
7	ARCH FOR BPCL	2
6	BOTTOM COVER FOR CLADDING	1
5	CLADDING CURVED 2500mm	4
4	CLADDING SRAIGHT 250MM	1
3	CLADDING SRAIGHT 1000MM	1
2	CLADDING STRAIGHT 2500mm	2
1	ANGLE	8

SR.NO	DESCRIPTION	QTY.
10	PILLER ARCH LIGHT	1
9	STRUCTURE FOR ARCH	4
8	SLIDDING CHANNEL FOR ARCH	4
7	ARCH FOR BPCL	4
6	BOTTOM COVER FOR CLADDING	2
5	CLADDING CURVED 2500mm	8
4	CLADDING SRAIGHT 250MM	2
3	CLADDING SRAIGHT 1000MM	2
2	CLADDING STRAIGHT 2500mm	4
1	ANGLE	16

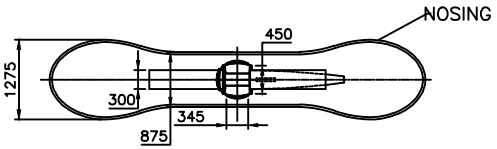

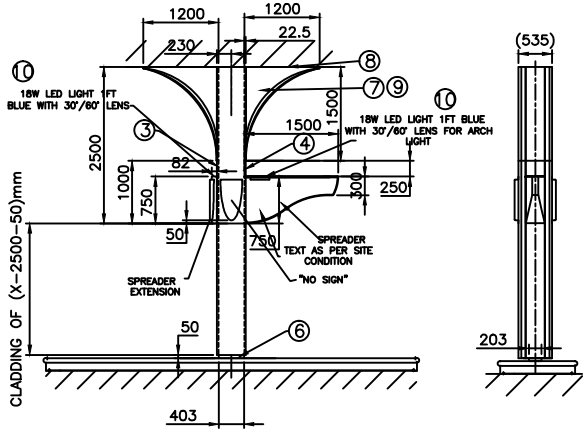

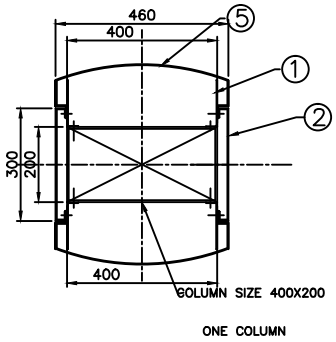

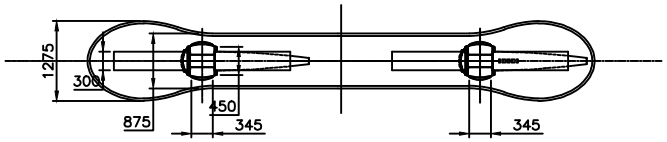

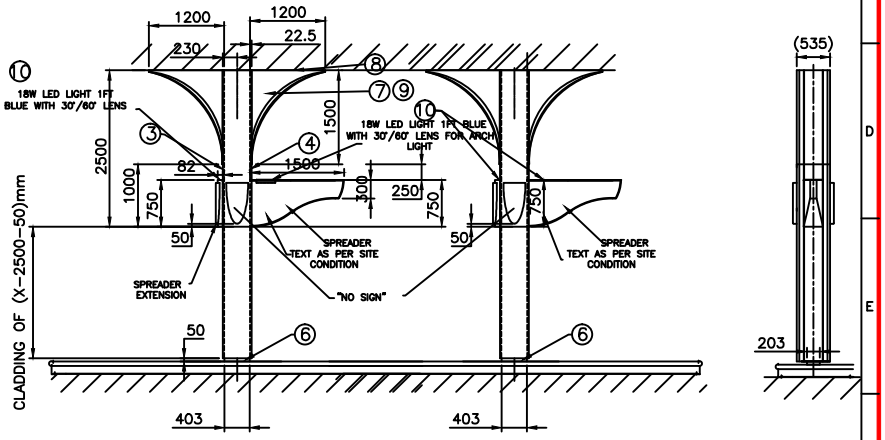

ABOVE 5M COLUMN HEIGHT

BHARAT PETROLEUM CORPORATION LTD.

TITLE :

COLUMN CLADDING FOR BPCL(5M)

REVISIONS	SCALE : 1:22	DRAWN:	CHECKED	SHEET NO. 2of11
	DATE : 23/5/18	GM.RE		

DATE | DRAWING NO.

NUMBERS CROSSED OUT ARE SUPERSEDED DRAWINGS

DRAWING NO : BP.RVI.CA-A02

DIN A2