SR.NO	DESCRIPTION	QTY.
10	PILLER ARCH LIGHT	1
9	STRUCTURE FOR ARCH	2
8	SLIDDING CHANNEL FOR ARCH	2
7	ARCH FOR BPCL	2
6	BOTTOM COVER FOR CLADDING	1
5	REMAIN CLADDING CURVED (2500mm)	2
4	CLADDING CURVED 2500mm(CUTOUT FOR NO SIGN)	2
3	CLADDING STRAIGHT (2750MM)	1
2	CLADDING STRAIGHT (3500mm)	1
1	ANGLE	8

SR.NO	DESCRIPTION	QTY.
10	PILLER ARCH LIGHT	1
9	STRUCTURE FOR ARCH	4
8	SLIDDING CHANNEL FOR ARCH	4
7	ARCH FOR BPCL	4
6	BOTTOM COVER FOR CLADDING	2
5	REMAIN CLADDING CURVED (2500mm)	4
4	CLADDING CURVED 2500mm(CUTOUT FOR NO SIGN)	4
3	CLADDING STRAIGHT (2750MM)	2
2	CLADDING STRAIGHT (3500mm)	2
1	ANGLE	16

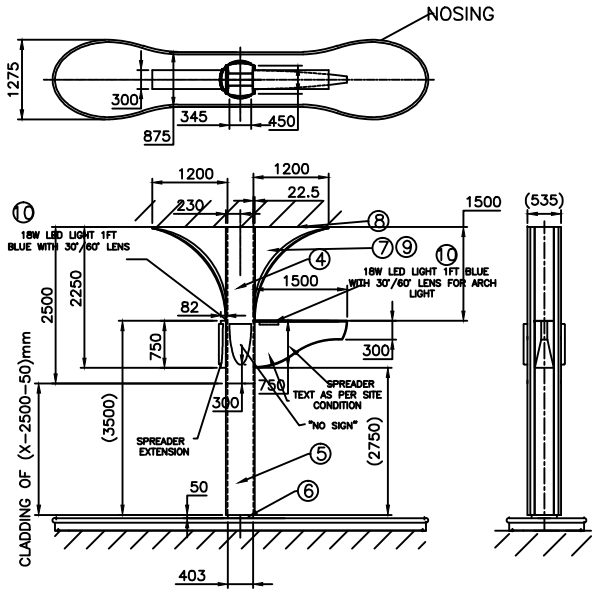

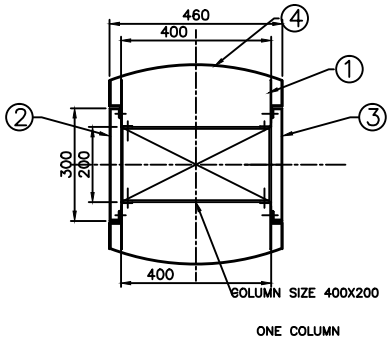

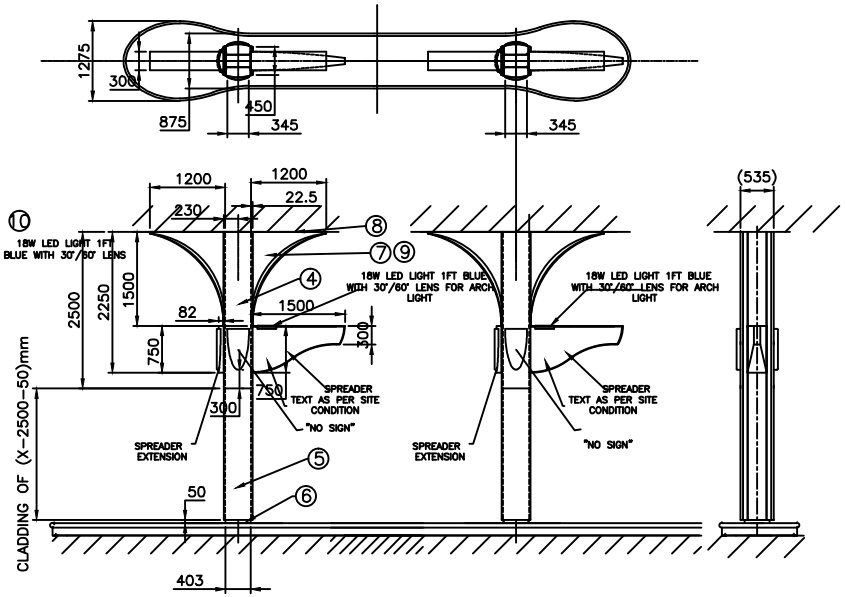

BELOW 5M COLUMN HEIGHT

BHARAT PETROLEUM CORPORATION LTD.

TITLE :

COLUMN CLADDING FOR BPCL(5M)
BELOW 5m COLUMN HEIGHT

SCALE : 1:22	DRAWN:	CHECKED	SHEET NO.	DRAWING NO :
DATE : 23/5/18	GM.RE		2of11	BP.RVI.CA-A02a

REVISIONS

DATE | DRAWING NO.

NUMBERS CROSSED OUT ARE SUPERSEDED DRAWINGS

DIN A2