


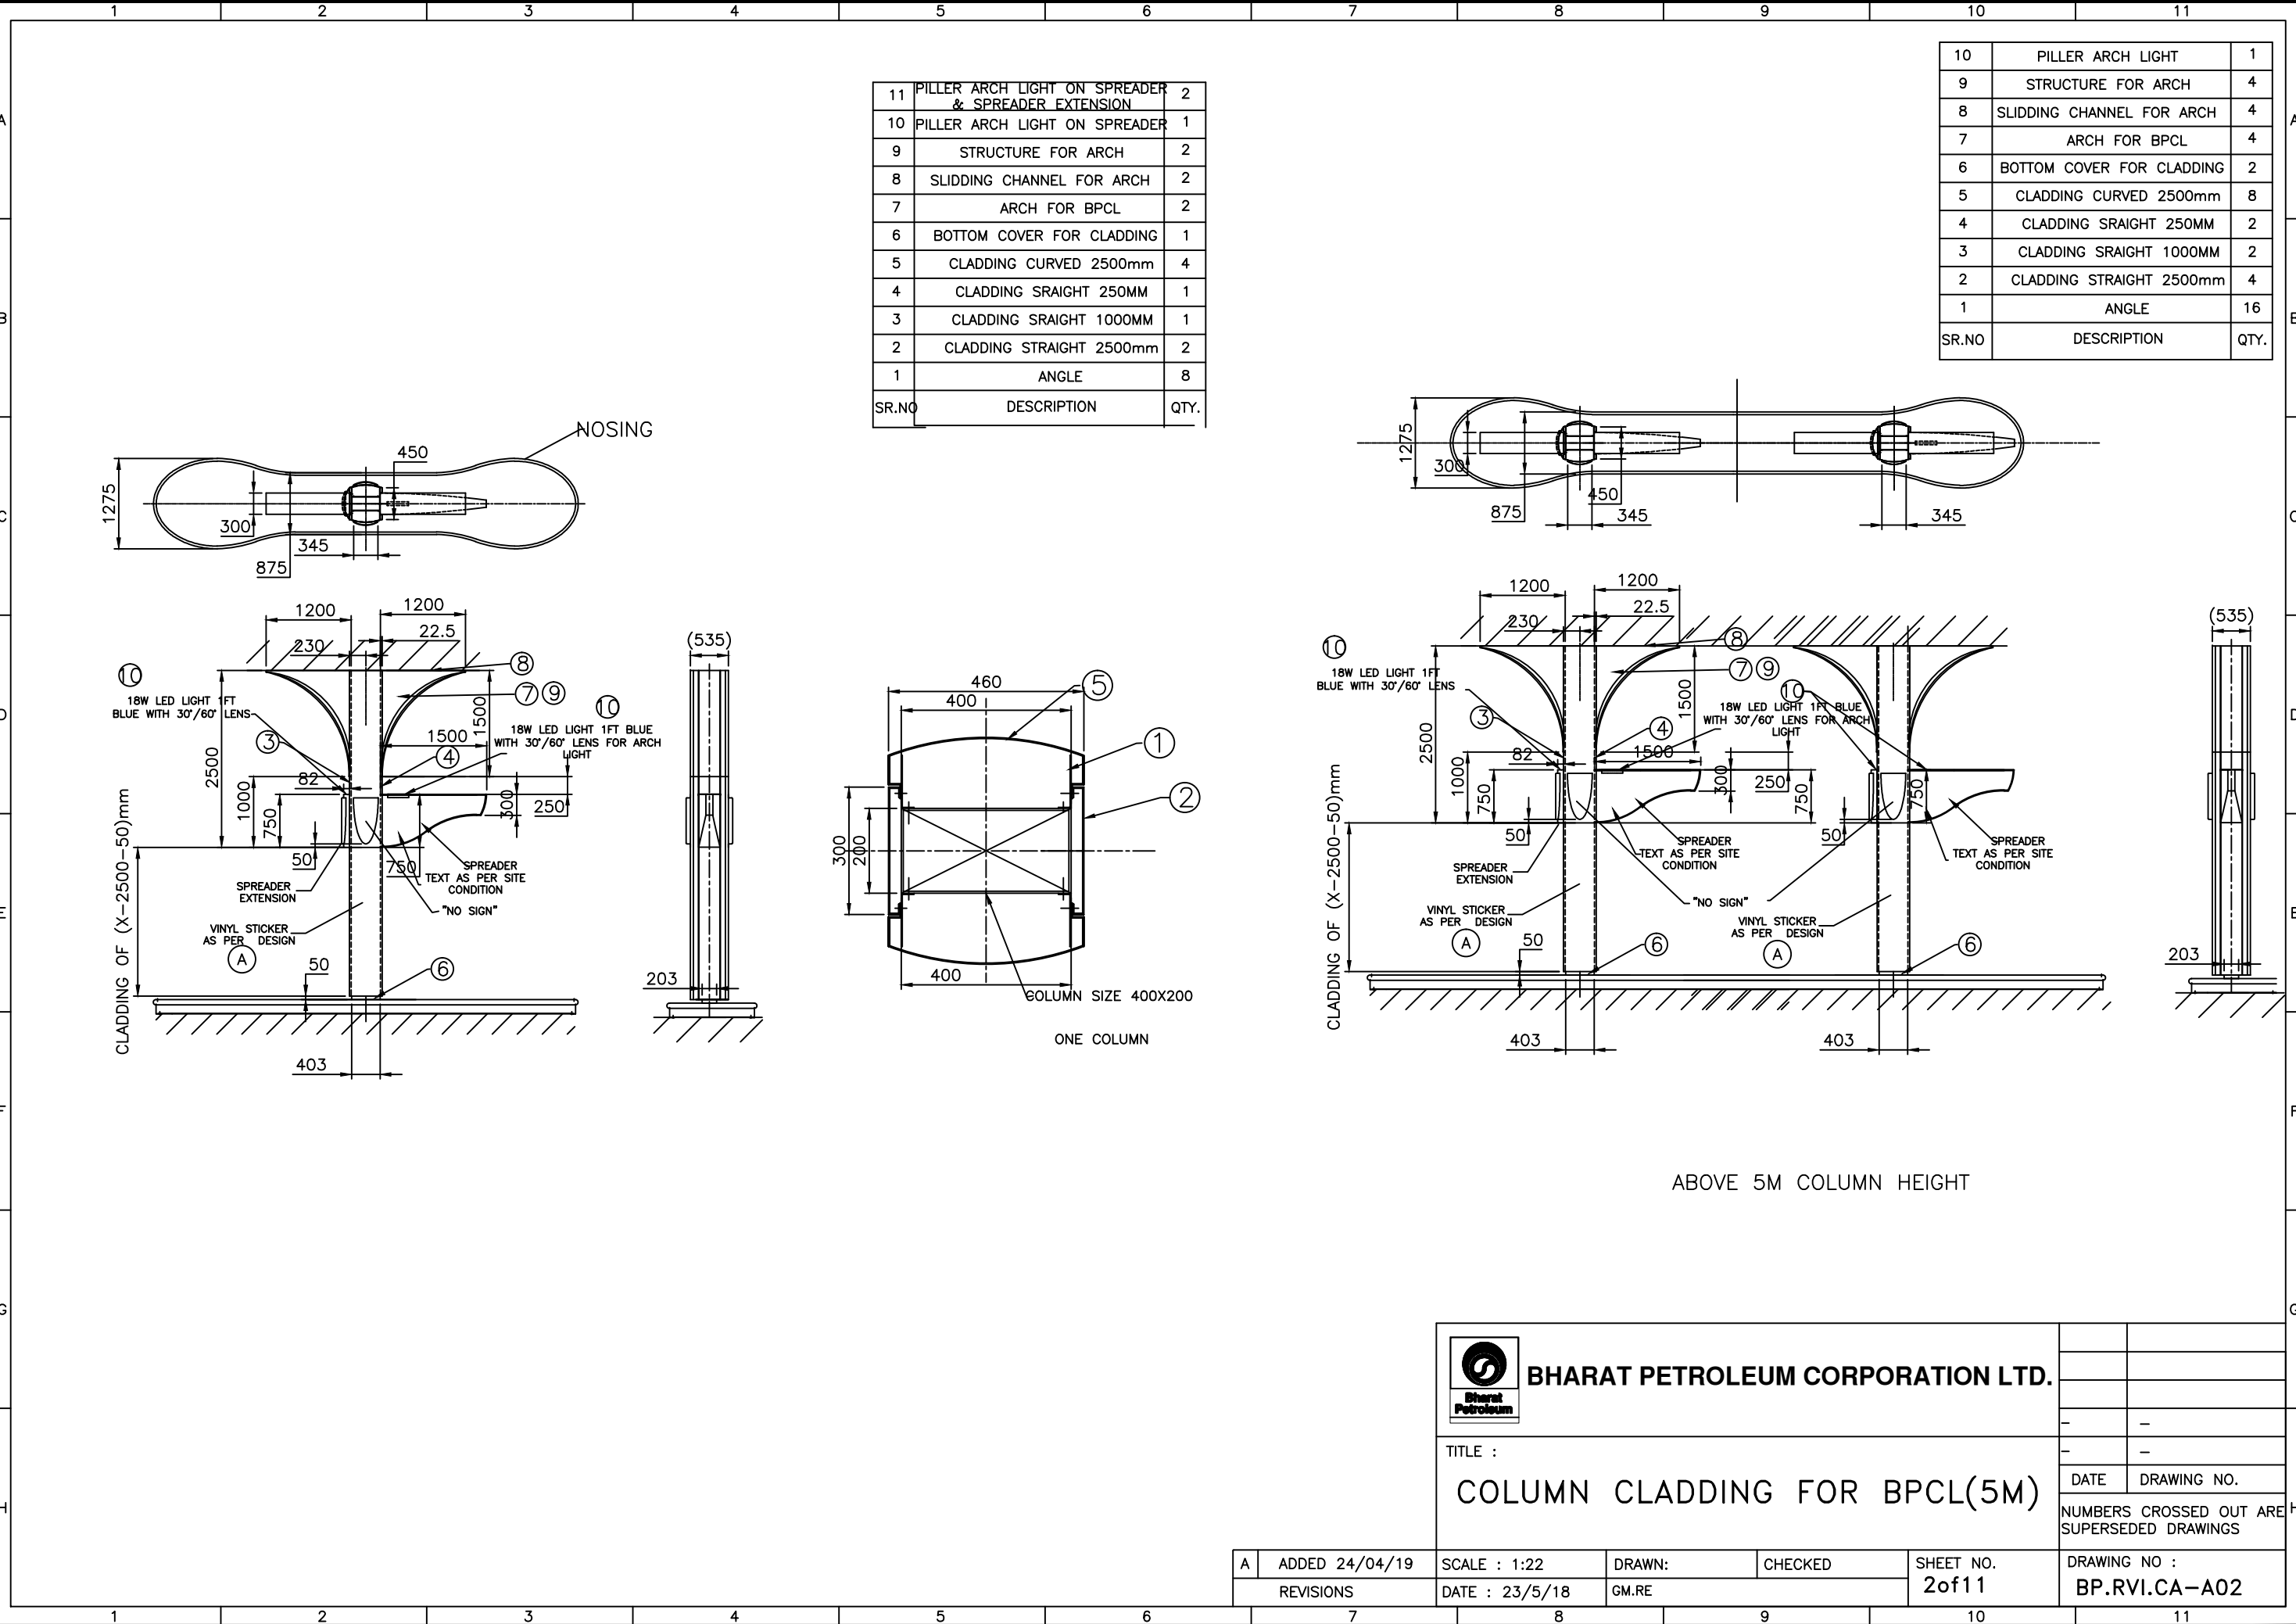

11	PILLER ARCH LIGHT ON SPREADER & SPREADER EXTENSION	2
10	PILLER ARCH LIGHT ON SPREADER	1
9	STRUCTURE FOR ARCH	2
8	SLIDGING CHANNEL FOR ARCH	2
7	ARCH FOR BPCL	2
6	BOTTOM COVER FOR CLADDING	1
5	CLADDING CURVED 2500mm	4
4	CLADDING SRAIGHT 250MM	1
3	CLADDING SRAIGHT 1000MM	1
2	CLADDING STRAIGHT 2500mm	2
1	ANGLE	8
SR.NO	DESCRIPTION	QTY.

10	PILLER ARCH LIGHT	1
9	STRUCTURE FOR ARCH	4
8	SLIDGING CHANNEL FOR ARCH	4
7	ARCH FOR BPCL	4
6	BOTTOM COVER FOR CLADDING	2
5	CLADDING CURVED 2500mm	8
4	CLADDING SRAIGHT 250MM	2
3	CLADDING SRAIGHT 1000MM	2
2	CLADDING STRAIGHT 2500mm	4
1	ANGLE	16
SR.NO	DESCRIPTION	QTY.



BHARAT PETROLEUM CORPORATION LTD.

TITLE :

COLUMN CLADDING FOR BPCL(5M)

A	ADDED 24/04/19
REVISIONS	

SCALE : 1:22
DATE : 23/5/18

DRAWN:	CHECKED
GM.RE	

SHEET NO.
2 of 11

DRAWING NO :
BP.RVI.CA-A02

NUMBERS CROSSED OUT ARE SUPERSEDED DRAWINGS

DATE

DRAWING NO.