
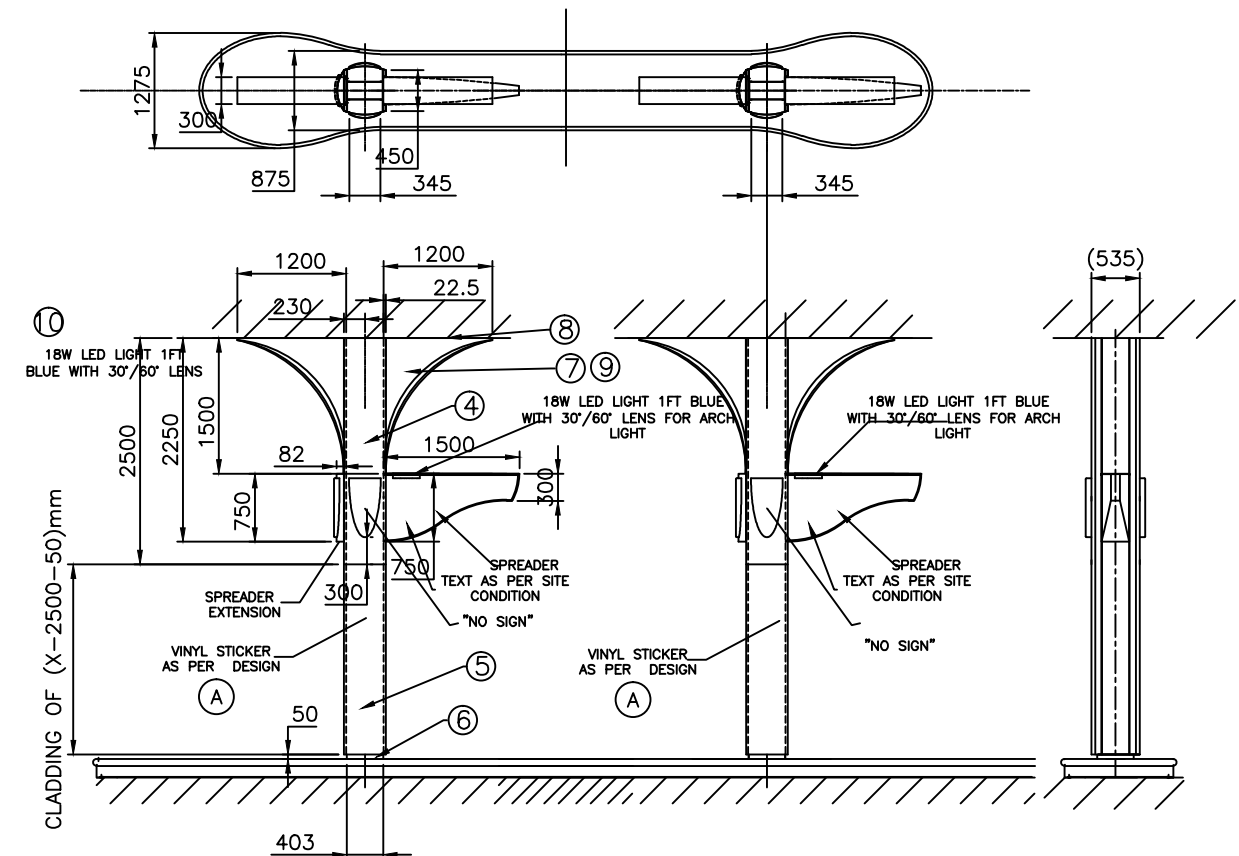


10	PILLER ARCH LIGHT	1
9	STRUCTURE FOR ARCH	4
8	SLIDDING CHANNEL FOR ARCH	4
7	ARCH FOR BPCL	4
6	BOTTOM COVER FOR CLADDING	2
5	REMAIN CLADDING CURVED (2500mm)	4
4	CLADDING CURVED 2500mm(CUTOUT FOR NO SIGN)	4
3	CLADDING STRAIGHT (2750MM)	2
2	CLADDING STRAIGHT (3500mm)	2
1	ANGLE	16
SR.NO	DESCRIPTION	QTY.

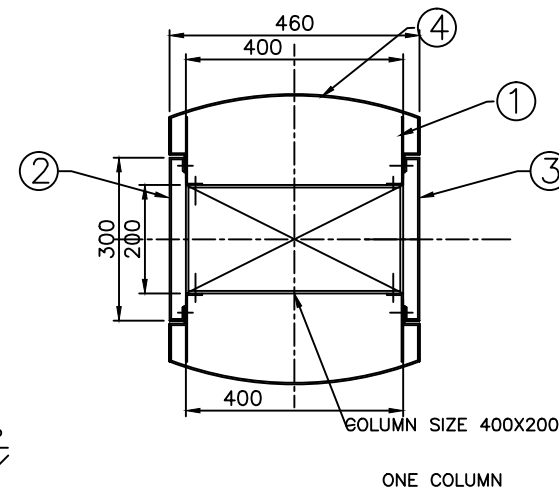

**Bharat
Petroleum**

A	ADDED 24/04/19	SCALE : 1:22	DRAWN:	CHECKED	SHEET NO. 2 of 11	DRAWING NO : BP.RVI.CA-A02a
REVISIONS		DATE : 23/5/18	GM.RE			