


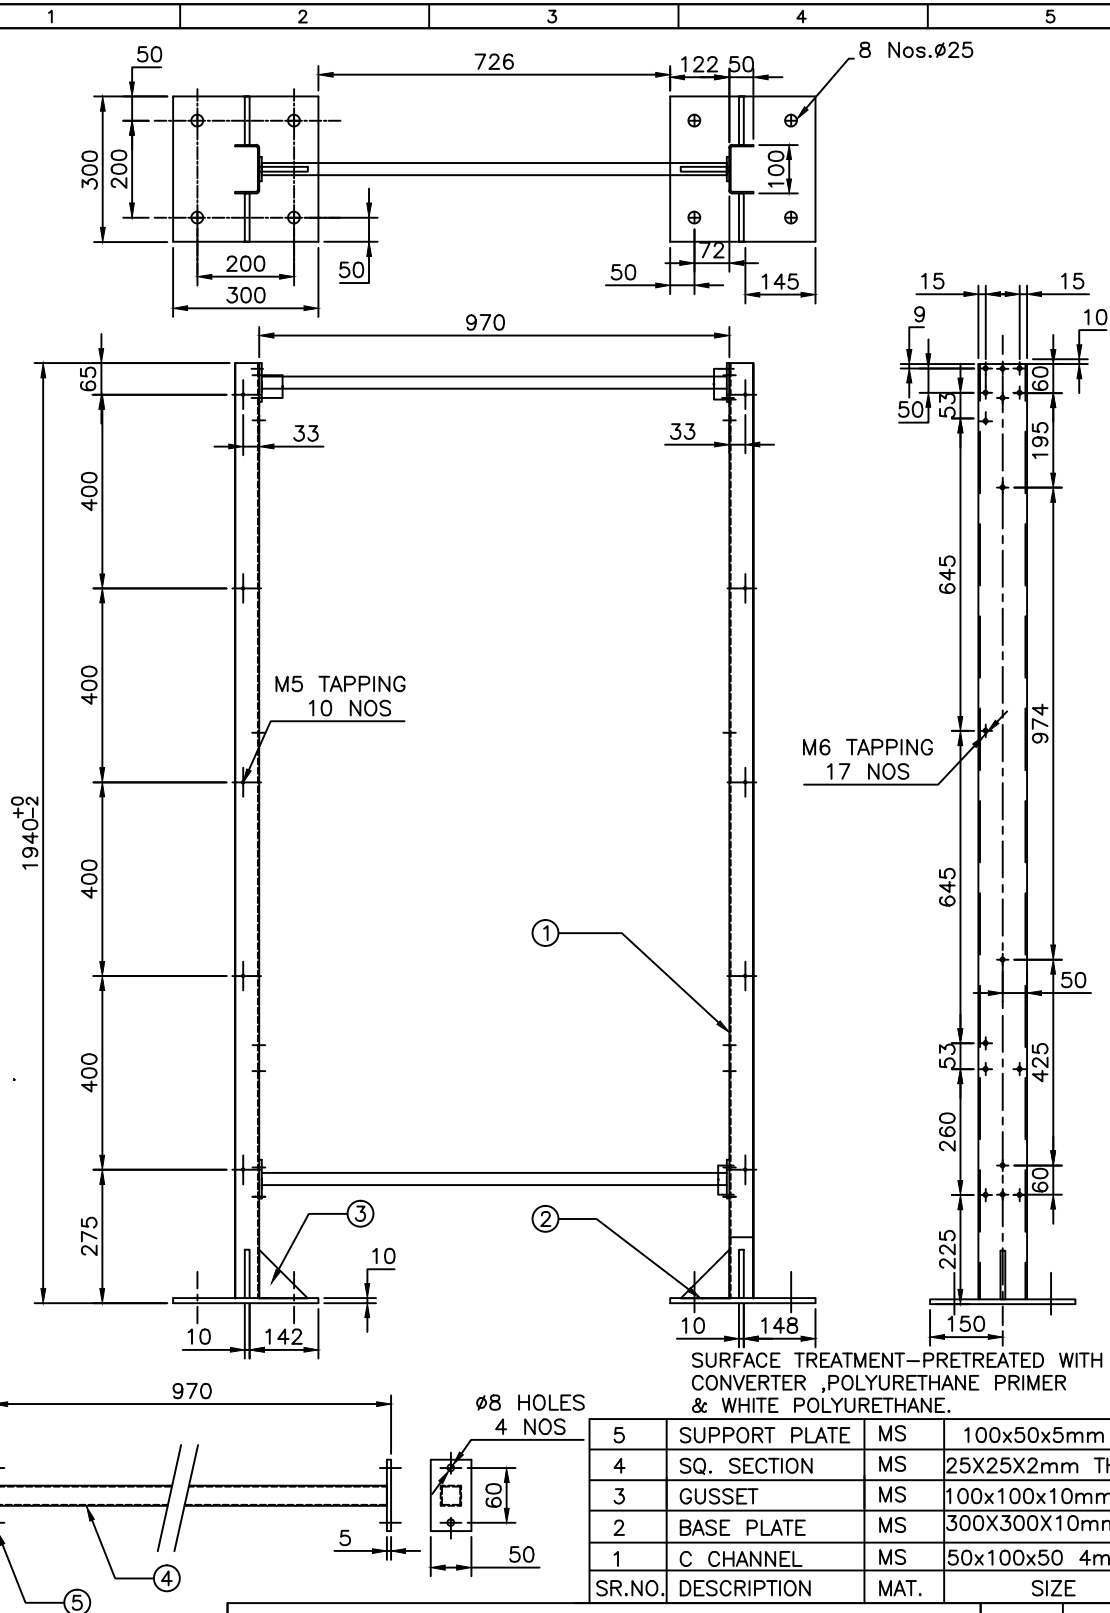

BHARAT PETROLEUM CORPORATION LTD.

TITLE :

POLE STRUCTURE (FACILITY SIGN)

A RETRO 26/5/18	SCALE : 1:1	DRAWN:	CHECKED	SHEET NO.	DRAWING NO :
REVISIONS	DATE : 17/2/05	GM.RE		5 OF 17	BP.RVI.FS.-P05