


Ø5HOLES
2 NOS

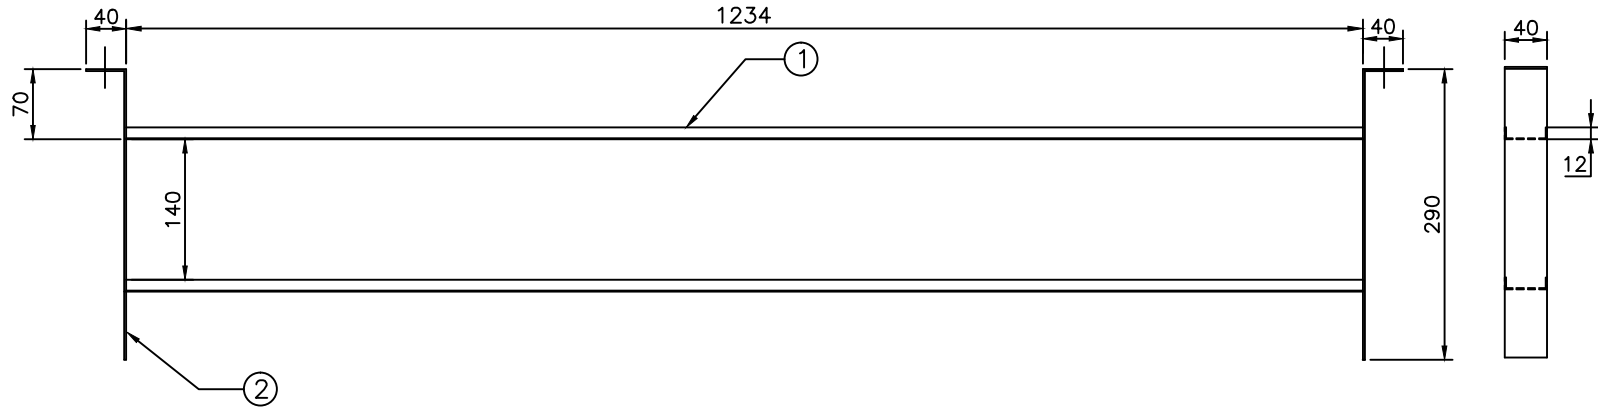

SURFACE TREATMENT—PRETREATED
& WHITE PAINTED

2	L BRACKET	CRCA	290X40X2mm THK	2
1	C CHANNEL	CRCA	12X40X12mm 1.2THK 1234 LENGTH.	2
SR NO	DESCRIPTION	MATERIAL	SIZE	QTY.



BHARAT PETROLEUM CORPORATION LTD.

TITLE :

TUBE FRAME (SPREADER)

SCALE : 1:20

DRAWN:

CHECKED

SHEET NO.

DRAWING NO :

DATE : 24/5/18

GM.RE

5 of 8

BP.RVI.SU-P05

REVISION