


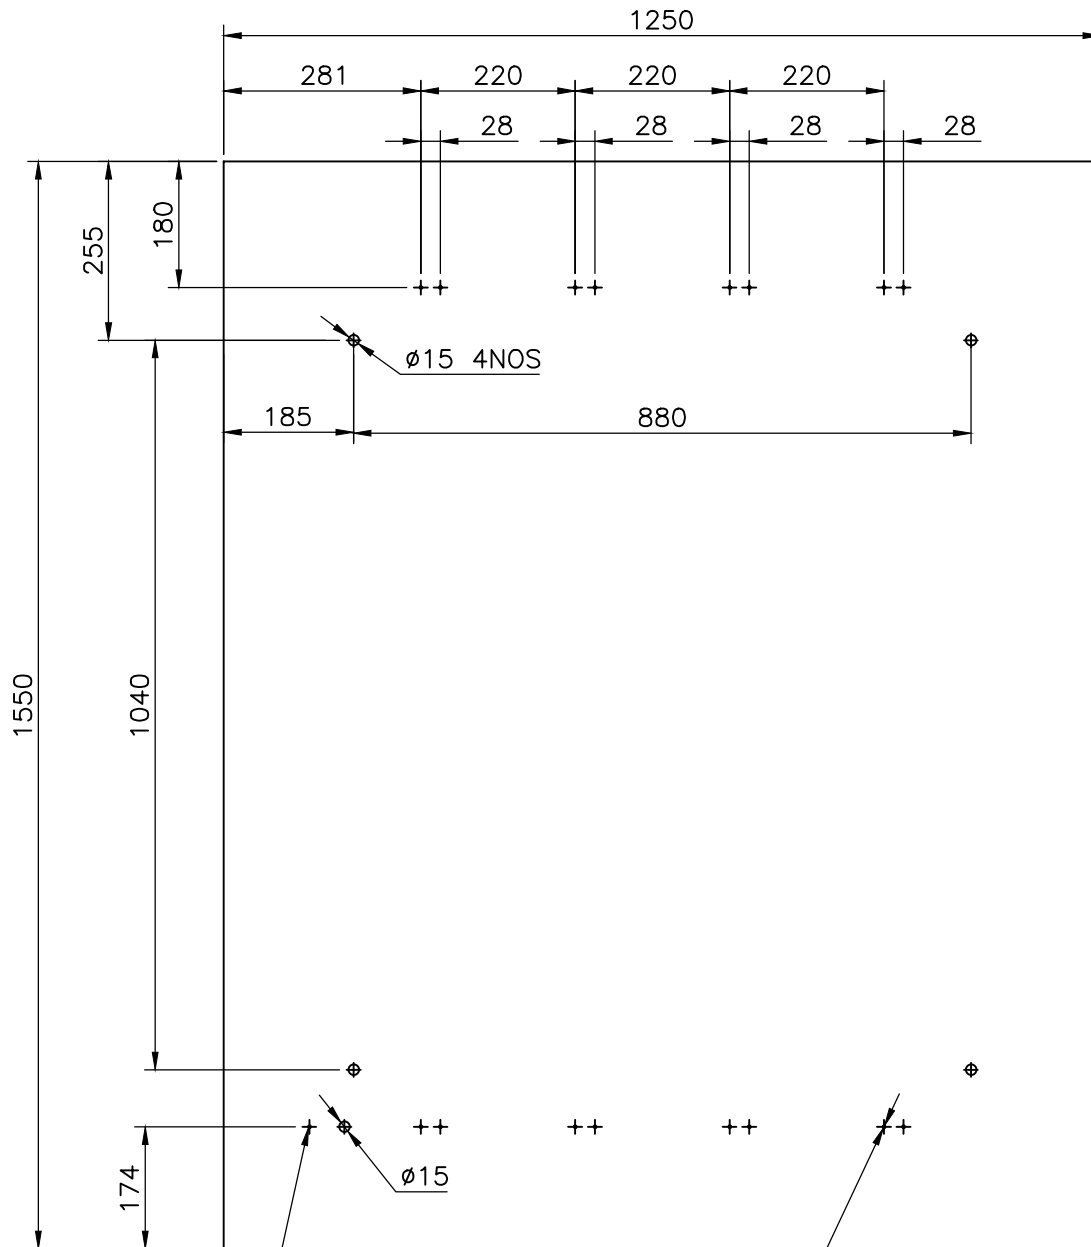

M4 BUSH $\phi 10 \times 10$ MM
HEIGHT TAG WELDED

M4 TAPPING 16 NOS

MATERIAL—CRCA STEEL SHEET 2mm THK.IS:513.
SURFACE TREATMENT—POWDER COATING WHITE SEMI GLOSSY 50
MICRON.



BHARAT PETROLEUM CORPORATION LTD.

TITLE :

BACK SHEET

SCALE : 1:10

DRAWN: SUK

CHECKED

SHEET NO.

DRAWING NO :

DATE : 1/11/04

Sr. Mgr. (DESIGN & DEVP.)

6 OF 7

BP.RVI.WM.PO6