



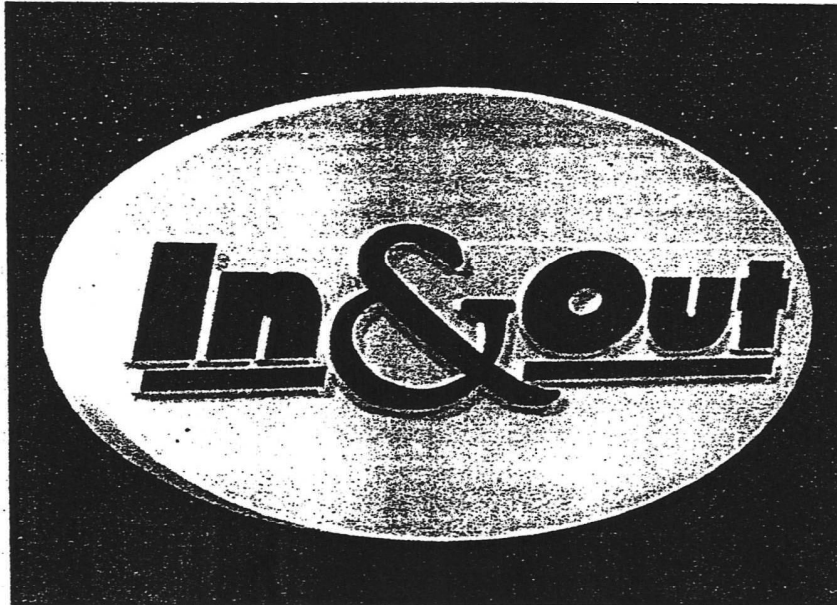

In & Out Sign

- In & Out Sign displays the shop orientation. It is fixed to the white portion above the entrance to the shop
- Materials used are aluminium, and PET-G letter moulds.
- In & Out sign is backlit.
- The dimensions are 1830x800mm (600mm over white and 200mm over sales room Blue fascia).

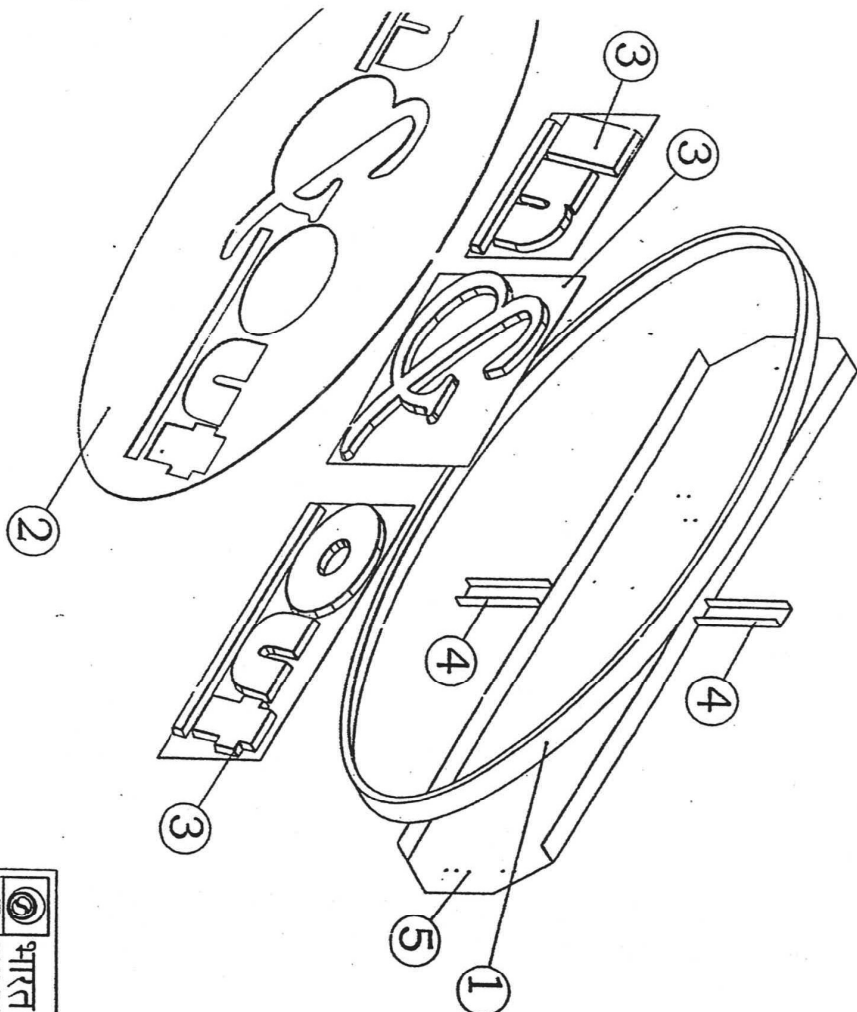


5	GEAR TREY	1
4	C-CHANNEL	2
3	PET-G LETTERS	1SET
2	DISPLAY SHEET	1
1	FRAME	1
SR. NO	NAME OF COMPONENT	QTY

भारत पेट्रोलियम कॉर्पोरेशन लिमिटेड BHARAT PETROLEUM CORPORATION LTD.			
SUBJECT: R V M			
TITLE: IN & OUT SIGN			
SCALE: 1:10	DRAWN	TRACED	CHECKED
DATE: 12/8/04	CHEF MGR. (P&E) NO	SHEET NO: 1 OF 4	
DRAWING NO.		DRAWING NO.	
NUMBERS CROSS-OUT		NUMBERS CROSS-OUT	
DRAWING NO.		DRAWING NO.	
BP.RV.I.O-A01			





98

DN/AS

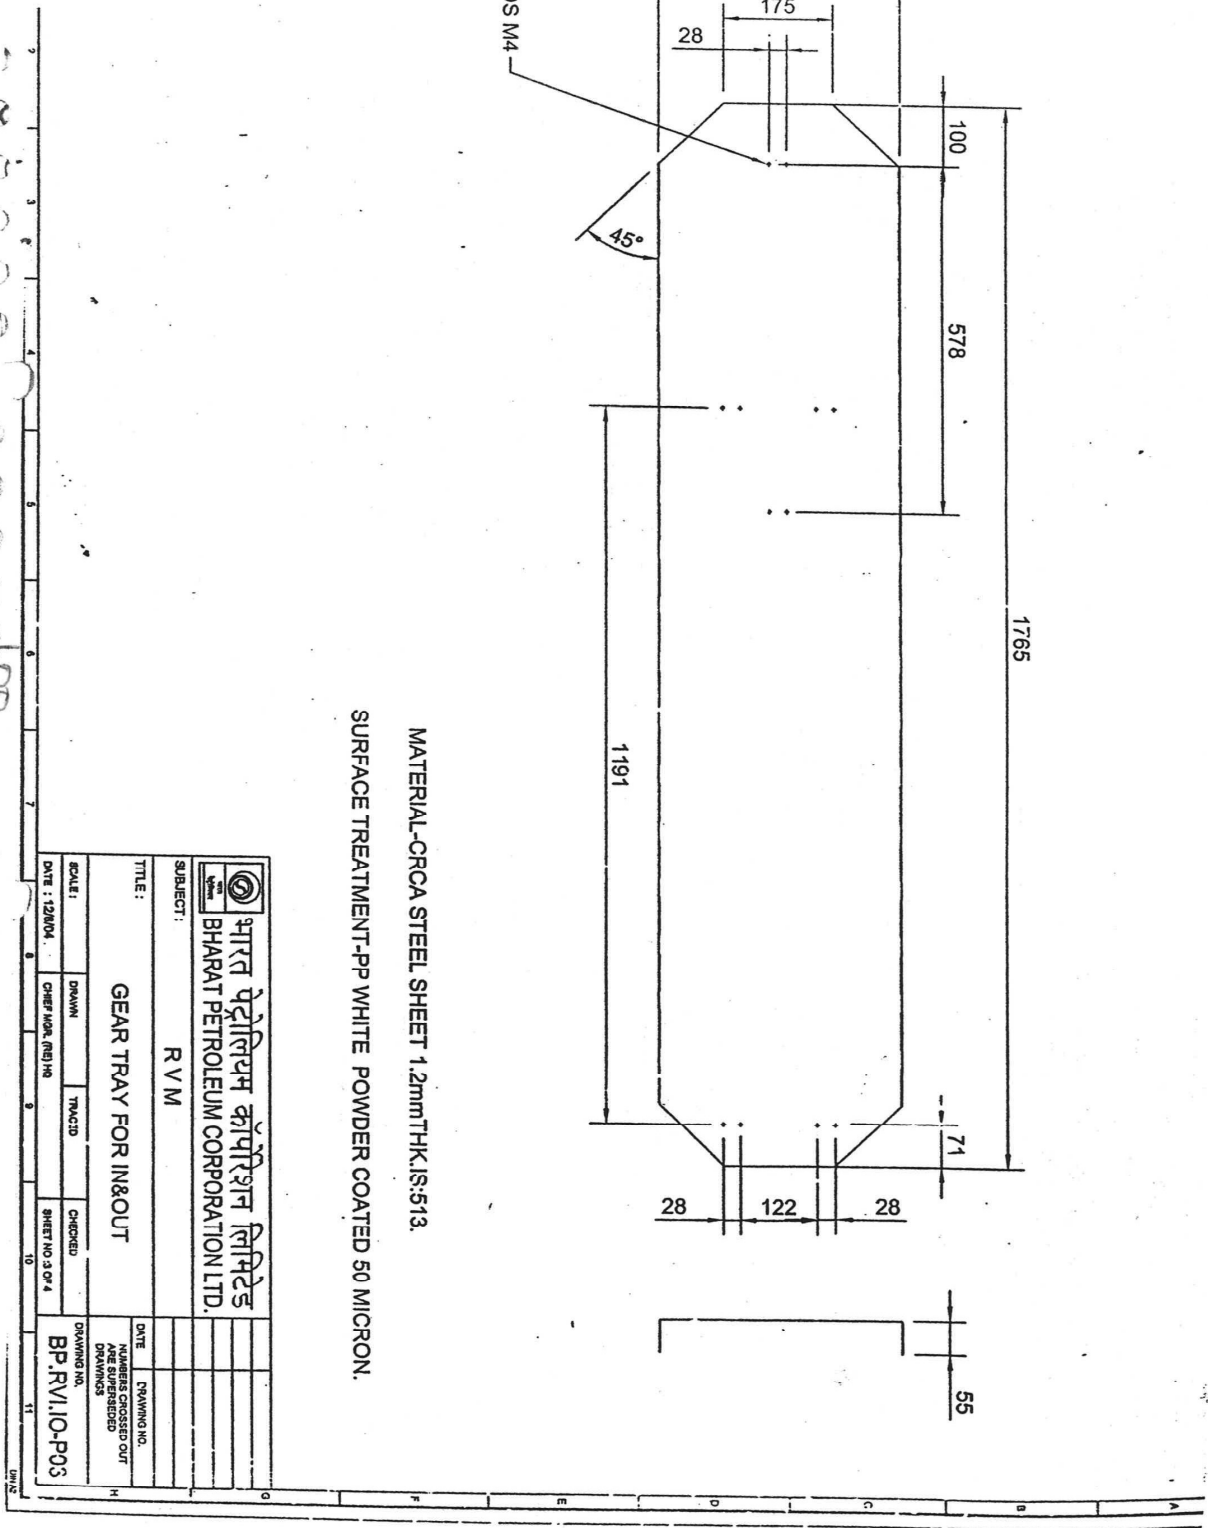

SURFACE TREATMENT-PP WHITE POWDER COATED 50 MICRON.

		भारत पेट्रोलियम कॉर्पोरेशन लिमिटेड BHARAT PETROLEUM CORPORATION LTD.	
SUBJECT:		R V M	
TITLE:		GEAR TRAY FOR IN&OUT	
SCALE:	DRAWN	TYPICD	CHECKED
DATE : 12/04/04	CHRG MGR. (S/N)	BHMT NO	3 OF 4
DRAWING NO.		DATE	
BP.RVI.I.O.P-03		NUMBERS CROSSED OUT ARE SUPERSEDED DRAWINGS	

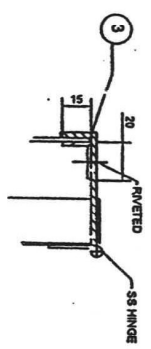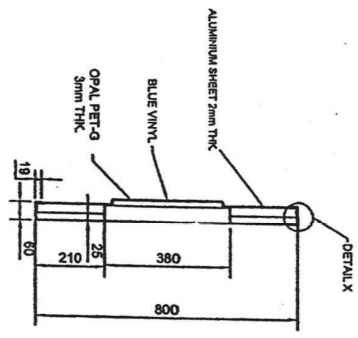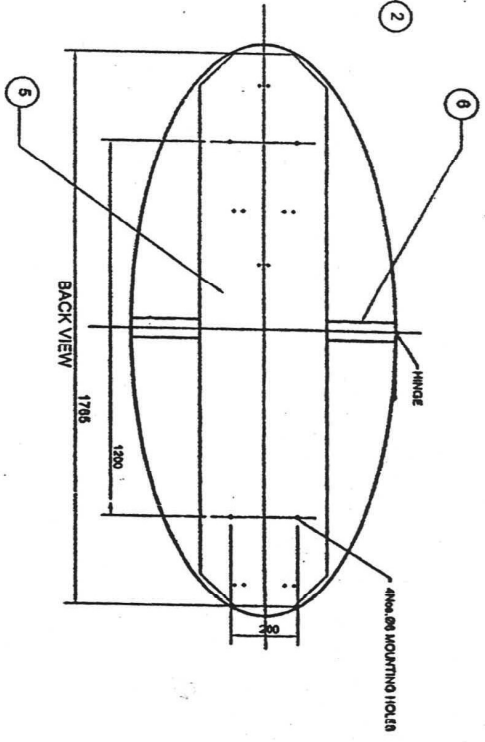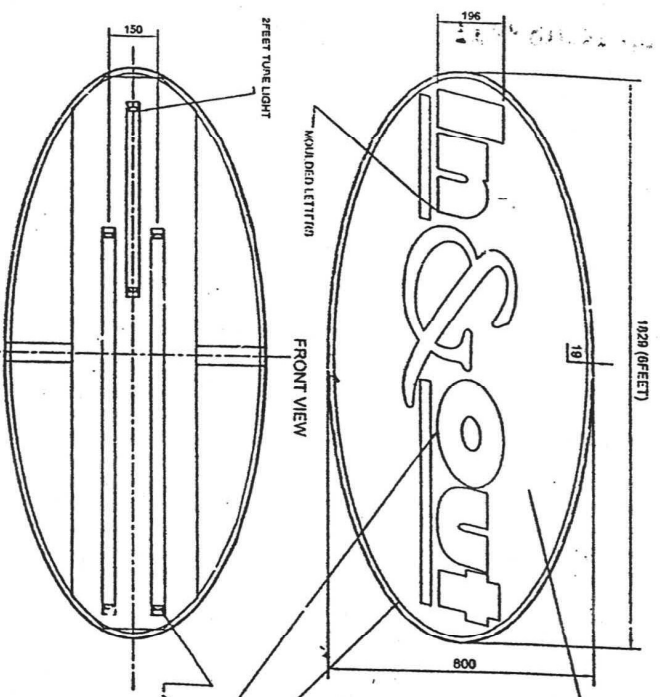

SCALE R:1 DETAIL X
BACK VIEW

FRONT VIEW WITHOUT FRONT SHEET

ITEM NO.	DESCRIPTION	MATERIAL / SPECIFICATION	QTY.
1	HINGE		1
2	CONNECTOR	2WAY 15 AMP	1
3	CONNECTOR	2WAY 10 AMP	2
4	CONNECTOR	4WAY 5 AMP	2
5	BRACKET HOLDER		6
6	BALLAST	ELECTRONIC BALLAST 20W	1
7	BALLAST	ELECTRONIC BALLAST 40W PHILIPS MAKE	2
8	TUBE LIGHT	2 FEET	1
9	TUBE LIGHT	4 FEET	2
10	C CHANNEL	CROCA STEEL SHEET 1.2 mm THK IS:513	2
11	GEAR TRAY	PP WHITE POWDER COATED 50 MICRON.	1
12	FORMED LETTERS	OPAL PET-G 3mm THK FORMED	
13	ANGLE	ALUMINIUM SHEET 1.6mm THK IS:737	4
14	DISPLAY SHEET	ALUMINIUM SHEET 2mm THK IS:737 CHROMATE TREATED & PP PCL YELLOW POWDER COATED 50micron	1
15	FRAME	ALUMINIUM SHEET 3mm THK IS:737 PP WHITE POWDER COATED 50micron.	1

भारत पेट्रोलियम कॉर्पोरेशन लिमिटेड BHARAT PETROLEUM CORPORATION LTD.			
SUBJECT: R V M			
TITLE: IN & OUT SIGN			
SCALE: 1/20/04	DRAWN	TRACED	CHECKED
DATE: 12/06/04	CHEF MOD. (RS) NO		SHEET NO 2 OF 4
DRAWING NO. BP.R.V.I.10-A-52			DATE
NUMBERS CROSSED OUT ARE UNREVERSED			DRAWING NO.

99