


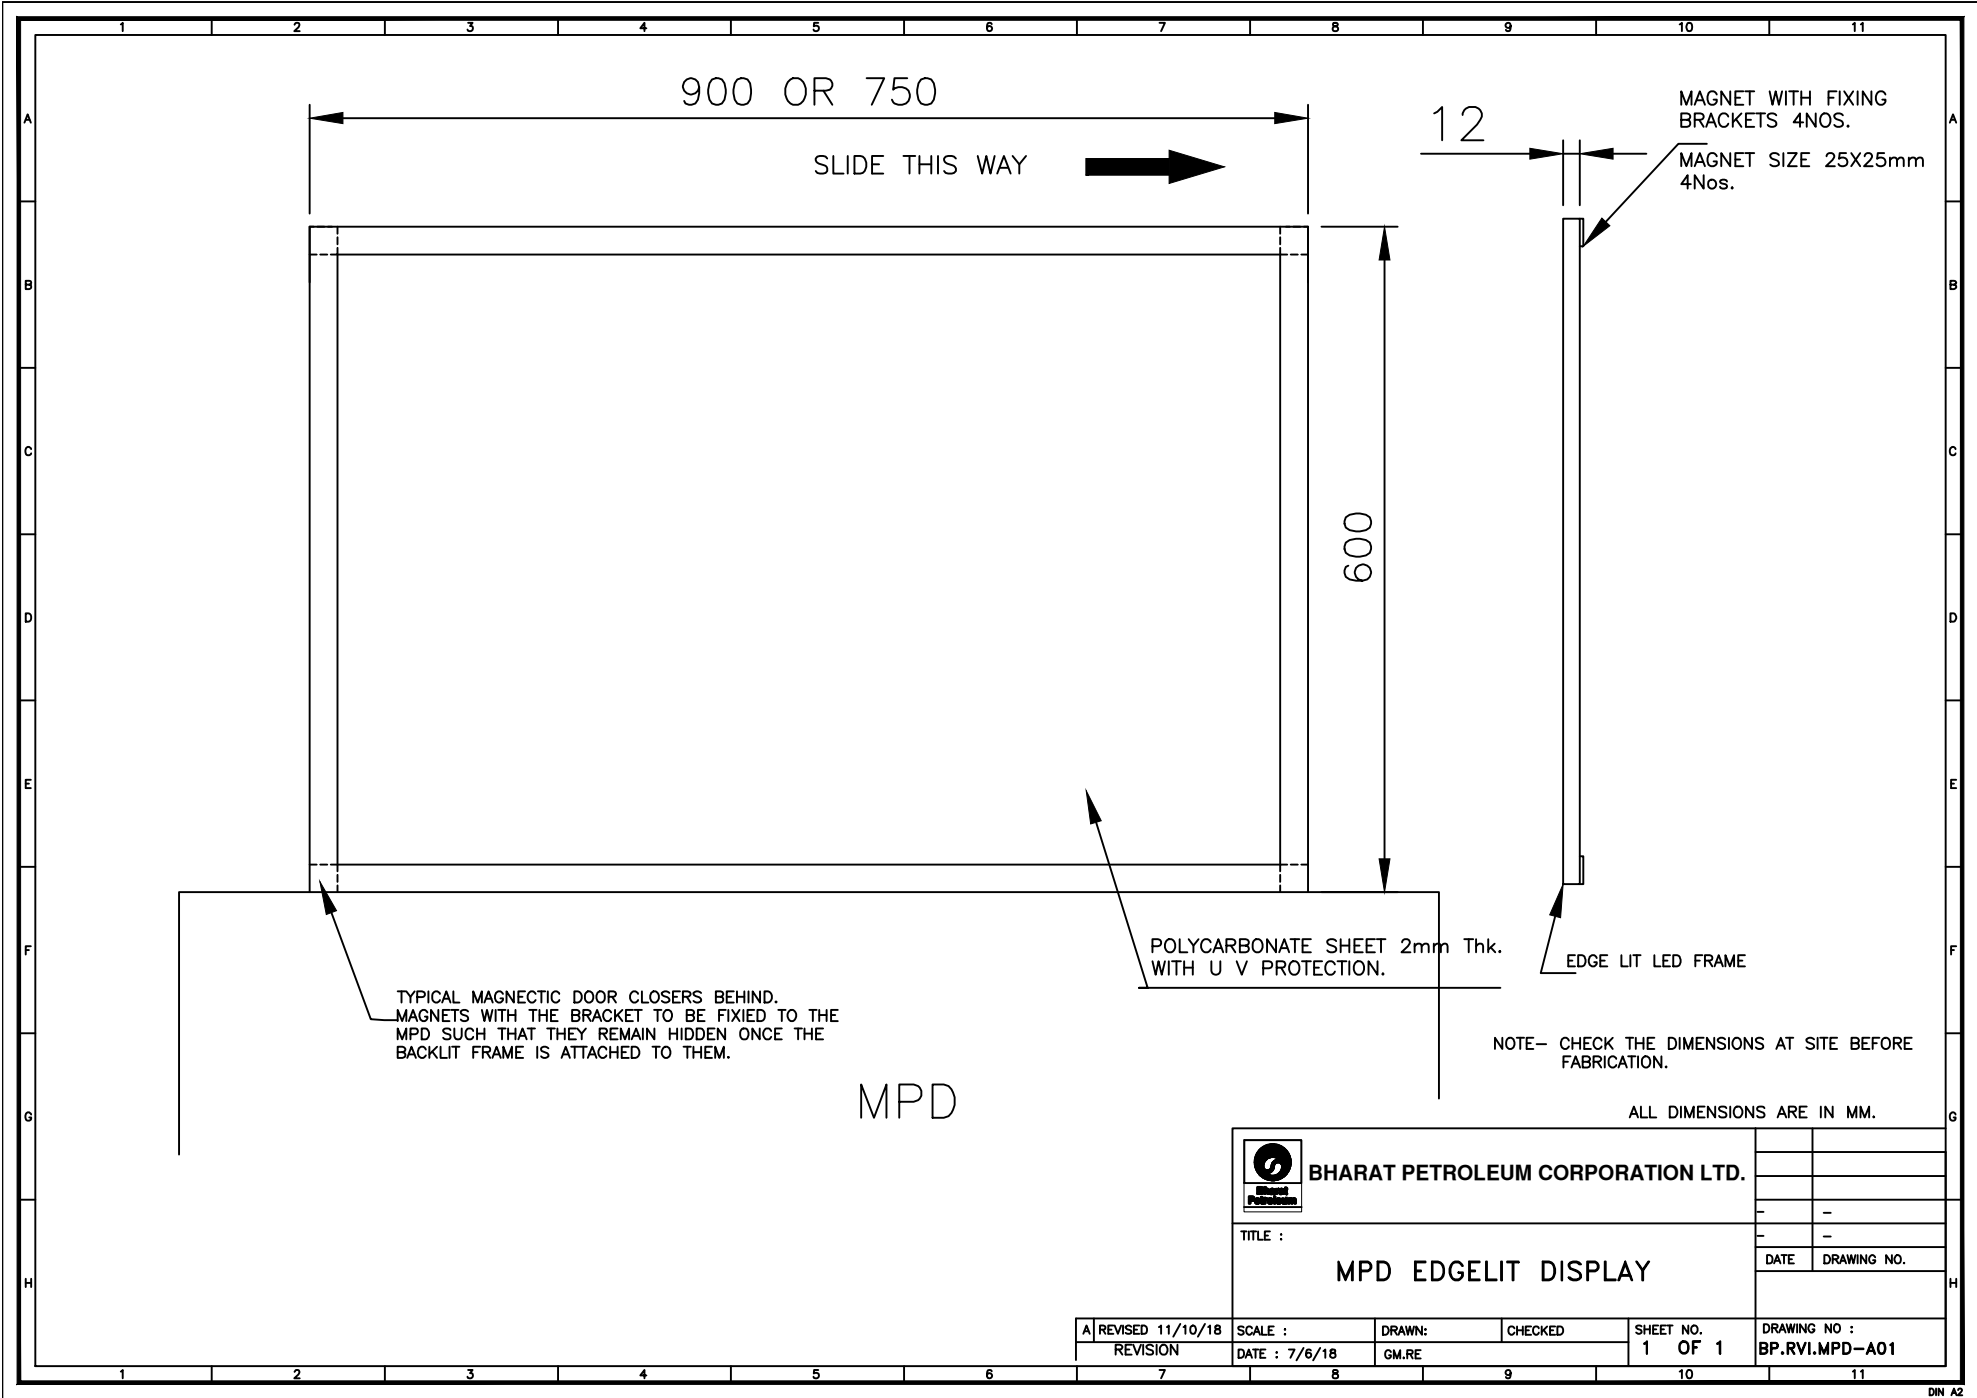

900 OR 750

SLIDE THIS WAY

12

MAGNET WITH FIXING
BRACKETS 4NOS.
MAGNET SIZE 25X25mm
4NOS.

600

TYPICAL MAGNETIC DOOR CLOSERS BEHIND.
MAGNETS WITH THE BRACKET TO BE FIXED TO THE
MPD SUCH THAT THEY REMAIN HIDDEN ONCE THE
BACKLIT FRAME IS ATTACHED TO THEM.

POLYCARBONATE SHEET 2mm Thk.
WITH U V PROTECTION.

EDGE LIT LED FRAME

NOTE- CHECK THE DIMENSIONS AT SITE BEFORE
FABRICATION.

MPD

ALL DIMENSIONS ARE IN MM.

	BHARAT PETROLEUM CORPORATION LTD.					
	TITLE :					
	MPD EDGELIT DISPLAY				DATE	DRAWING NO.
A	REVISED 11/10/18	SCALE :	DRAWN:	CHECKED	SHEET NO.	DRAWING NO :
	REVISION	DATE : 7/6/18	GM.RE		1 OF 1	BP.RVI.MPD-A01