


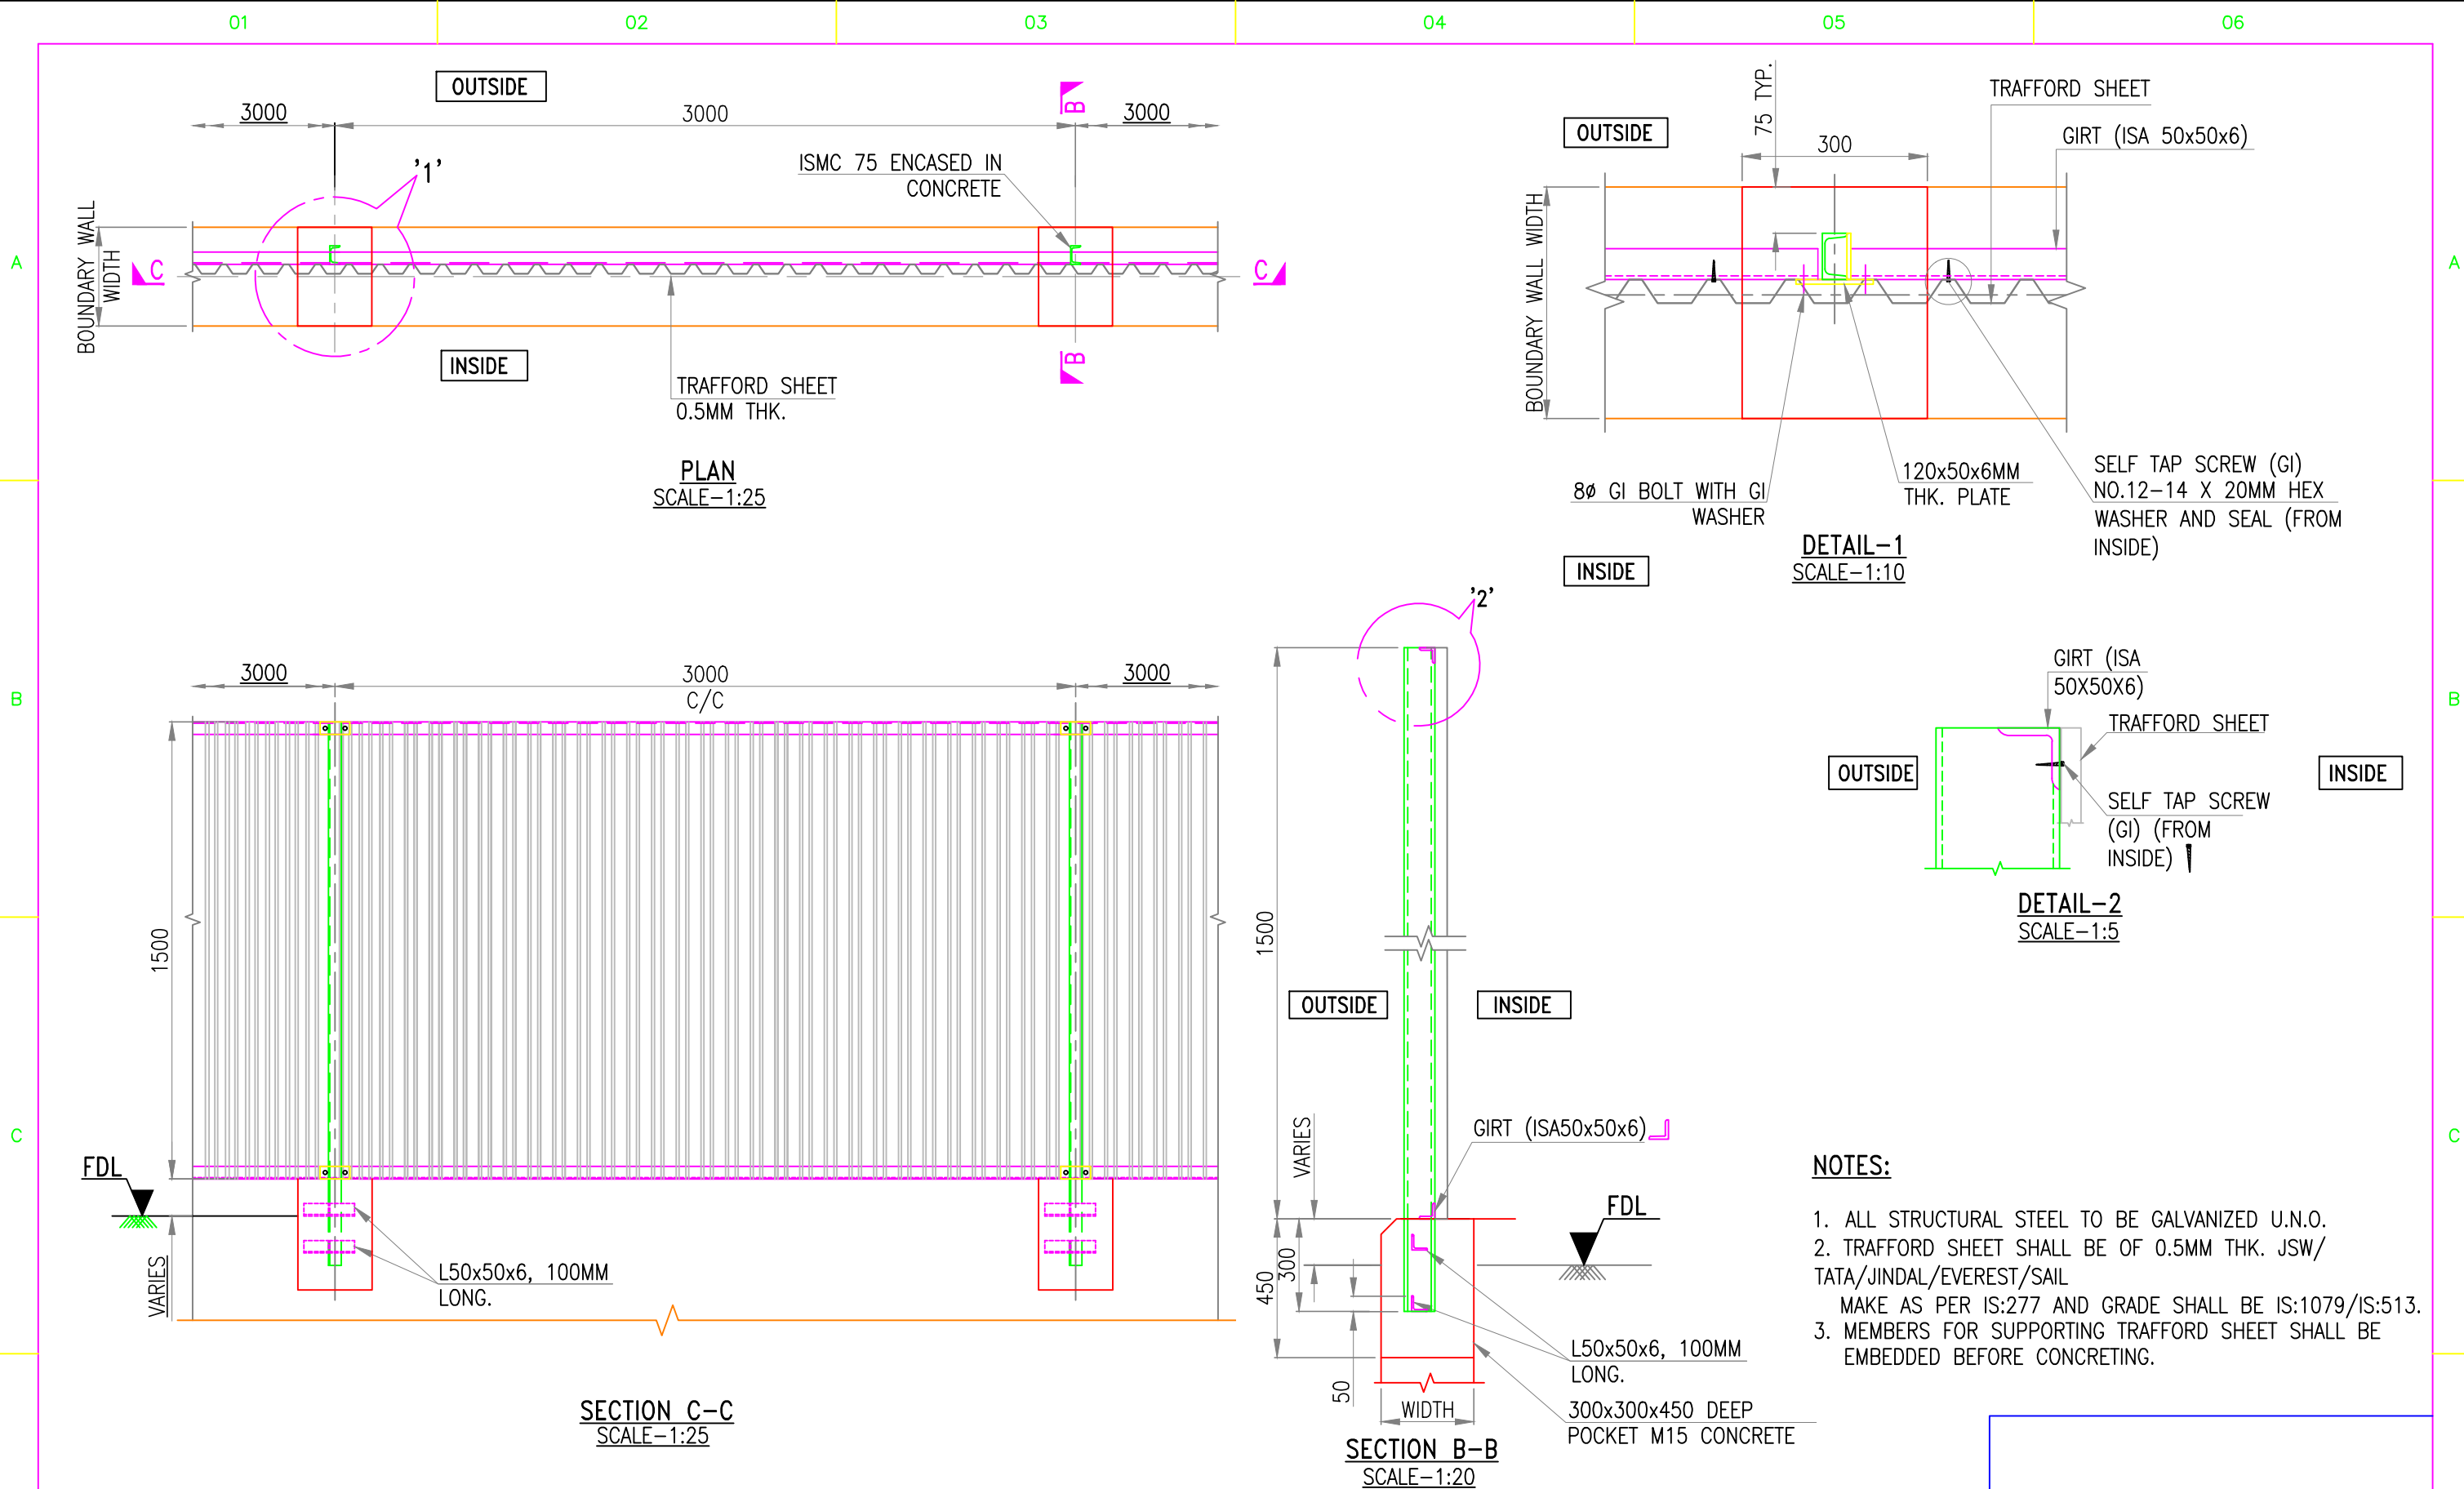

GENERAL NOTES										CLIENT										CONSULTANT																													
1. ALL DIMENSIONS ARE IN MILLIMETERS UNLESS NOTED OTHERWISE. 2. DIMENSIONS ARE NOT TO BE SCALED. 3. ANY DISCREPANCY MUST BE BROUGHT TO THE NOTICE OF ENGINEER IN CHARGE.																				 MEINHARDT EPCM INDIA PRIVATE LIMITED.																													
										PROJECT										PROJECT NUMBER																													
										BHARAT PETROLEUM										MHISCO																													
0 E ISSUED FOR CONSTRUCTION										JK RGS SR JC 10/02/20										STANDARD DRAWING-GENERAL																													
REV. I.T. DESCRIPTION										DESIG DRAW CKD. APPR. DATE										BOUNDARY WALL – TRAFFORD SHEET DETAILS																													
REFERENCE DOCUMENTS										REVISIONS										SCALE										DRAWING NUMBER										REV.									
1. SITE CODE-LA-03 3. SITE CODE-LA-04										I.T. - ISSUE (A) PRELIMINARY (C) FOR INFORMATION (E) FOR CONSTRUCTION (G) AS BUILT										AS SHOWN										MHISCO-CS-27										0									
2. SITE CODE-CS-03										(B) FOR APPROVAL (D) FOR QUOTATION (F) AS PURCHASED (H) CANCELED																																							
										THIS DOCUMENT DISCLOSES PROPRIETARY INFORMATION OF MEINHARDT EPCM (INDIA) PRIVATE LIMITED. IT MAY BE REPRODUCED OR DISCLOSED ONLY WITH THE WRITTEN PERMISSION AND IS NOT TO BE USED IN ANY WAY DETRIMENTAL TO THE INTEREST OF MEINHARDT EPCM (INDIA) PRIVATE LIMITED.																																							