

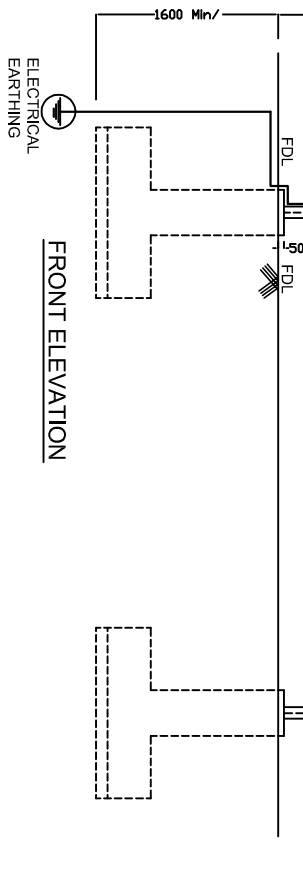



SECTIONAL PLAN

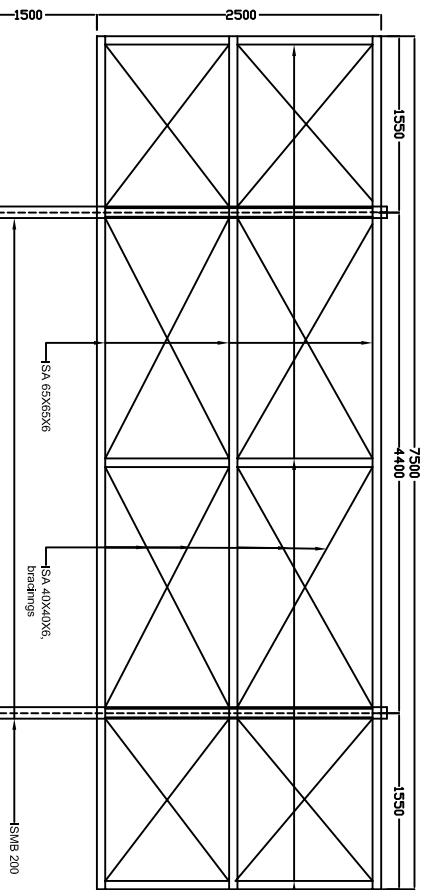


FRONT ELEVATION

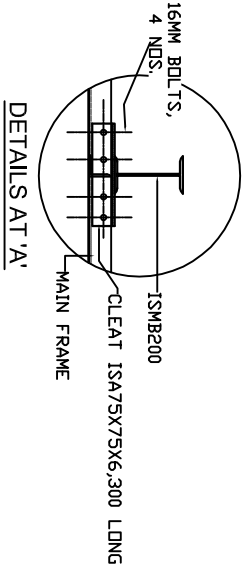


DETAILS AT 'A'

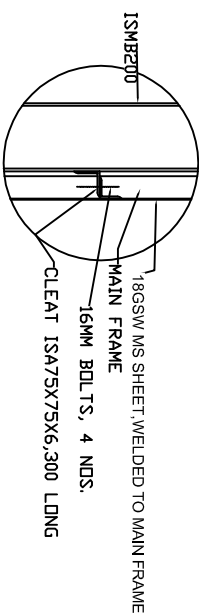


DETAILS AT 'B'

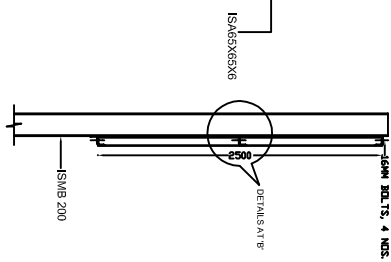


SHEET FIXING DETAIL

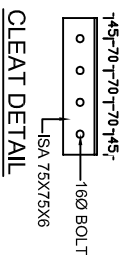


CLEAT DETAIL

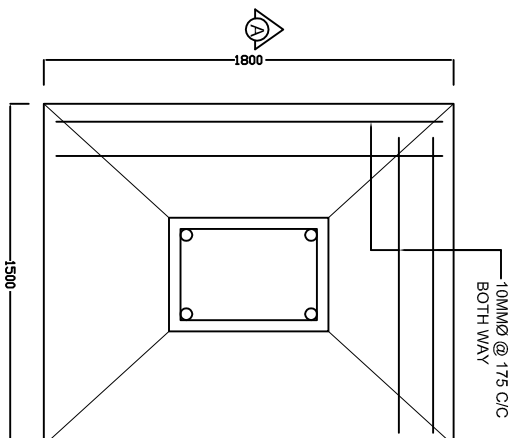


COLUMN FOOTING DETAIL

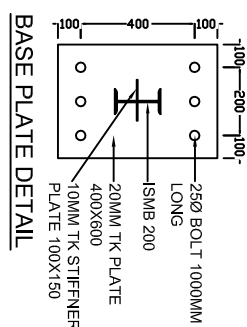

BASE PLATE DETAIL

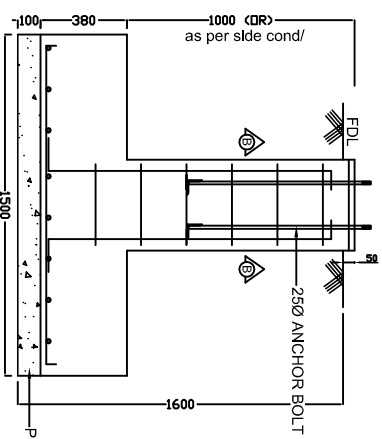

SECTION ON A-A

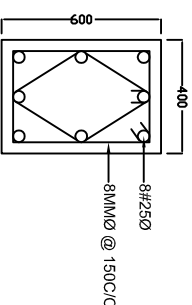

SECTION ON B-B







(A GOVERNMENT OF INDIA ENTERPRISE)

SUB TITLE

STANDARD HOARDING (SIZE 7.50MX2.50M),
SINGLE SIDE WITH BASE PLATE










DRG:- A/O H8 DATE -24.02.2015

SCALE:- NTS REV.

    

STANDARD HOARDING (SIZE 10.0MX2.50M),
SINGLE SIDE WITH BASE PLATE

DRG:- A0H10 DATE -24.02.2015
SCALE:- NTS REV.

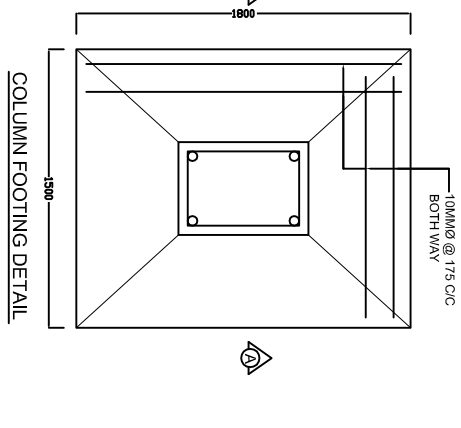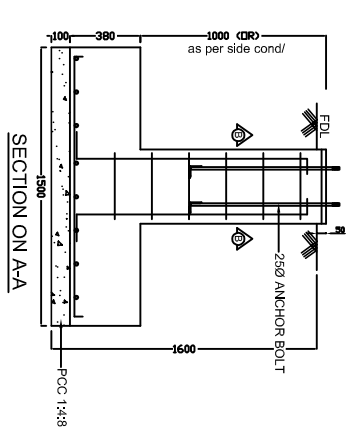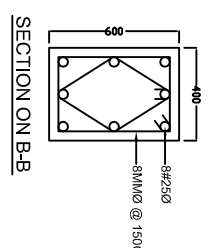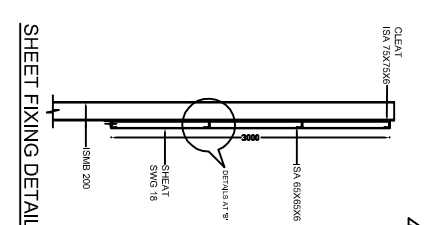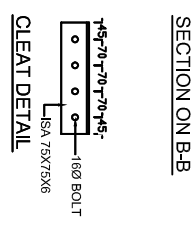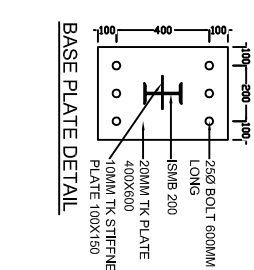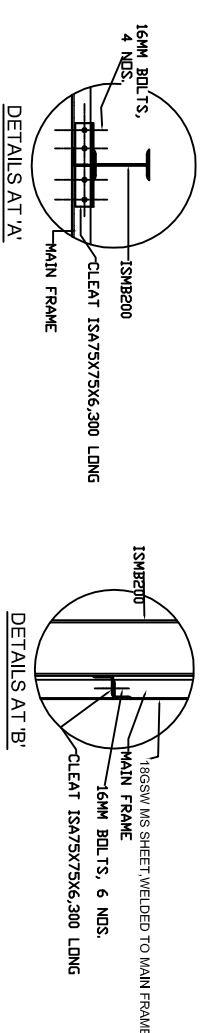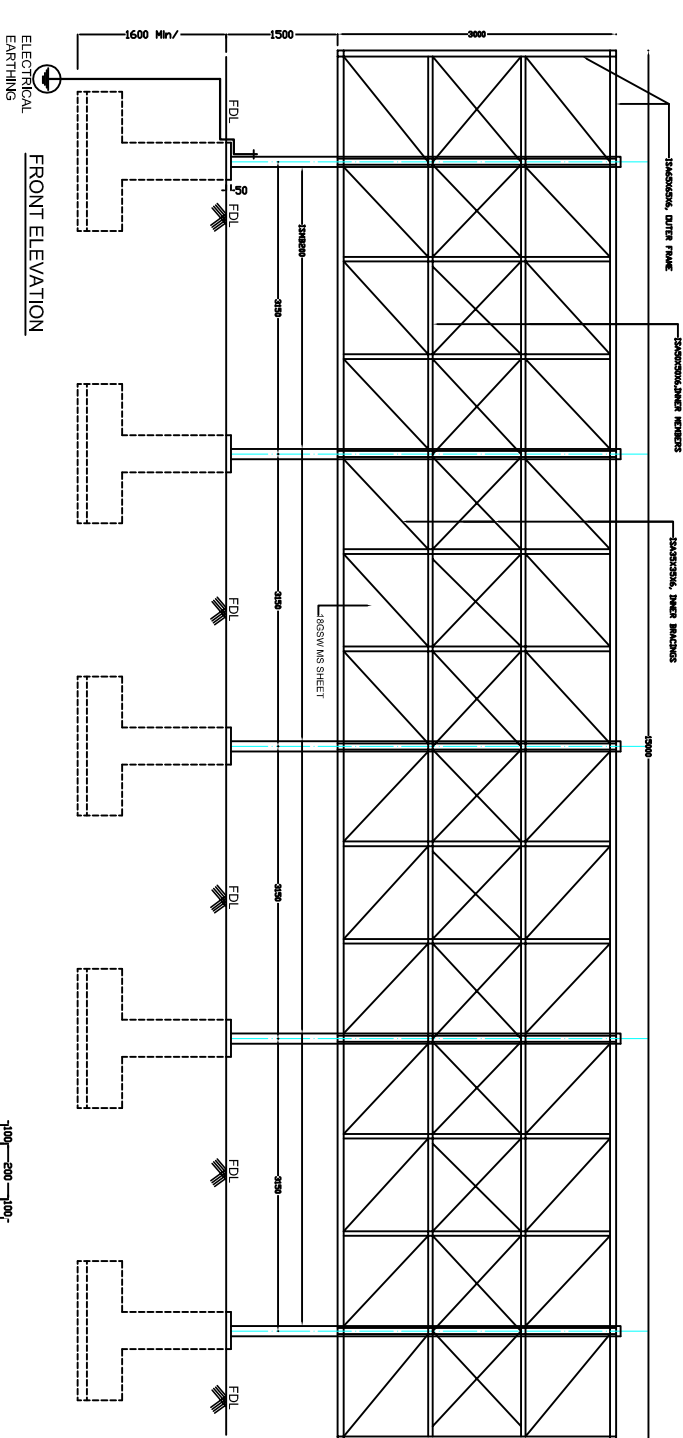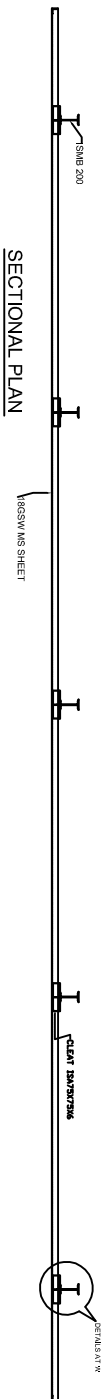

	(A) GOVERNMENT OF INDIA ENTERPRISE
SUB TITLE	STANDARD HOARDING (SIZE 15,000X3,000), SINGLE SIDE WITH BASE PLATE
DRG:- A/O H12	DATE -24.02.2015
SCALE:- NTS	REV.