


ajay
kumar

Digitally signed
by ajay kumar
Date: 2022.02.18
09:43:02 +05'30'

B0/2 BUILDING

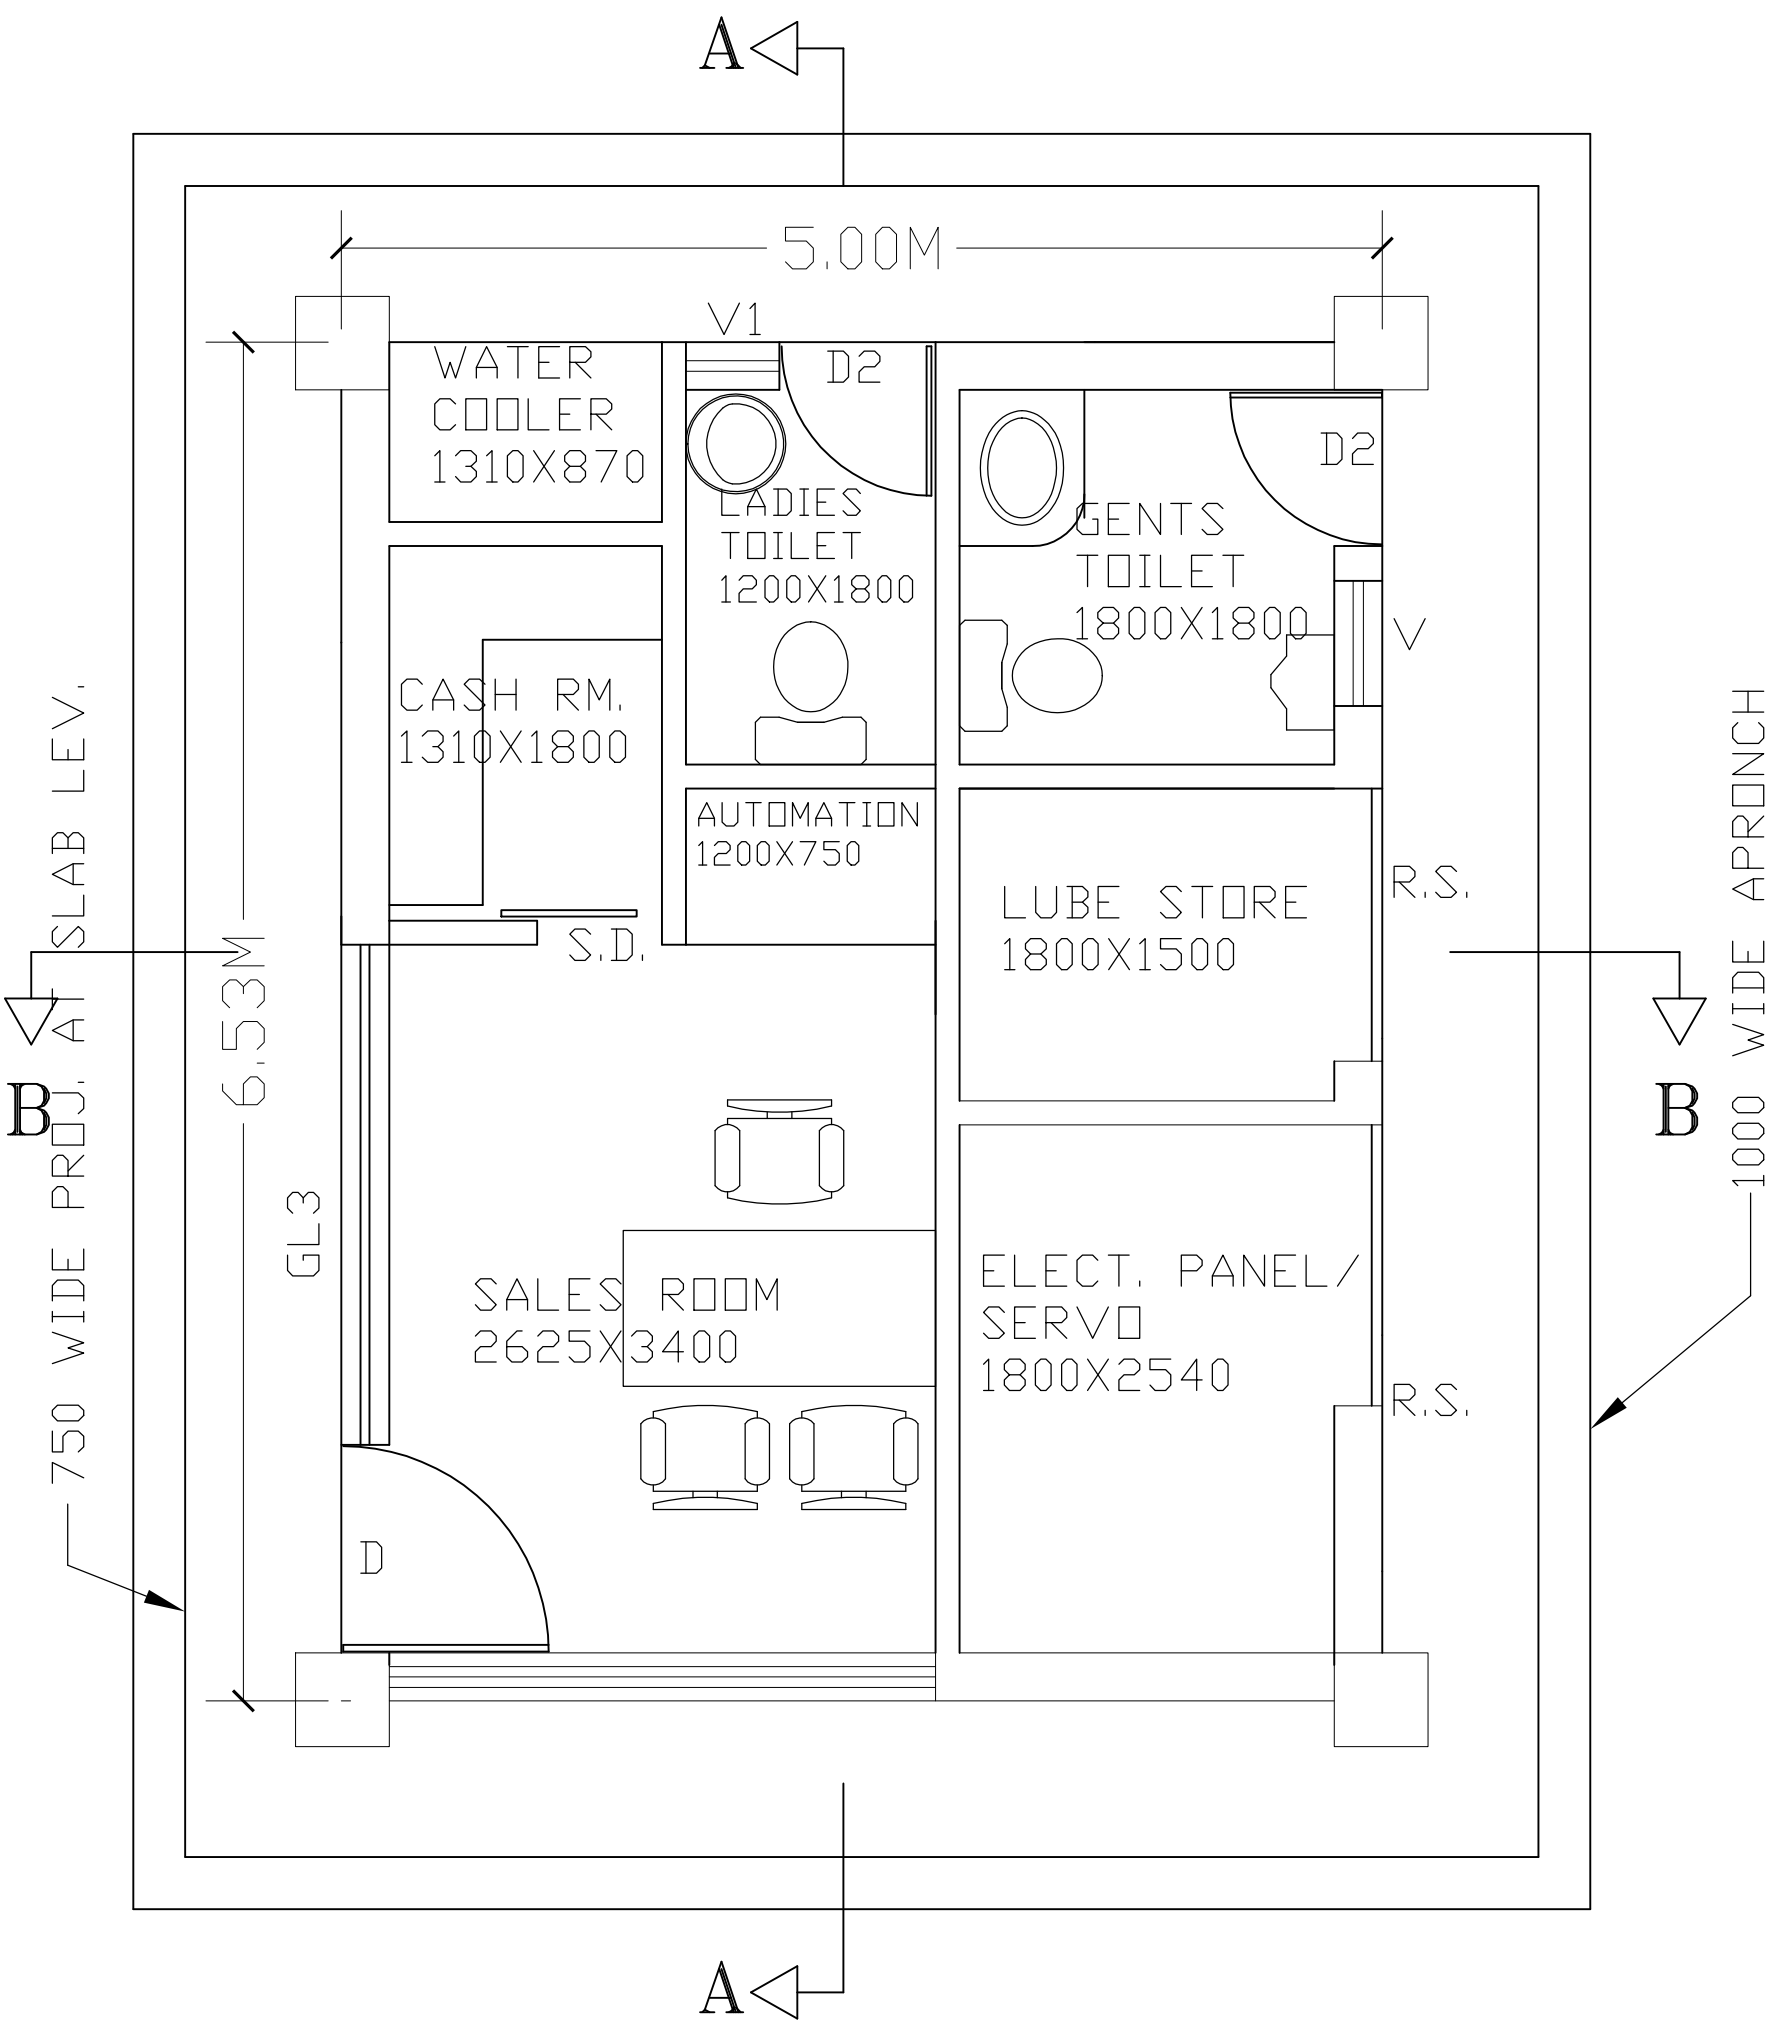


GROUND FLOOR LAYOUT PLAN

GROUND FLOOR LAYOUT PLAN


SCHEDULE OF DOORS & WINDOWS					
S.N	TYPE	SIZE	SILL	LINTEL	REMARKS
1	D	1000 X 2700	-	2700	
2	D1	900 X 2100	-	2100	
3	D2	750 X 2100	-	2700	
4	GL1	2625 X 2500	200	2700	
5	GL2	2250 X 2500	200	2700	
5	GL3	2400 X 2500	200	2700	
6	W	1000 X 1200	900	2100	
7	V	600 X 600	1500	2100	
8	V1	450 X 450	1650	2100	
9	R.S.	1200 X 2100	900	2100	

ajay kumar


Digitally signed by
ajay kumar
Date: 2022.02.18
09:41:15 +05'30'

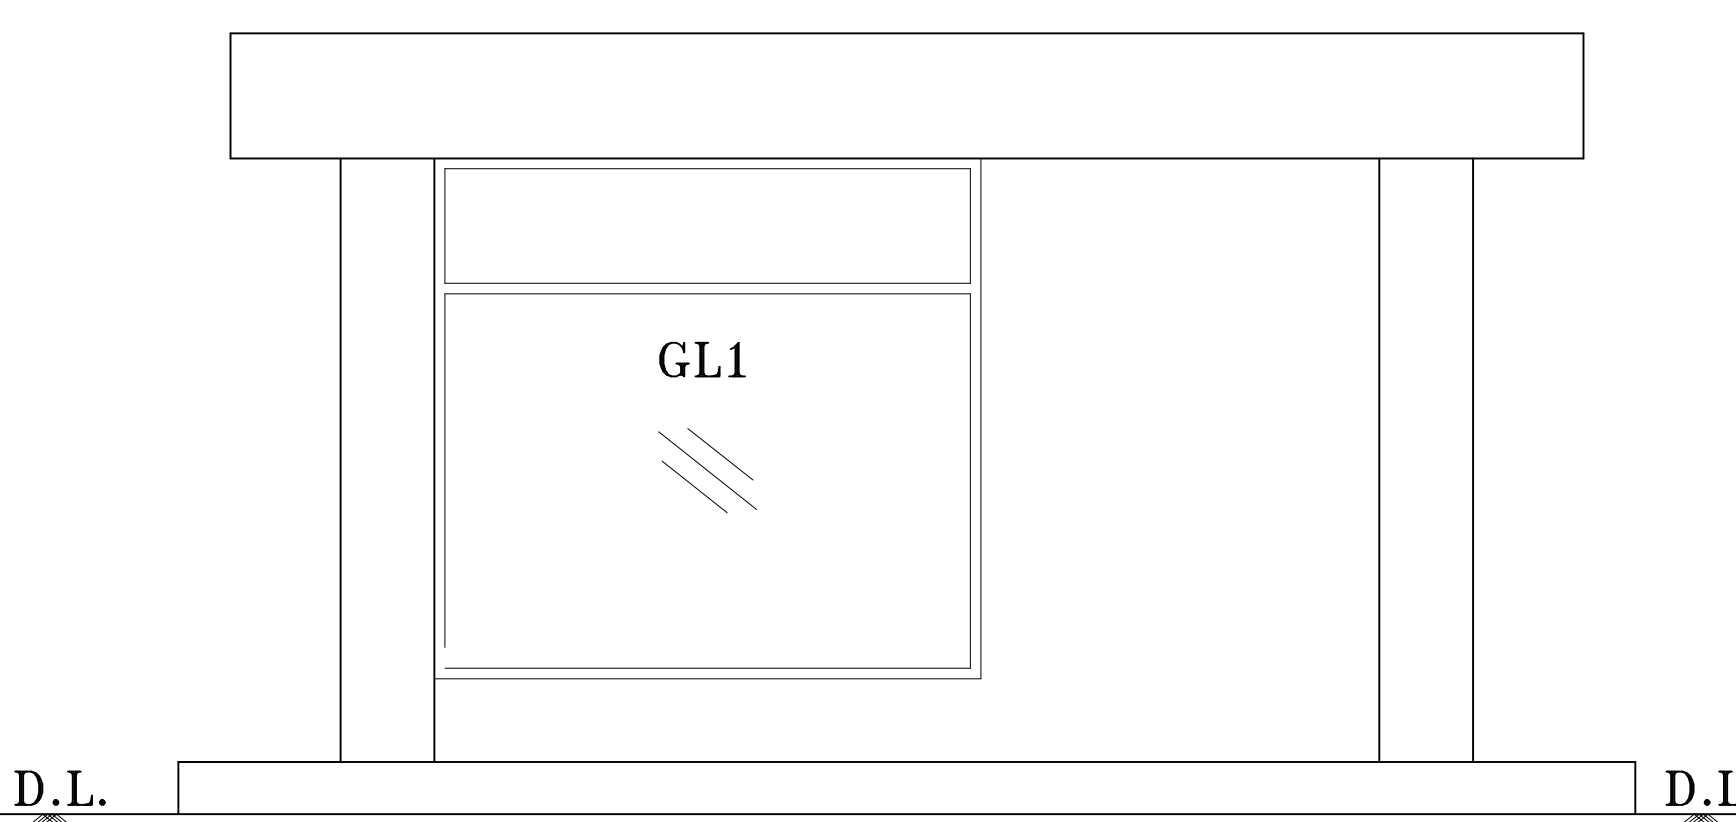


FRONT ELEVATION

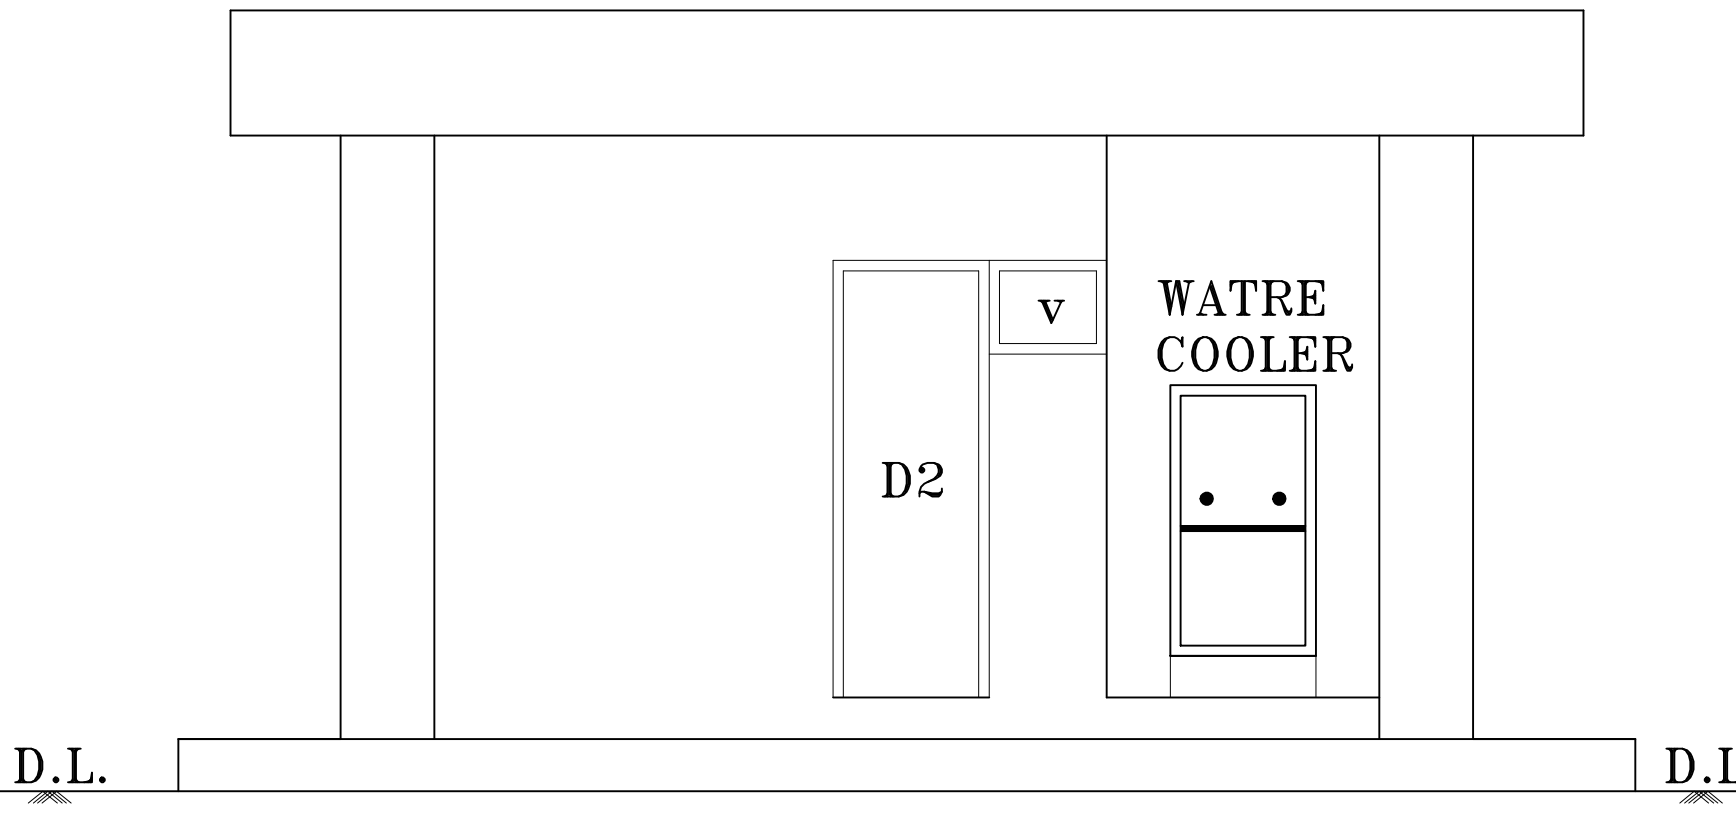


REAR ELEVATION

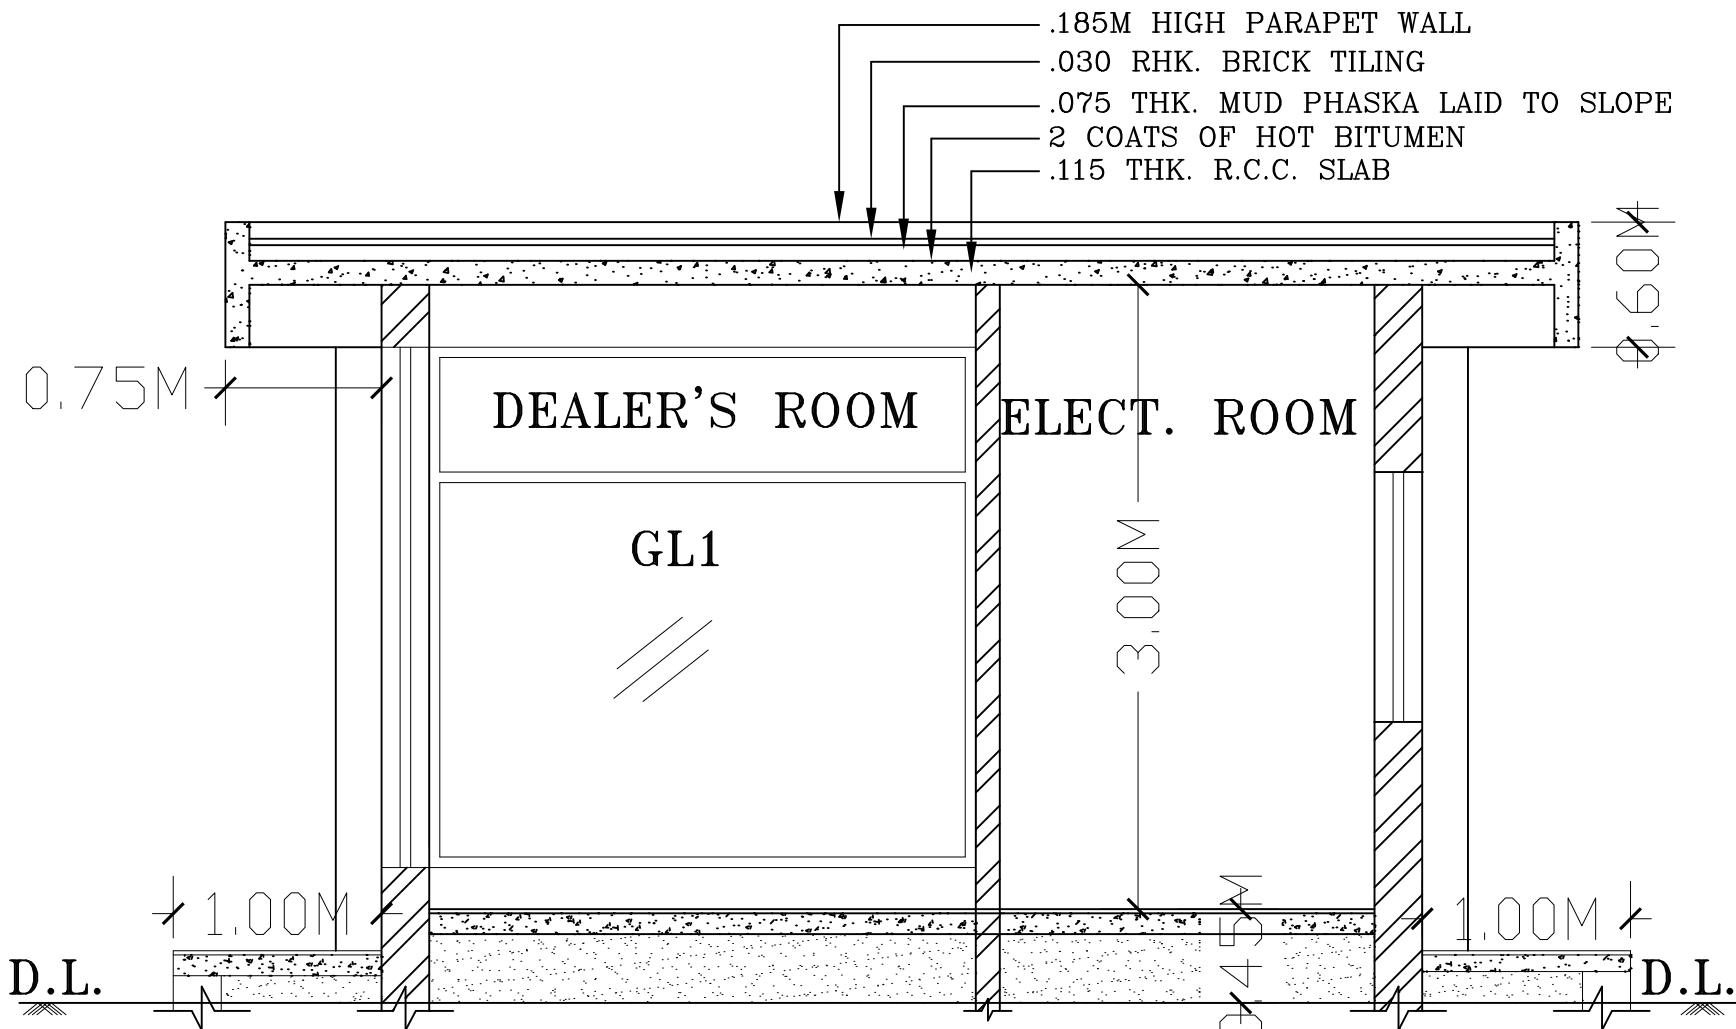


SECTION B-B

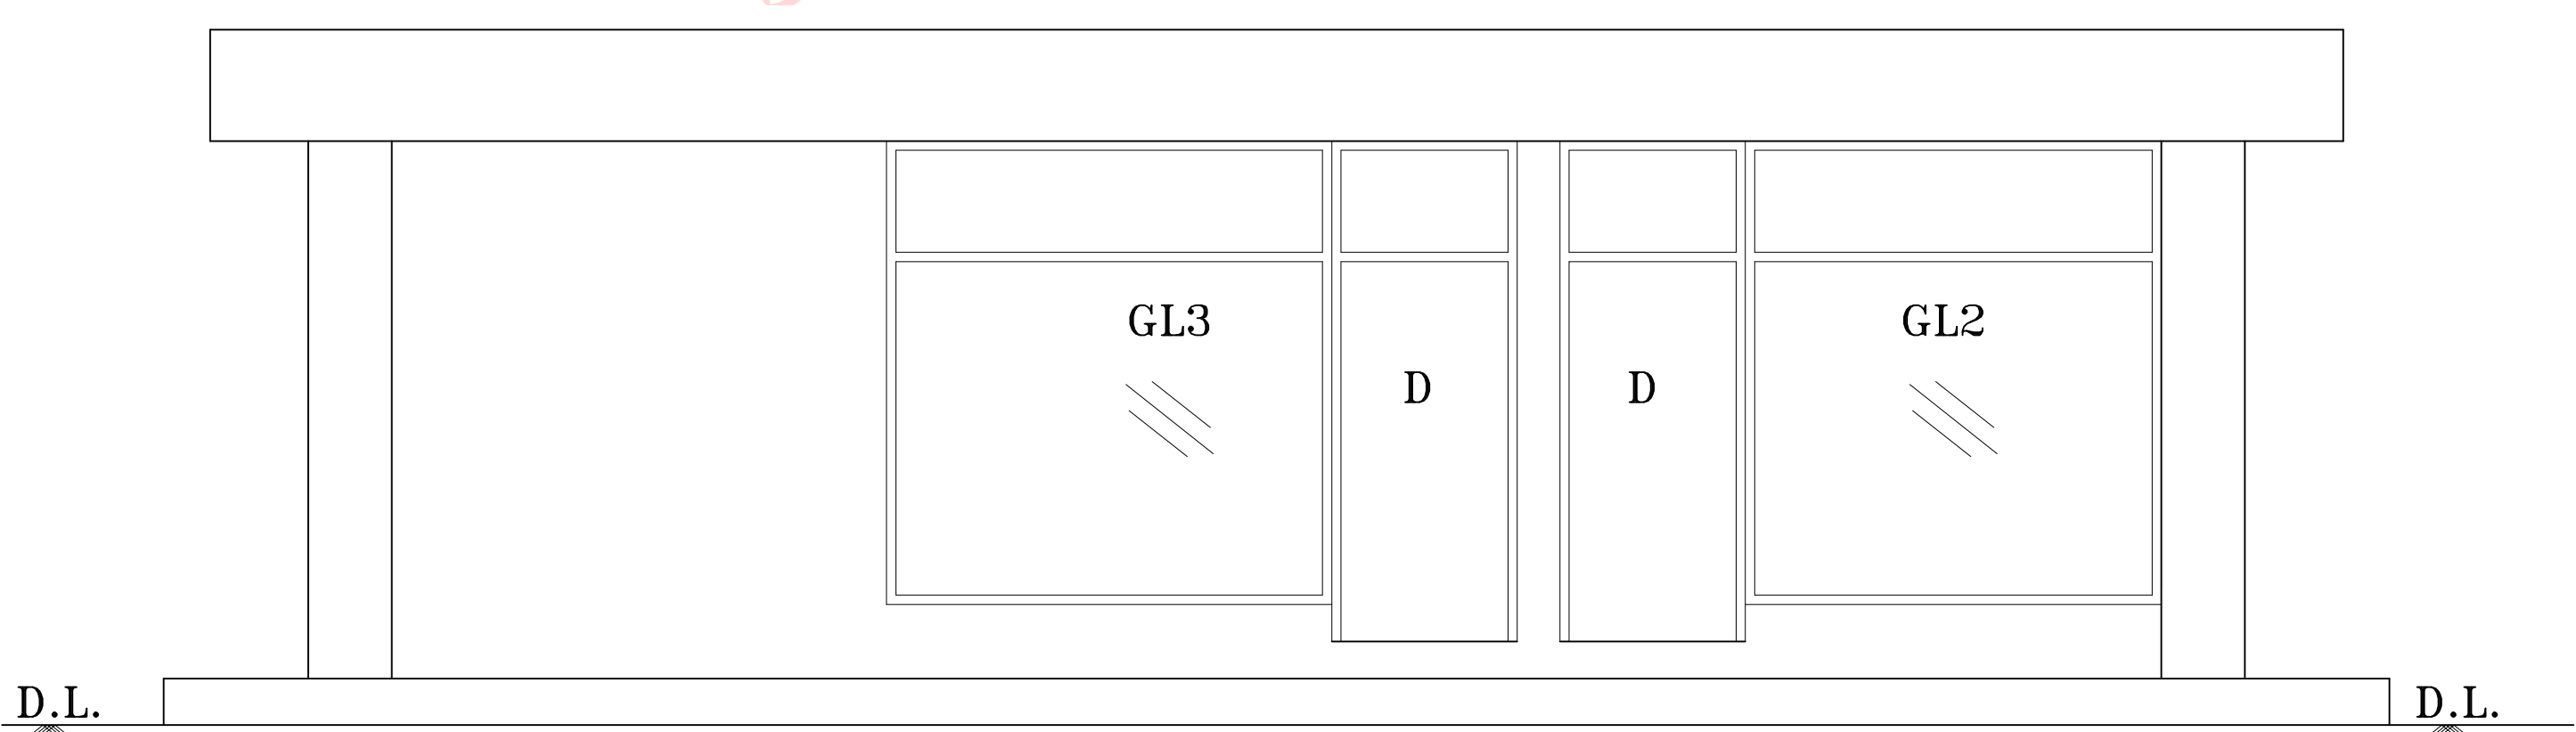

LEFT SIDE ELEVATION

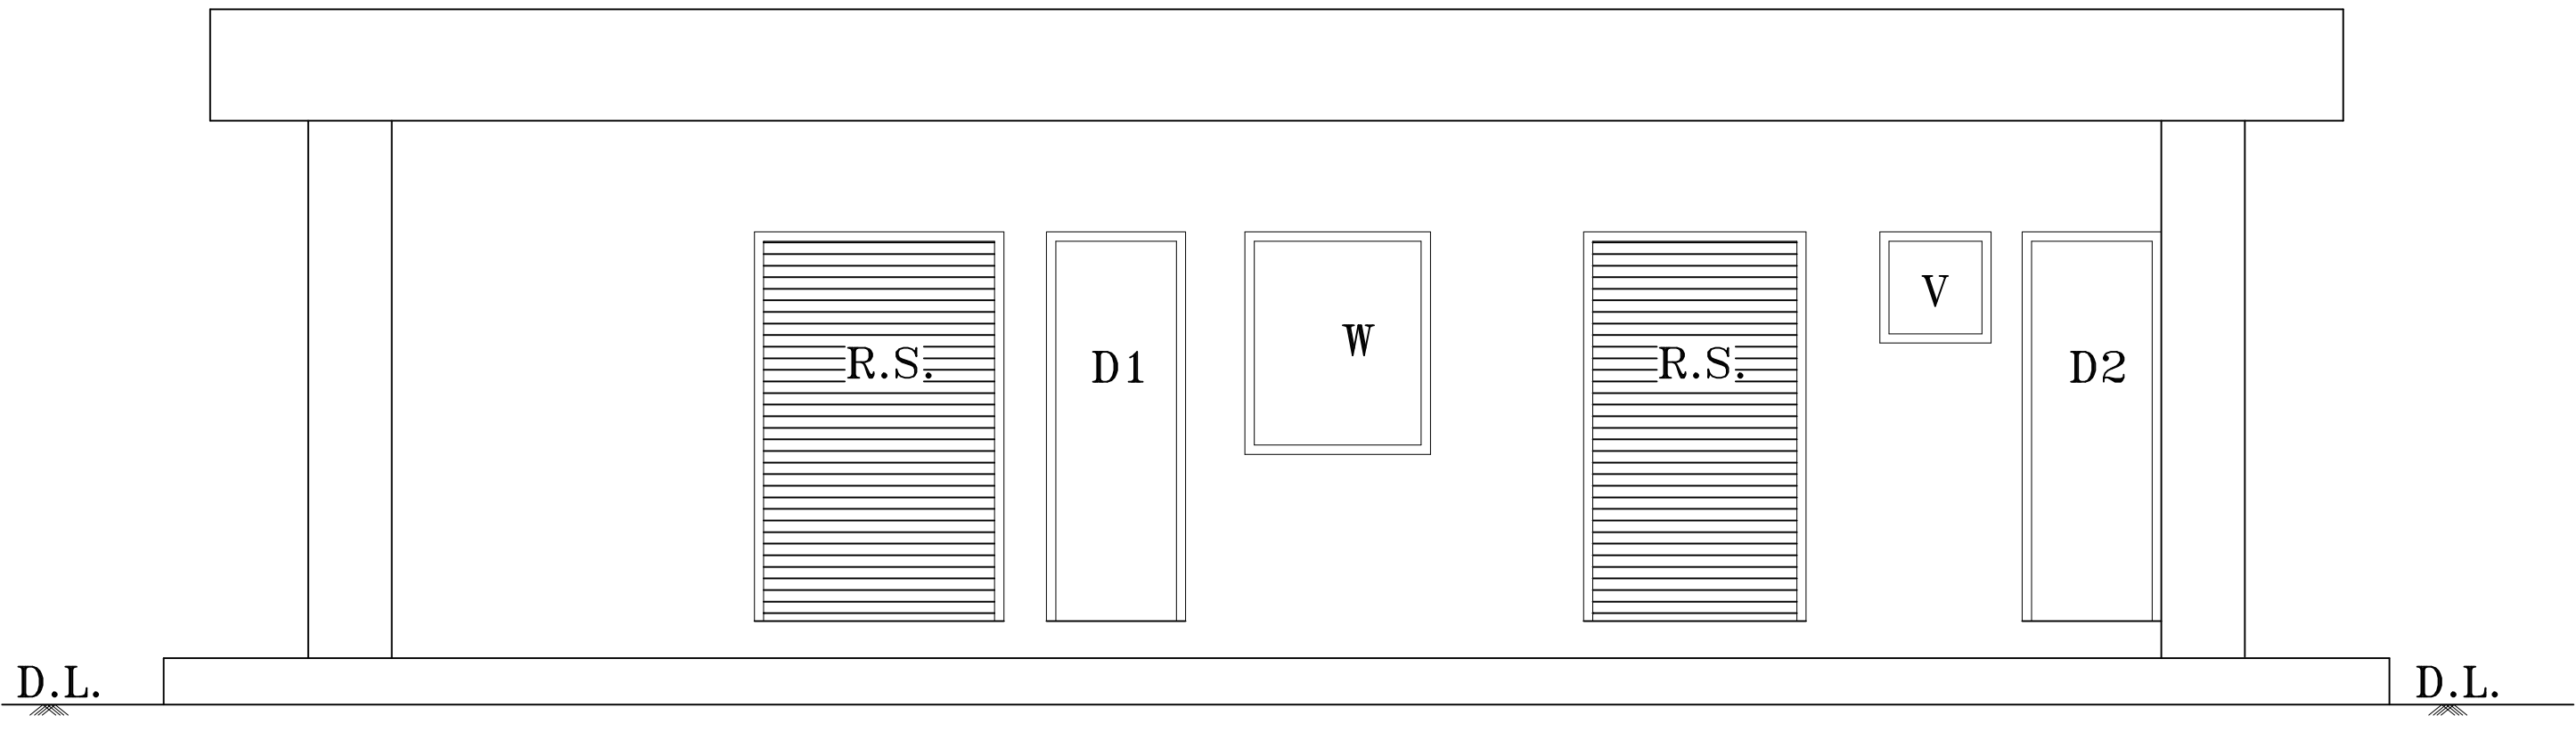

RIGHT SIDE ELEVATION

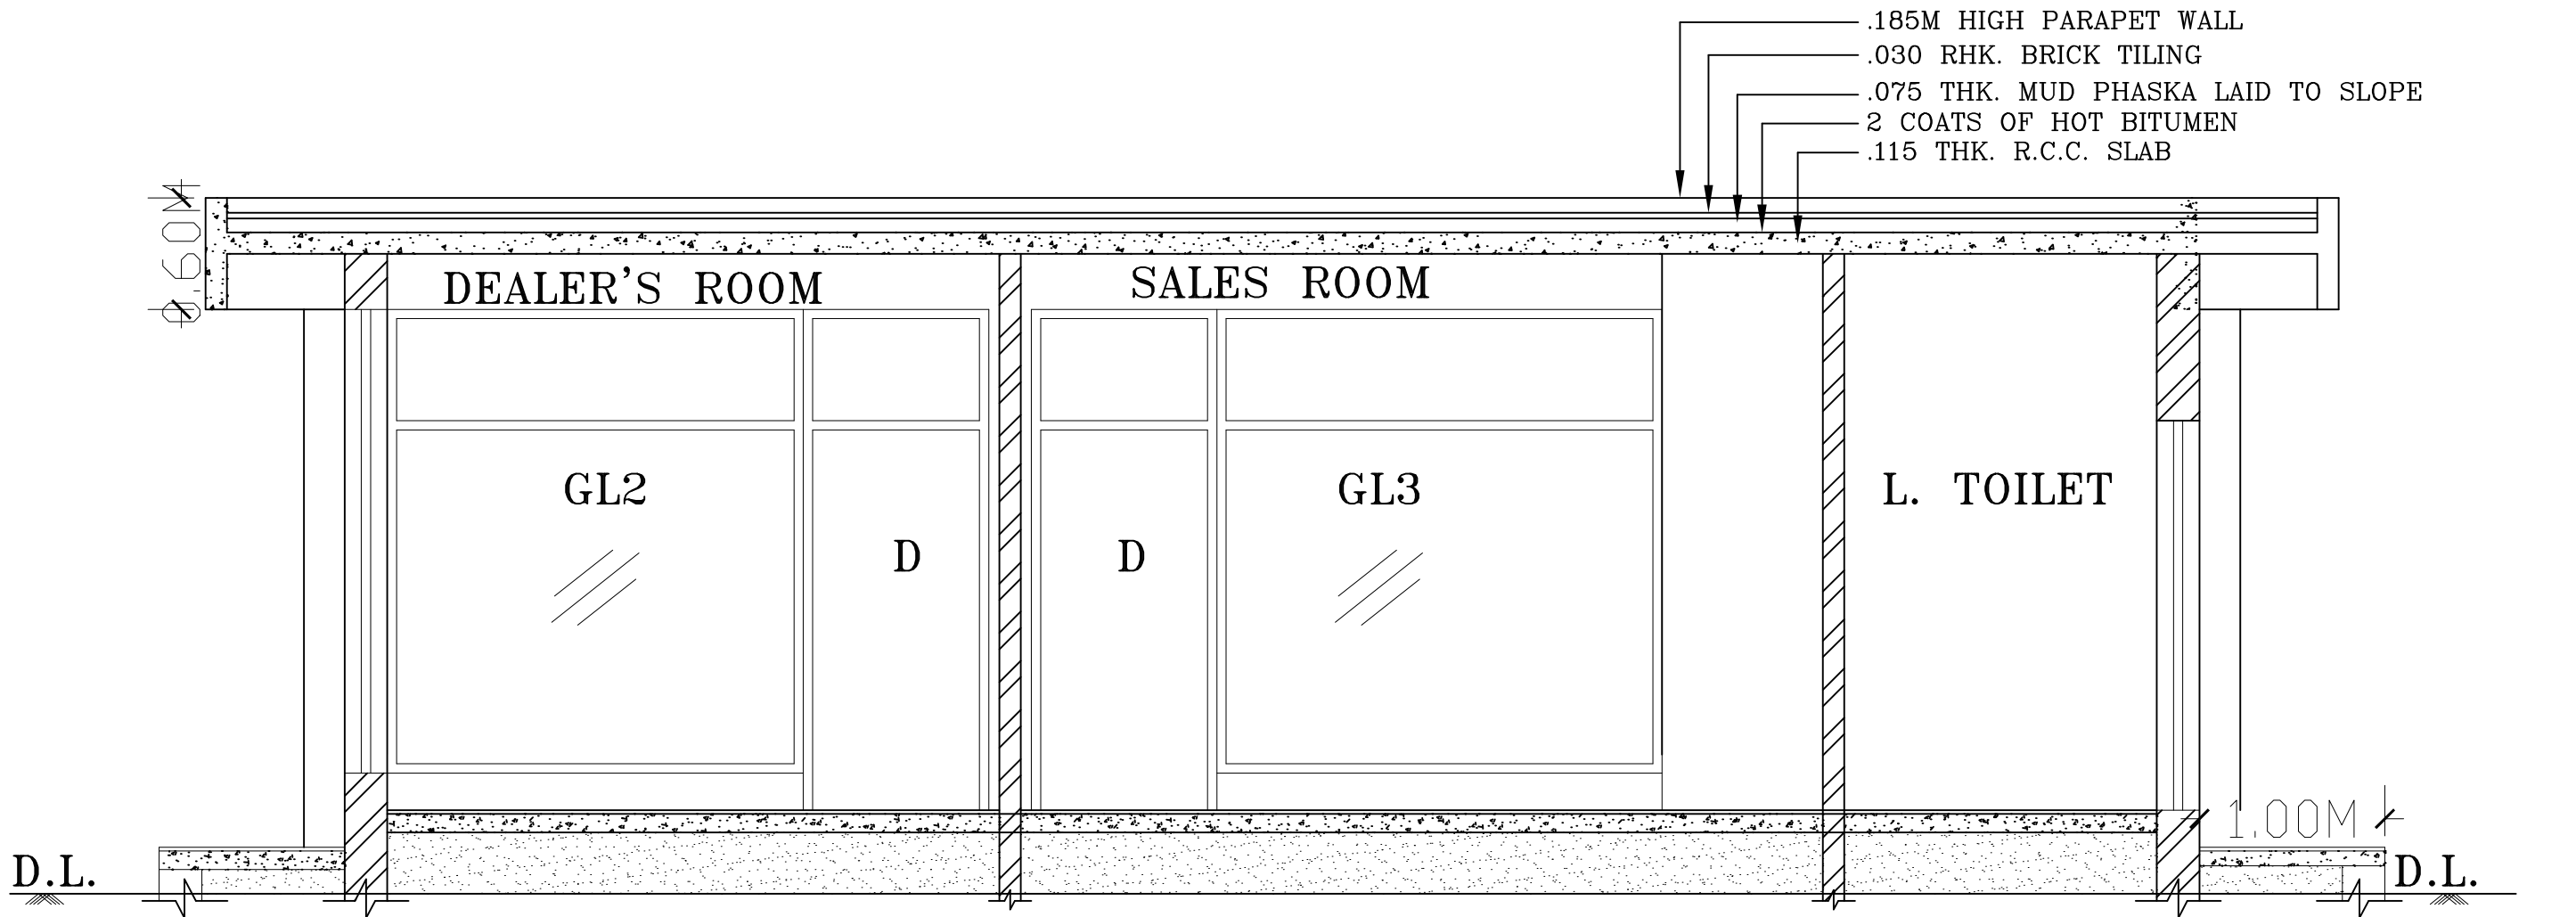

SECTION A-A

1. B0/2 BUILDING FOR RURAL AND URBAN ROS (IF SPACE CONSTRAINT)
2. FOUNDATION TO BE DESIGNED AS PER SPECIFIC SITE CONDITIONS.

CLIENT:- BHARAT PETROLEUM CORP. LTD.

DATED : 18-02-2022


CHECKED BY:-

TITLE :-BUILDING (B0/2)FOR RURAL AND URBAN LAYOUT PLAN, ELEVATION & SECTION

ajay
kumar


Digitally signed
by ajay kumar
Date: 2022.02.18
09:42:41 +05'30'

B0 BUILDING

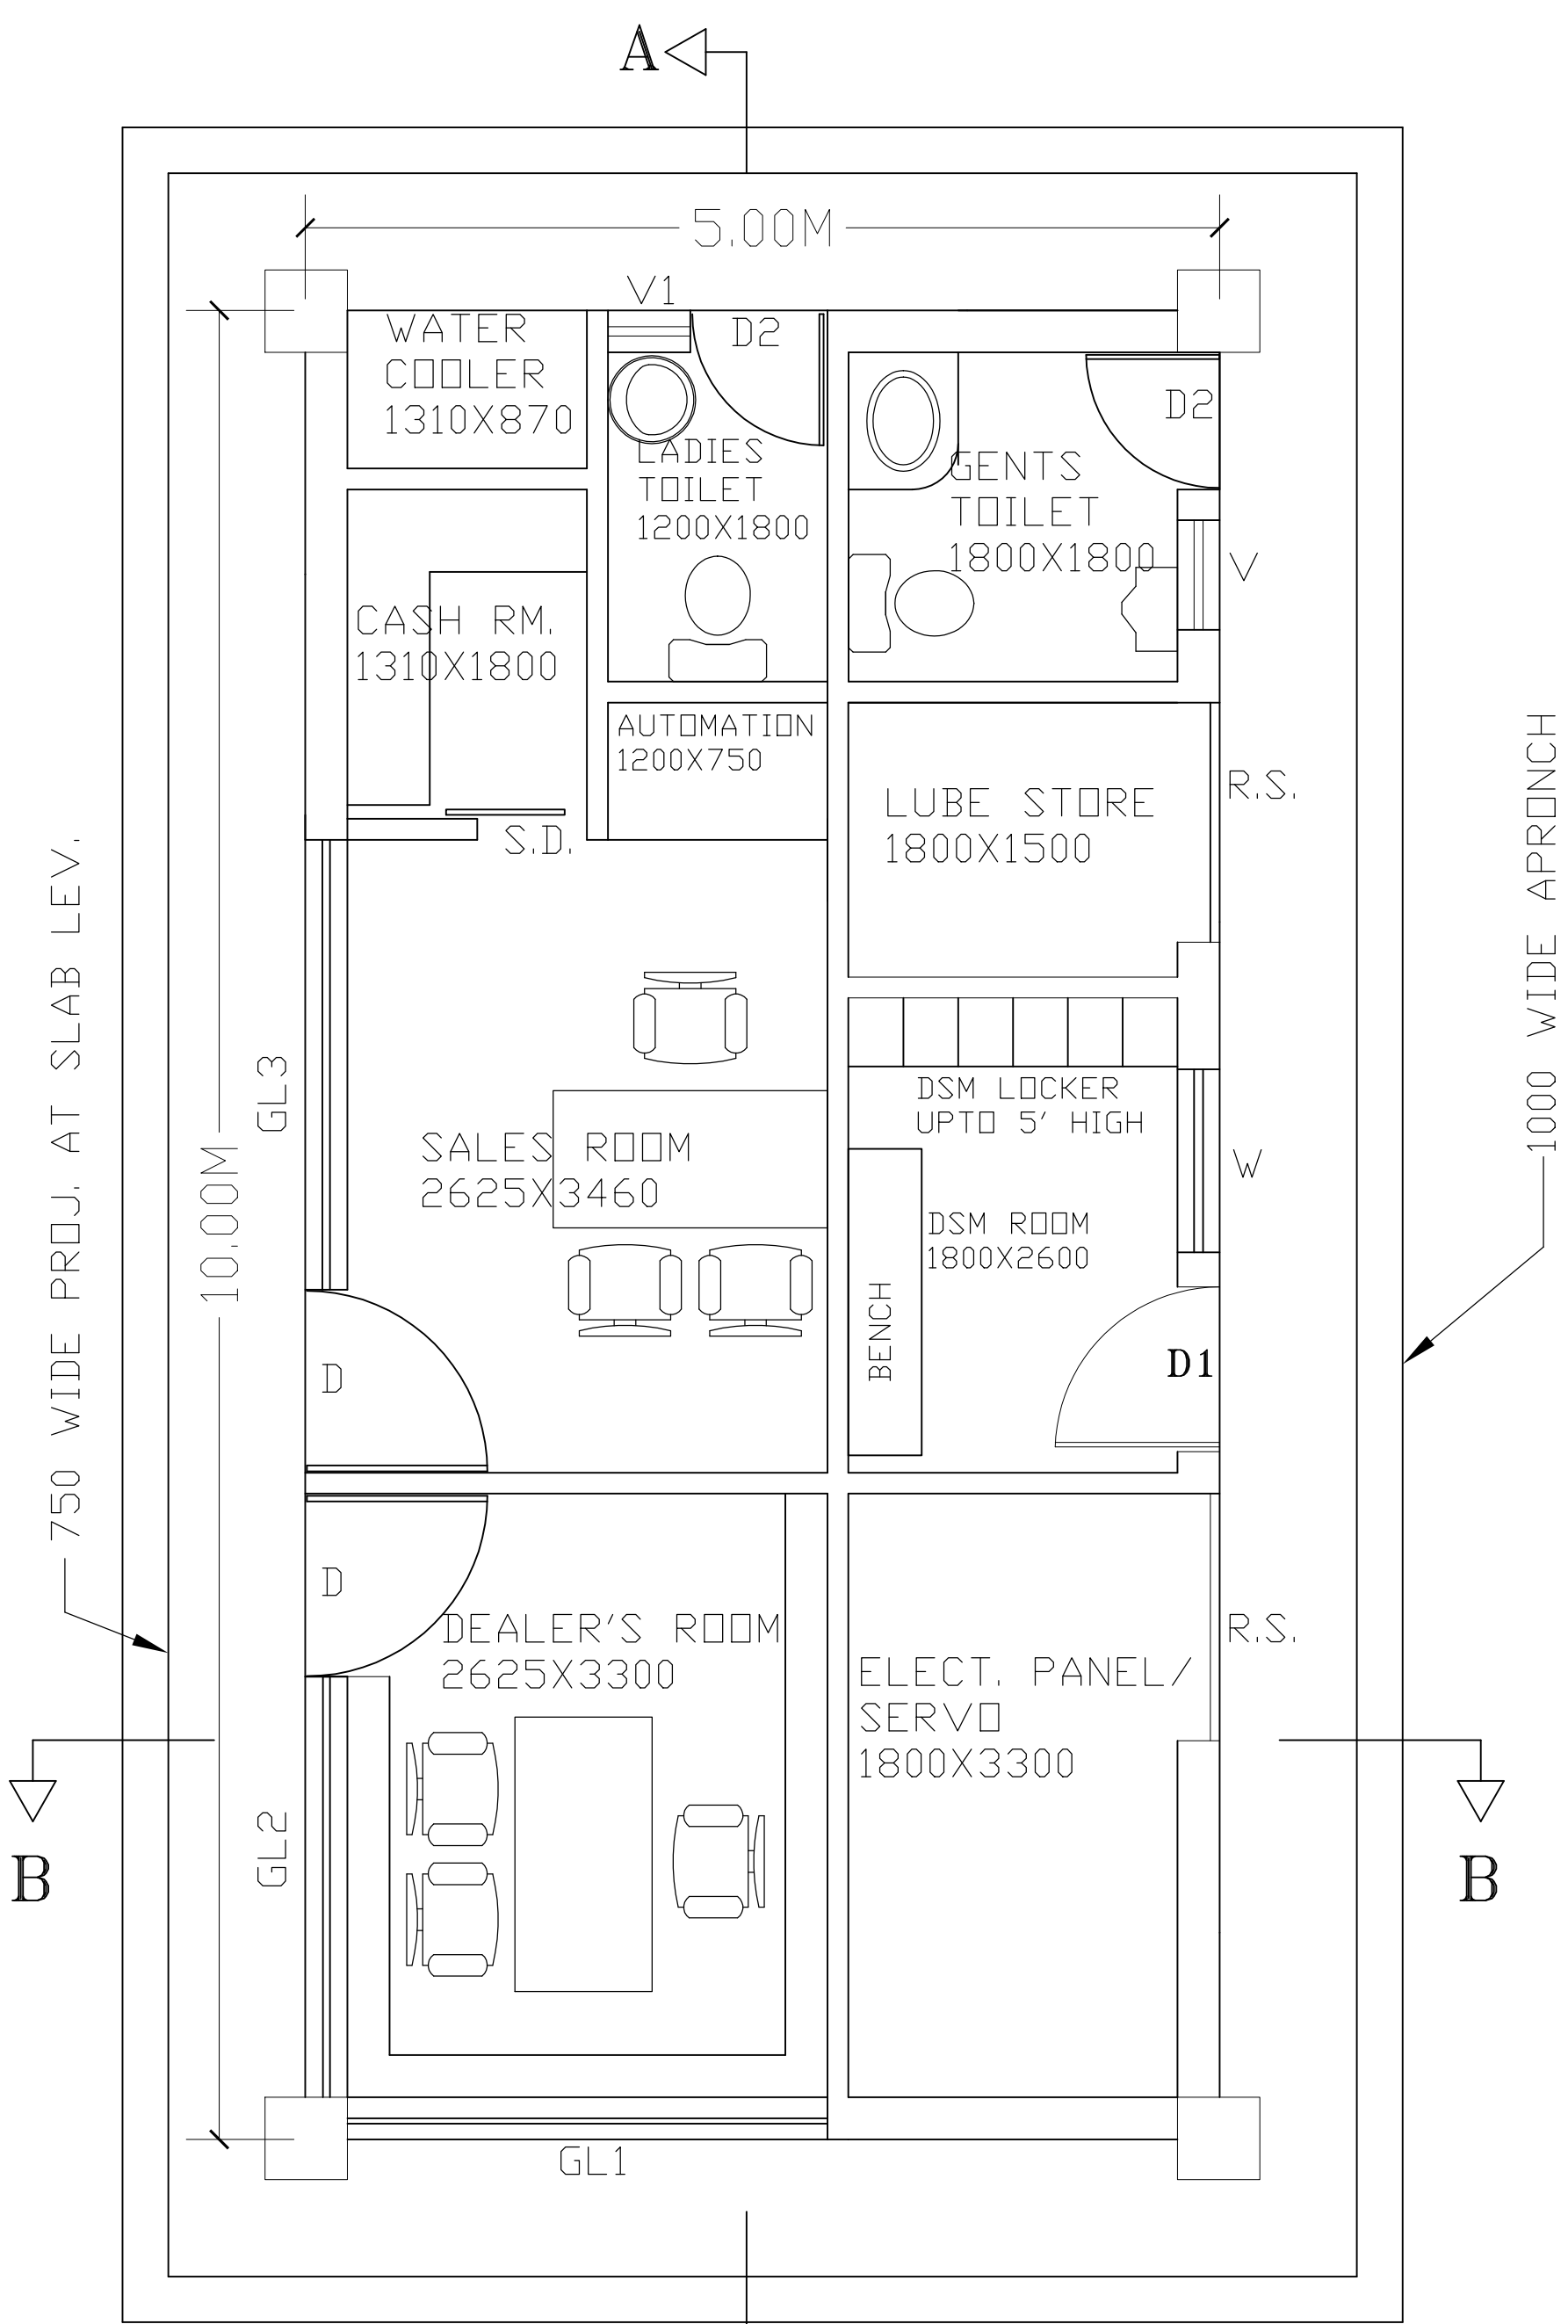


GROUND FLOOR LAYOUT PLAN


SCHEDULE OF DOORS & WINDOWS					
S.N	TYPE	SIZE	SILL	LINTEL	REMARKS
1	D	1000 X 2700	—	2700	
2	D1	900 X 2100	—	2100	
3	D2	750 X 2100	—	2700	
4	GL1	2625 X 2500	200	2700	
5	GL2	2250 X 2500	200	2700	
5	GL3	2400 X 2500	200	2700	
6	W	1000 X 1200	900	2100	
7	V	600 X 600	1500	2100	
8	V1	450 X 450	1650	2100	
9	R.S.	1200 X 2100	900	2100	

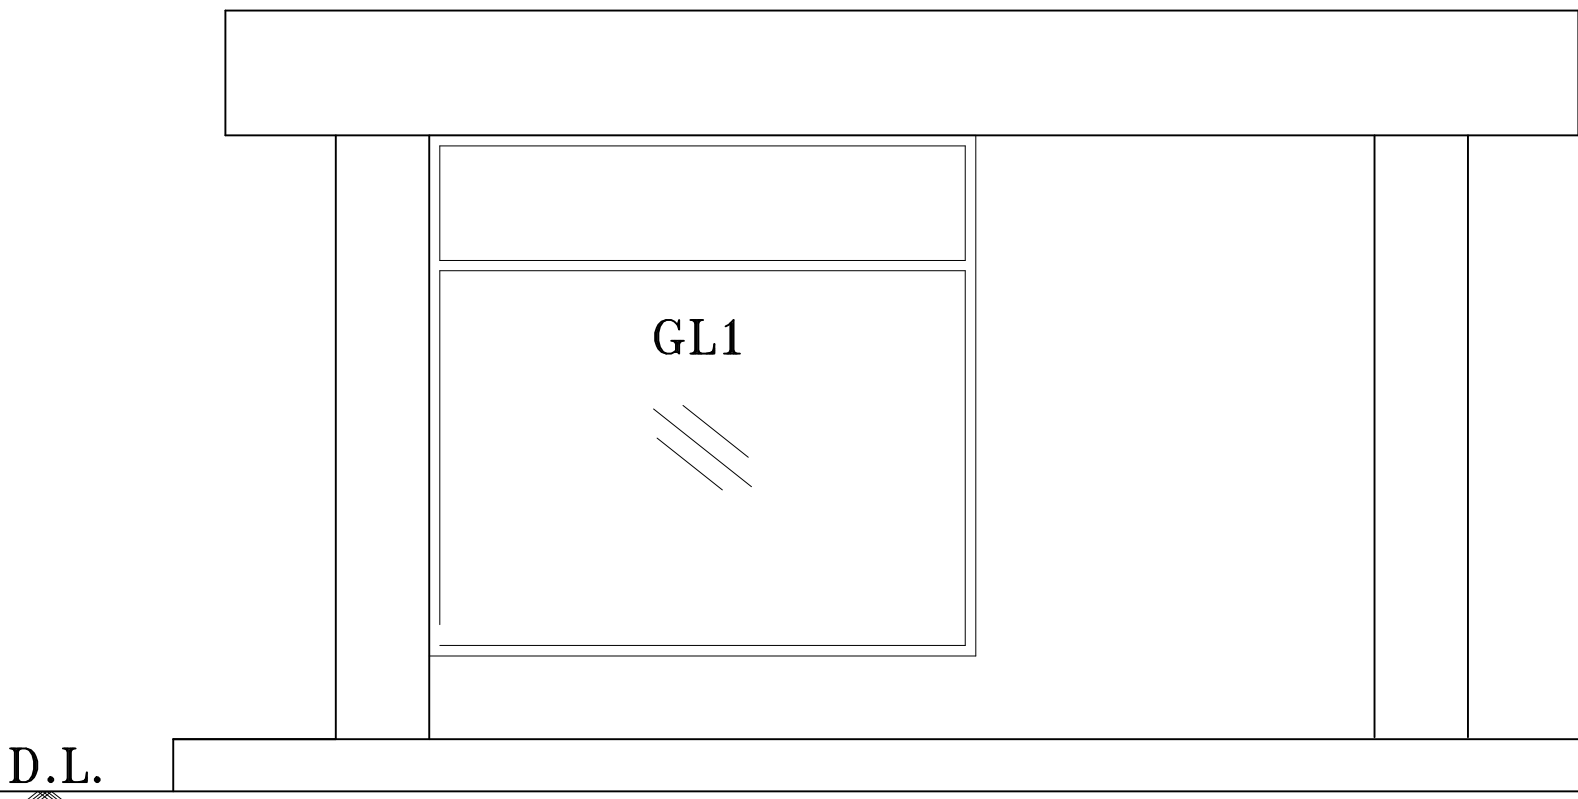


FRONT ELEVATION

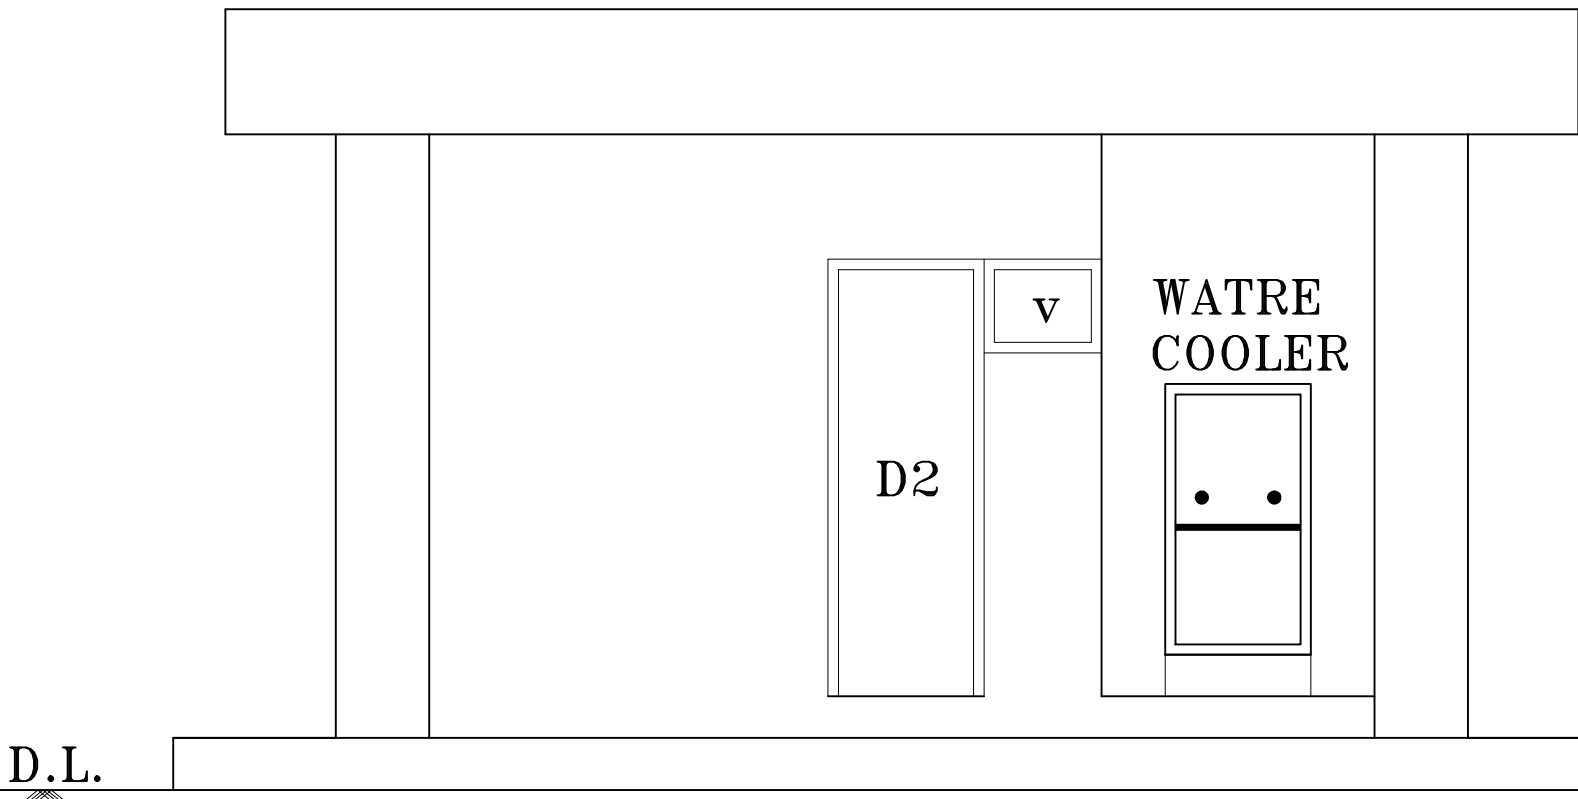


REAR ELEVATION

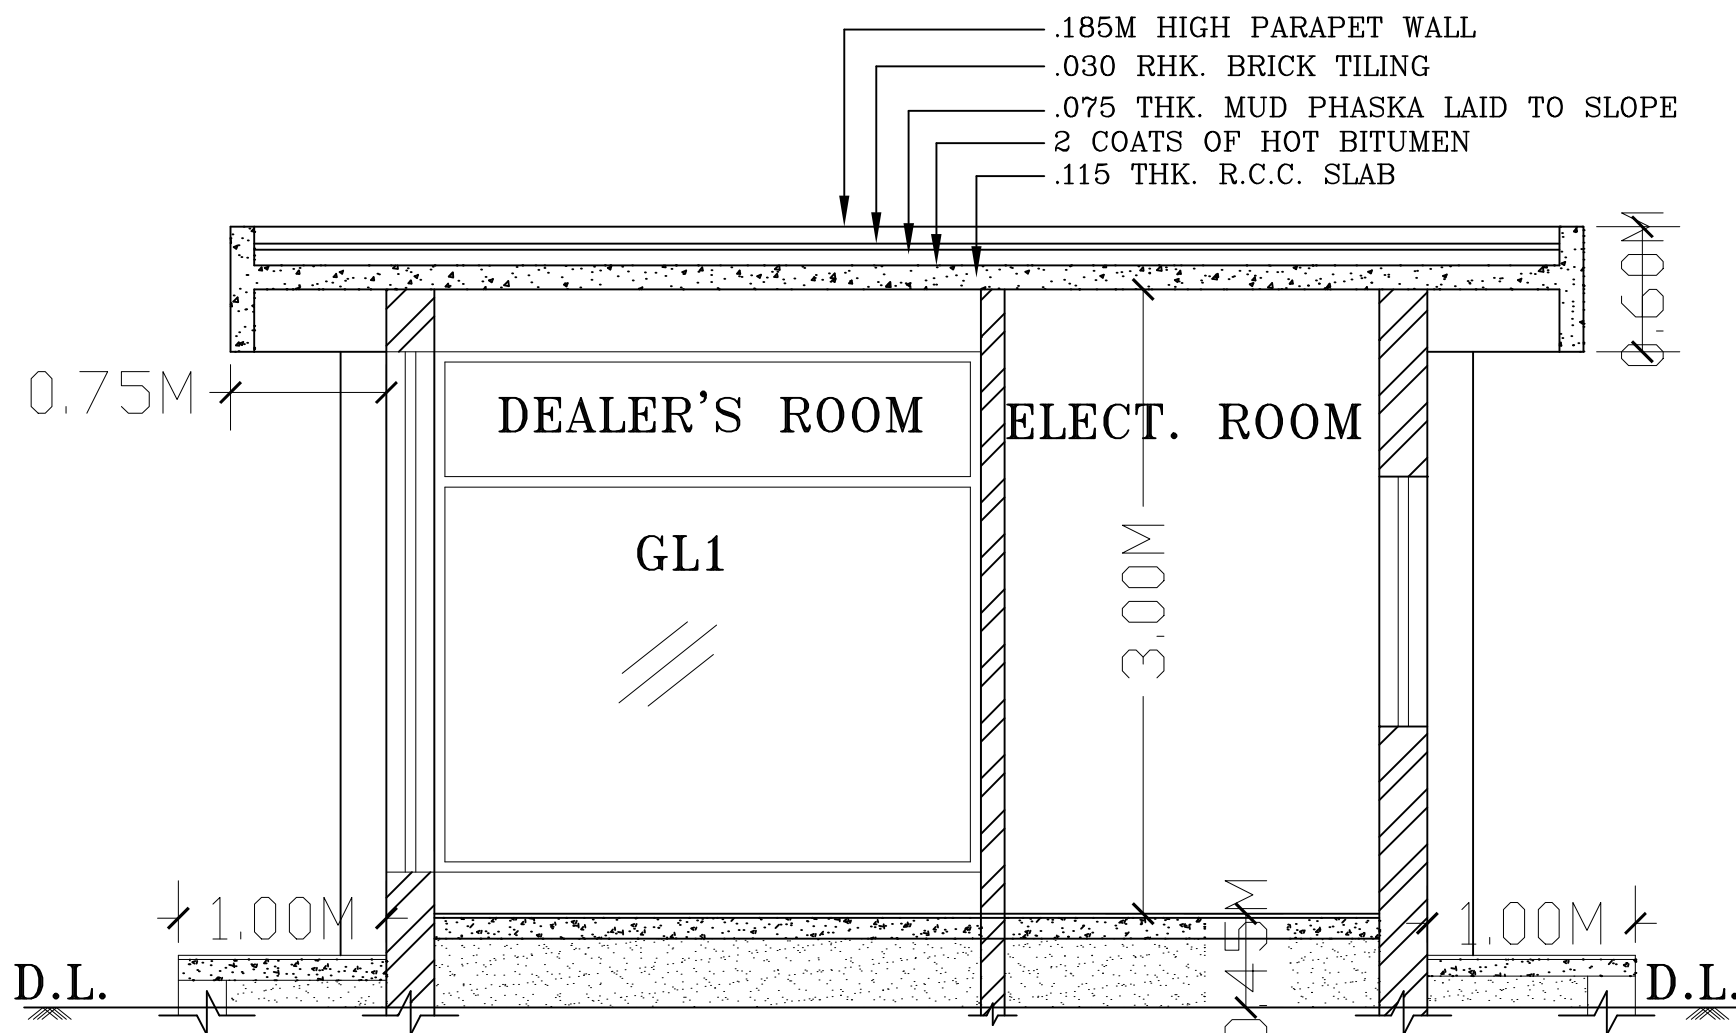


SECTION B-B

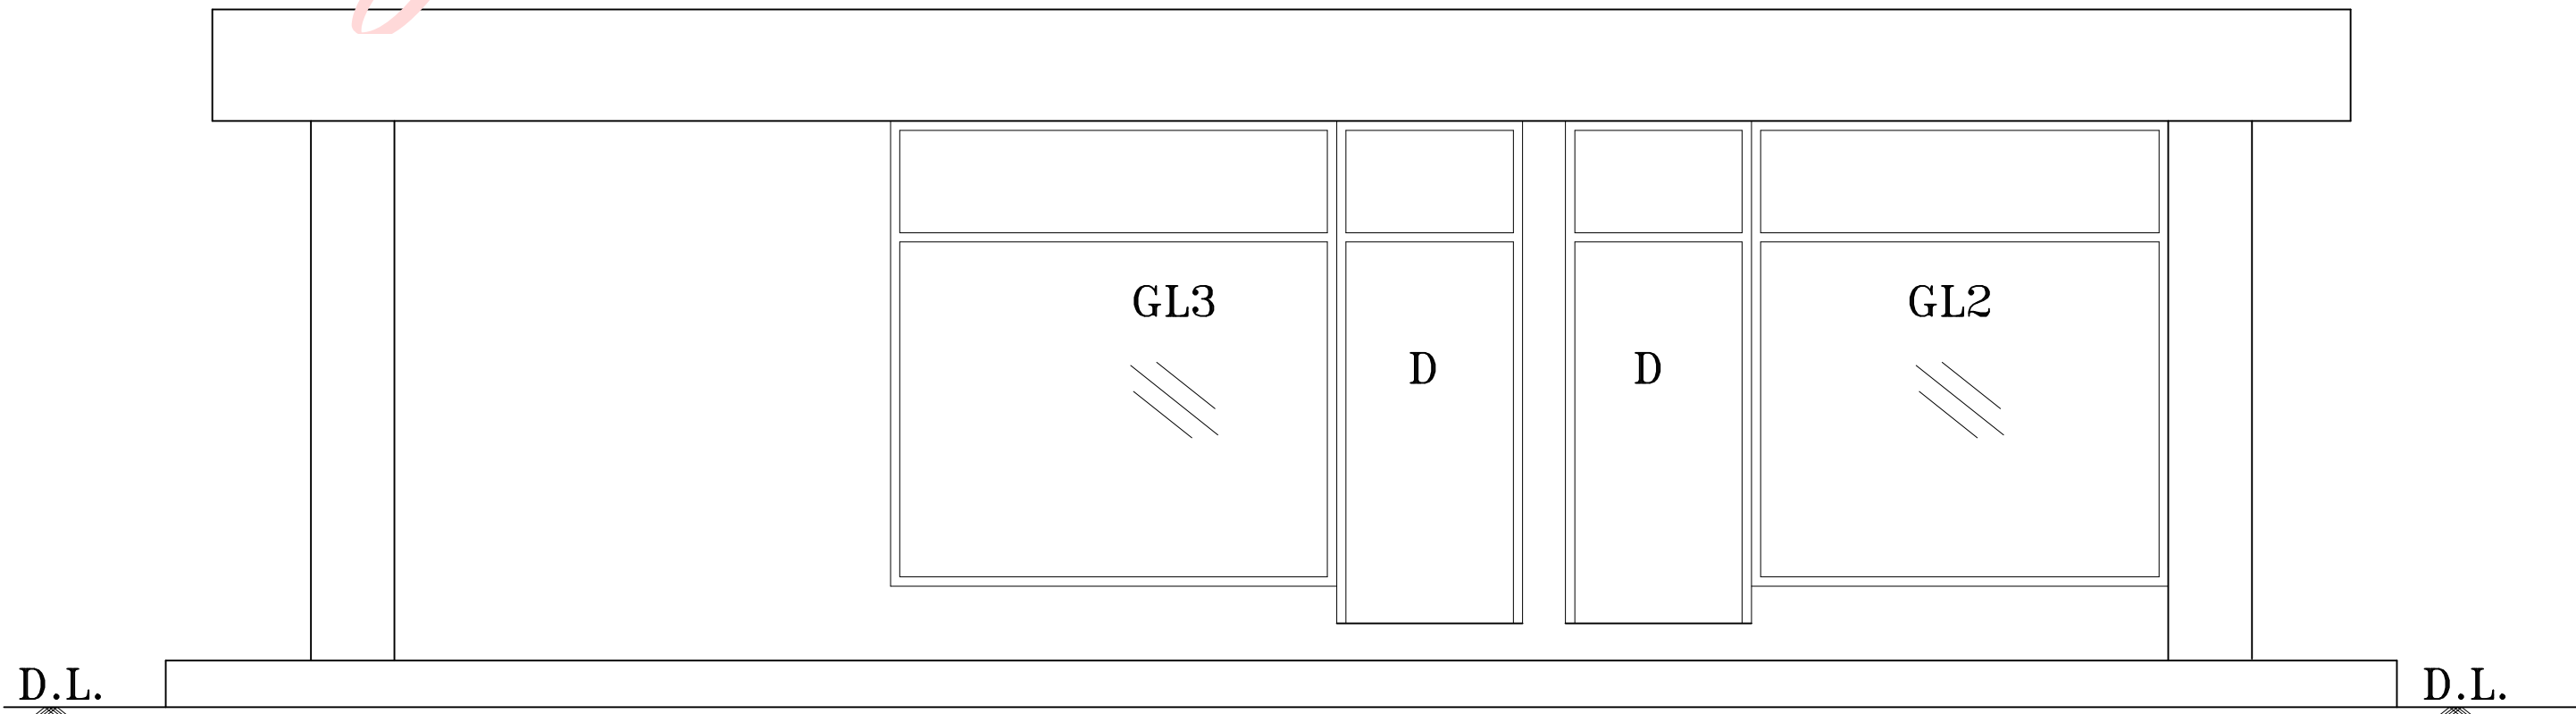

LEFT SIDE ELEVATION

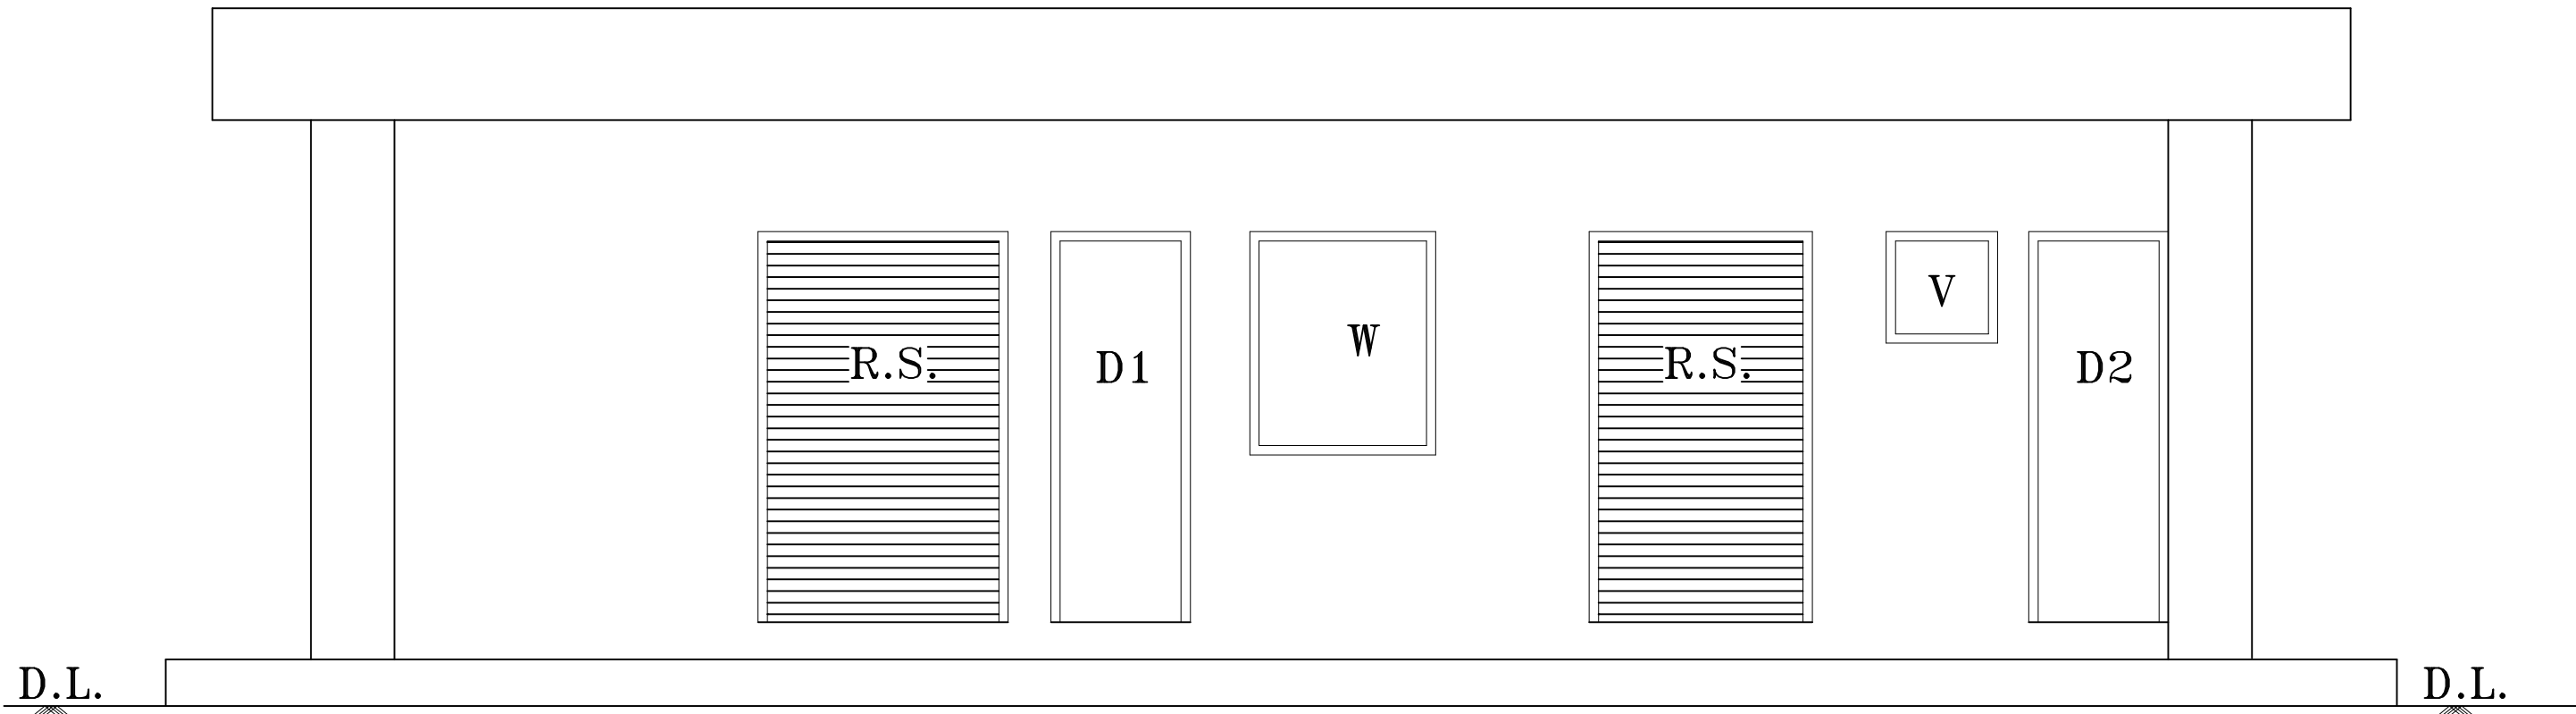

RIGHT SIDE ELEVATION

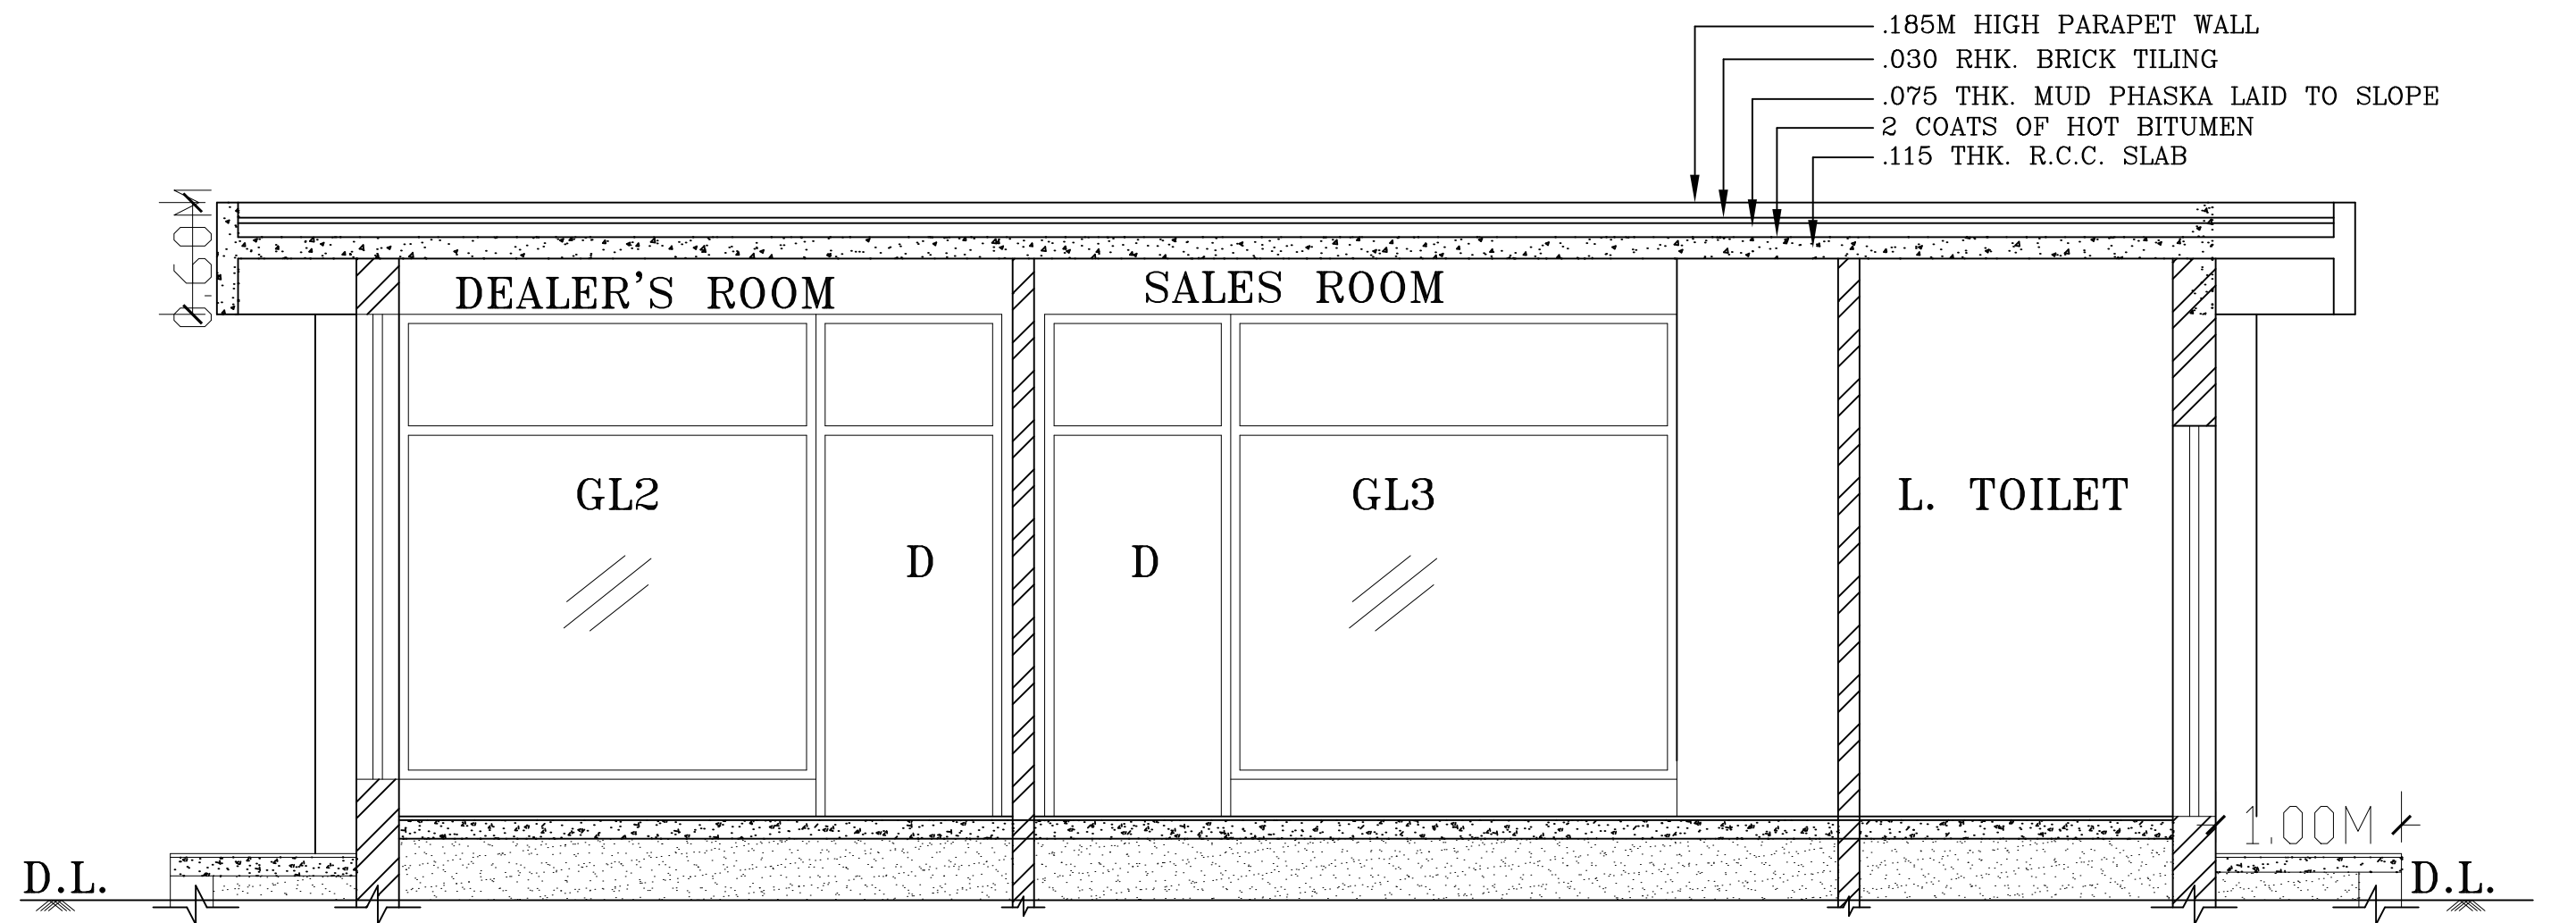

SECTION A-A

1. B0 BUILDING FOR NORMAL ROs IN A/B/C
2. FOUNDATION TO BE DESIGNED AS PER SPECIFIC SITE CONDITIONS.

CLIENT:— BHARAT PETROLEUM CORP. LTD.

DATED : 18-02-2022


CHECKED BY:—

TITLE :— B0 BUILDING LAYOUT PLAN, ELEVATION & SECTION

ajay
kumar


Digitally signed
by ajay kumar
Date: 2022.02.18
09:42:22 +05'30'

B1 BUILDING

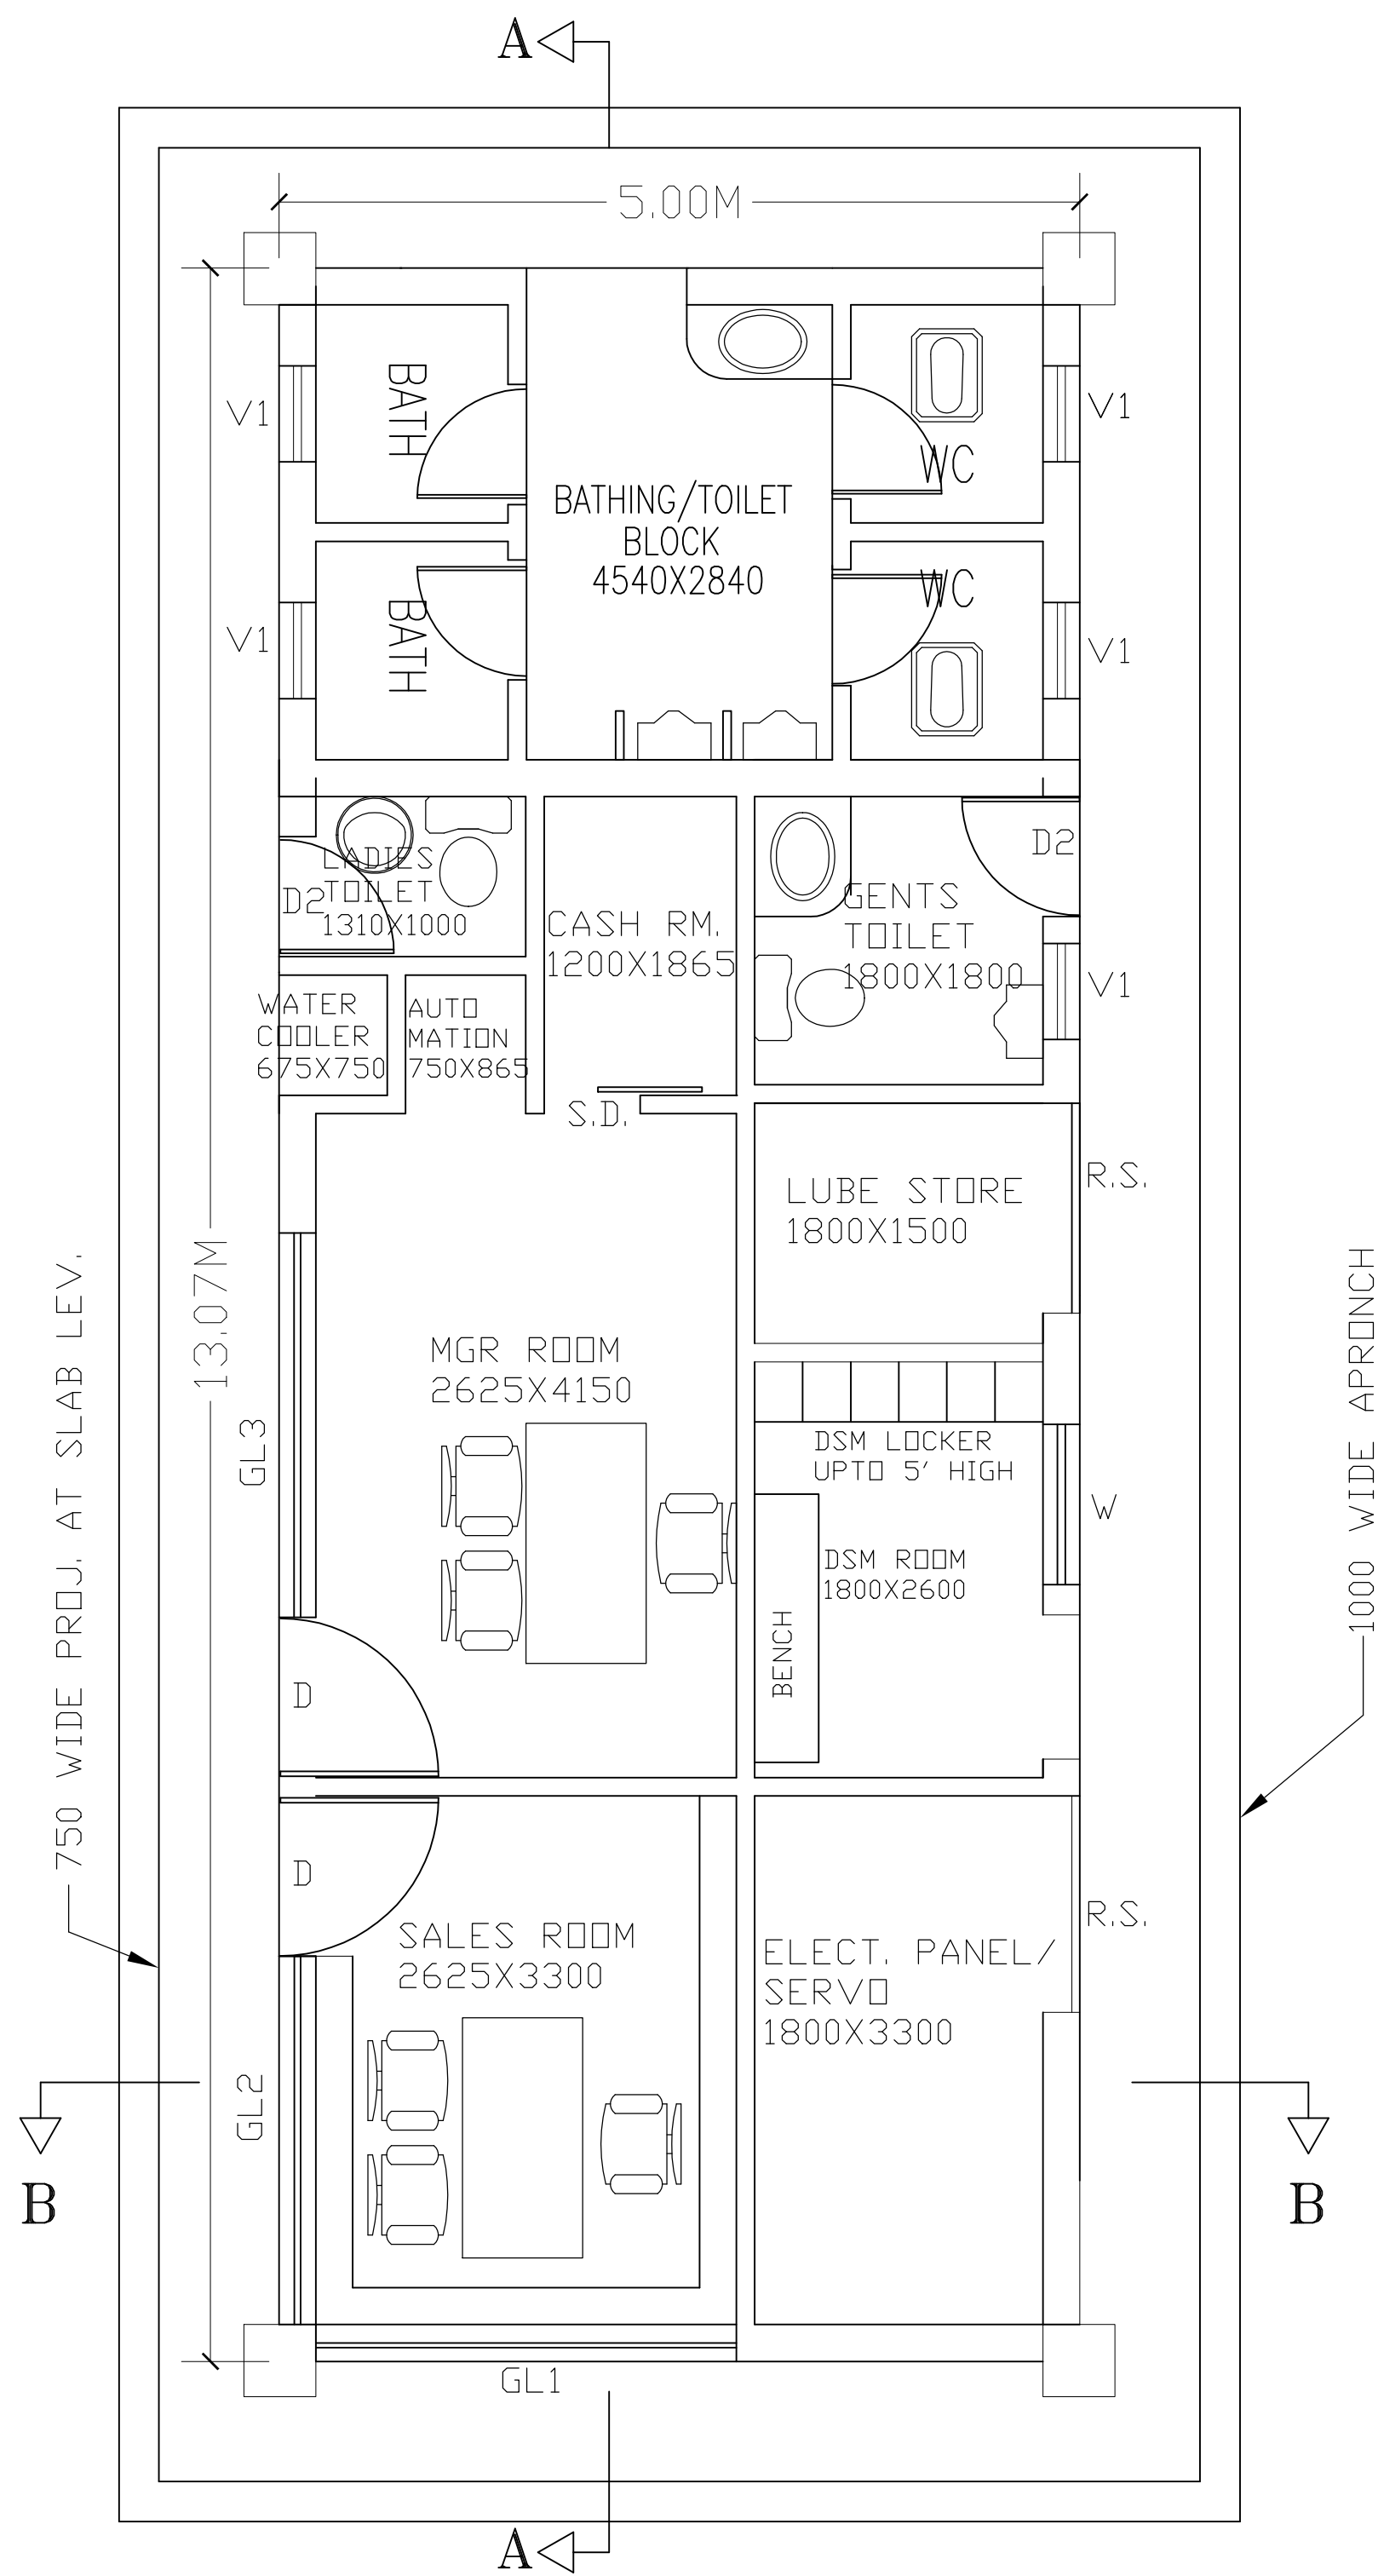


GROUND FLOOR LAYOUT PLAN


SCHEDULE OF DOORS & WINDOWS					
S.N	TYPE	SIZE	SILL	LINTEL	REMARKS
1	D	1000 X 2700	-	2700	
2	D1	900 X 2100	-	2100	
3	D2	750 X 2100	-	2700	
4	GL1	2625 X 2500	200	2700	
5	GL2	2250 X 2500	200	2700	
5	GL3	2400 X 2500	200	2700	
6	W	1000 X 1200	900	2100	
7	V	600 X 600	1500	2100	
8	V1	450 X 450	1650	2100	
9	R.S.	1200 X 2100	900	2100	

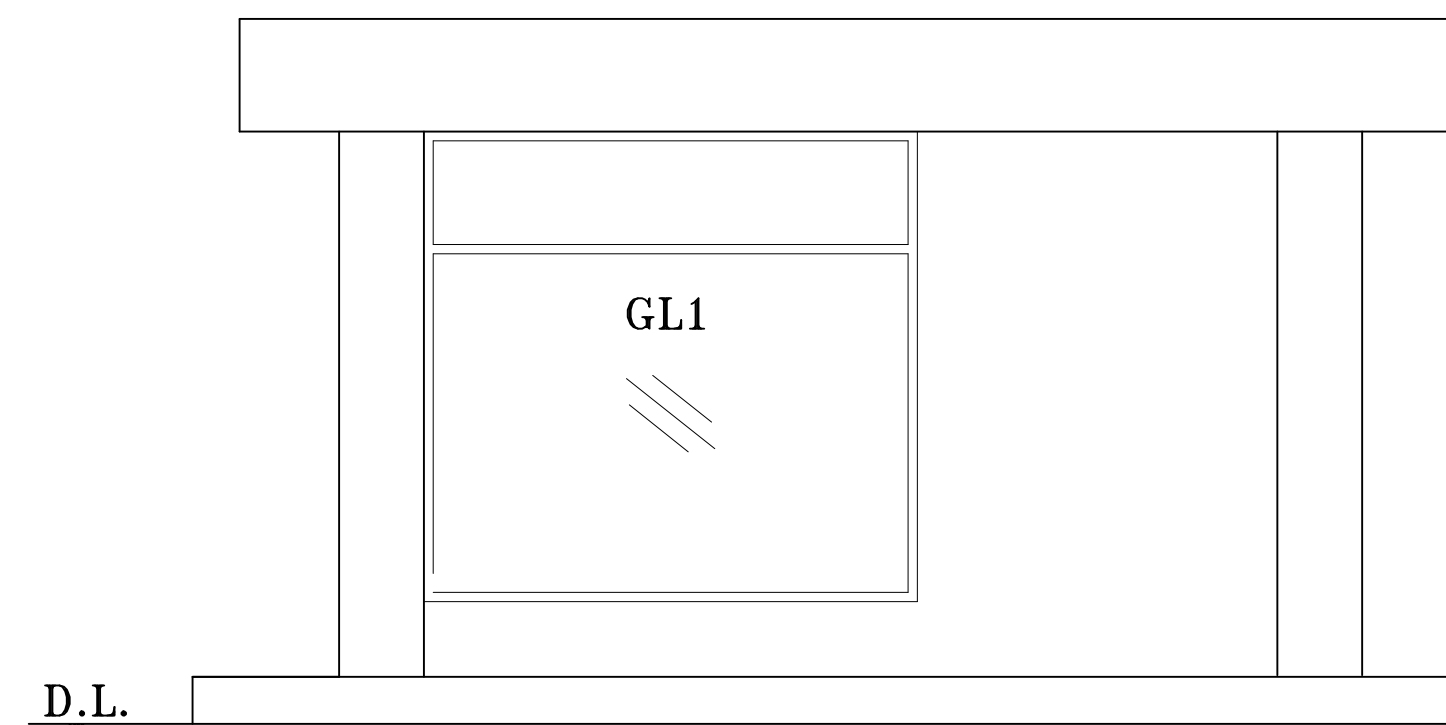


FRONT ELEVATION

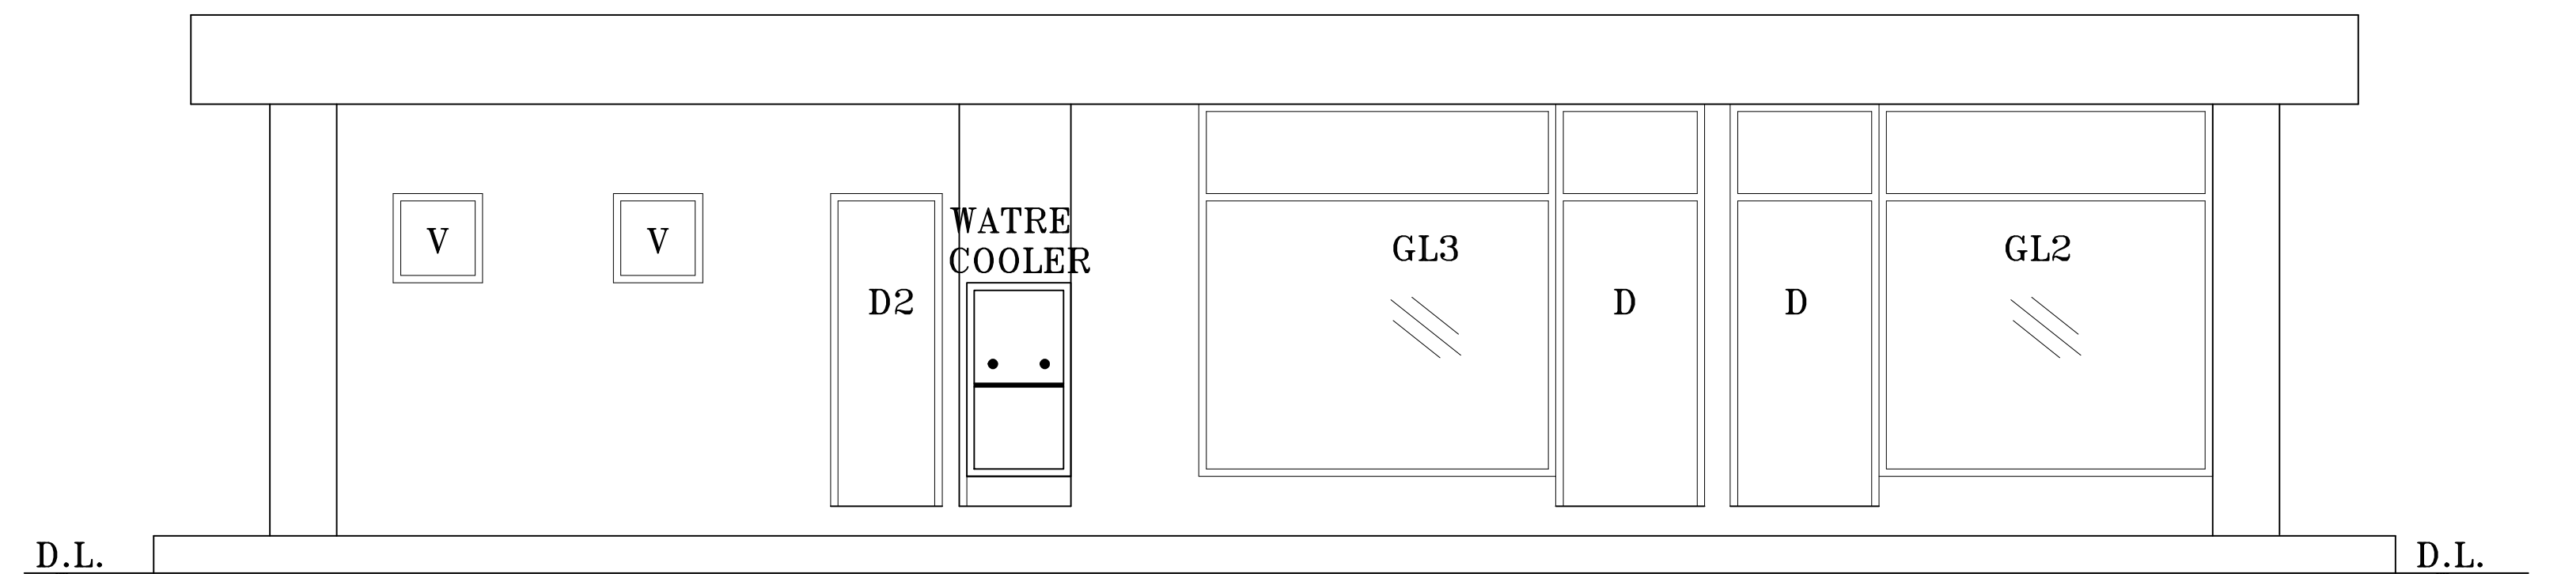


LEFT SIDE ELEVATION

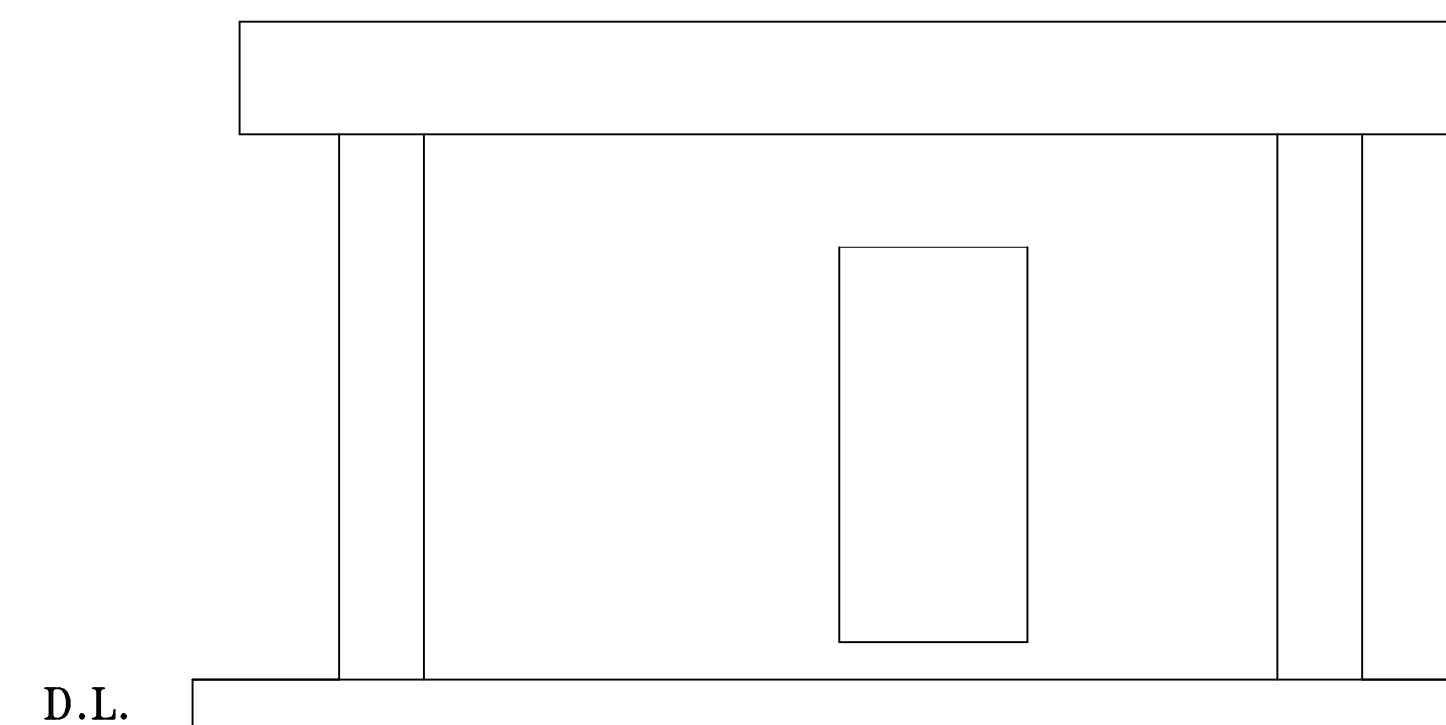


REAR ELEVATION

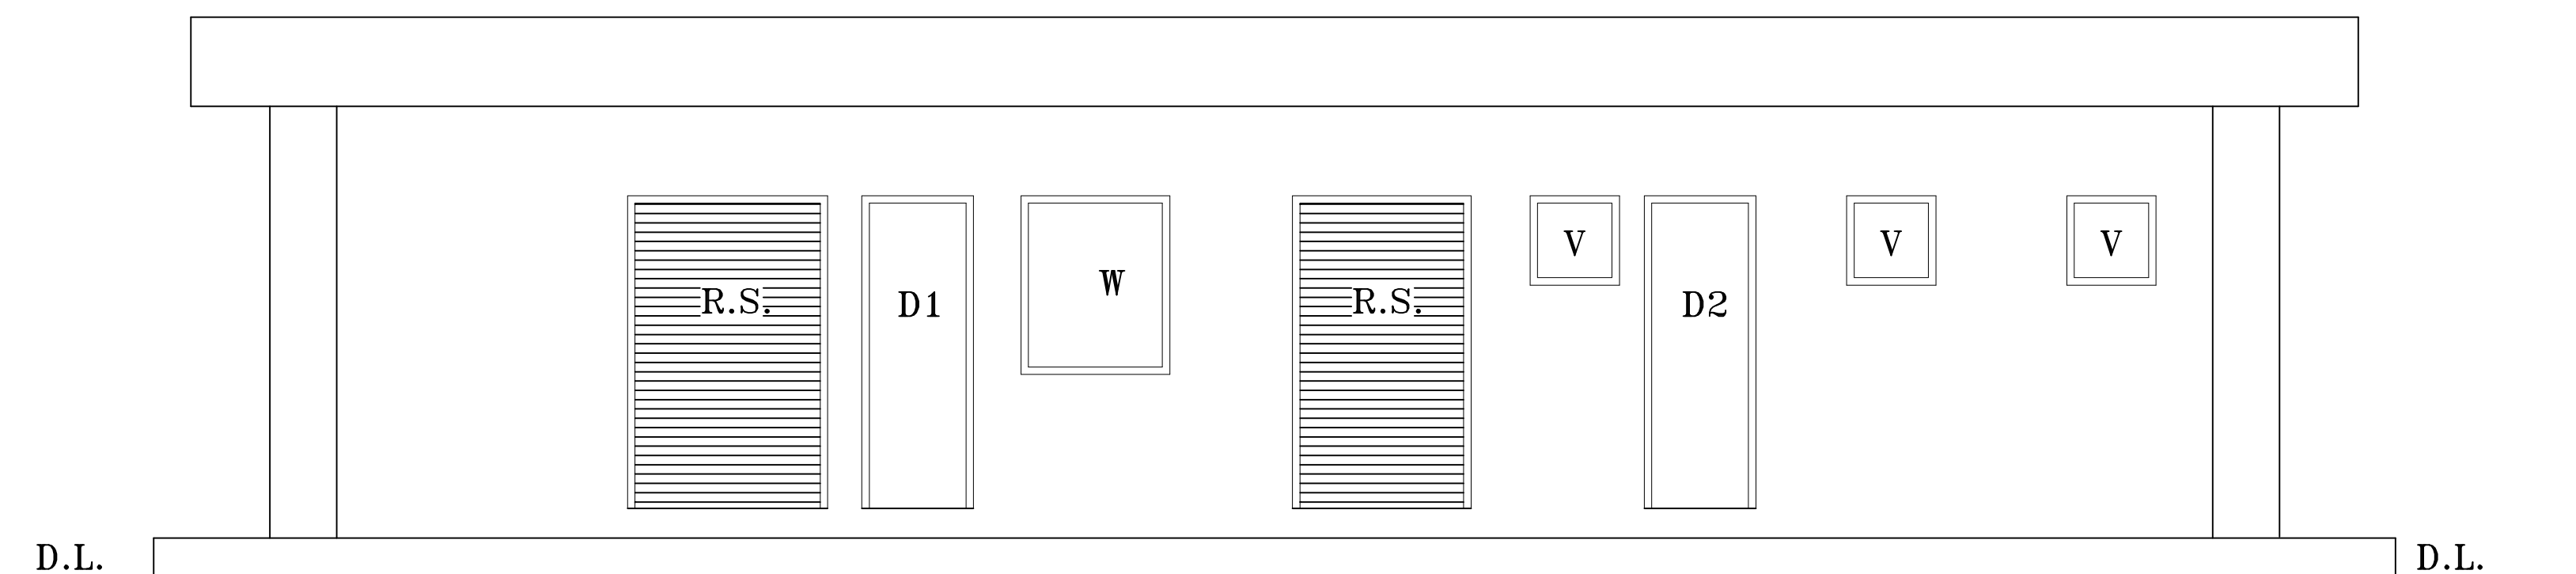

RIGHT SIDE ELEVATION

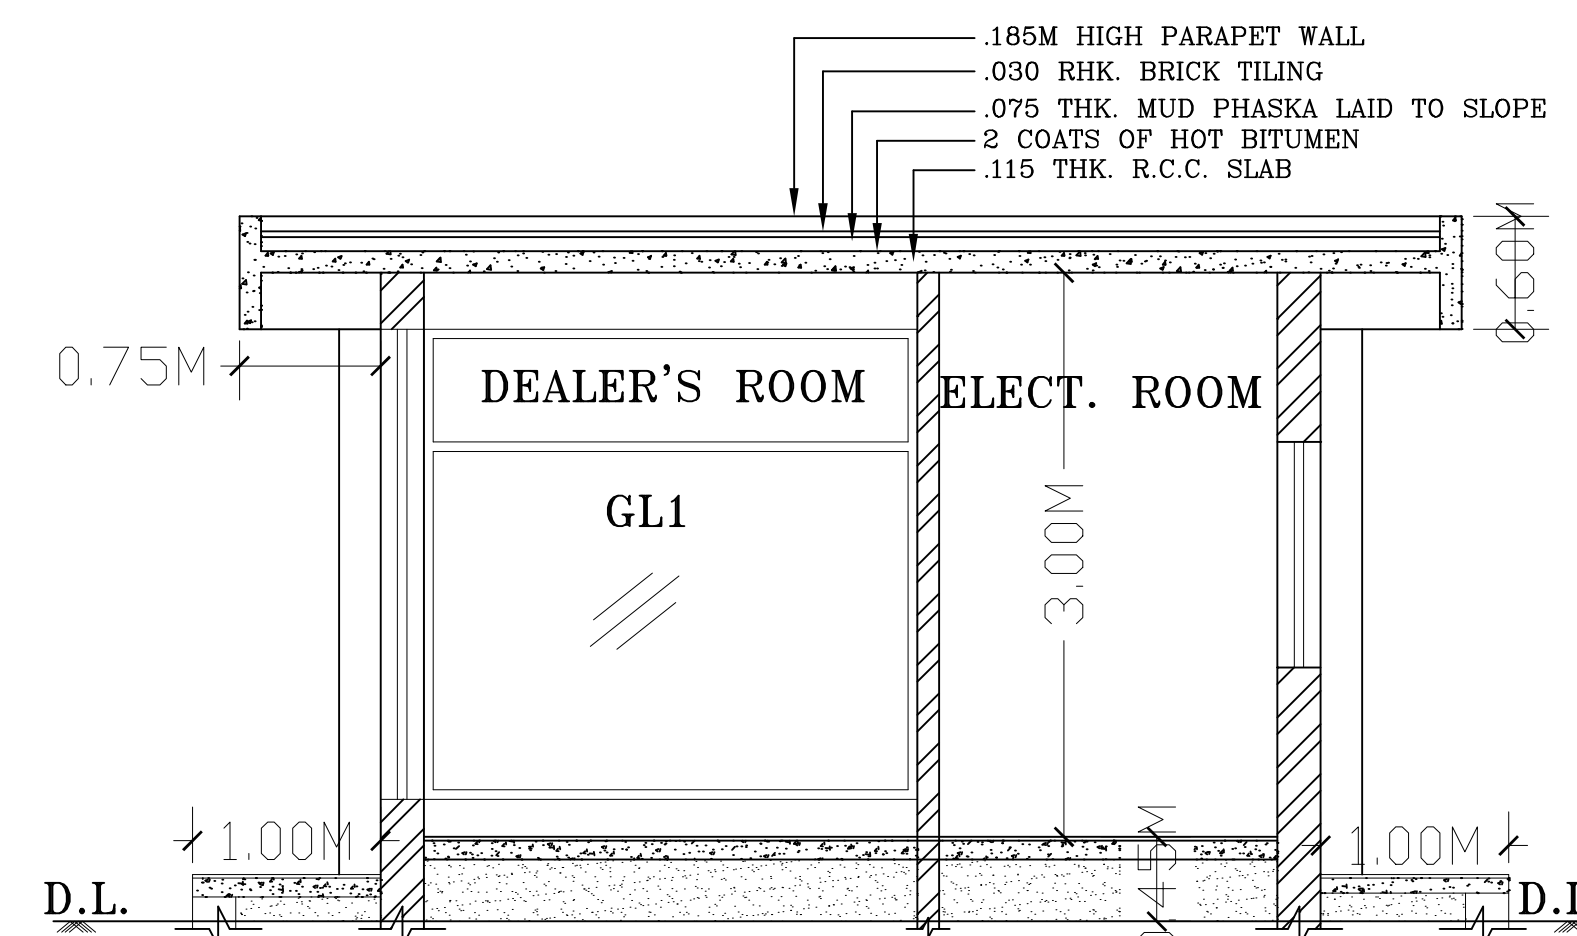

SECTION B-B

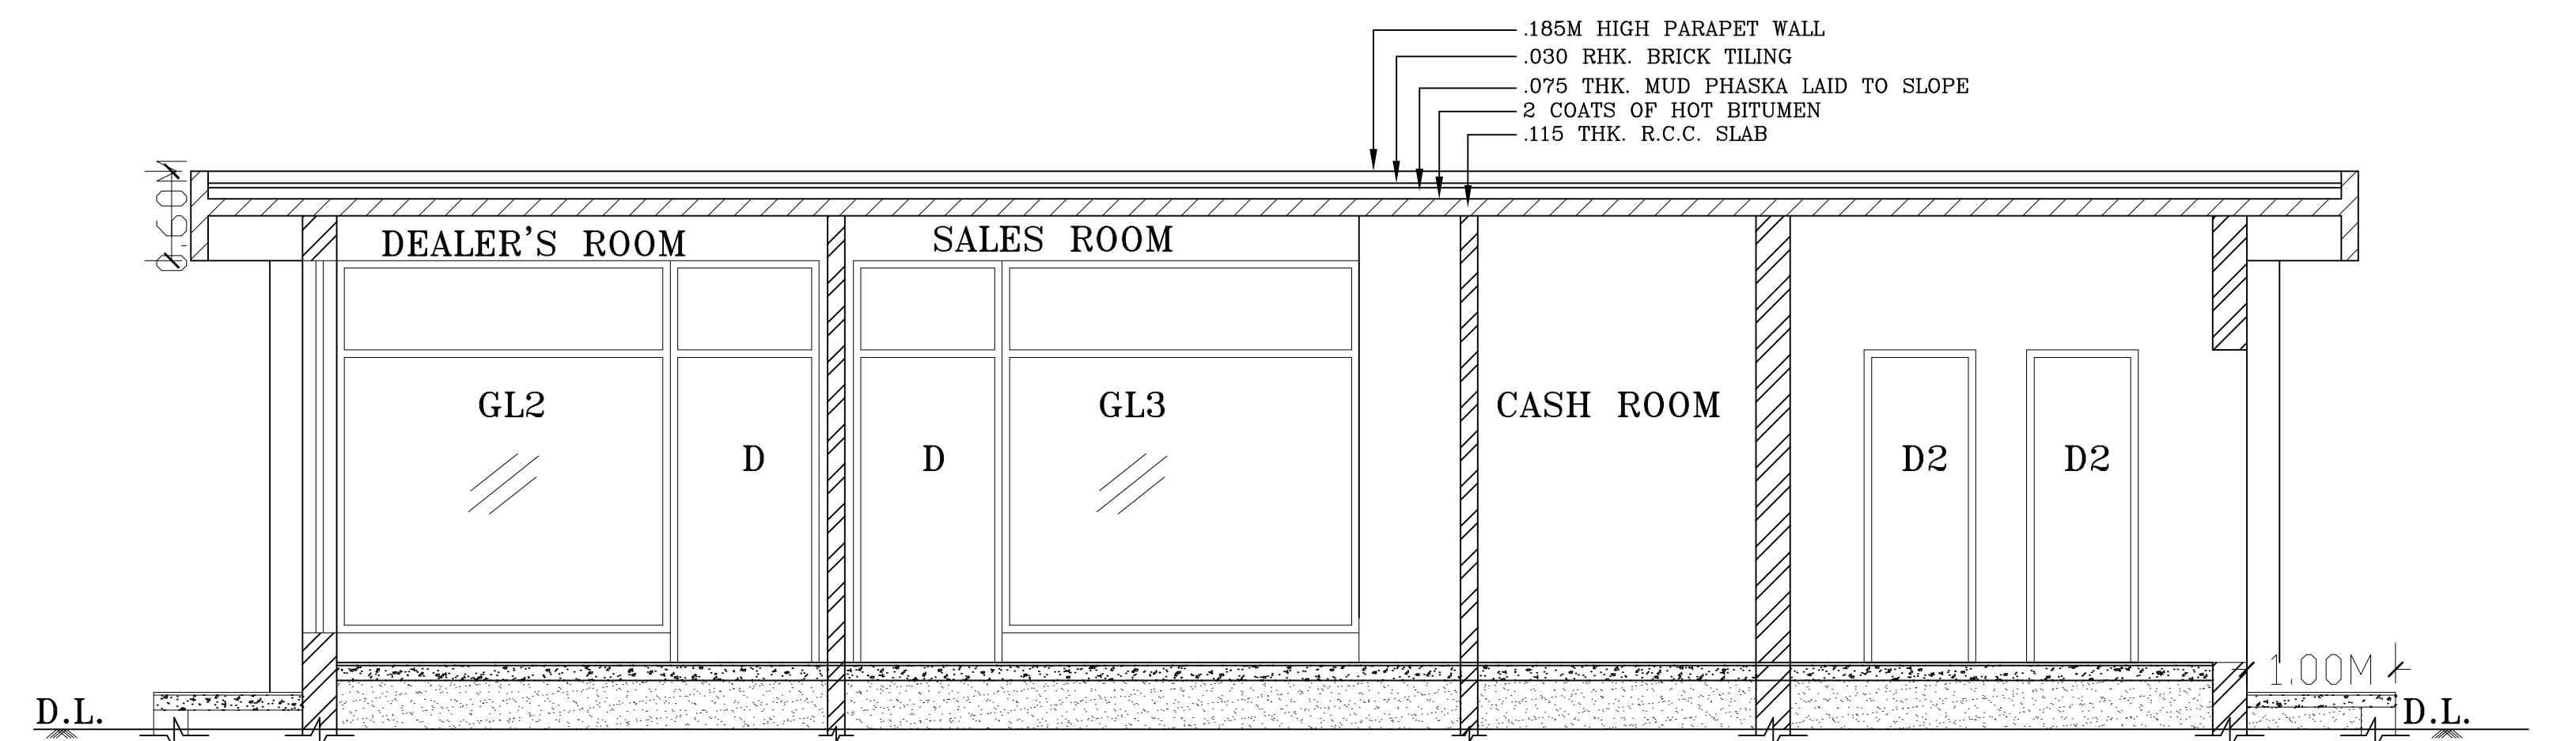

SECTION A-A

1. B1 BUILDING WITH INTEGRATED TOILET BLOCK FOR NATIONAL HIGHWAY ROS
2. FOUNDATION TO BE DESIGNED AS PER SPECIFIC SITE CONDITIONS.


CLIENT:- BHARAT PETROLEUM CORP. LTD.

DATED : 18-02-2022

CHECKED BY:-


TITLE :- B1 BUILDING WITH INTEGRATED TOILET BLOCK LAYOUT PLAN, ELEVATION & SECTION

B2 BUILDING

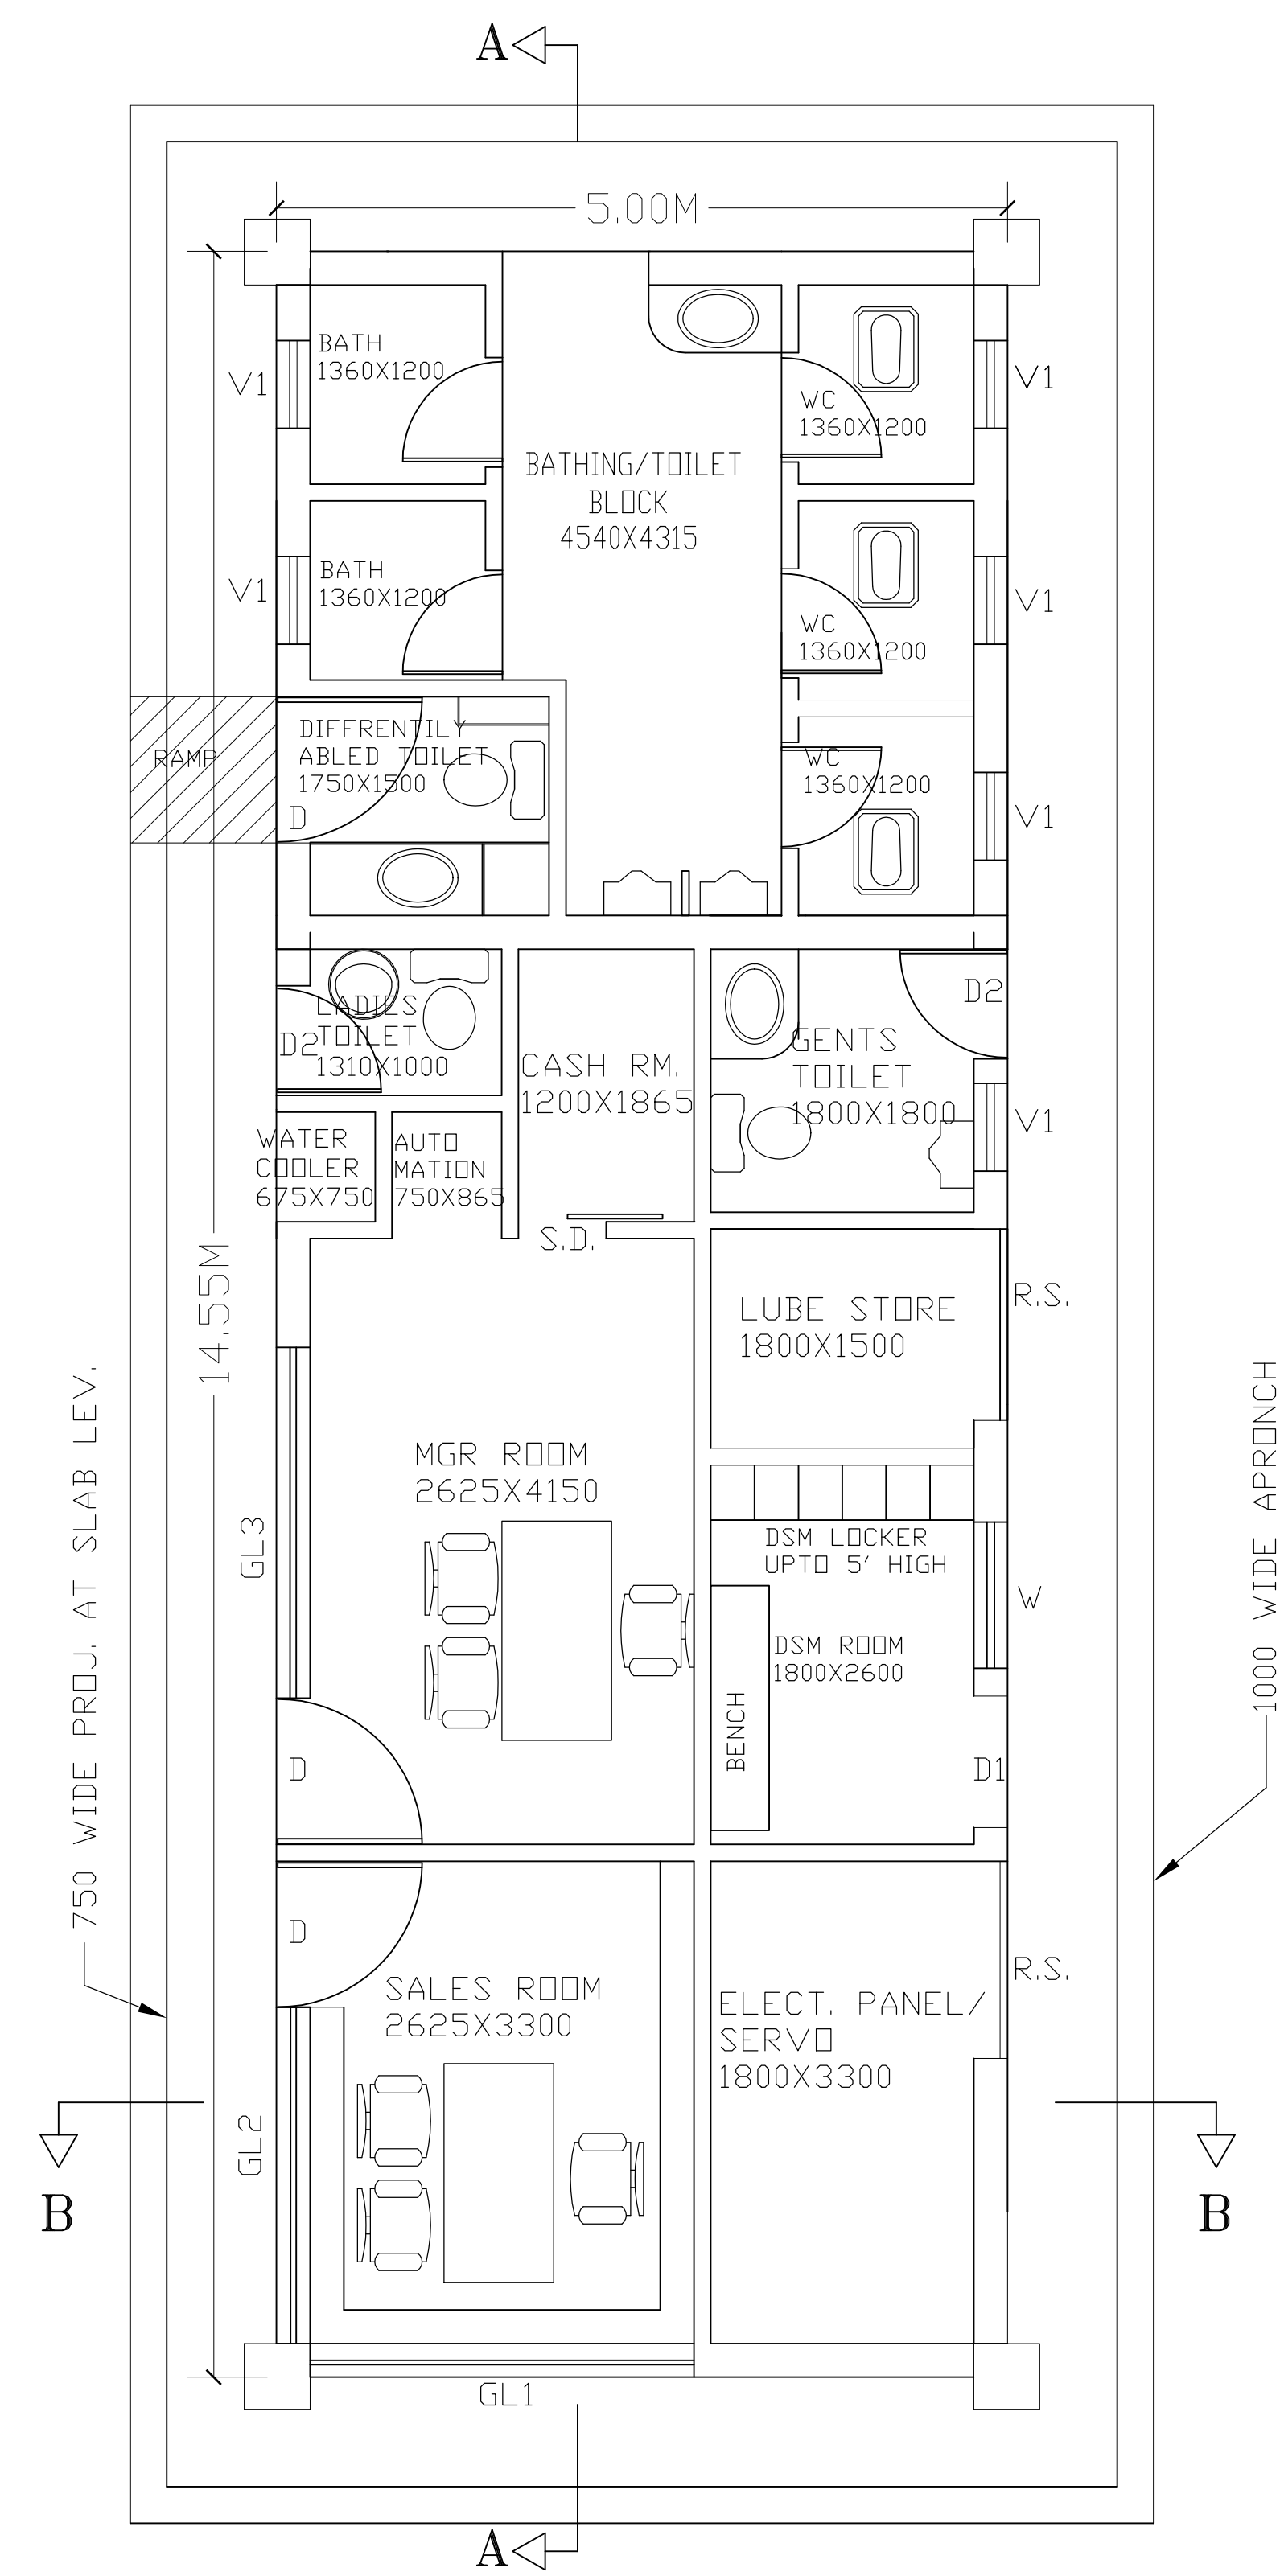


GROUND FLOOR LAYOUT PLAN


SCHEDULE OF DOORS & WINDOWS					
S.N	TYPE	SIZE	SILL	LINTEL	REMARKS
1	D	1000 X 2700	-	2700	
2	D1	900 X 2100	-	2100	
3	D2	750 X 2100	-	2700	
4	GL1	2625 X 2500	200	2700	
5	GL2	2250 X 2500	200	2700	
5	GL3	2400 X 2500	200	2700	
6	W	1000 X 1200	900	2100	
7	V	600 X 600	1500	2100	
8	V1	450 X 450	1650	2100	
9	R.S.	1200 X 2100	900	2100	

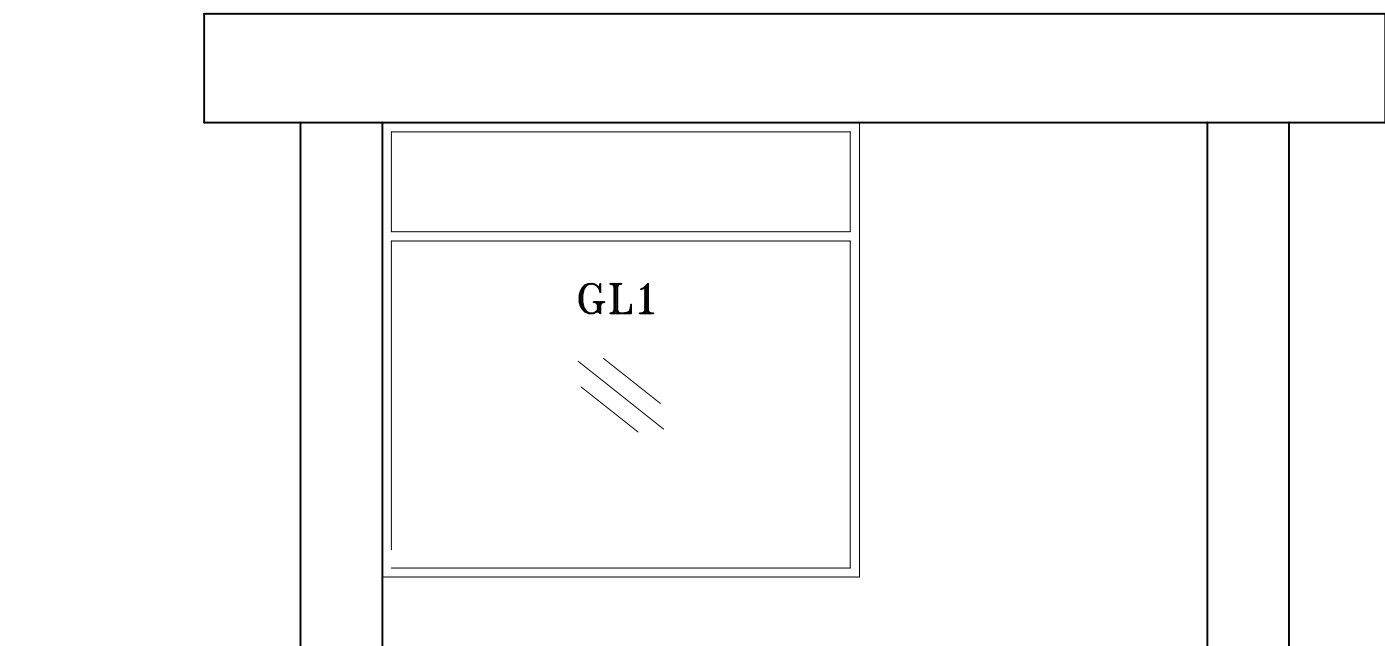


FRONT ELEVATION

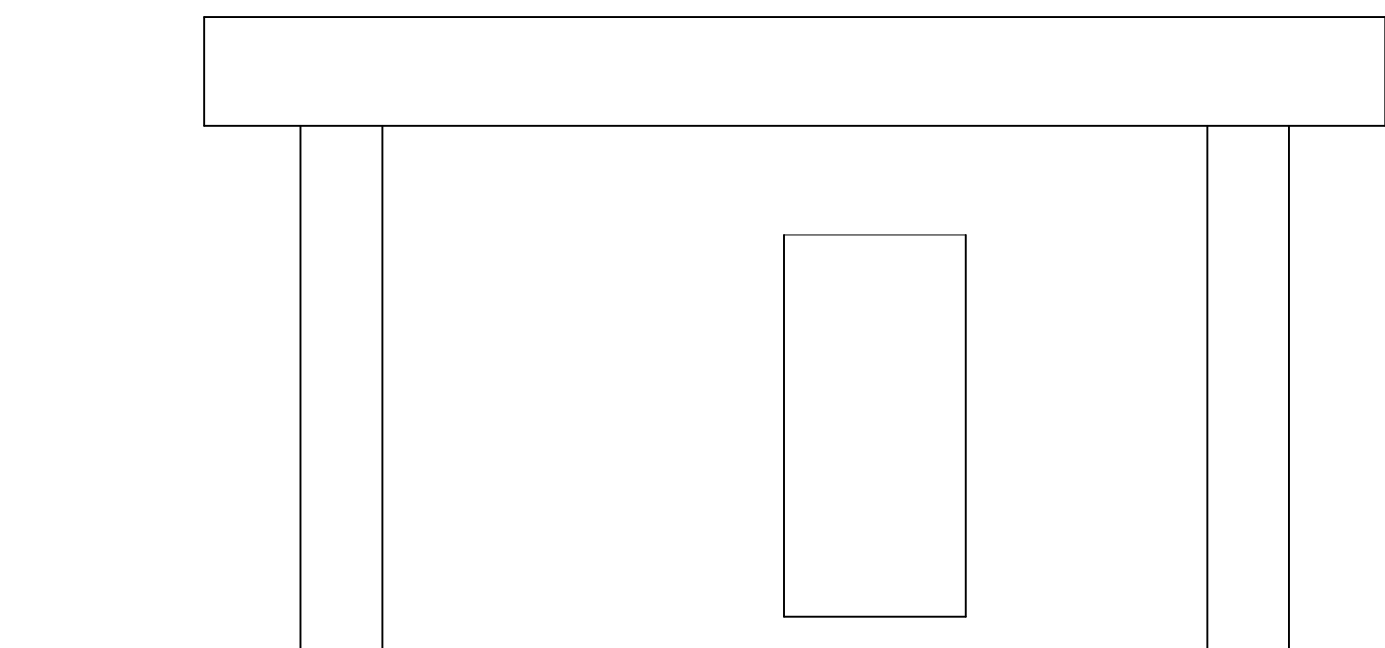


REAR ELEVATION

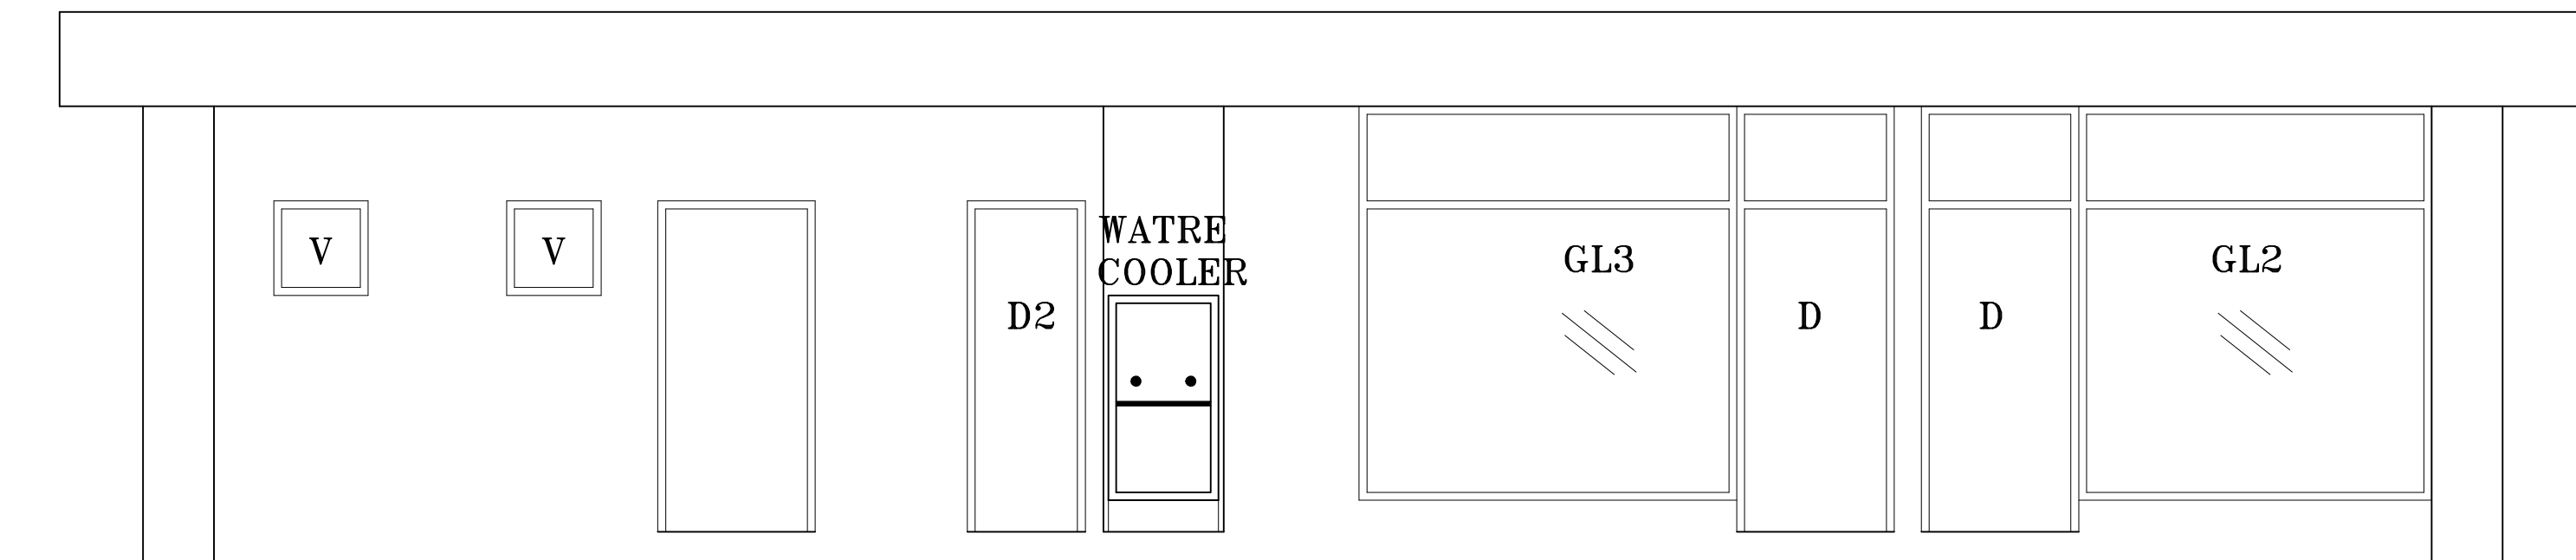


LEFT SIDE ELEVATION

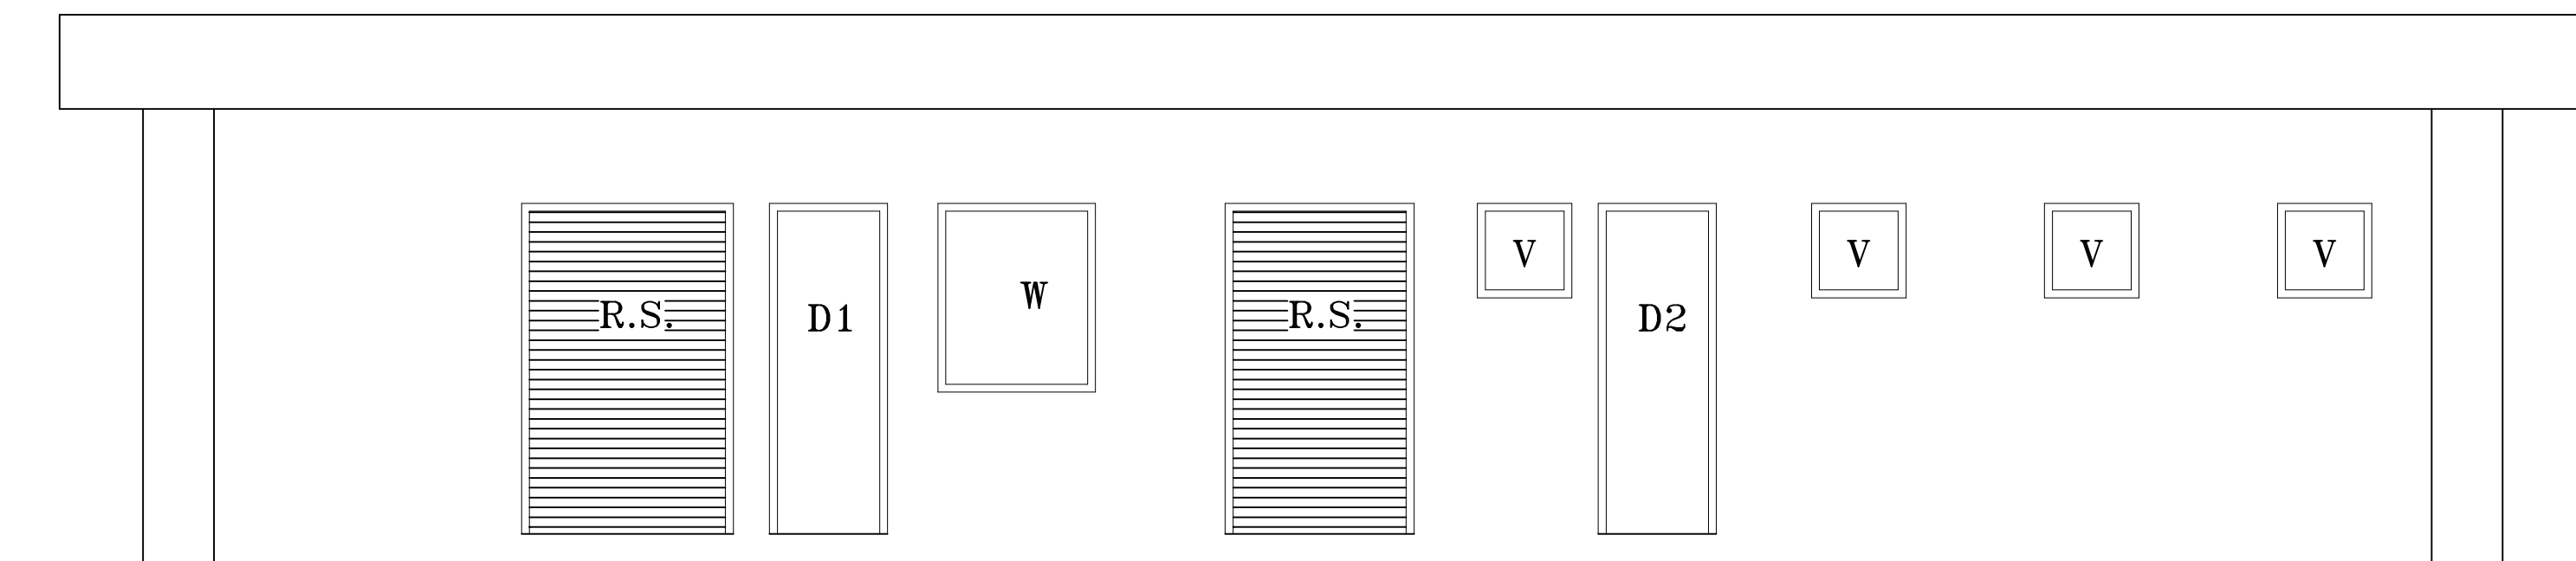

RIGHT SIDE ELEVATION

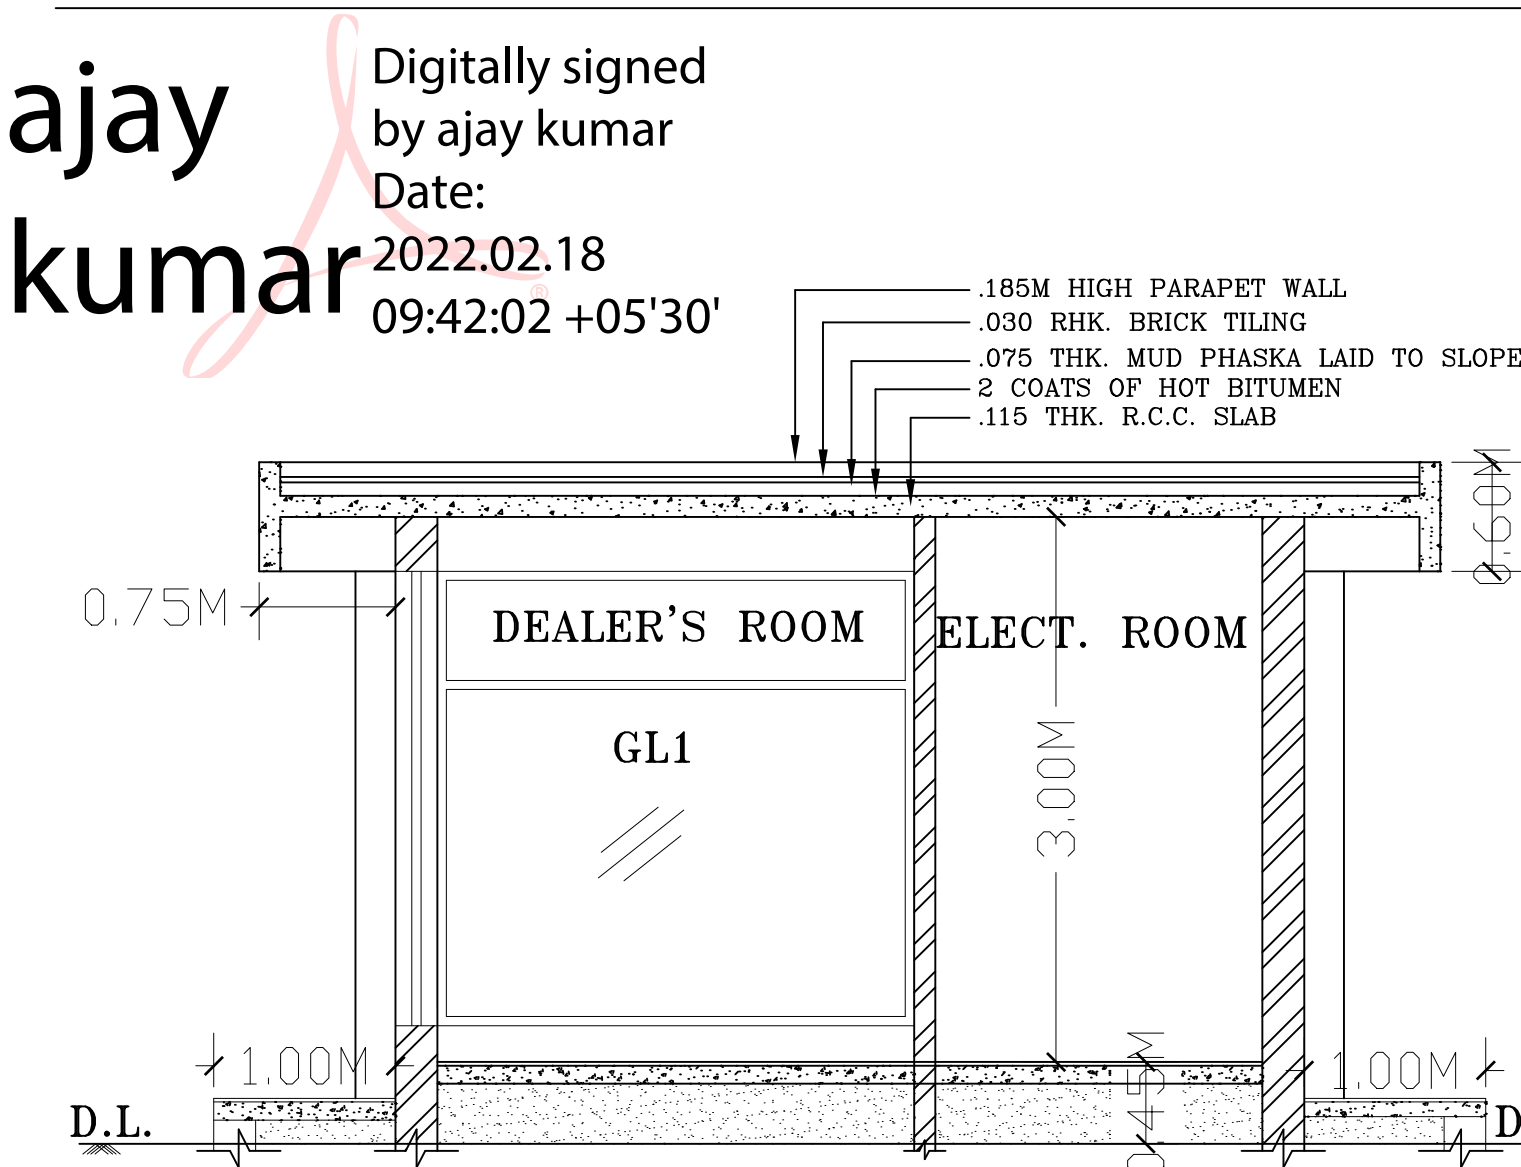

SECTION B-B

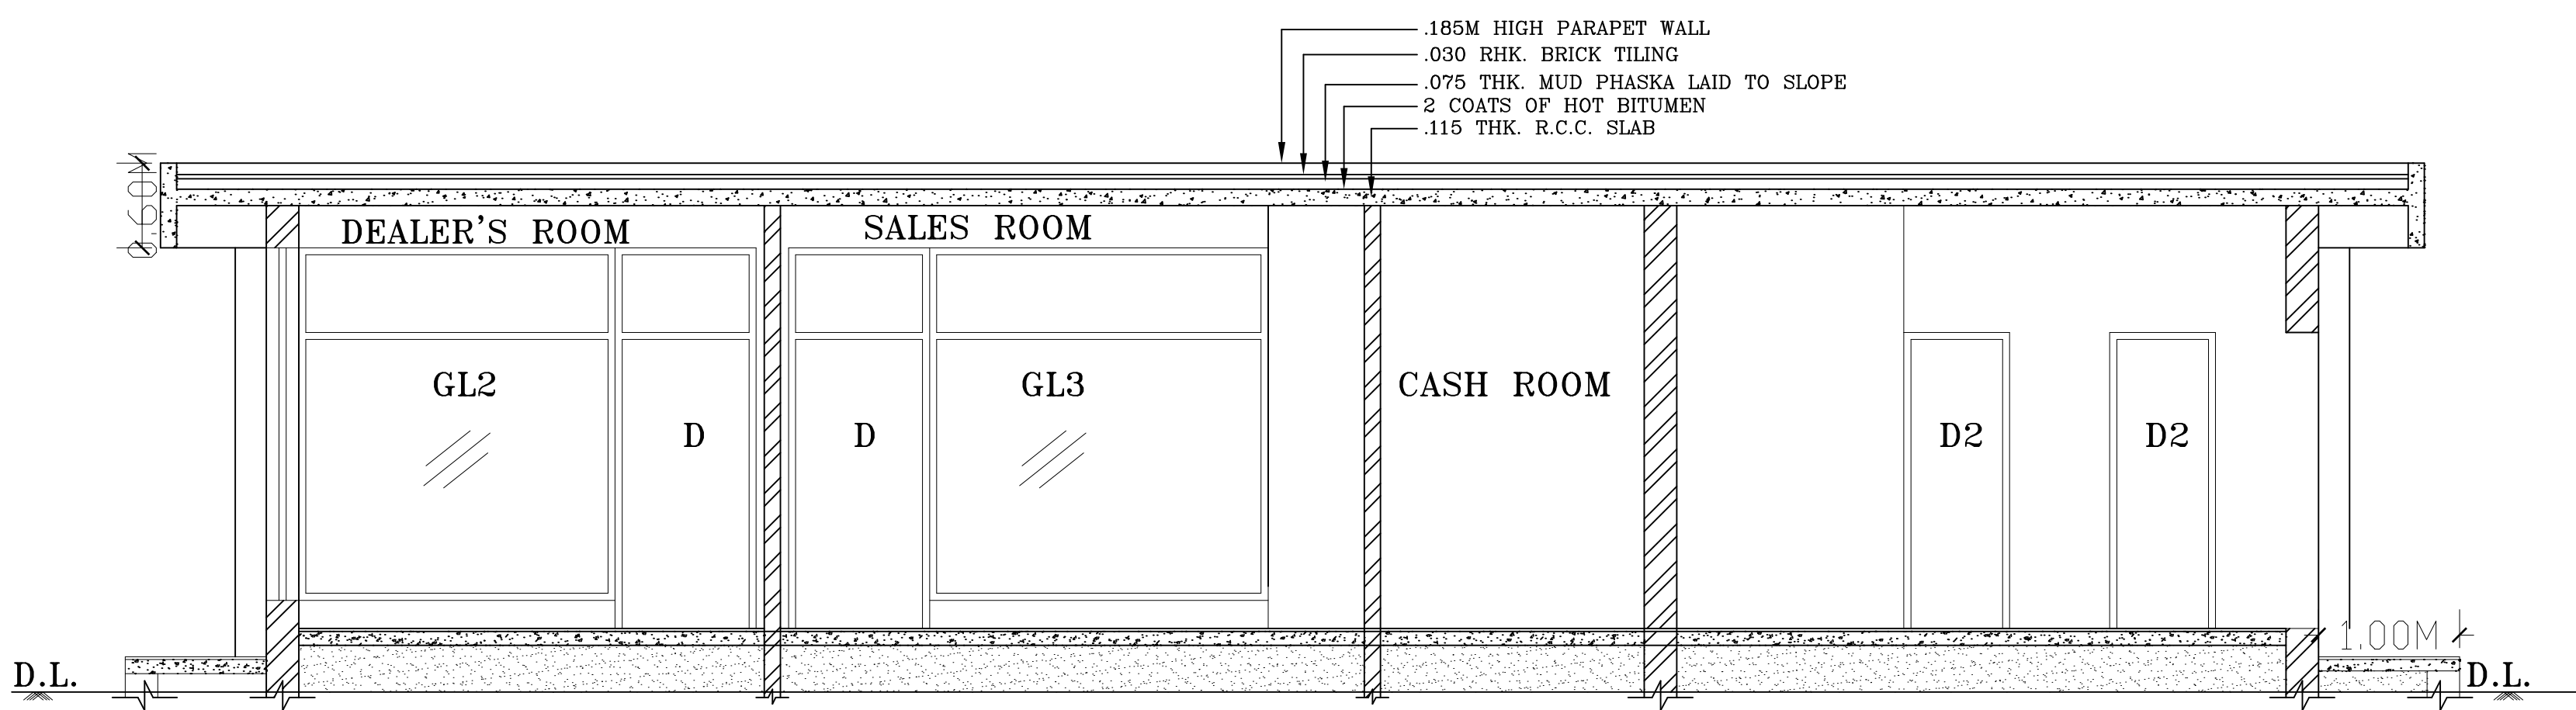

SECTION A-A

1. B2 BUILDING WITH INTEGRATED TOILET BLOCK FOR NATIONAL HIGHWAY ROS- HIGH POTENTAIL
2. FOUNDATION TO BE DESIGNED AS PER SPECIFIC SITE CONDITIONS.

CLIENT:- BHARAT PETROLEUM CORP. LTD.

DATED : 18-02-2022

CHECKED BY:-

TITLE :- B2 BUILDING WITH INTEGRATED TOILET BLOCK FOR NH LAYOUT PLAN, ELEVATION & SECTION