


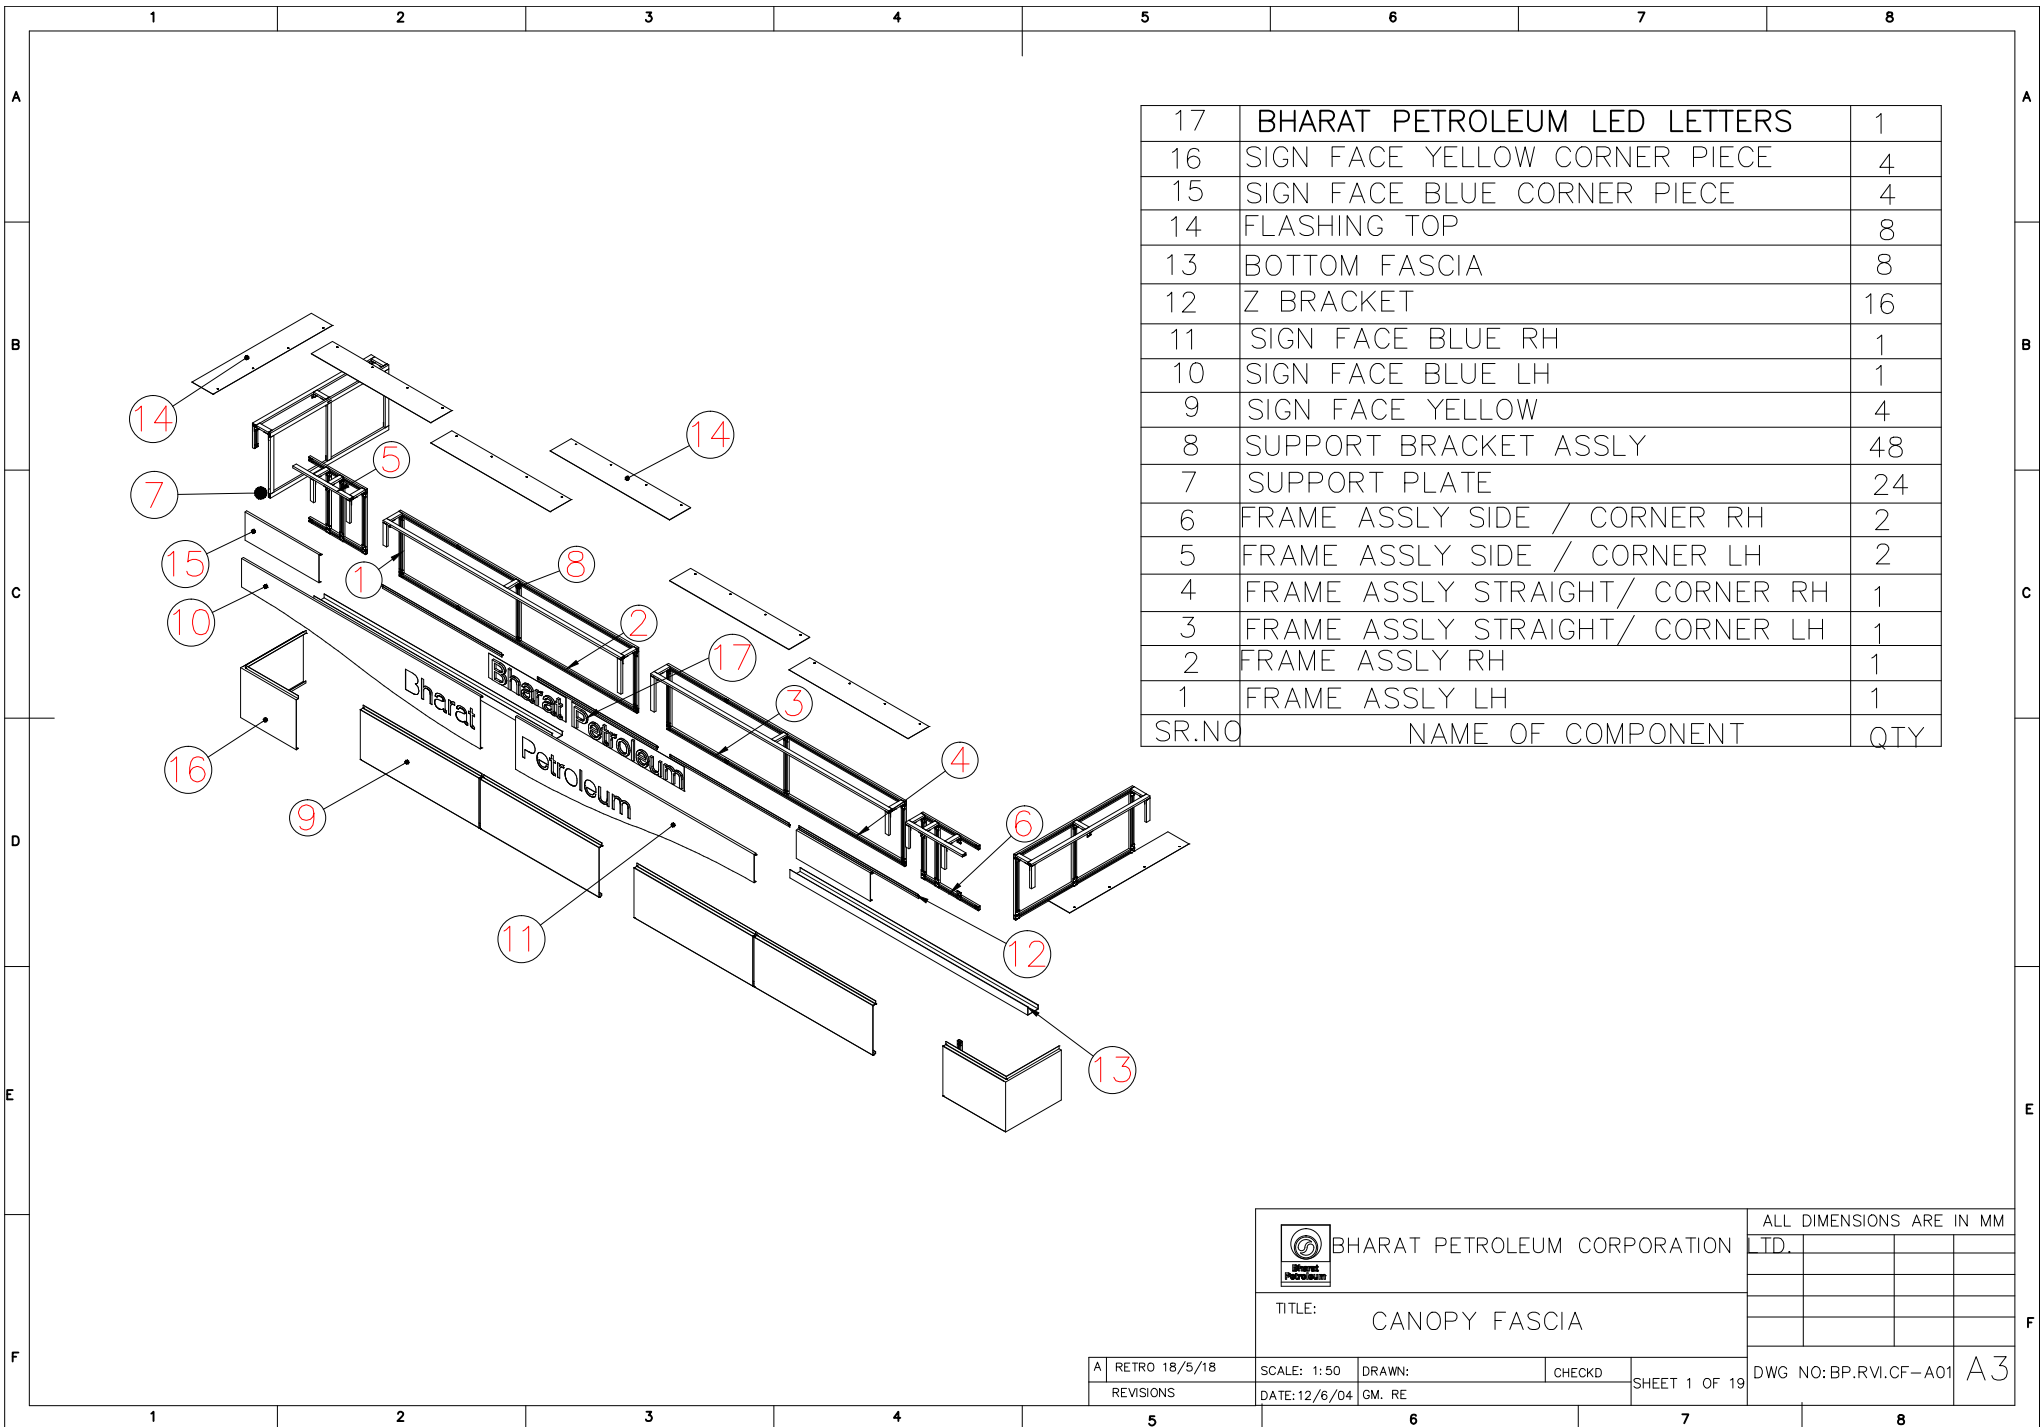

WAVE SIZE	6MT	7MT	8MT
A	5800	6800	7800
B	2900	3400	1950x2

18	LED FIXING BRACKET	1
17	BHARAT PETROLEUM LED LETTERS	1
16	SIGN FACE YELLOW CORNER PIECE	4
15	SIGN FACE BLUE CORNER PIECE	4
14	FLASHING TOP	8
13	BOTTOM FACIA	8
12	Z BRACKET	16
11	SIGN FACE BLUE RH	1
10	SIGN FACE BLUE LH	1
9	SIGN FACE YELLOW	4
8	GUSSET	48
7	SUPPORT PLATE	24
6	FRAME SIDE/CORNER RH	2
5	FRAME SIDE/CORNER LH	2
4	FRAME STRAIGHT/CORNER RH	1
3	FRAME STRAIGHT/CORNER LH	1
2	FRAME ASSY RH	1
1	FRAME ASSY LH	1
SR.NO.	DESCRIPTION	QTY.


DETAIL AT X
SCALE 1:5

LETTER HEIGHT 250mm

BHARAT PETROLEUM LED DISPLAY

MATERIAL-ACM BLUE SHEET 3mm thk.

Bharat Petroleum

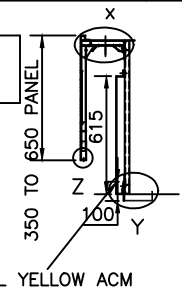

BPCL YELLOW ACM

ACM BLUE

L ANGLE

DETAIL AT Z

DETAIL AT Y



BHARAT PETROLEUM CORPORATION LTD.

TITLE :

CANOPY FASCIA MODULE

REVISIONS

SCALE :

DRAWN:

CHECKED

SHEET NO.


DRAWING NO :

DATE : 12/6/04

GM.RE

2 OF 19

BP.RVI.CF-A02

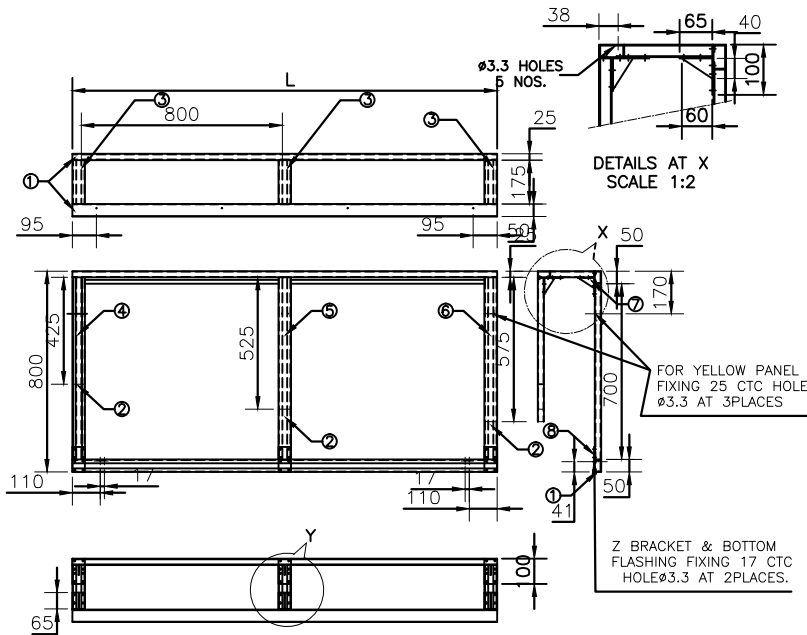


8	SUPPORT PLATE	3
7	GUSSET	6
6	C CHANNEL 575lg.	1
5	C CHANNEL 525lg.	1
4	C CHANNEL 425lg.	1
3	C CHANNEL 175lg.	3
2	C CHANNEL 700lg.	3
1	C CHANNEL 1690lg.	3
1	C CHANNEL 1690lg.(7m MODULE)	3
SR NO	DESCRIPTION	QTY

FRAME LH1

NOTE:- RIVETED & CO2 WELDED AT ALL JOINTS

L-FRAME LENGTH IS 1440mm for 6m MODULE.
VERTICAL CHANNEL IS SAME.

L -2)FRAME LENGTH IS 1940mm for 8m MODULE.

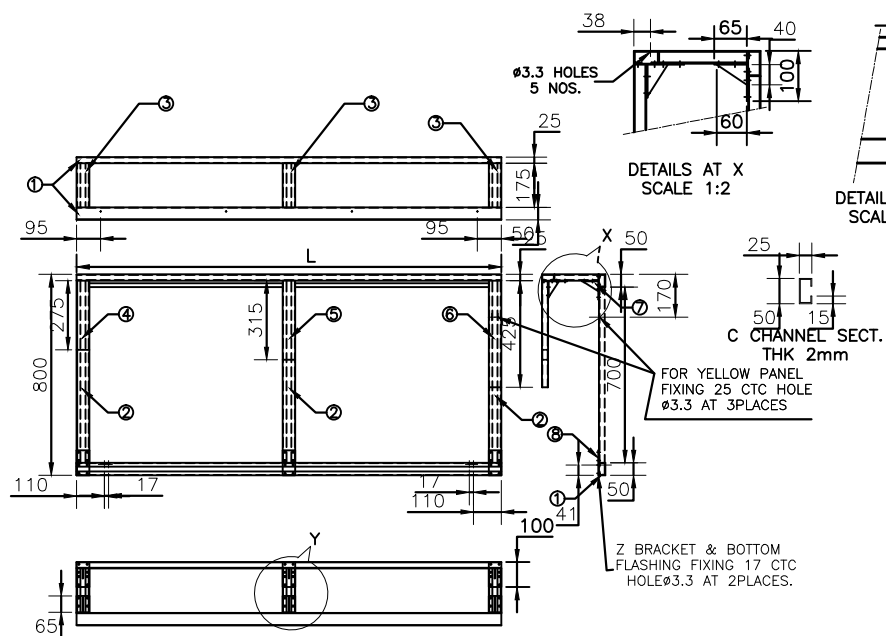


8	SUPPORT PLATE	3
7	GUSSET	6
6	C CHANNEL 425lg.	1
5	C CHANNEL 315lg.	1
4	C CHANNEL 275lg.	1
3	C CHANNEL 175lg.	3
2	C CHANNEL 700lg.	3
1	C CHANNEL 1690lg.(7m MODULE)	3
SR NO	DESCRIPTION	QTY

FRAME LH2

MS SQ.25X2MM Thk. PIPE
WELDED STRUCTURE
OR MS C CHANNEL
WELDED STRUCTURE

	BHARAT PETROLEUM CORPORATION LTD.			
	TITLE :		DATE	DRAWING NO.
	FRAME LH		NUMBERS CROSSED OUT ARE SUPERSEDED DRAWINGS	
REVISIONS		SCALE : 1:15	DRAWN:	CHECKED
DATE : 12/6/04		GM.RE	SHEET NO.	DRAWING NO :
			3of19	BP.RVI.CF-P03

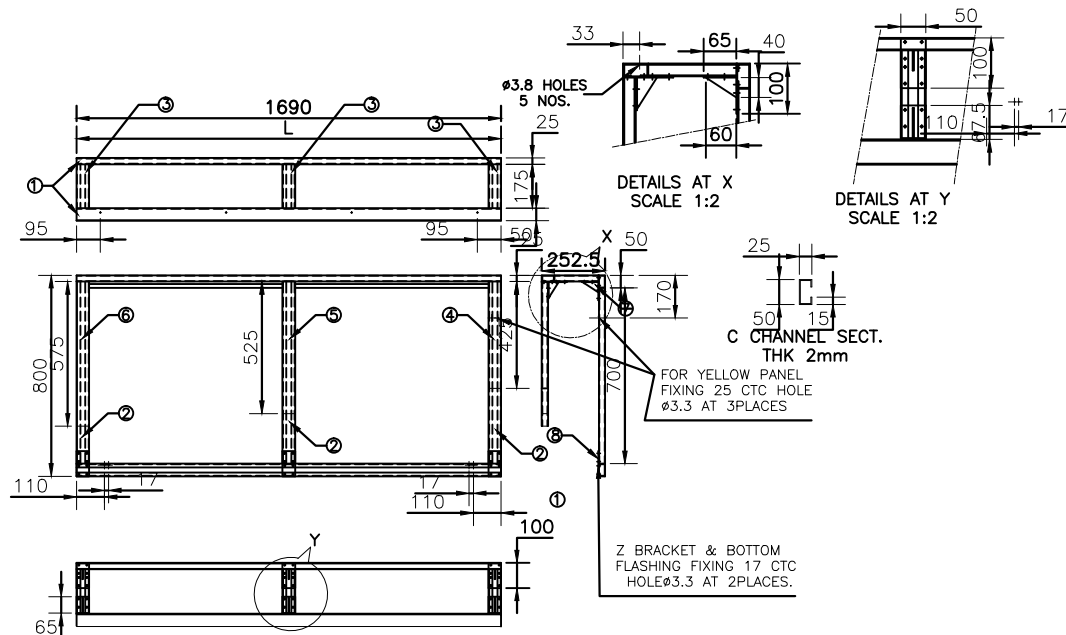


8	SUPPORT PLATE	3
7	GUSSET	6
6	C CHANNEL 575lg.	1
5	C CHANNEL 525lg.	1
4	C CHANNEL 425lg.	1
3	C CHANNEL 175lg.	3
2	C CHANNEL 700lg.	3
1	C CHANNEL 1690lg.(7m MODULE)	3
SR NO	DESCRIPTION	QTY

FRAME RH1

NOTE:- RIVETED & CO2 WELDED AT ALL JOINTS

L -1)FRAME LENGTH IS 1440mm for 6m MODULE.
VERTICAL CHANNEL IS SAME.

L -2)FRAME LENGTH IS 1940mm for 8m MODULE.

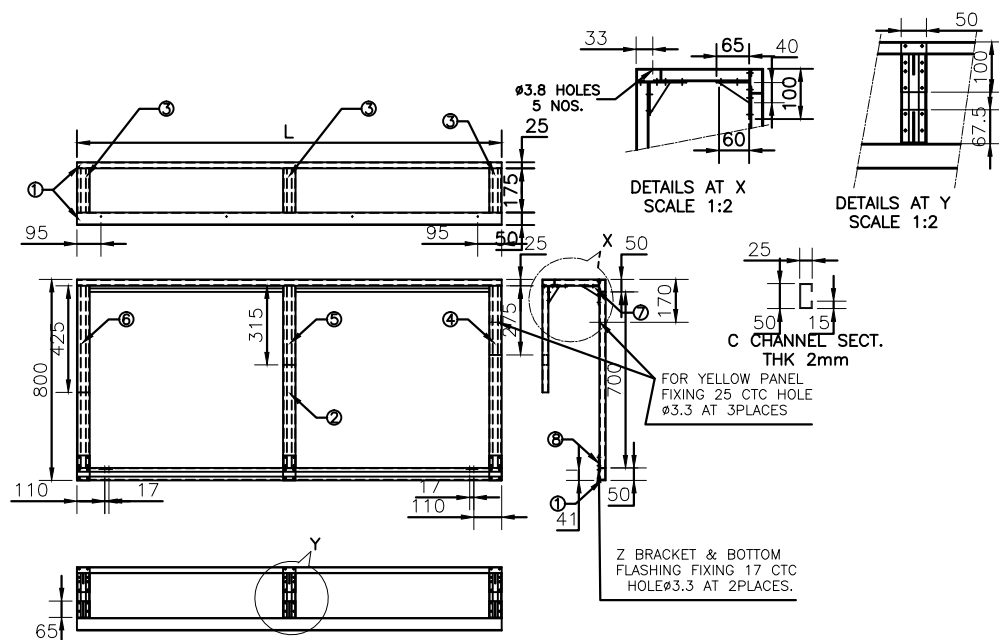


8	SUPPORT PLATE	3
7	GUSSET	6
6	C CHANNEL 425lg.	1
5	C CHANNEL 315lg.	1
4	C CHANNEL 275lg.	1
3	C CHANNEL 175lg.	3
2	C CHANNEL 700lg.	3
1	C CHANNEL 1690lg.(7m MODULE)	3
SR NO	DESCRIPTION	QTY


FRAME RH2


MS SQ.25X2MM Thk. PIPE
WELDED STRUCTURE
OR MS C CHANNEL
WELDED STRUCTURE

 BHARAT PETROLEUM CORPORATION LTD.			
FRAME RH		DATE	DRAWING NO.
		NUMBERS CROSSED OUT ARE SUPERSEDED DRAWINGS	
TITLE : FRAME RH		DRAWING NO : BP.RVI.CF-P04	

A	RETRO 24/5/18	SCALE : 1:15	DRAWN:	CHECKED	SHEET NO. 4 of 19
REVISIONS		DATE : 12/6/04	GM.RE		

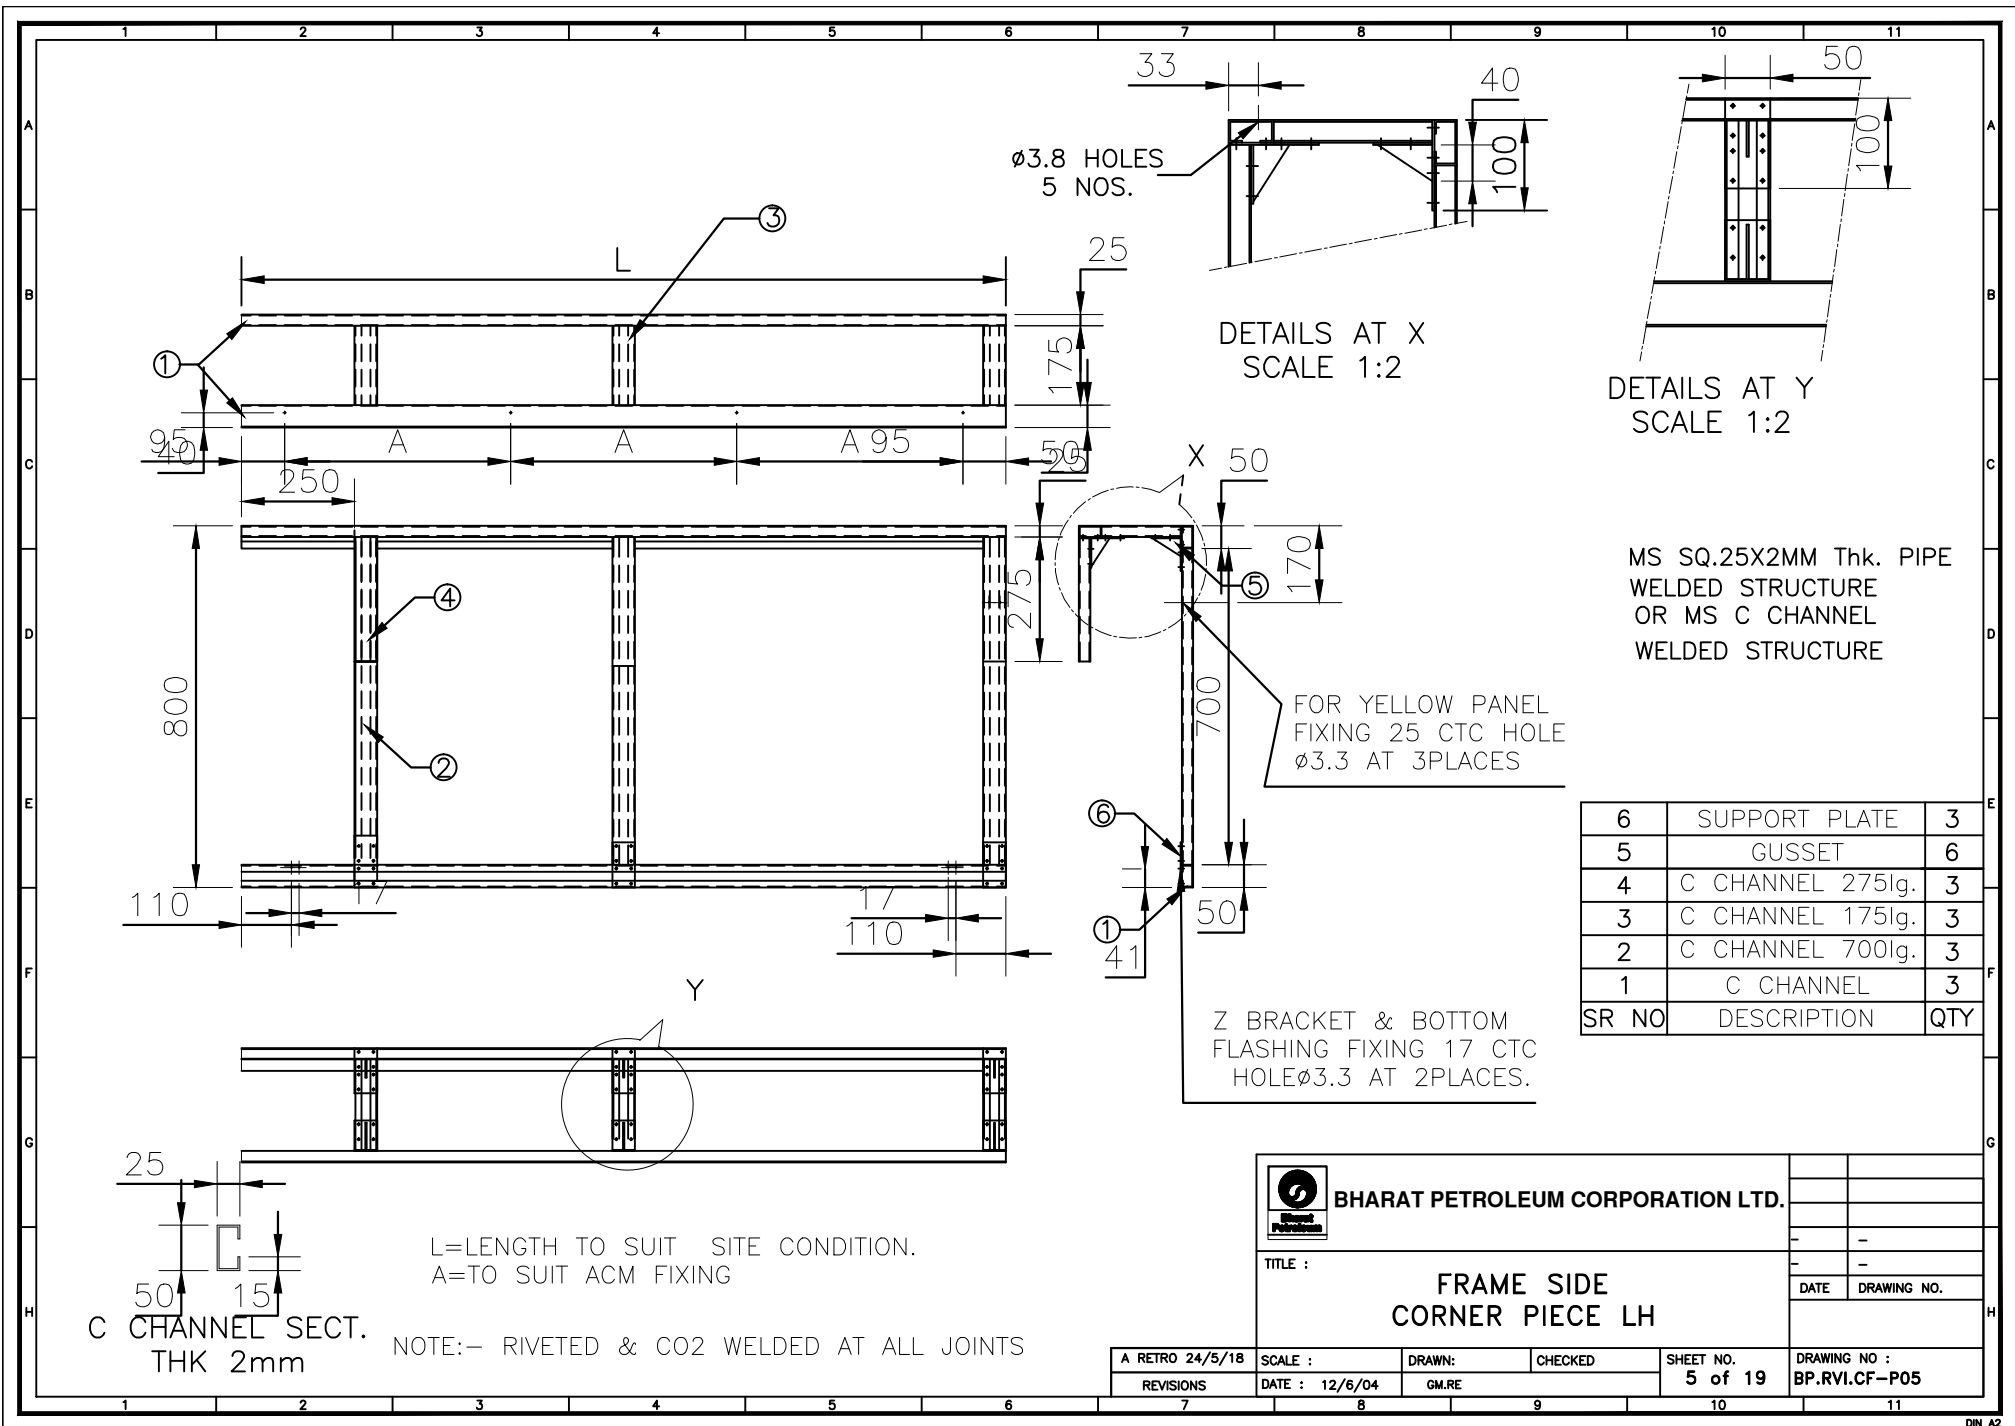

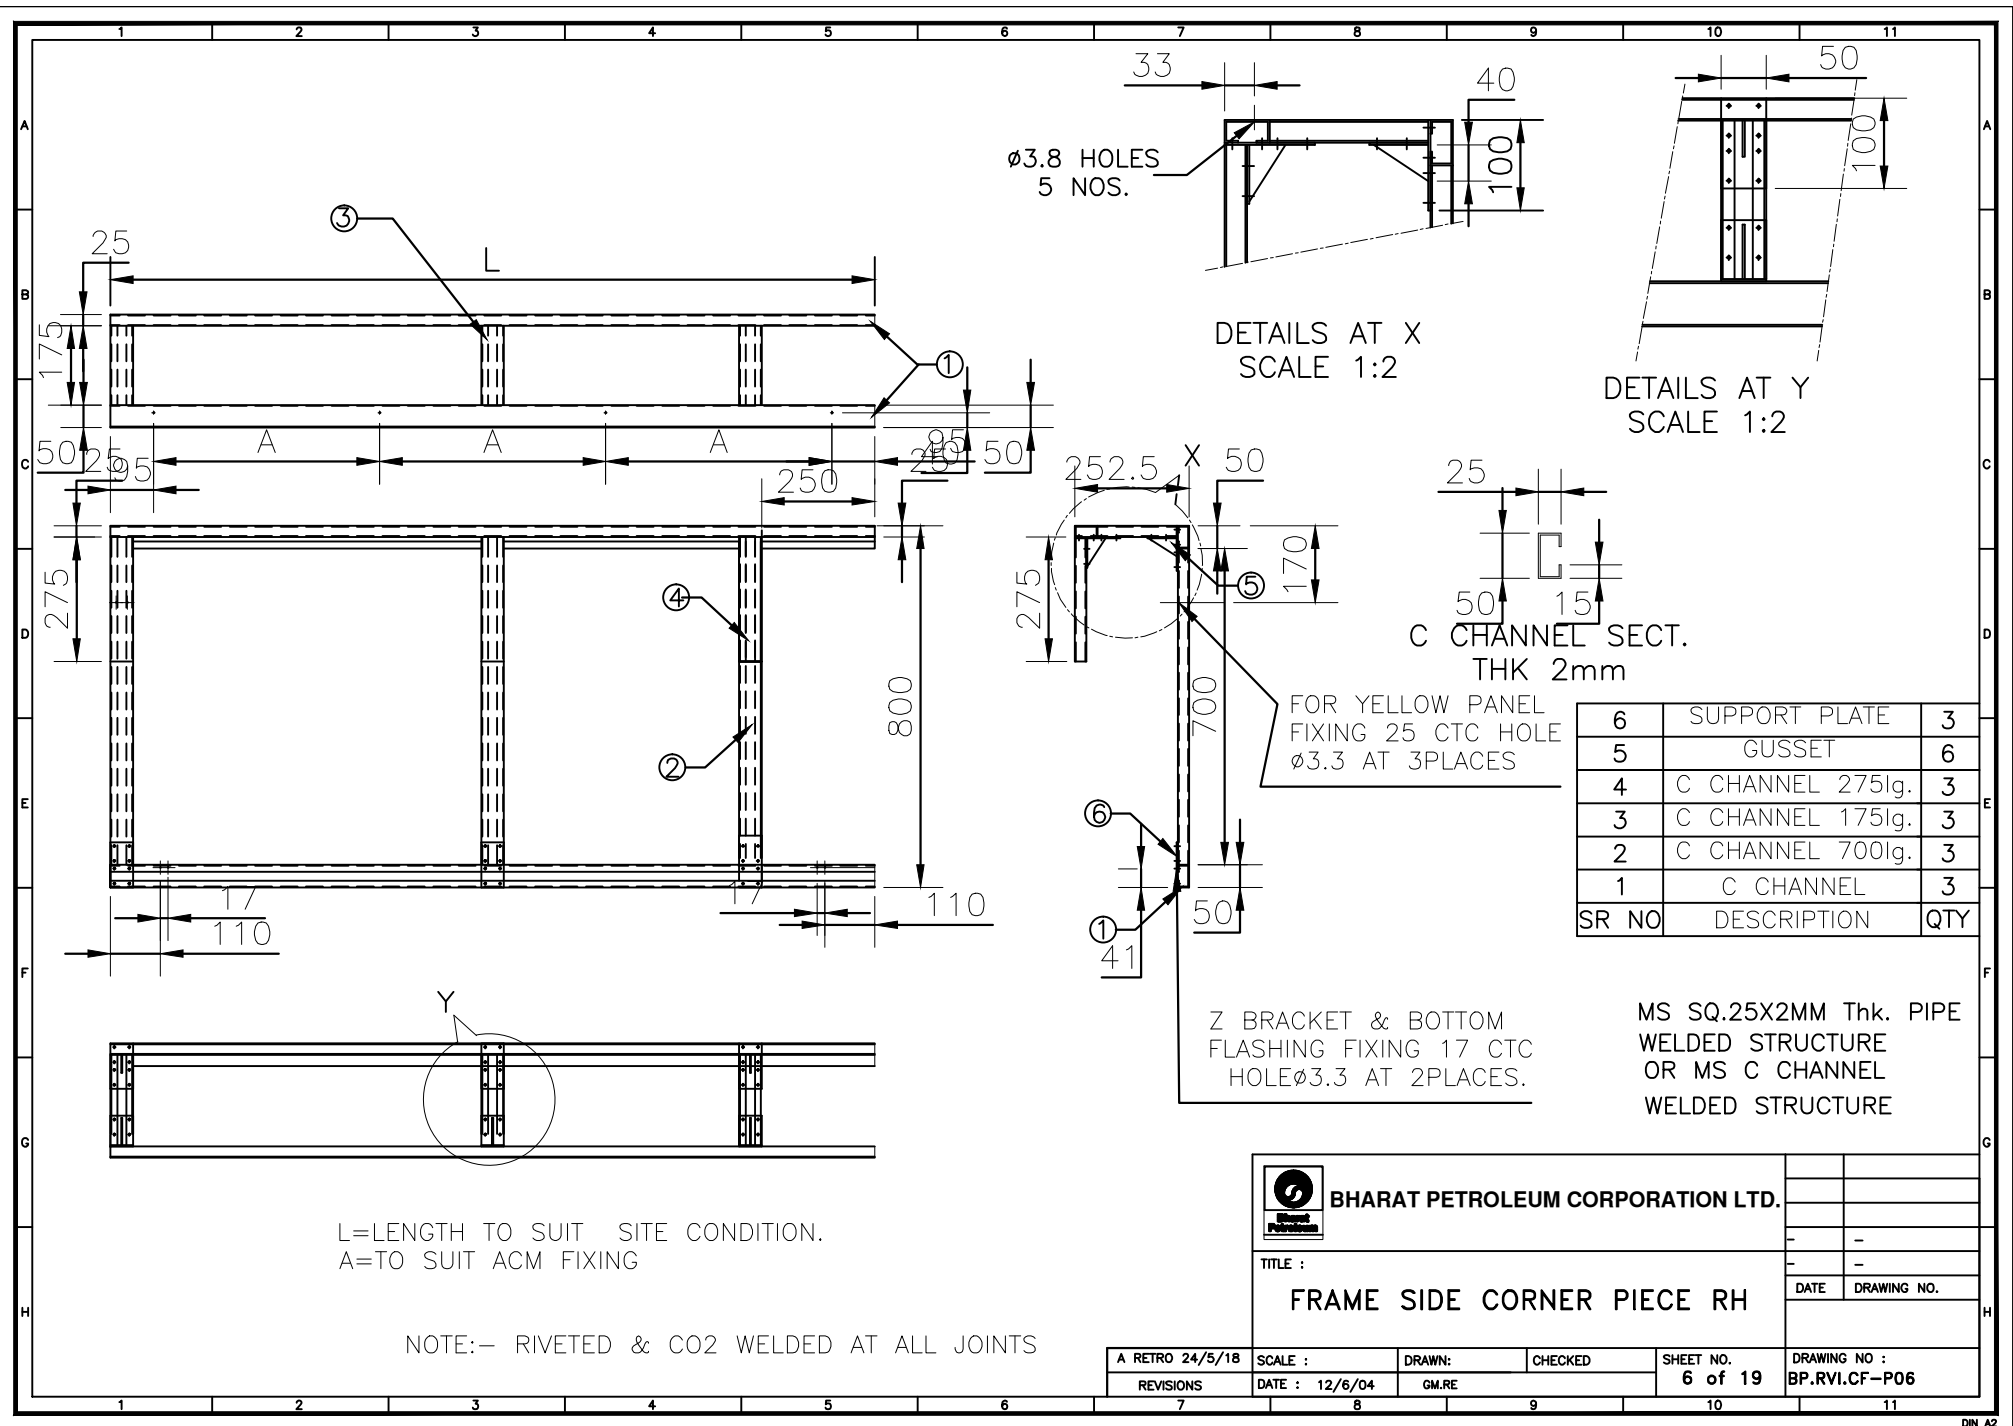

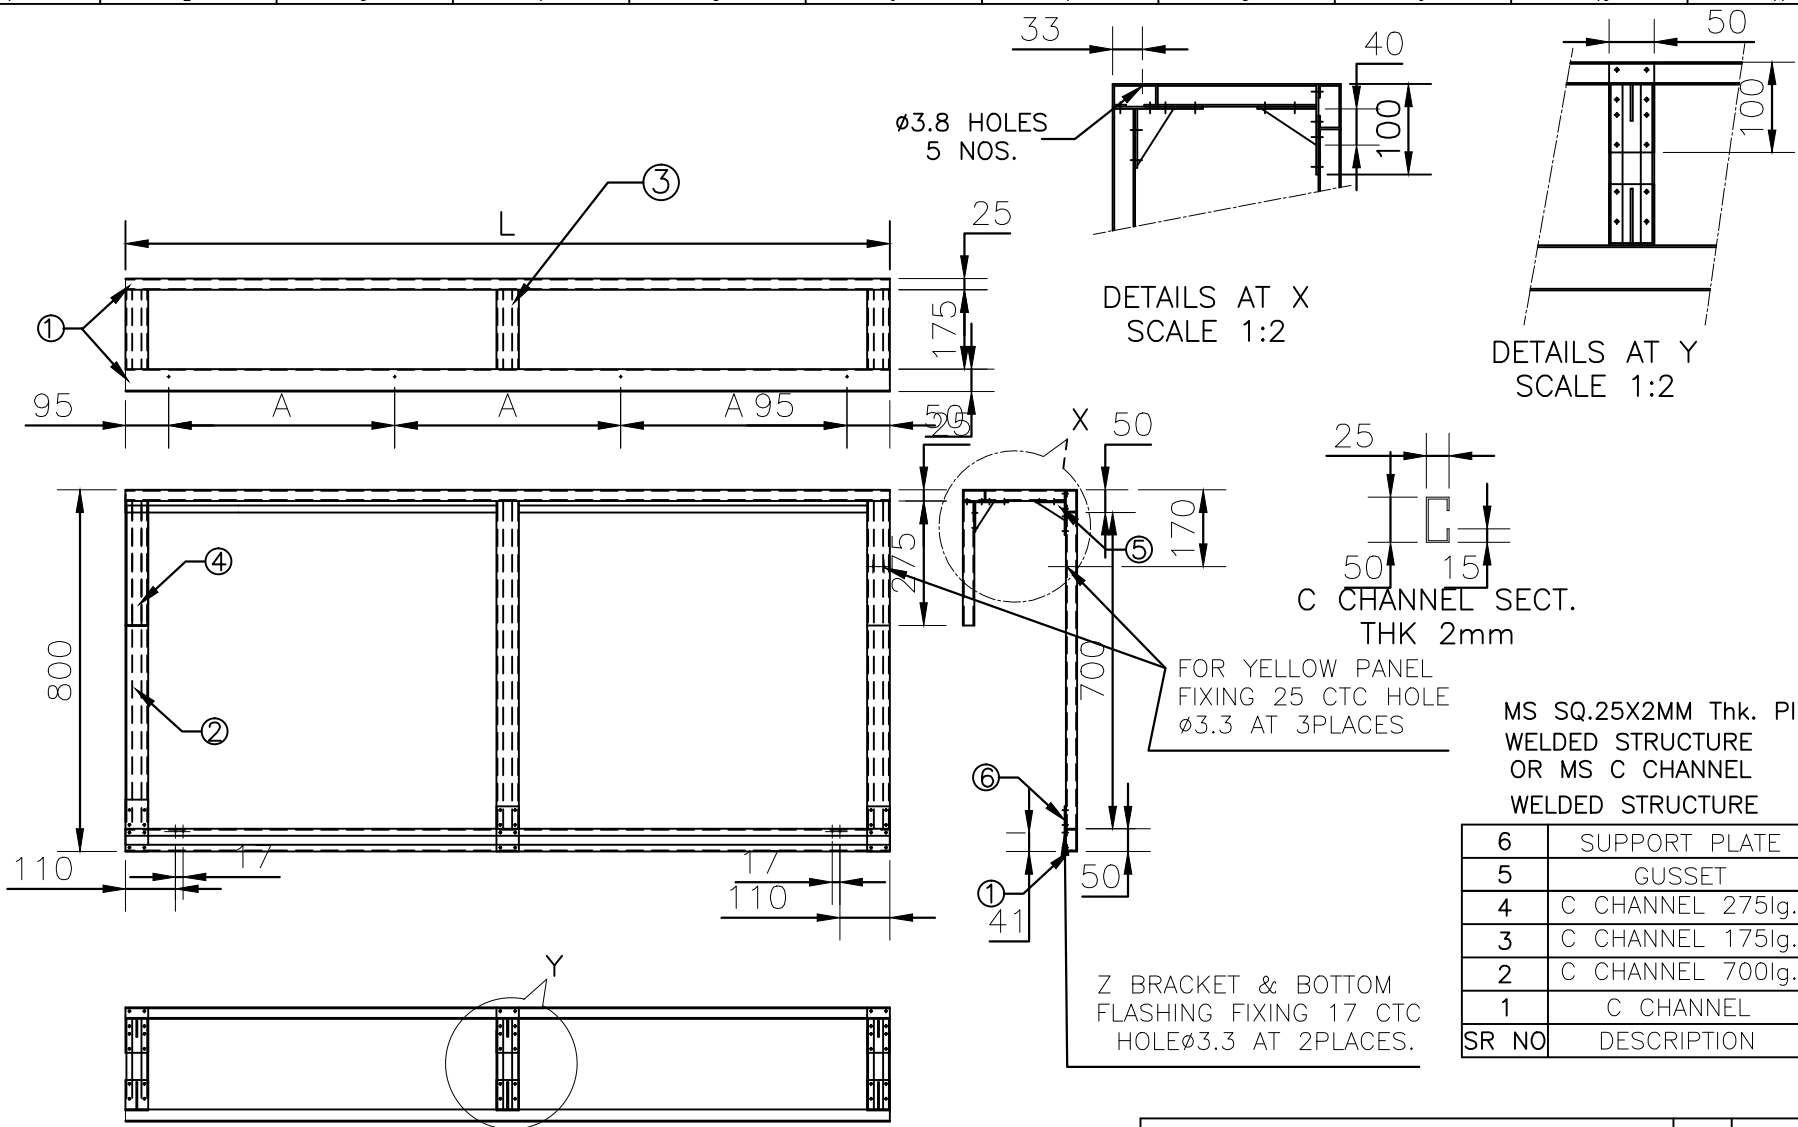

L=LENGTH TO SUIT SITE CONDITION.
A=TO SUIT ACM FIXING

NOTE:- RIVETED & CO2 WELDED AT ALL JOINTS

MS SQ.25X2MM Thk. PIPE
WELDED STRUCTURE
OR MS C CHANNEL
WELDED STRUCTURE

6	SUPPORT PLATE	3
5	GUSSET	6
4	C CHANNEL 275lg.	3
3	C CHANNEL 175lg.	3
2	C CHANNEL 700lg.	3
1	C CHANNEL	3
SR NO	DESCRIPTION	QTY



BHARAT PETROLEUM CORPORATION LTD.



TITLE :

FRAME STRAIGHT CORNER PIECE

A RETRO 24/5/18	SCALE :	DRAWN:	CHECKED	SHEET NO.
REVISIONS	DATE : 12/6/04	GM.RE		7 of 19

DRAWING NO :
BP.RVI.CF-P07

WAVE SIZE	6MT	7MT	8MT
A	2900	3400	1950x2

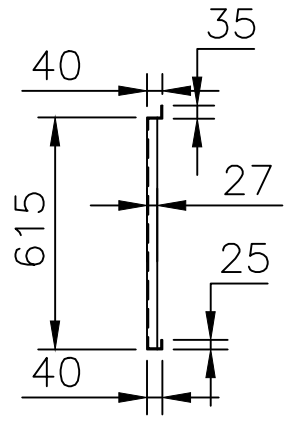 

MATERIAL-ACM YELLOW SHEET 3mm thk.





BHARAT PETROLEUM CORPORATION LTD.

TITLE :

SIGN FACE YELLOW

DATE	DRAWING NO.

REVISIONS	SCALE :	DRAWN:	CHECKED	SHEET NO.	DRAWING NO :
	DATE : 12/6/04	GM.RE		10 OF 19	BP.RVI.CF-P10

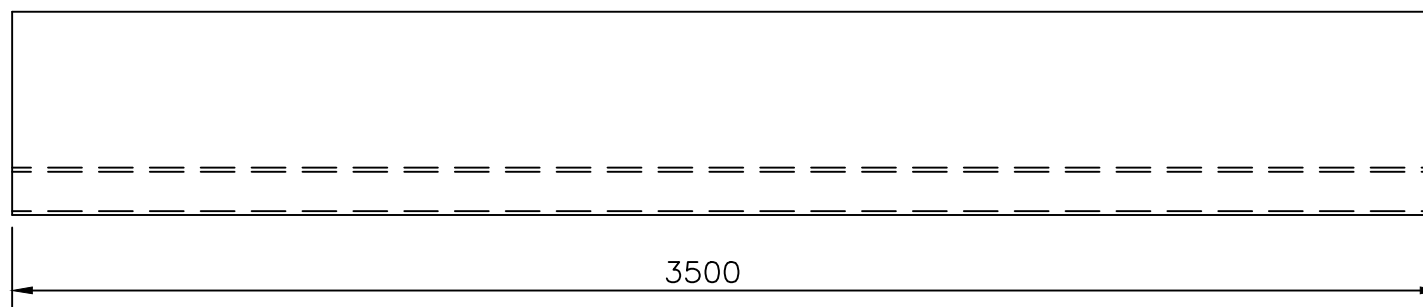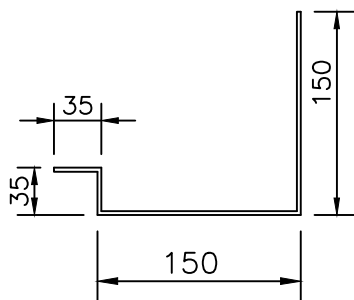

MATERIAL : WHITE ACM 3MM THK



BHARAT PETROLEUM CORPORATION LTD.

TITLE :




BOTTOM FASCIA

DATE DRAWING NO.

A RETRO 24/5/18
REVISIONS

SCALE :	DRAWN:	CHECKED	SHEET NO.
DATE : 12/6/04	GM.RE		11 of 19

DRAWING NO :
BP.RVI.CF-P11

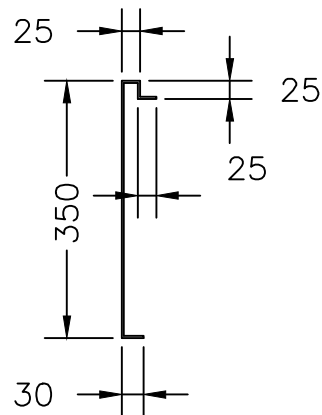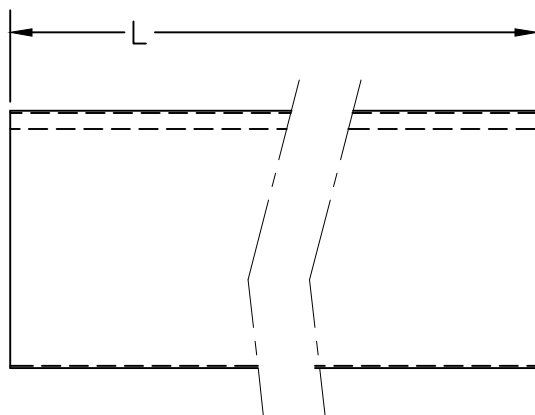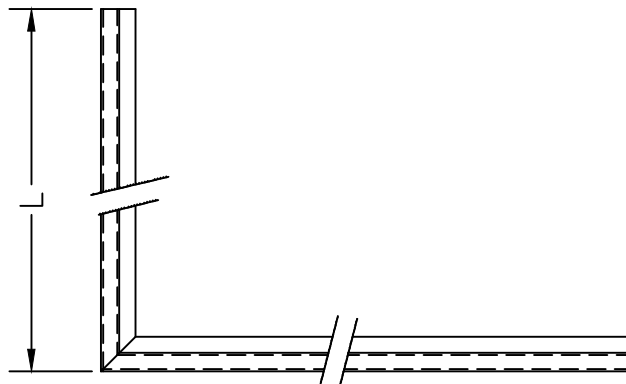

L= LENGTH AS PER REQUIREMENT
MATERIAL-ACM BLUE SHEET 3mm thk.



BHARAT PETROLEUM CORPORATION LTD.

TITLE :

CORNER PIECE FOR BLUE SIGN FACE

DATE DRAWING NO.


A RETRO 24/5/18
REVISIONS

SCALE :
DATE : 12/6/04

DRAWN:
GM.RE.

CHECKED
SHEET NO.
12 OF 19

DRAWING NO :
BP.RVI.CF-P12

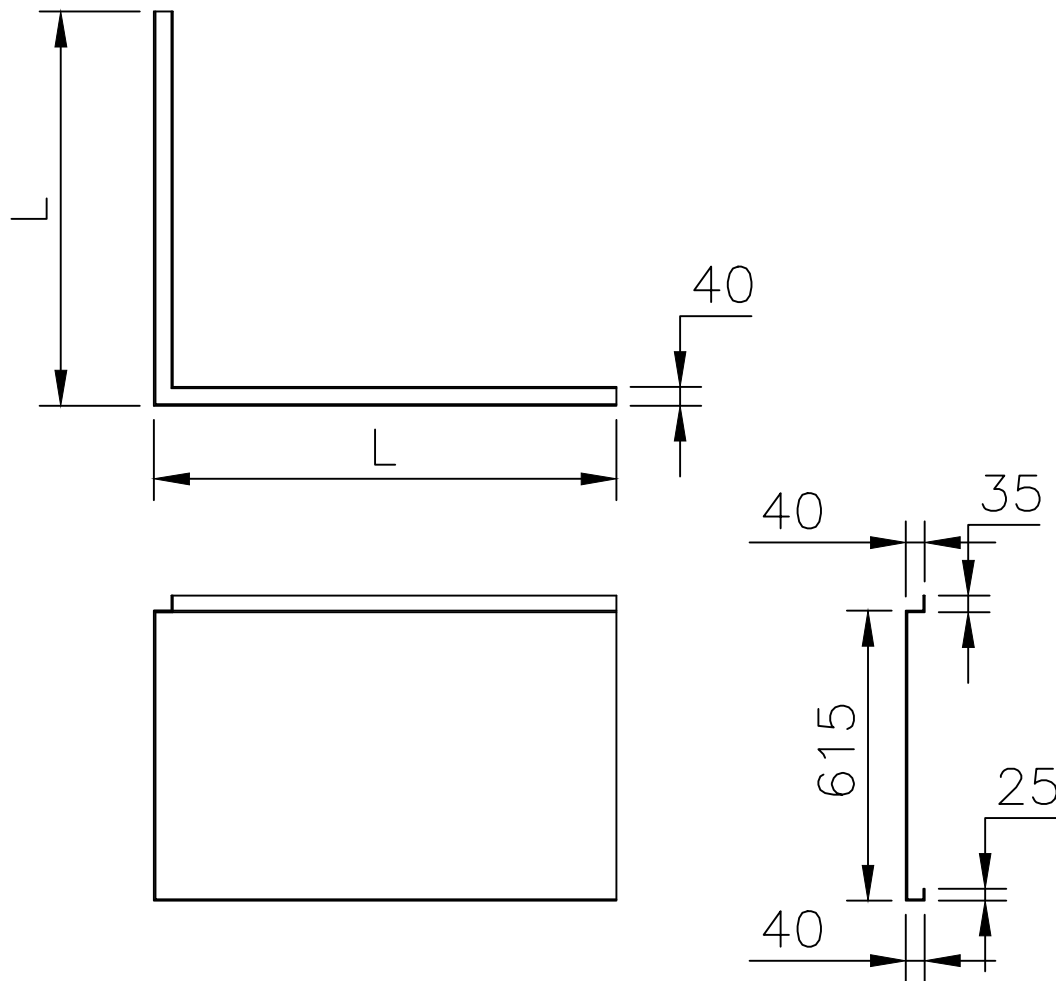

L= LENGTH AS PER REQUIREMENT.

MATERIAL-ACM YELLOW SHEET 3mm thk.



BHARAT PETROLEUM CORPORATION LTD.

TITLE :

CORNER PIECE FOR YELLOW SIGN FACE

A RETRO 24/5/18

REVISIONS

SCALE :

DATE : 12/6/04

DRAWN:

GM.RE



CHECKED

SHEET NO.

13 OF 19



DRAWING NO :

BP.RVI.CF-P13

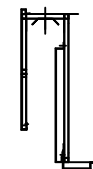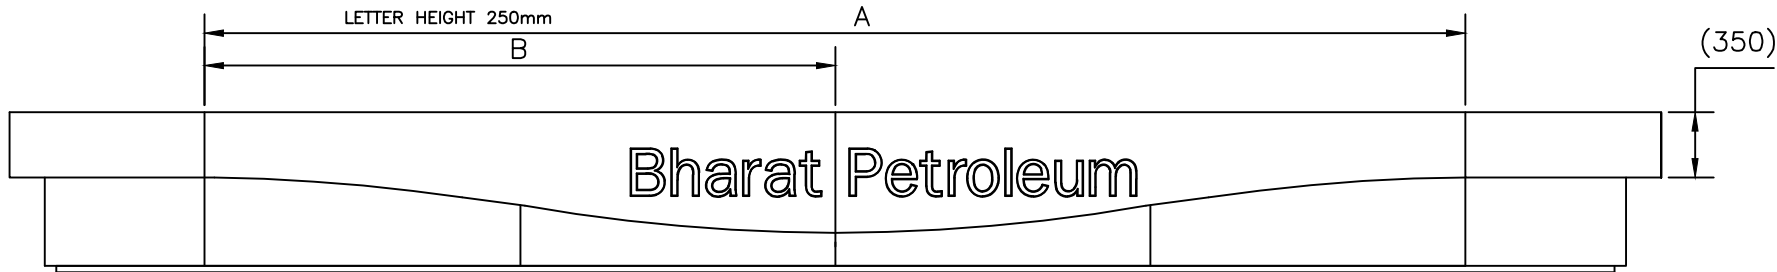

WAVE SIZE	6MT	7MT	8MT
A	5800	6800	7800
B	2900	3400	1950x4

WAVE SIZE	6MT	7MT	8MT	QTY.
A	5800	6800	7800	-
LENGTH	680	800	930	8

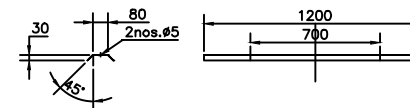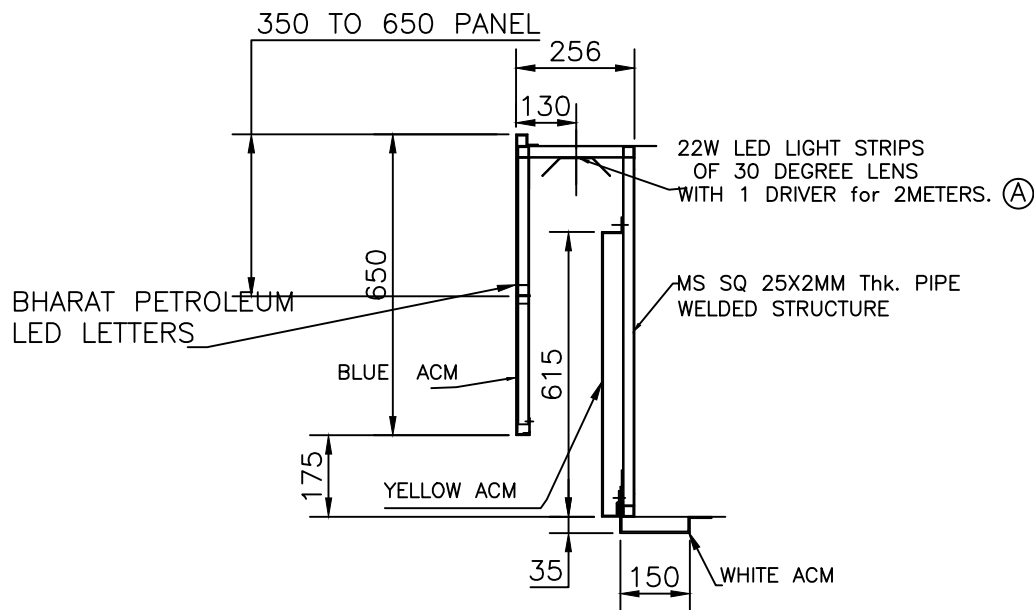


MATERIAL—CRCA STEEL SHEET 1mm
thk.IS:513.
LED FITTING MOUNTING BRACKET

ALL DIMENSIONS ARE IN MM.

A	WAS 1 DRIVER 4METER 3/5/19
REVISIONS	

 BHARAT PETROLEUM CORPORATION LTD.					
TITLE :					
LED LIGHT FITTING ARRANGEMENT FOR FASCIA					
SCALE : 1:9	DRAWN:	CHECKED	SHEET NO.	DATE	DRAWING NO.
DATE : 24/5/18	GM.RE		14 of 18		
				NUMBERS CROSSED OUT ARE SUPERSEDED DRAWINGS	
				DRAWING NO : BP.RVI.CF-P14	

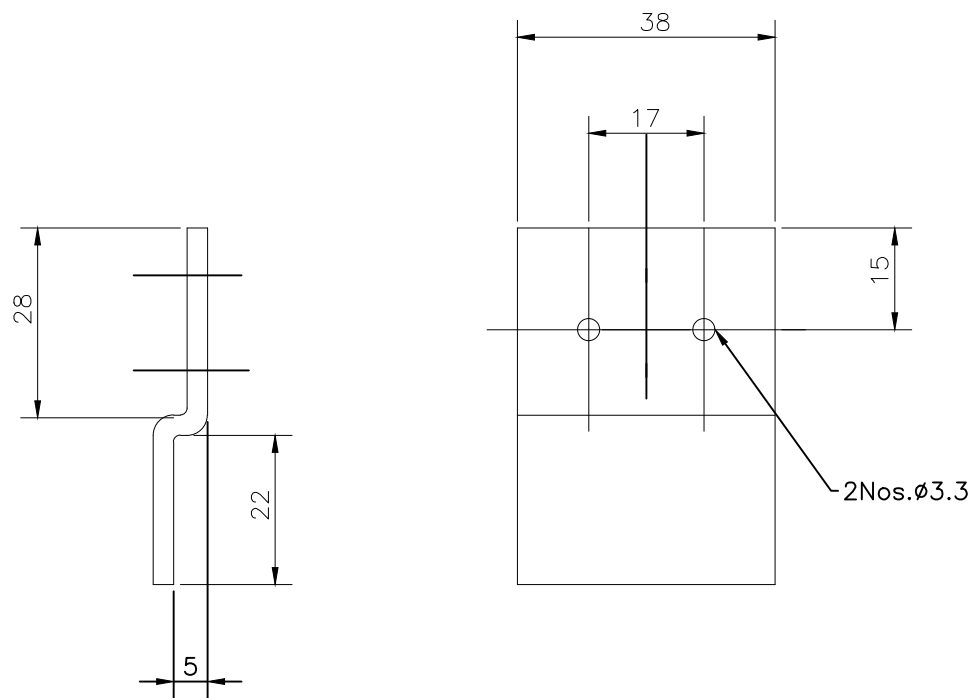

MATERIAL—ALUMINIUM SHEET 3mm thk.IS:737.





BHARAT PETROLEUM CORPORATION LTD.


TITLE :

Z BRACKET


A	RETRO 24/5/18	SCALE :	DRAWN	CHECKED	SHEET NO. 15 OF 19	DRAWING NO : BP.RVI.CF-P15
	REVISIONS	DATE : 12/6/04	GM.RE			

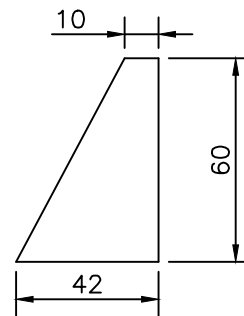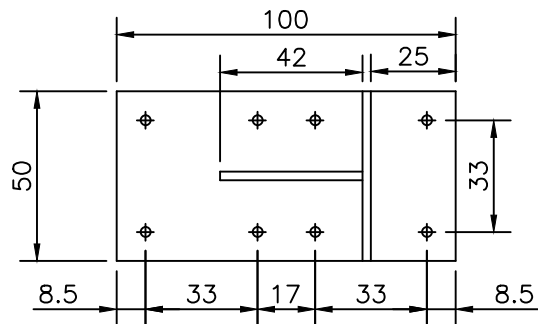


GUSSET

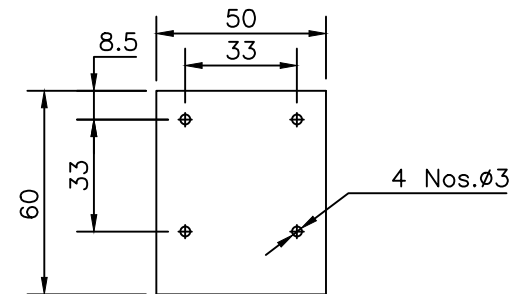

VERTICAL PLATE

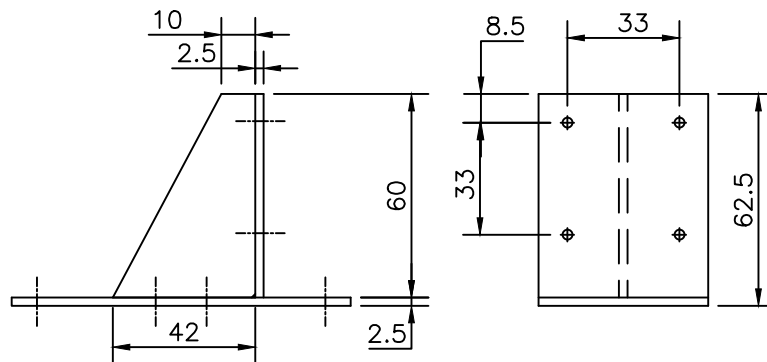

ASSY OF SUPPORT PLATE & GUSSET

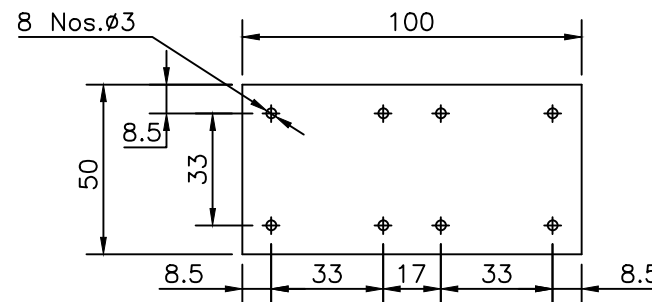

SUPPORT PLATE

SURFACE TREATMENT-ZINC PLATED YELLOW PASSIVATED 5 MICRON
MATERIAL-CRCA STEEL SHEET 2.5 THK.



BHARAT PETROLEUM CORPORATION LTD.

TITLE :

SUPPORT PLATE & GUSSET

A RETRO 24/5/18

REVISIONS

SCALE :

DATE : 12/6/04

DRAWN:

GM.RE


CHECKED

SHEET NO.


16 OF 19

DRAWING NO :

BP.RVI.CF-P16

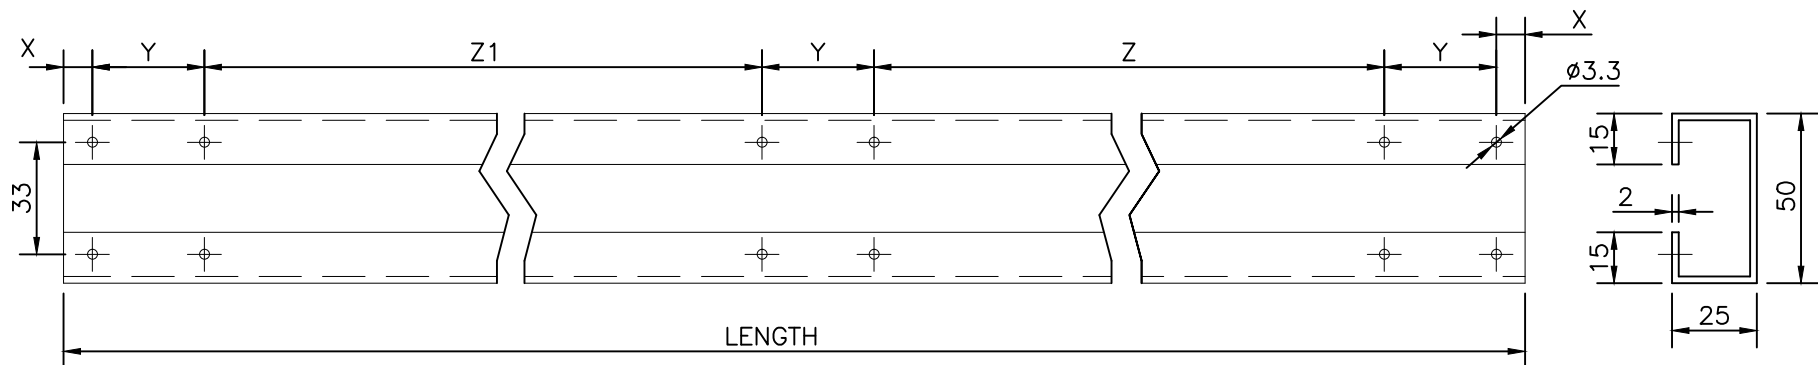

C CHANNEL CROSS SECTION

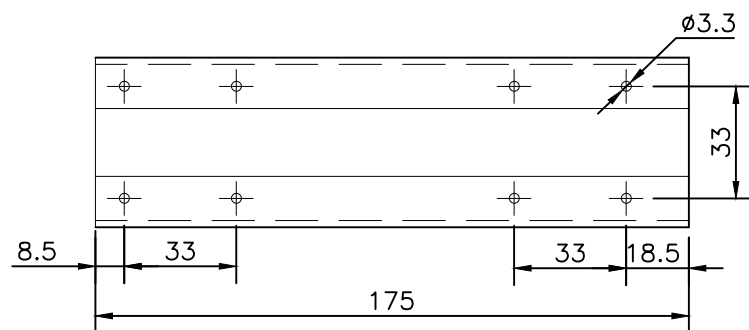

C CHANNEL LENGTH 175

MATERIAL—G.I. SHEET 2mm thk.IS:277.

L -1)FRAME LENGTH IS 1440mm for 6m MODULE.

L -1)FRAME LENGTH IS 1690mm for 7m MODULE.

L -2)FRAME LENGTH IS 1940mm for 8m MODULE.

7	575	18.5	33	---	---
6	525	18.5	33	---	---
5	425	18.5	33	---	---
4	315	18.5	33	---	---
3	275	18.5	33	---	---
2	700	8.5	33	617	---
1	(L)1690	8.5	33	787	787
SR NO	CHANNEL LENGTH	X	Y	Z	Z1



BHARAT PETROLEUM CORPORATION LTD.

TITLE :

CHANNELS FOR FASCIA STRUCTURE

A RETRO 24/5/18
REVISIONS

SCALE :
DATE : 12/6/04

DRAWN:
GM.RE

CHECKED

SHEET NO.
17 OF 19

DRAWING NO :
BP.RVI.CF-P17


Bharat

Petroleum

TEXT FONT—FRANKLIN GOTHIC BOOK
LETTER HEIGHT—250mm

LED ARRANGEMENT

	BHARAT PETROLEUM CORPORATION LTD.					
	TITLE :					
	BHARAT PETROLEUM LETTERS				DATE	DRAWING NO.
A	RETRO 25/5/18	SCALE :	DRAWN:	CHECKED	SHEET NO.	DRAWING NO :
	REVISIONS	DATE : 12/6/04	GM.RE		18 OF 19	BP.RVI.CF-P18


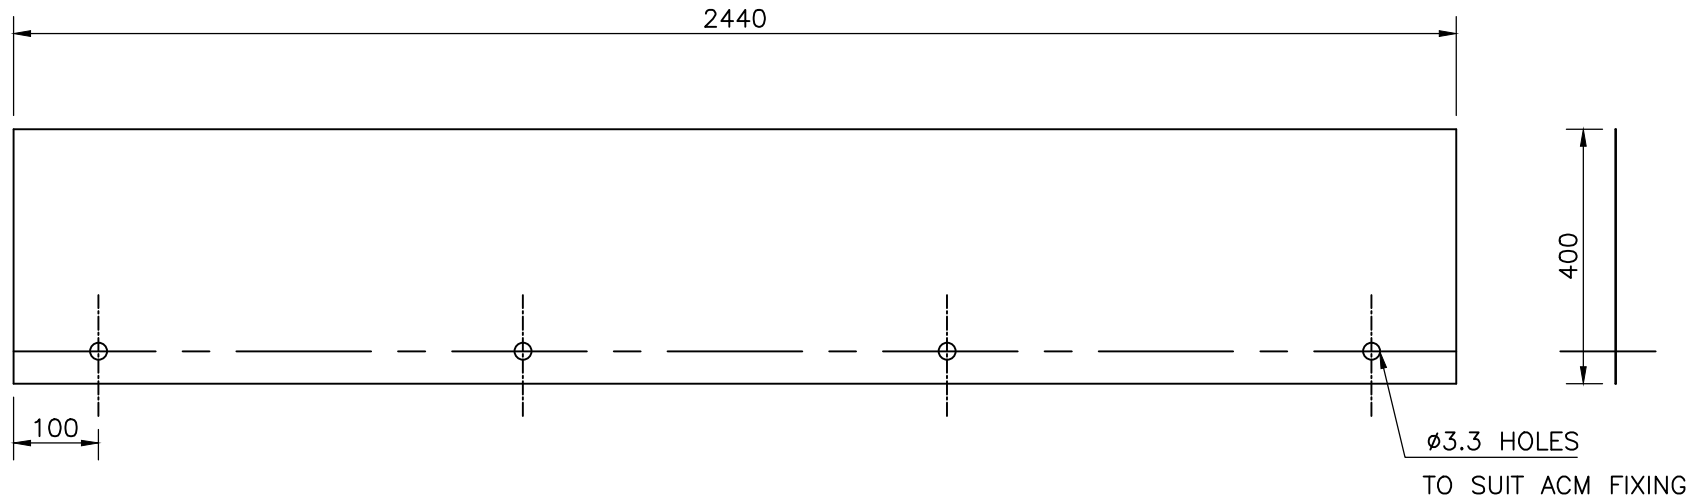


MATERIAL—GI SHEET 1mm THK.IS:277.

ALL DIMS ARE IN MM.



A	RETRO 24/5/18
REVISIONS	

		BHARAT PETROLEUM CORPORATION LTD.			
		TITLE :		DATE	DRAWING NO.
		FLASHING TOP (ROOFING SHEET)			
SCALE :		DRAWN	CHECKED	SHEET NO.	DRAWING NO :
DATE : 12/6/04		GM. RE		19 OF 19	BP.RVI.CF-P19

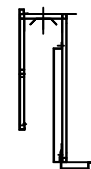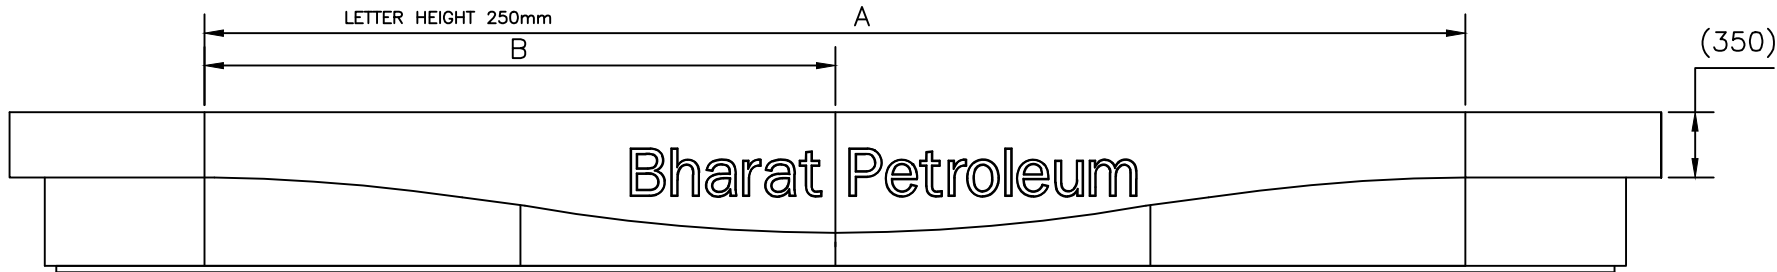

WAVE SIZE	6MT	7MT	8MT
A	5800	6800	7800
B	2900	3400	1950x4

WAVE SIZE	6MT	7MT	8MT	QTY.
A	5800	6800	7800	-
LENGTH	680	800	930	8

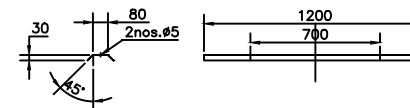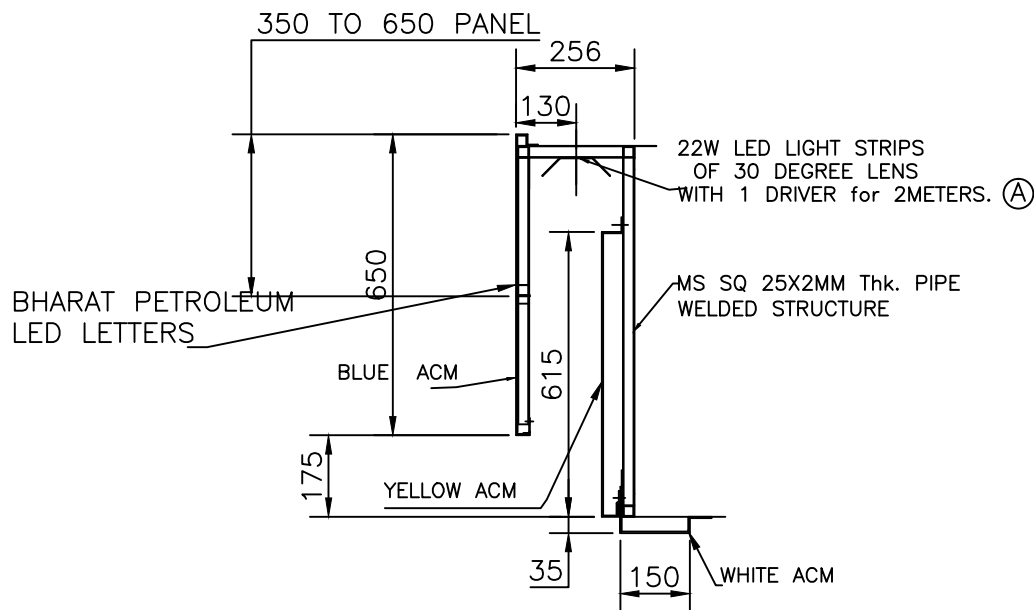


MATERIAL—CRCA STEEL SHEET 1mm
thk.IS:513.
LED FITTING MOUNTING BRACKET

ALL DIMENSIONS ARE IN MM.


A	WAS 1 DRIVER 4METER 3/5/19
REVISIONS	

 BHARAT PETROLEUM CORPORATION LTD.					
TITLE :					
LED LIGHT FITTING ARRANGEMENT FOR FASCIA					
SCALE : 1:9	DRAWN:	CHECKED	SHEET NO.	DATE	DRAWING NO.
DATE : 24/5/18	GM.RE		14 of 18		
				NUMBERS CROSSED OUT ARE SUPERSEDED DRAWINGS	
				DRAWING NO : BP.RVI.CF-P14	

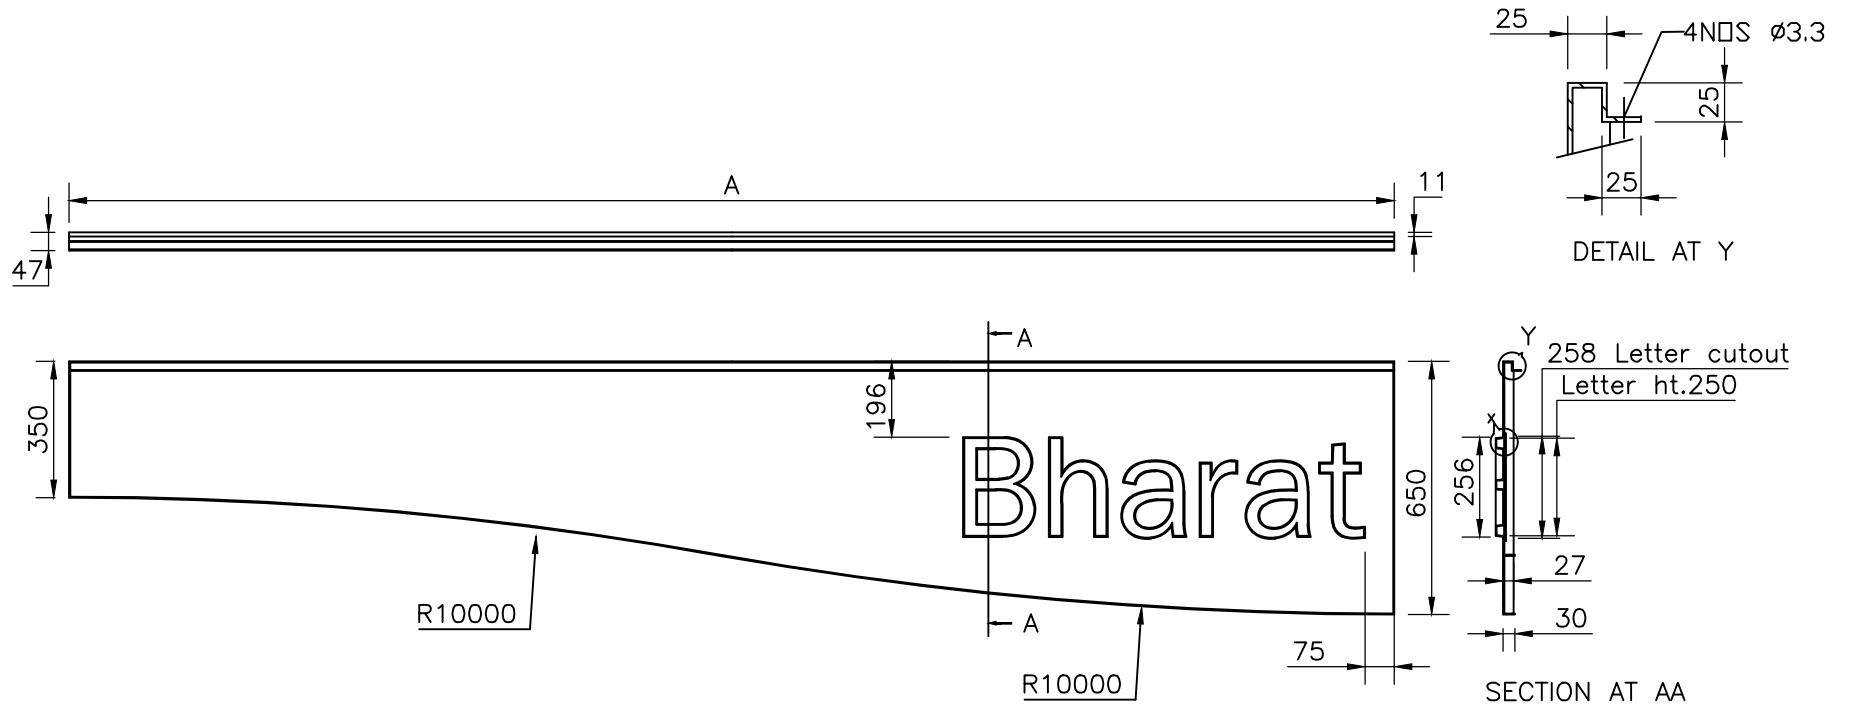


NOTE-LETTERS WILL BE ONLY IN ONE MODULE AT 6M,7M&8M OTHERS MODULES WILL HAVE SAME CONSTRUCTION EXCEPT CUTOUT FOR LETTER.

MATERIAL-ACM BLUE SHEET 3mm thk.
FONT-FRANKLIN GOTHIC BOOK


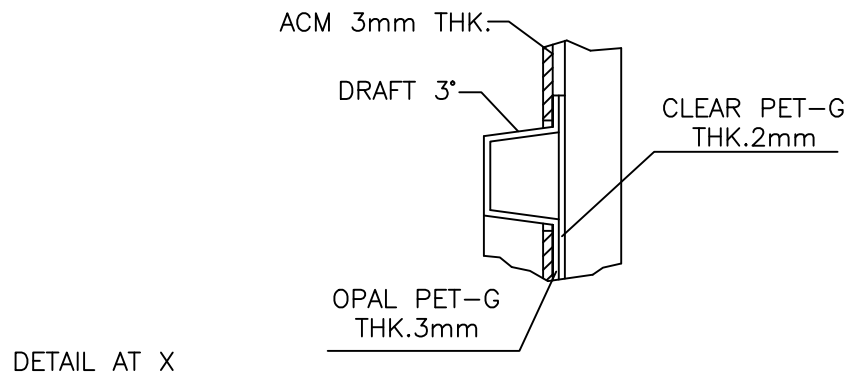


 BHARAT PETROLEUM CORPORATION LTD.				
TITLE :				
SIGN FACE BLUE LH				
SCALE :	DRAWN:SUK	CHECKED	SHEET NO.	DRAWING NO :
DATE : 24/04/19	Sr. Mgr. (DESIGN & DEVP.)		8 OF 19	BP.RVI.CF-P08


WAVE SIZE	6MT	7MT	8MT
A	2900	3400	1950x2

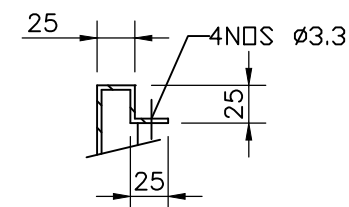

DETAIL AT Y

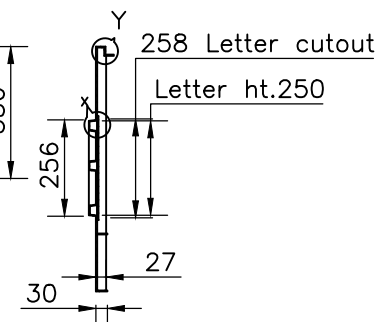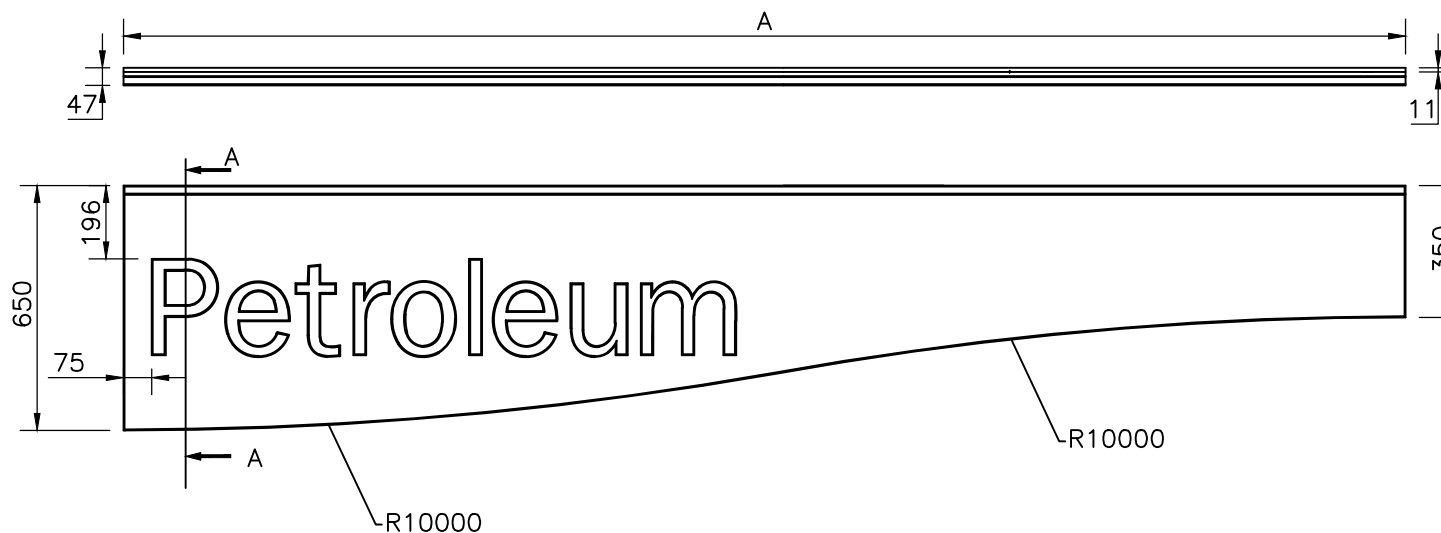

SECTION AT AA

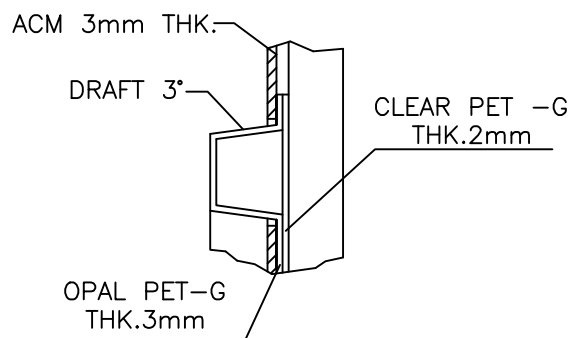

DETAIL AT X

NOTE-LETTERS WILL BE ONLY IN ONE MODULE AT 6M,7M&8M OTHERS MODULES WILL HAVE SAME CONSTRUCTION EXCEPT CUTOUT FOR LETTER.

MATERIAL-ACM BLUE SHEET 3mm thk.
FONT-FRANKLIN GOTHIC BOOK

 BHARAT PETROLEUM CORPORATION LTD.					
TITLE :				DATE	DRAWING NO.
SIGN FACE BLUE RH					
SCALE :	DRAWN:SUK	CHECKED	SHEET NO.	DRAWING NO :	
DATE : 24/04/19	Sr. Mgr. (DESIGN & DEVP.)		9 OF 19	BP.RVI.CF-P09	