


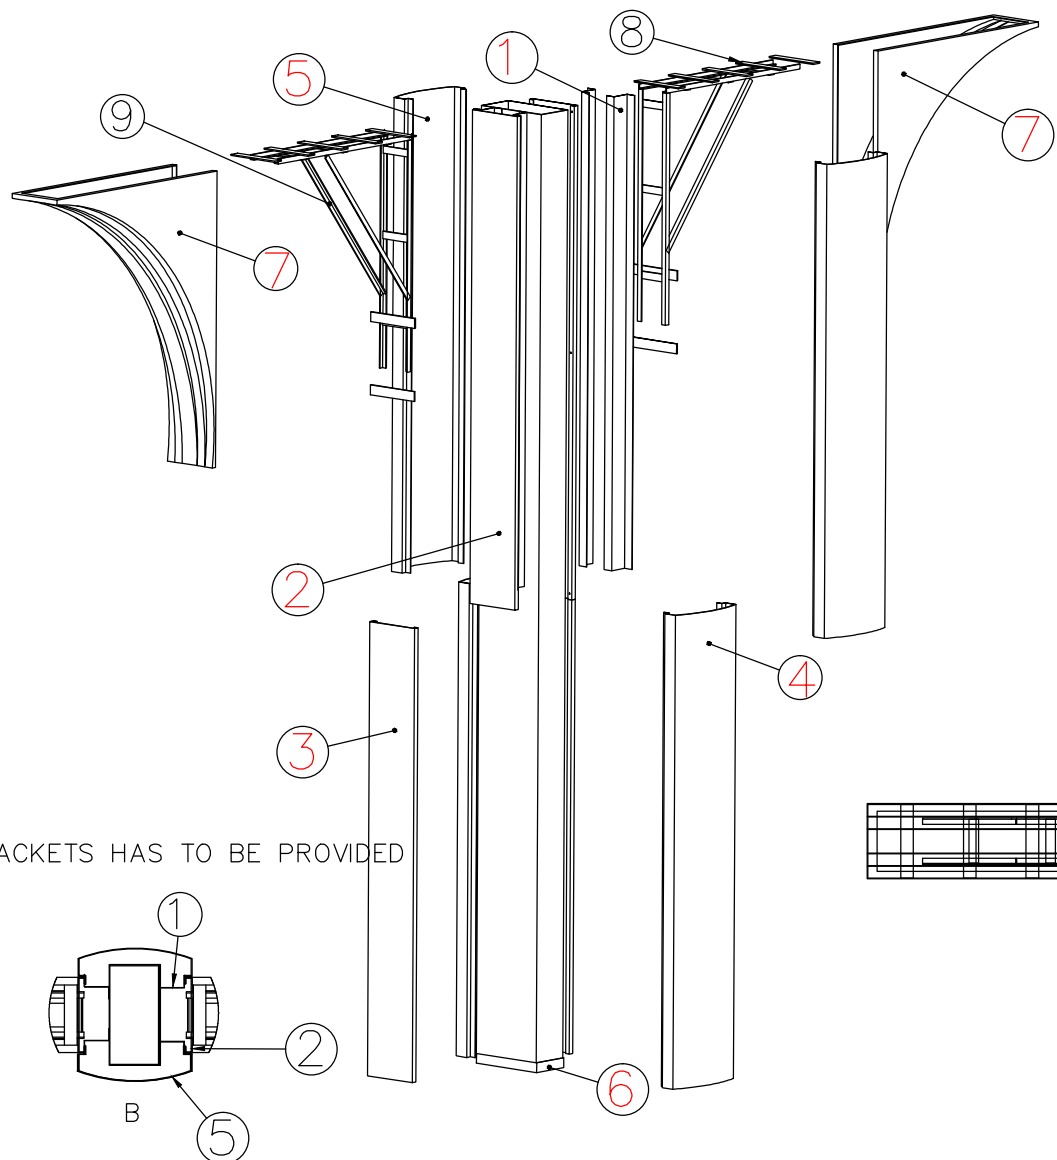

9	STRUCTURE FOR ARCH	2
8	SLIDING CHANNEL FOR ARCH	2
7	ARCH FOR BPCL	2
6	BOTTOM COVER FOR CLADDING	1
5	CLADDING CURVED 2500mm	2
4	CLADDING CURVED 1000mm	2
3	CLADDING STRAIGHT 1000mm	2
2	CLADDING STRAIGHT 2500mm	2
1	Z BRACKET	8
SR.NO	NAME OF COMPONENT	QTY



Z BRACKETS HAS TO BE PROVIDED

ORIENTATION OF THE CLADDING IS CHANGED DEPEND UPON THE SITE

 BHARAT PETROLEUM CORPORATION LTD.					
TITLE :					
COLUMN CLADDING FOR BPCL(5M)				DATE	DRAWING NO.
				NUMBERS CROSSED OUT ARE SUPERSEDED DRAWINGS	
SCALE : 1:22	DRAWN:	CHECKED	SHEET NO.	DRAWING NO :	
DATE : 23/5/18	GM.RE		1 of 11	BP.RVI.CA-A01	

REVISIONS

10	PILLER ARCH LIGHT	1
9	STRUCTURE FOR ARCH	4
8	SLIDING CHANNEL FOR ARCH	4
7	ARCH FOR BPCL	4
6	BOTTOM COVER FOR CLADDING	2
5	REMAIN CLADDING CURVED (2500mm)	4
4	CLADDING CURVED 2500mm(CUTOOUT FOR NO SIGN)	4
3	CLADDING STRAIGHT (2750MM)	2
2	CLADDING STRAIGHT (3500mm)	2
1	ANGLE	16
SR.NO	DESCRIPTION	QTY.

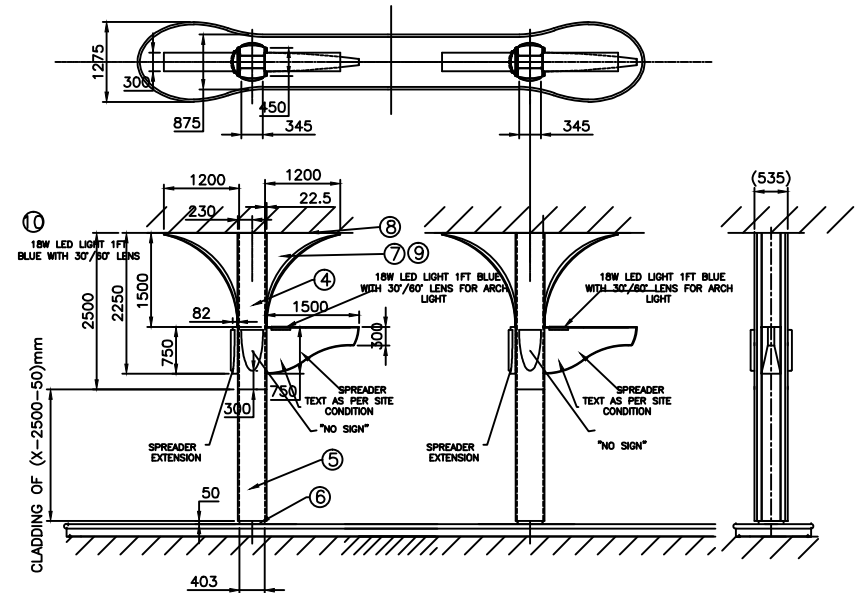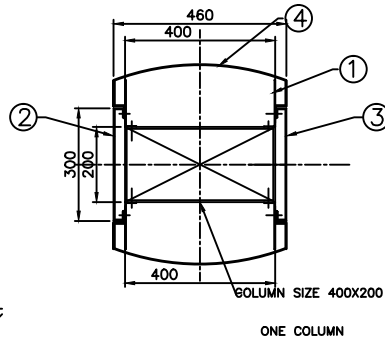

BELOW 5M COLUMN HEIGHT



BHARAT PETROLEUM CORPORATION LTD.

TITLE :

COLUMN CLADDING FOR BPCL(5M)
BELOW 5m COLUMN HEIGHT

SCALE : 1:22

DRAWN:

	CHECKED
--	---------

SHEET NO.

	DRAWING NO :
--	--------------

NUMBERS CROSSED OUT ARE SUPERSEDED DRAWINGS


REVISIONS

DATE : 23/5/18


	GM.RE
--	-------

2 of 11

BP.RVI.CA-A02a

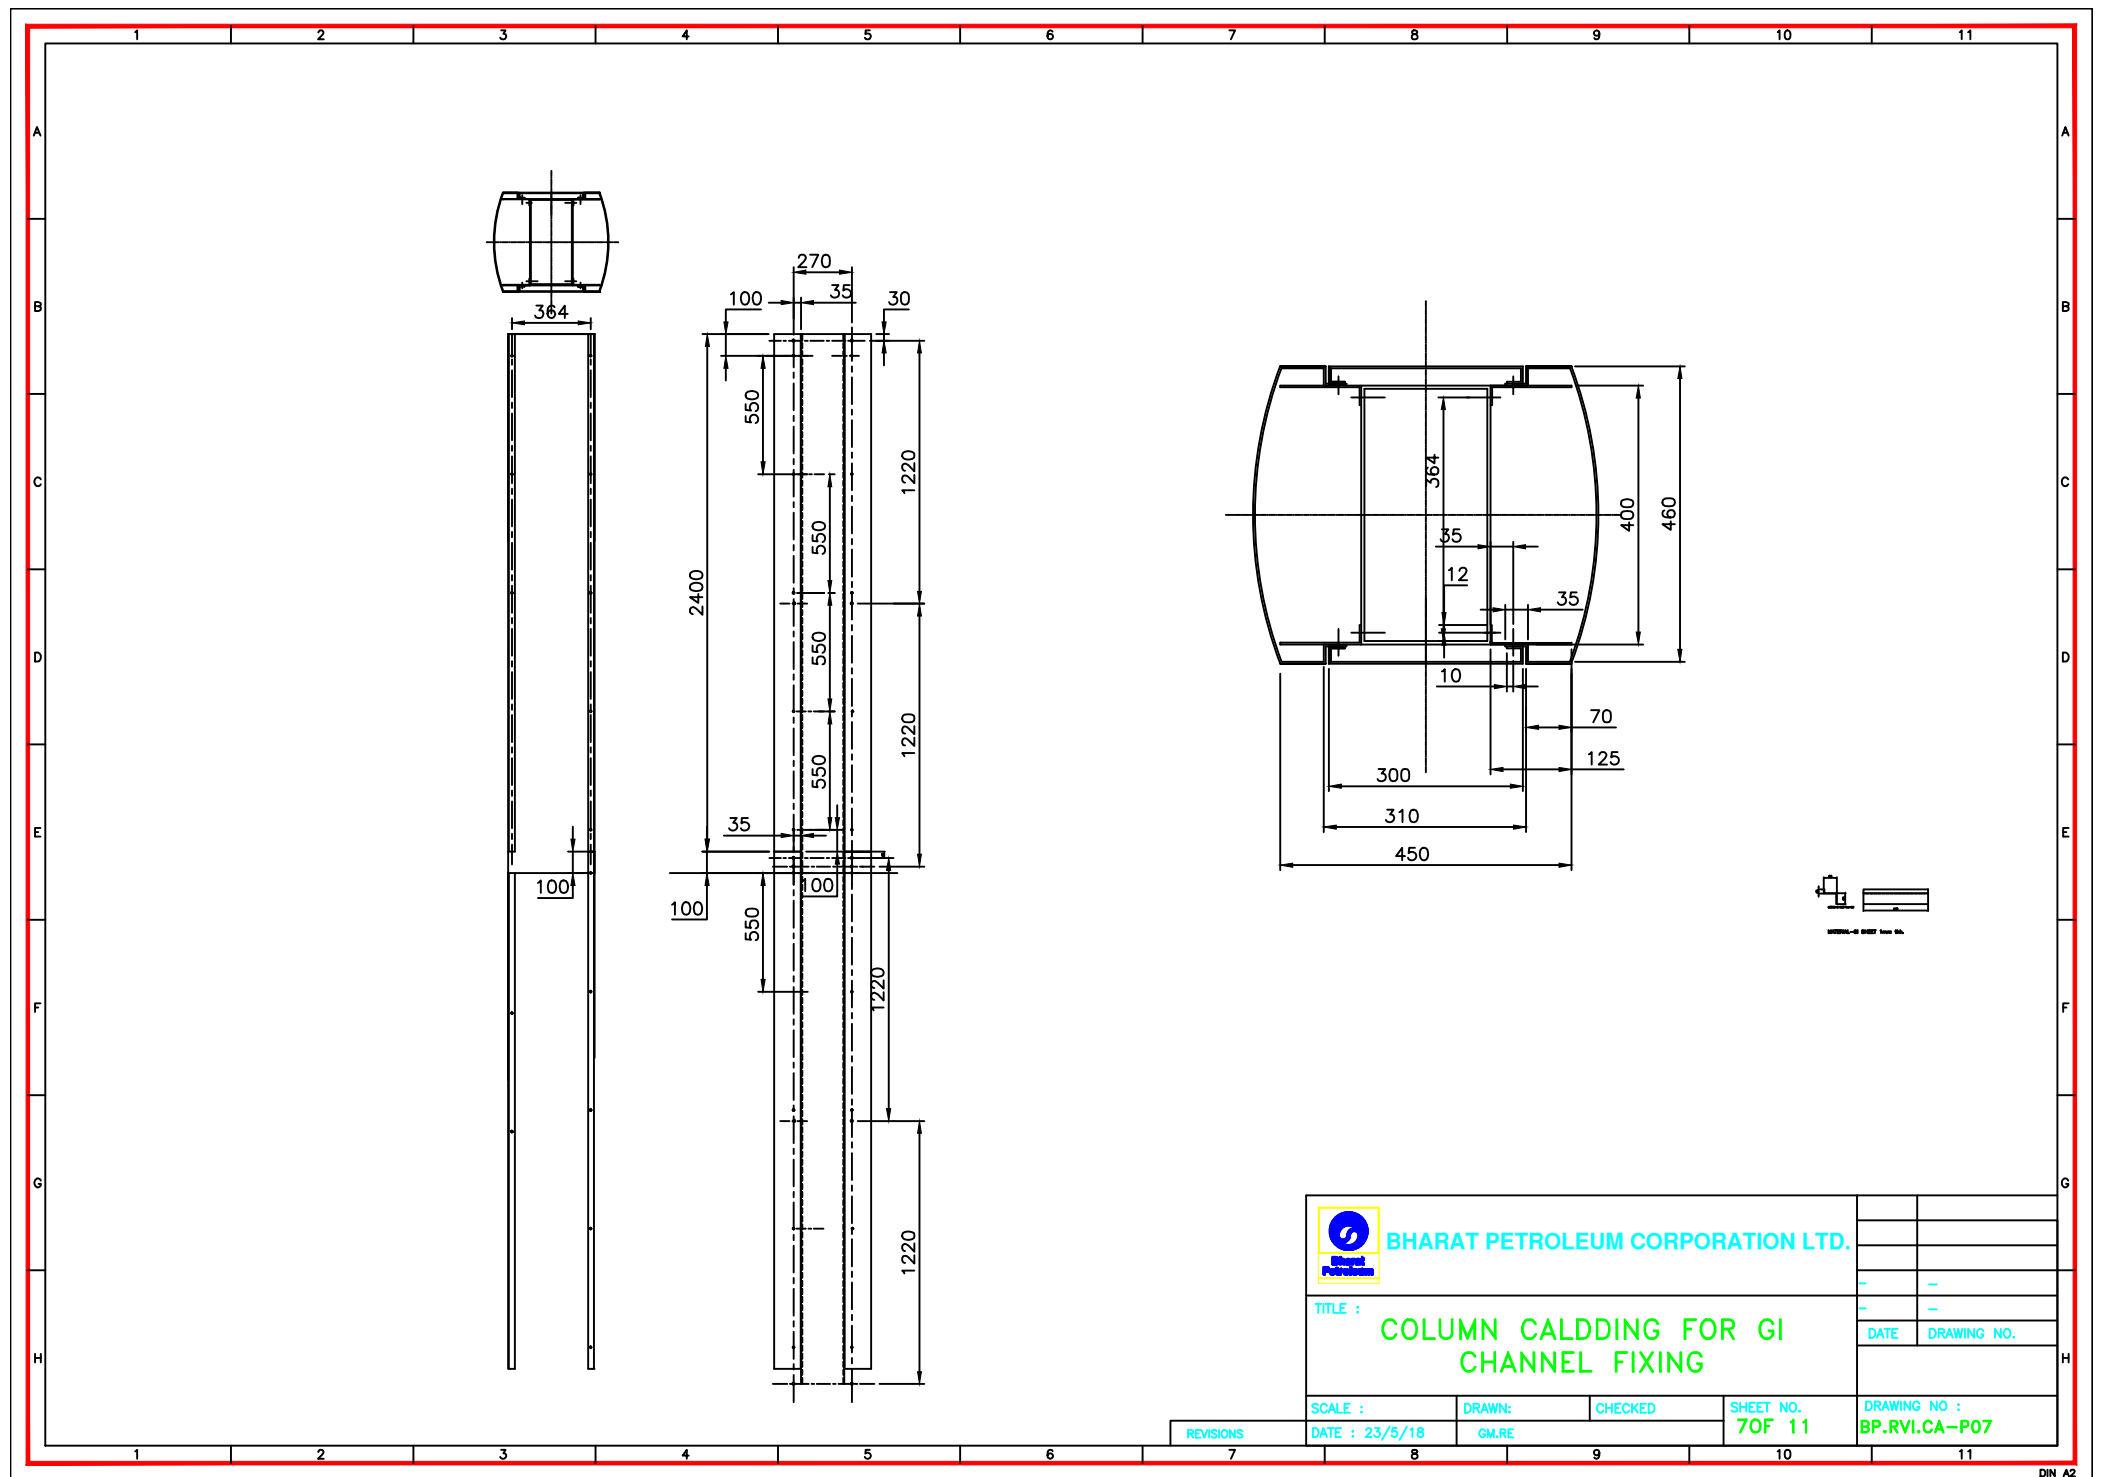



				BHARAT PETROLEUM CORPORATION LTD.			
TITLE : COLUMN CALDDING FOR GI CHANNEL FIXING						-	-
						-	-
						DATE	DRAWING NO.
SCALE :		DRAWN:	CHECKED	SHEET NO.	DRAWING NO :	F	
DATE : 23/5/18		GM.RE		70F 11	BP.RVI.CA-P07		

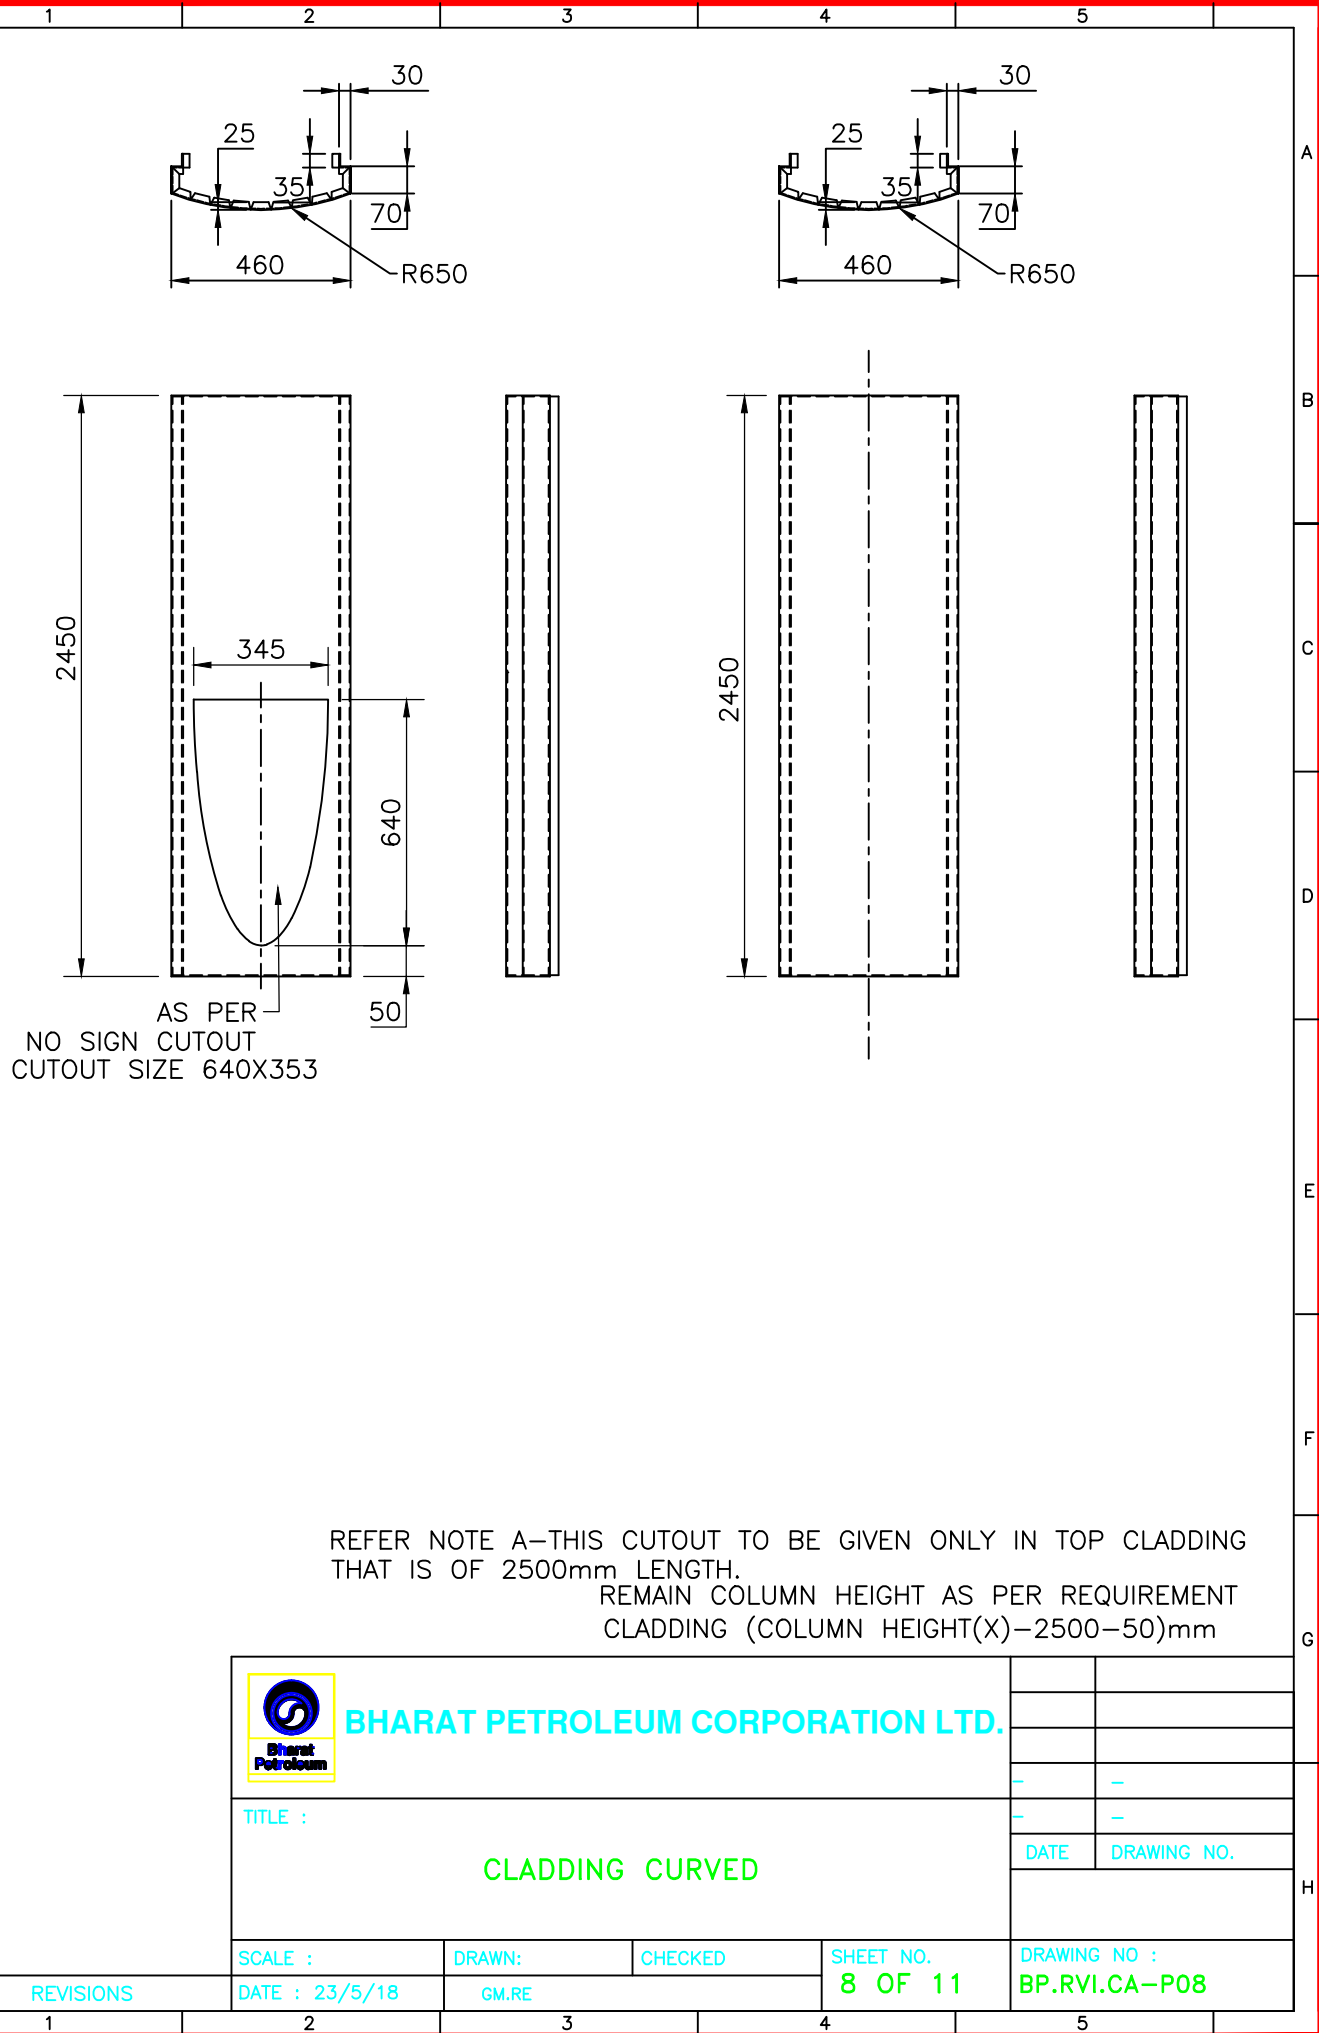


REFER NOTE A—THIS CUTOUT TO BE GIVEN ONLY IN TOP CLADDING THAT IS OF 2500mm LENGTH.
REMAIN COLUMN HEIGHT AS PER REQUIREMENT
CLADDING (COLUMN HEIGHT(X)–2500–50)mm

 BHARAT PETROLEUM CORPORATION LTD.			
TITLE : CLADDING CURVED		DATE	DRAWING NO.
SCALE :	DRAWN:	CHECKED	SHEET NO.
DATE : 23/5/18	GM.RE		8 OF 11
DRAWING NO : BP.RVI.CA–P08			

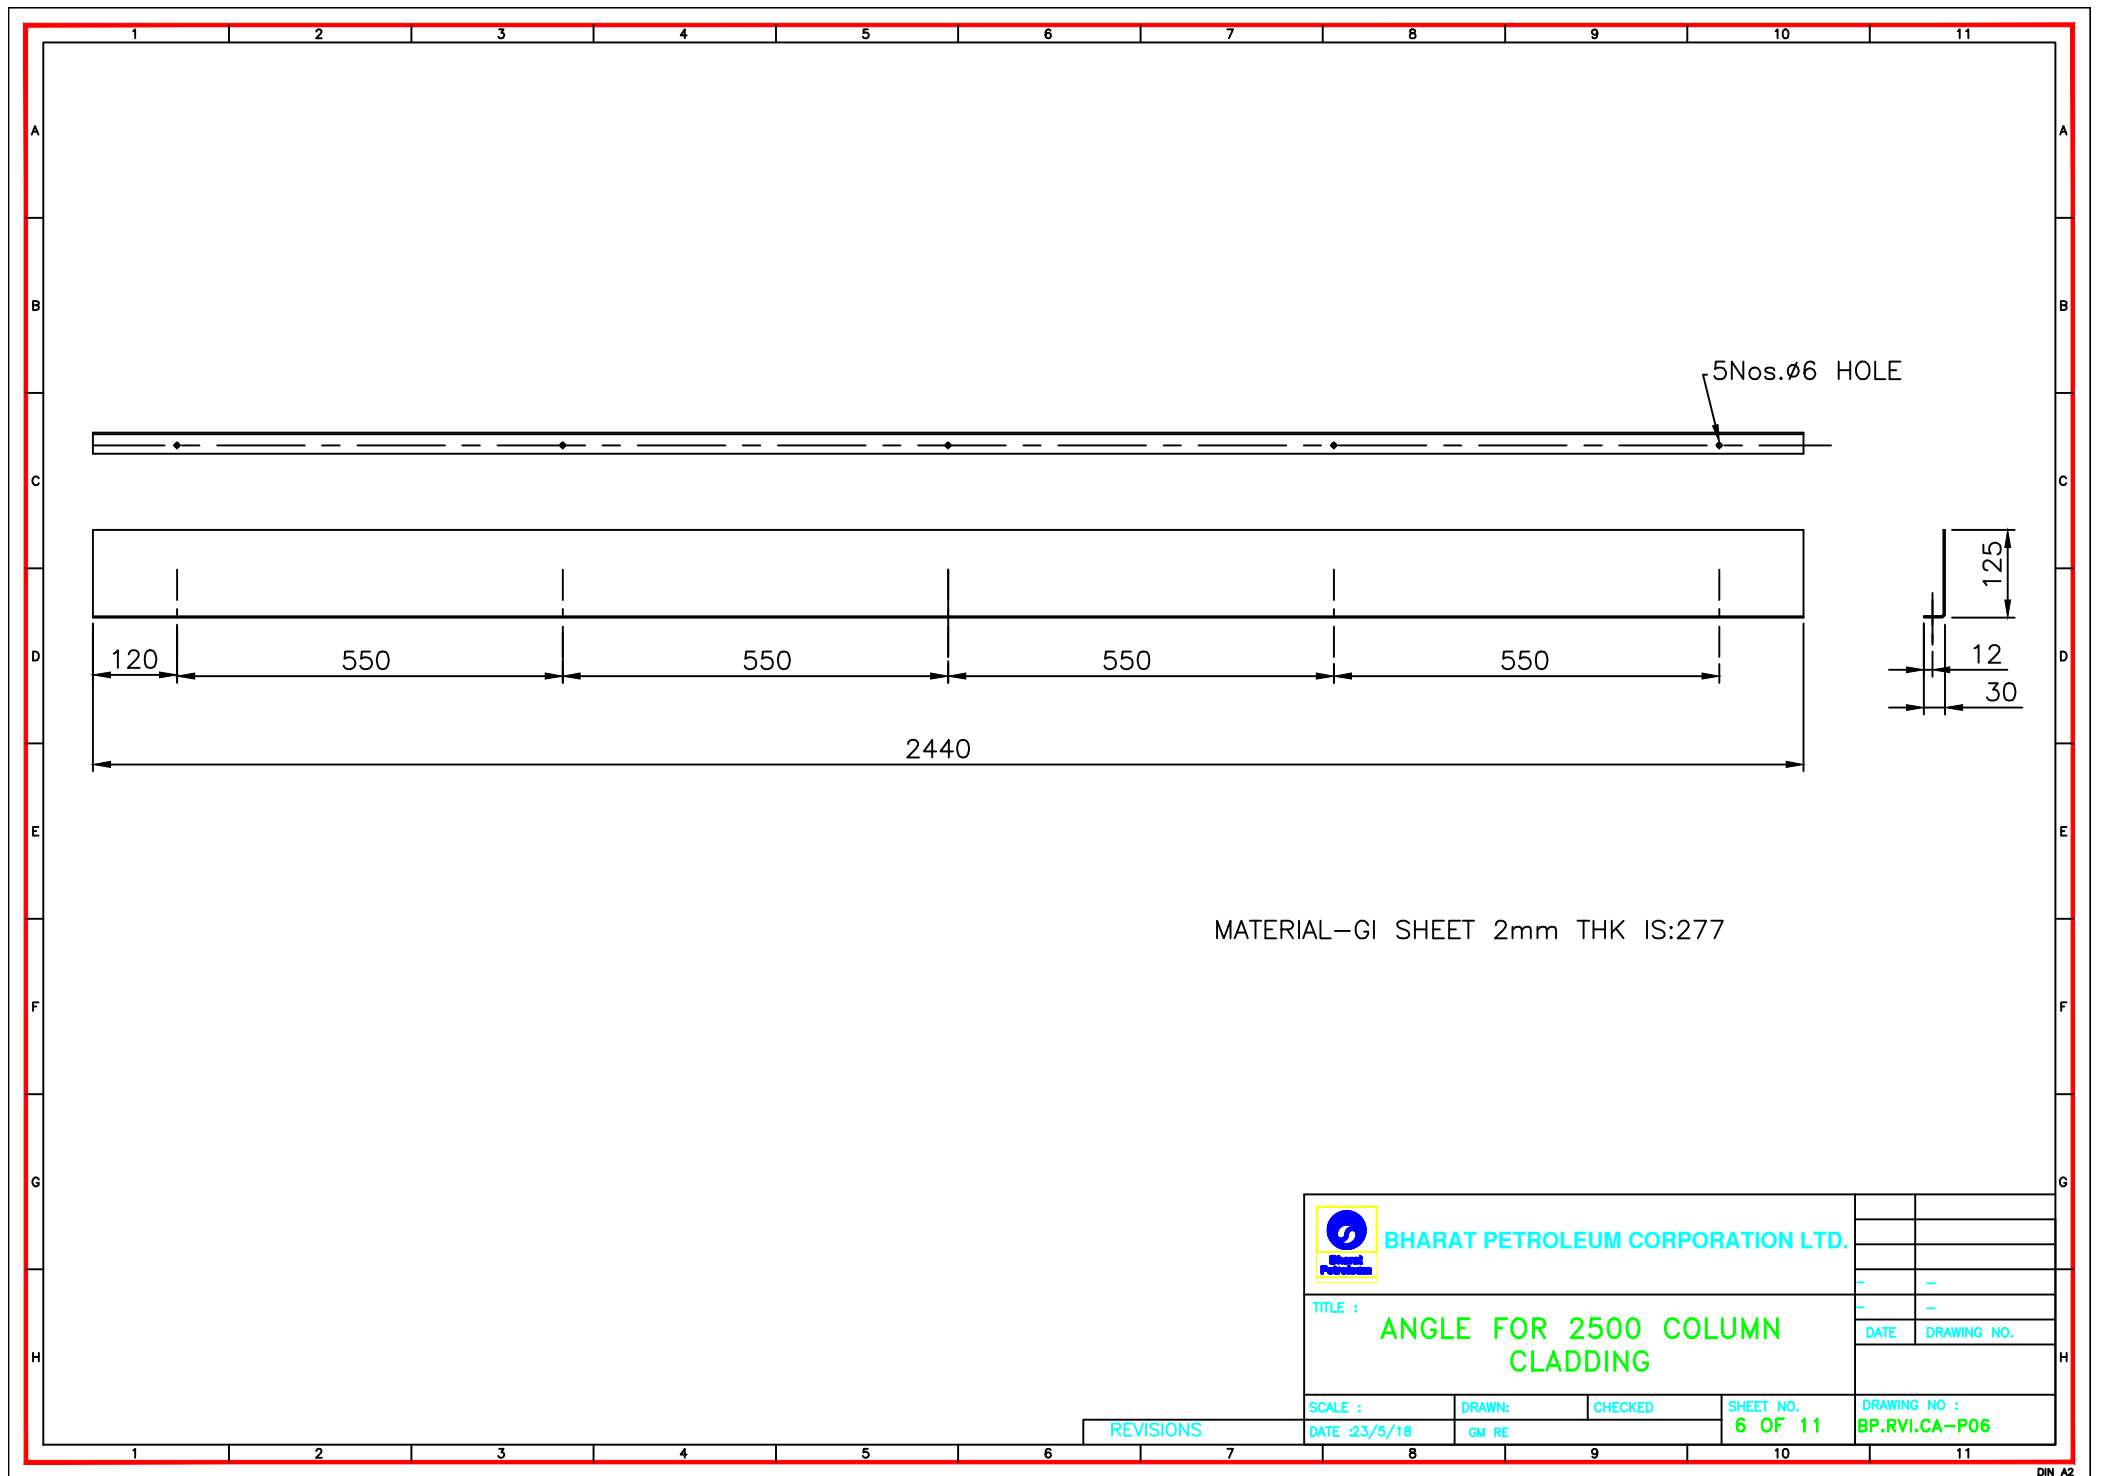


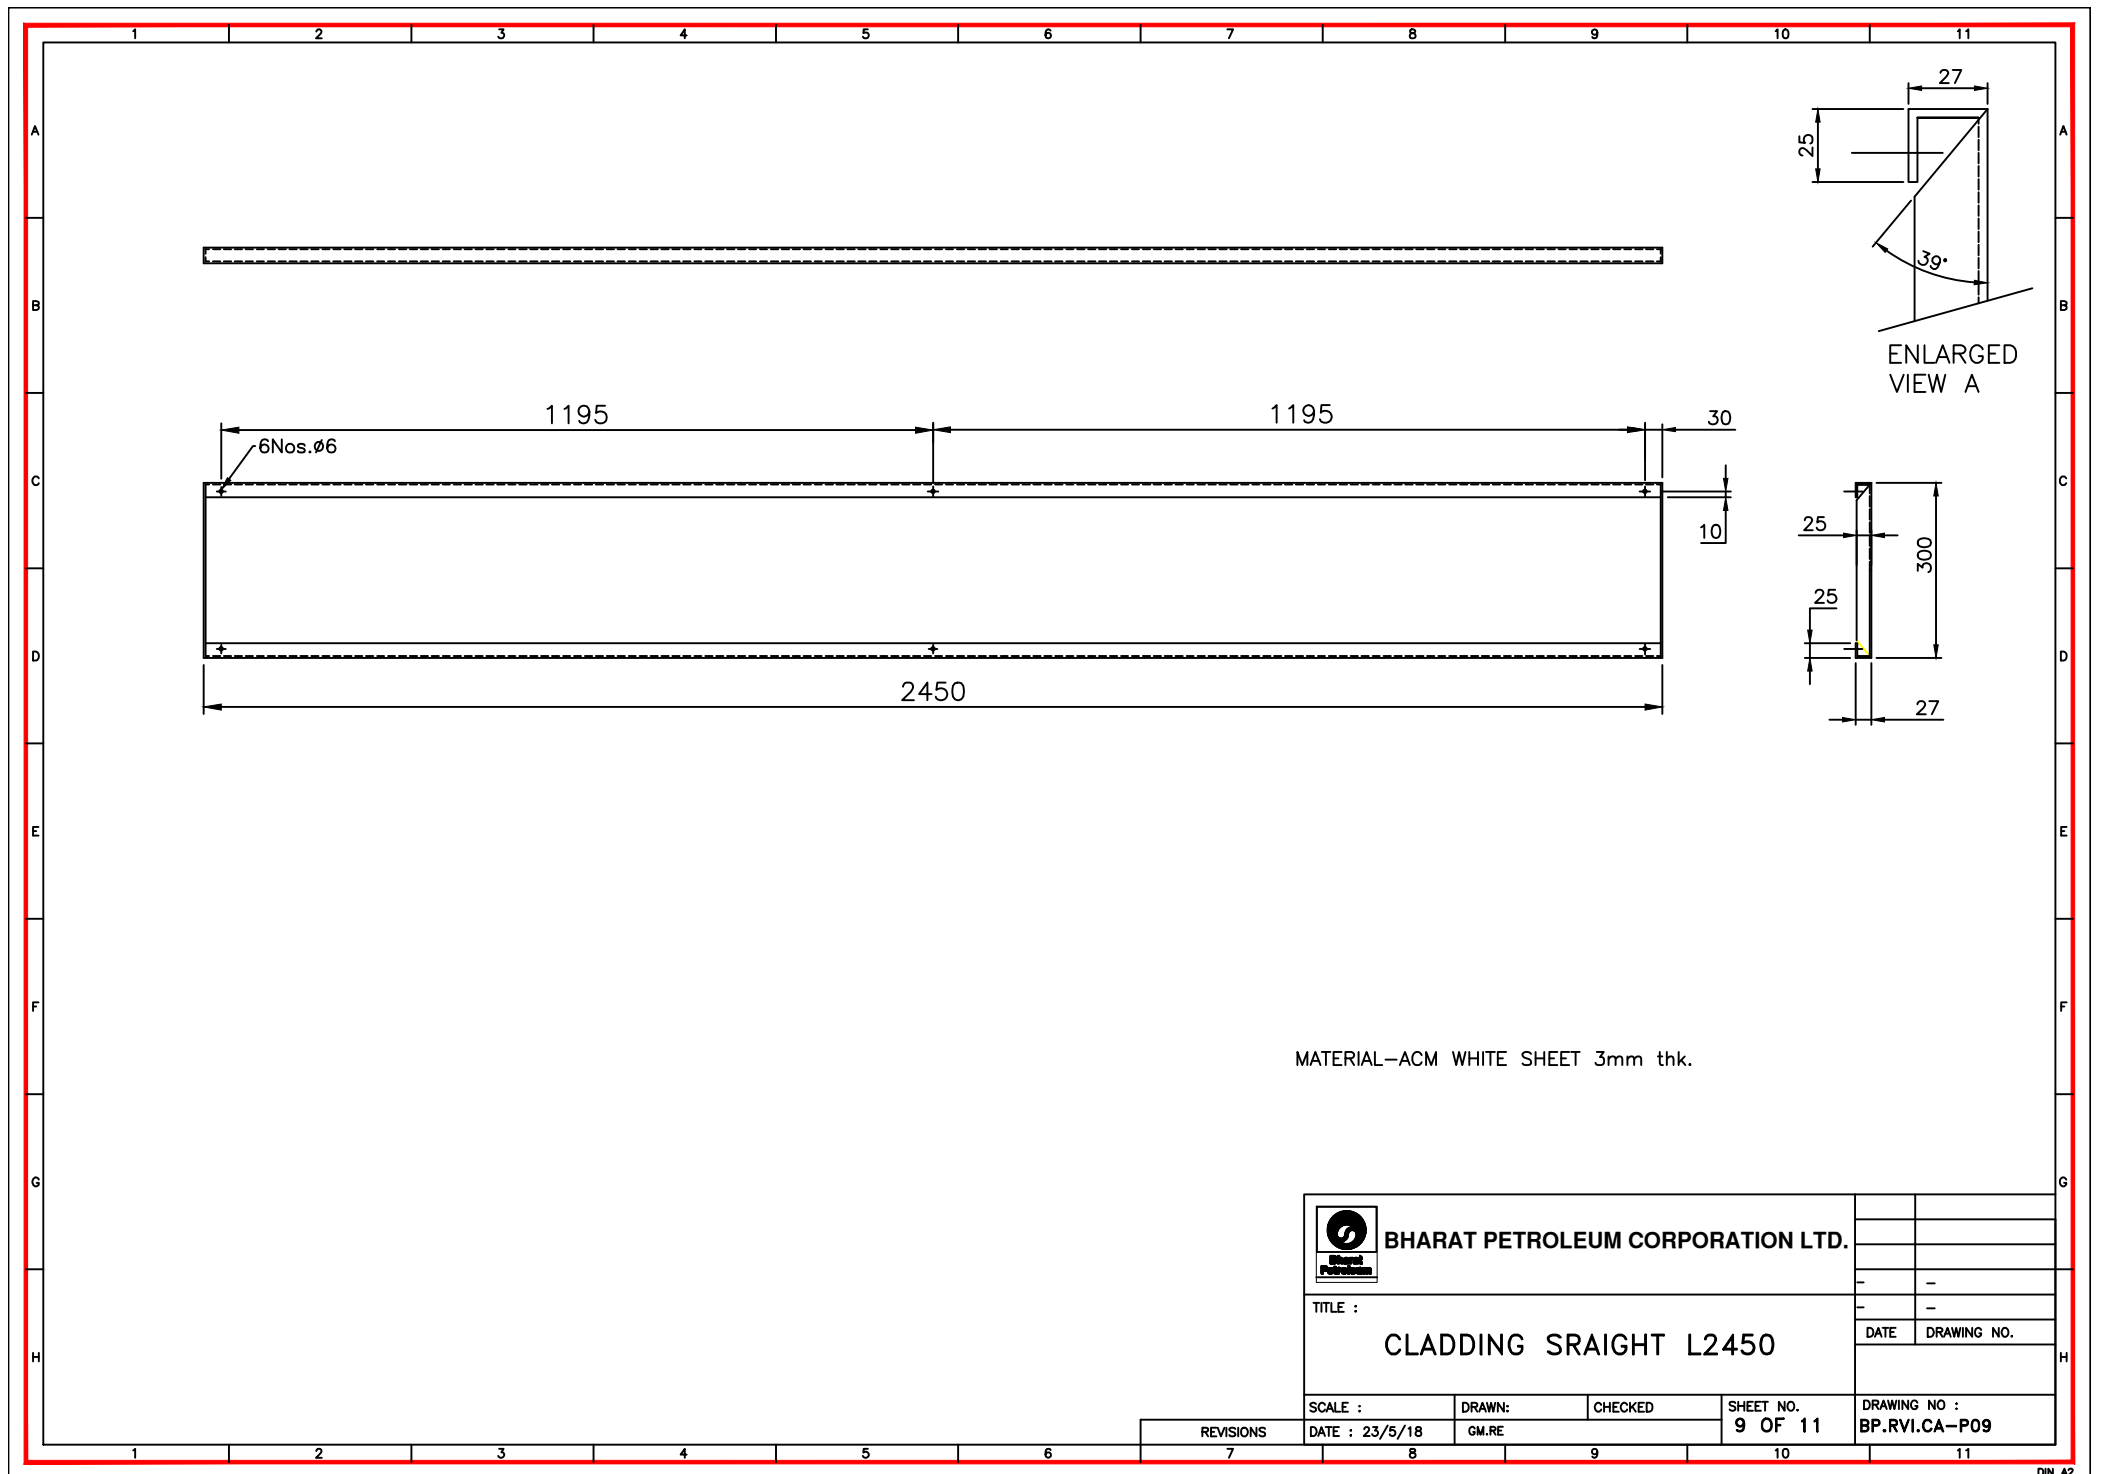


 BHARAT PETROLEUM CORPORATION LTD.					
TITLE :				-	-
CLADDING SRAIGHT L2450				-	-
SCALE :				DATE	DRAWING NO.
DATE : 23/5/18					
DRAWN:		CHECKED	SHEET NO.	DRAWING NO :	
GM.RE			9 OF 11	BP.RVI.CA-P09	
REVISIONS					

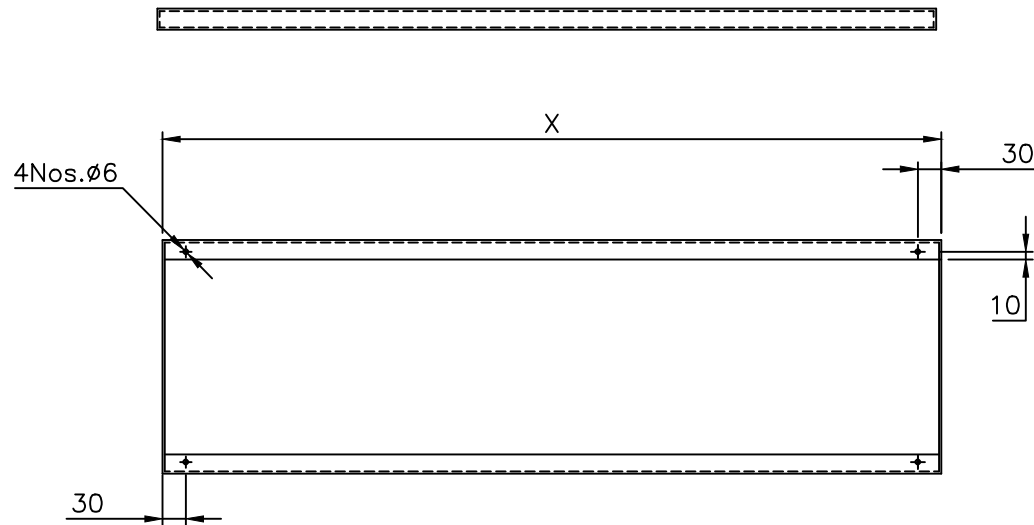

REMAINING COLUMN HEIGHT X

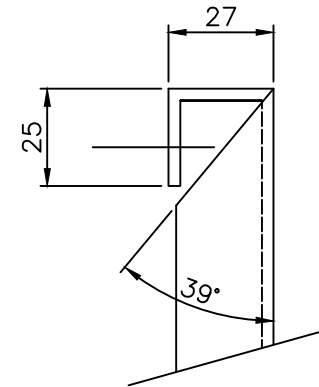


ENLARGED
VIEW A


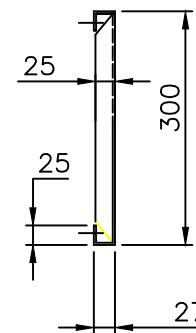


MATERIAL-ACM WHITE SHEET 3mm thk.

 BHARAT PETROLEUM CORPORATION LTD.					
TITLE :				-	-
CLADDING SRAIGHT REMAINING HT				DATE	DRAWING NO.
SCALE :				DRAWING NO :	
DATE : 23/5/18				BP.RVI.CA-P10	
DRAWN:				SHEET NO.	
GM.RE				10 of 11	
CHECKED					
REVISIONS					

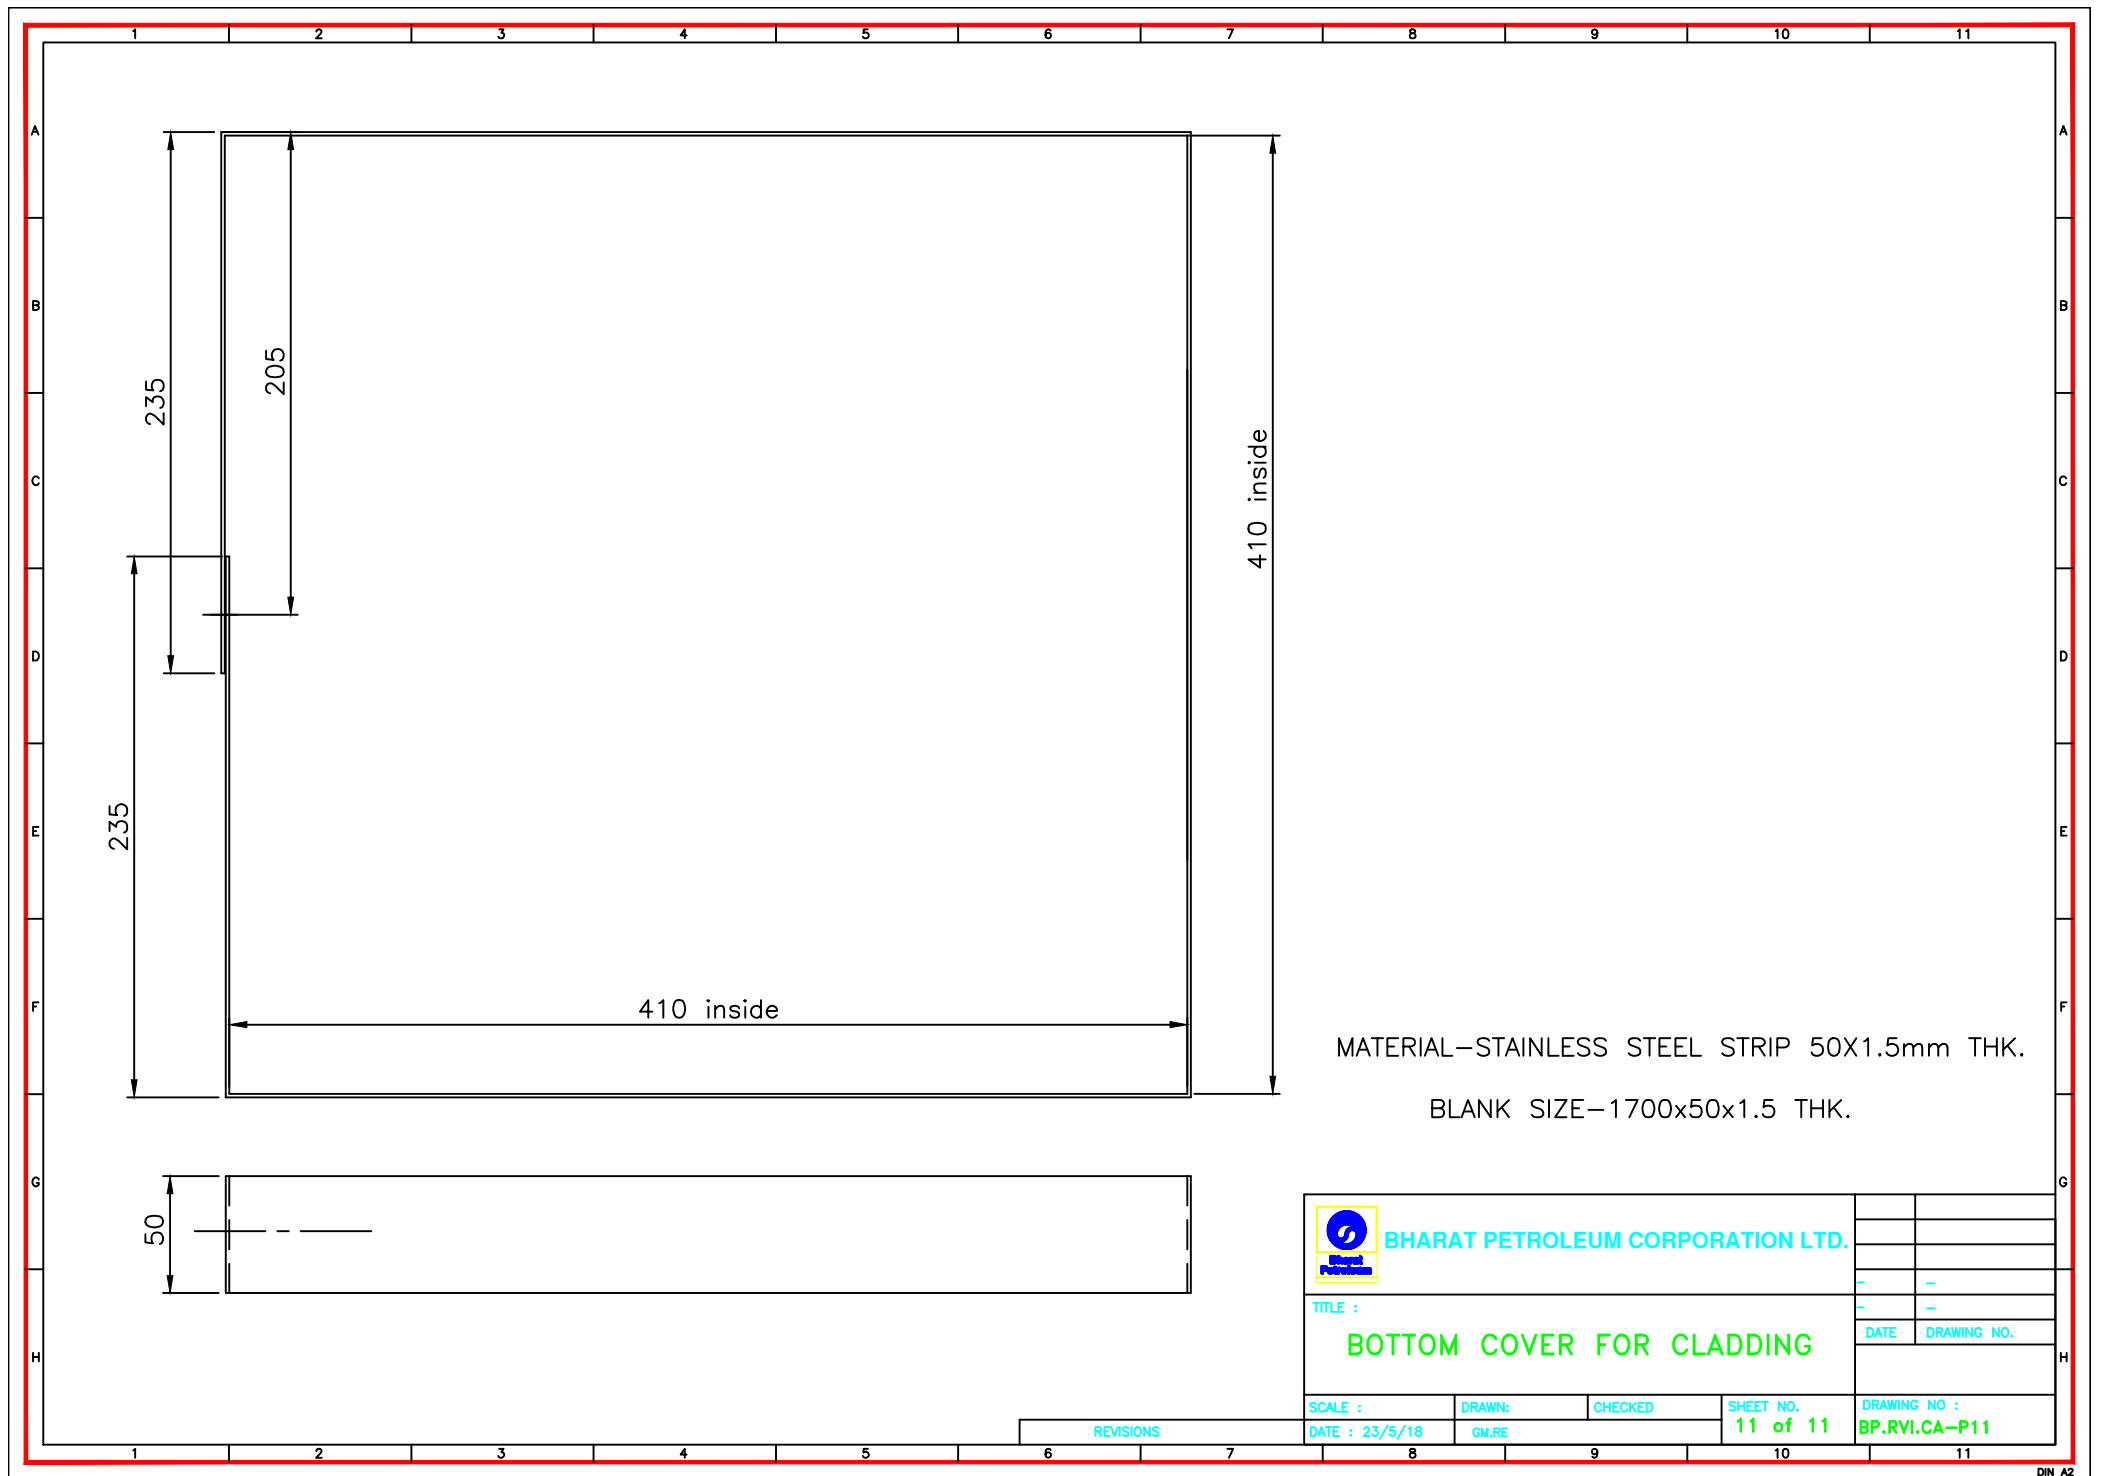

10	PILLER ARCH LIGHT	1
9	STRUCTURE FOR ARCH	4
8	SLIDDING CHANNEL FOR ARCH	4
7	ARCH FOR BPCL	4
6	BOTTOM COVER FOR CLADDING	2
5	CLADDING CURVED 2500mm	8
4	CLADDING SRAIGHT 250MM	2
3	CLADDING SRAIGHT 1000MM	2
2	CLADDING STRAIGHT 2500mm	4
1	ANGLE	16
SR.NO	DESCRIPTION	QTY.

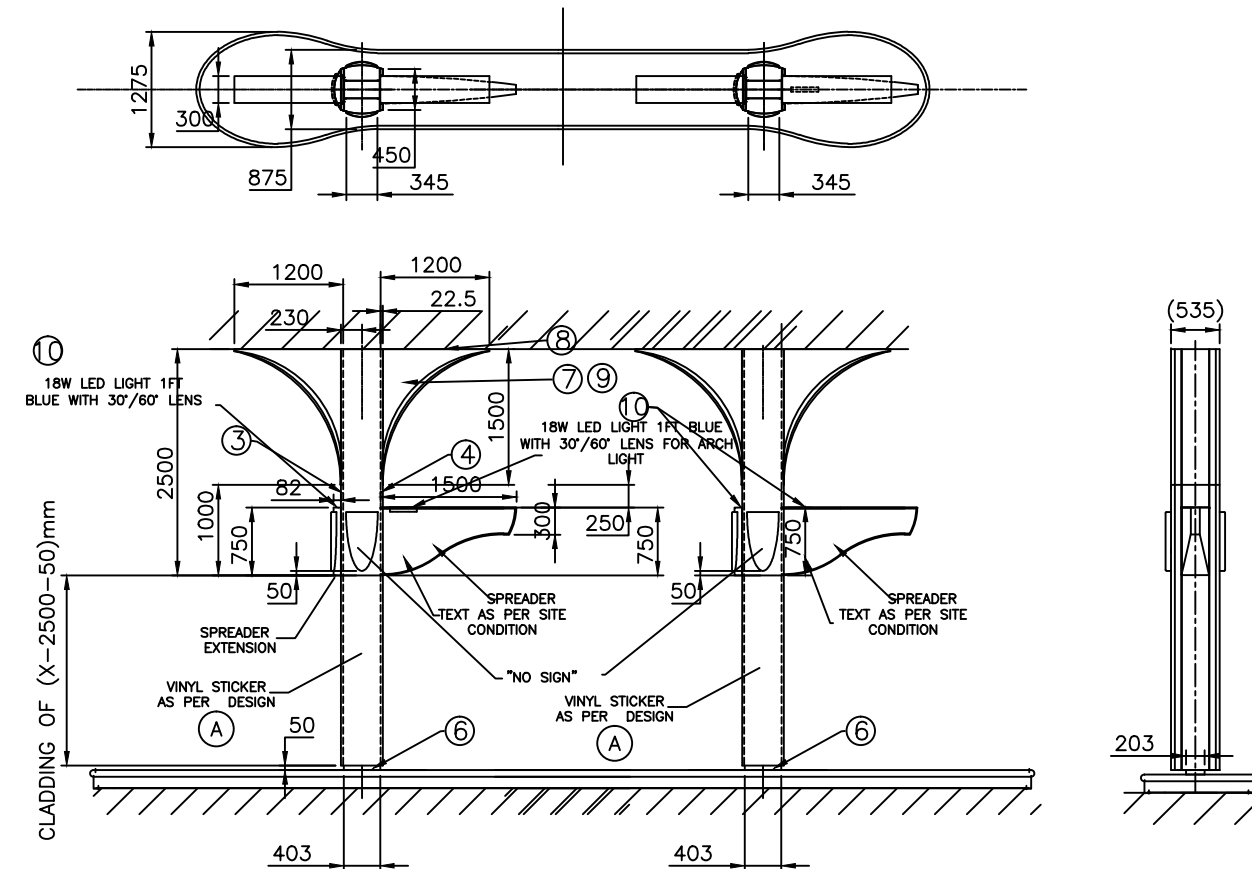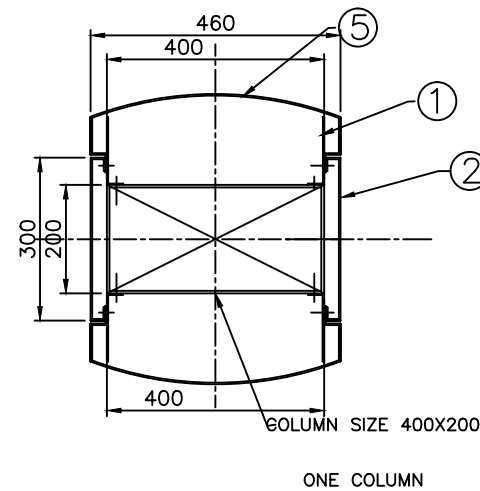

**Bharat
Petroleum**

TITLE :



DATE	DRAWING NO.
------	-------------

NUMBERS CROSSED OUT
SUPERSEDED DRAWINGS

DRAWING NO :
BP.RVI.CA-A02


A	ADDED 24/04/19	SCALE : 1:22	DRAWN:	CHECKED	SHEET NO. 2of11
	REVISIONS	DATE : 23/5/18	GM.RE		

10	PILLER ARCH LIGHT	1
9	STRUCTURE FOR ARCH	4
8	SLIDDING CHANNEL FOR ARCH	4
7	ARCH FOR BPCL	4
6	BOTTOM COVER FOR CLADDING	2
5	REMAIN CLADDING CURVED (2500mm)	4
4	CLADDING CURVED 2500mm(CUTOUT FOR NO SIGN)	4
3	CLADDING STRAIGHT (2750MM)	2
2	CLADDING STRAIGHT (3500mm)	2
1	ANGLE	16
SR.NO	DESCRIPTION	QTY.

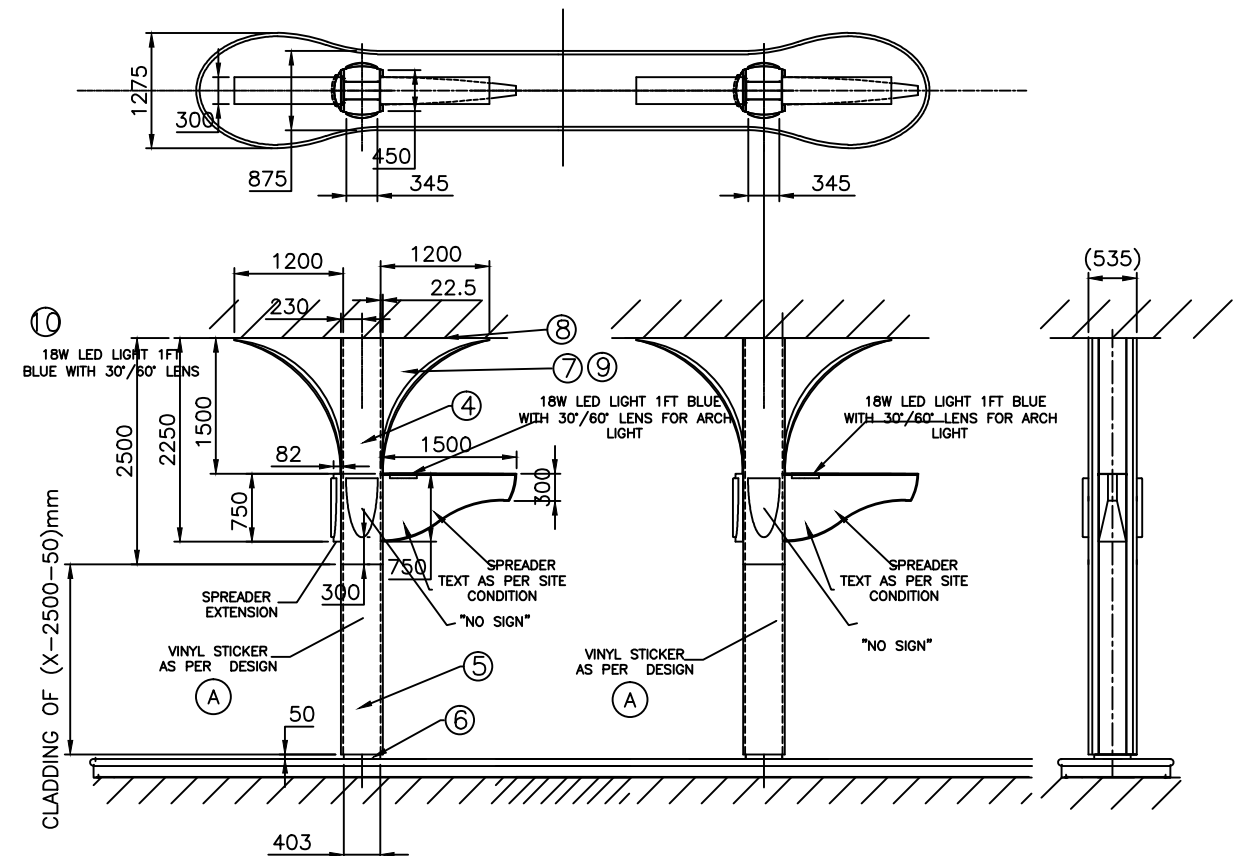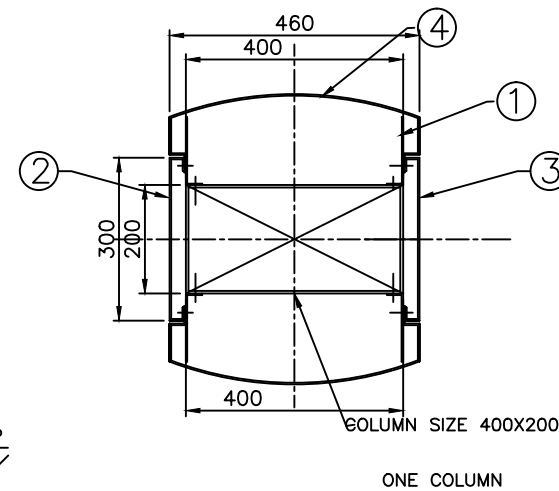

DRAWING NO :	BP.RVI.CA-A02a
--------------	----------------

A	ADDED 24/04/19	SCALE : 1:22	DRAWN:	CHECKED	SHEET NO. 2 of 11	DRAWING NO : BP.RVI.CA—A02a
REVISIONS		DATE : 23/5/18	GM.RE			

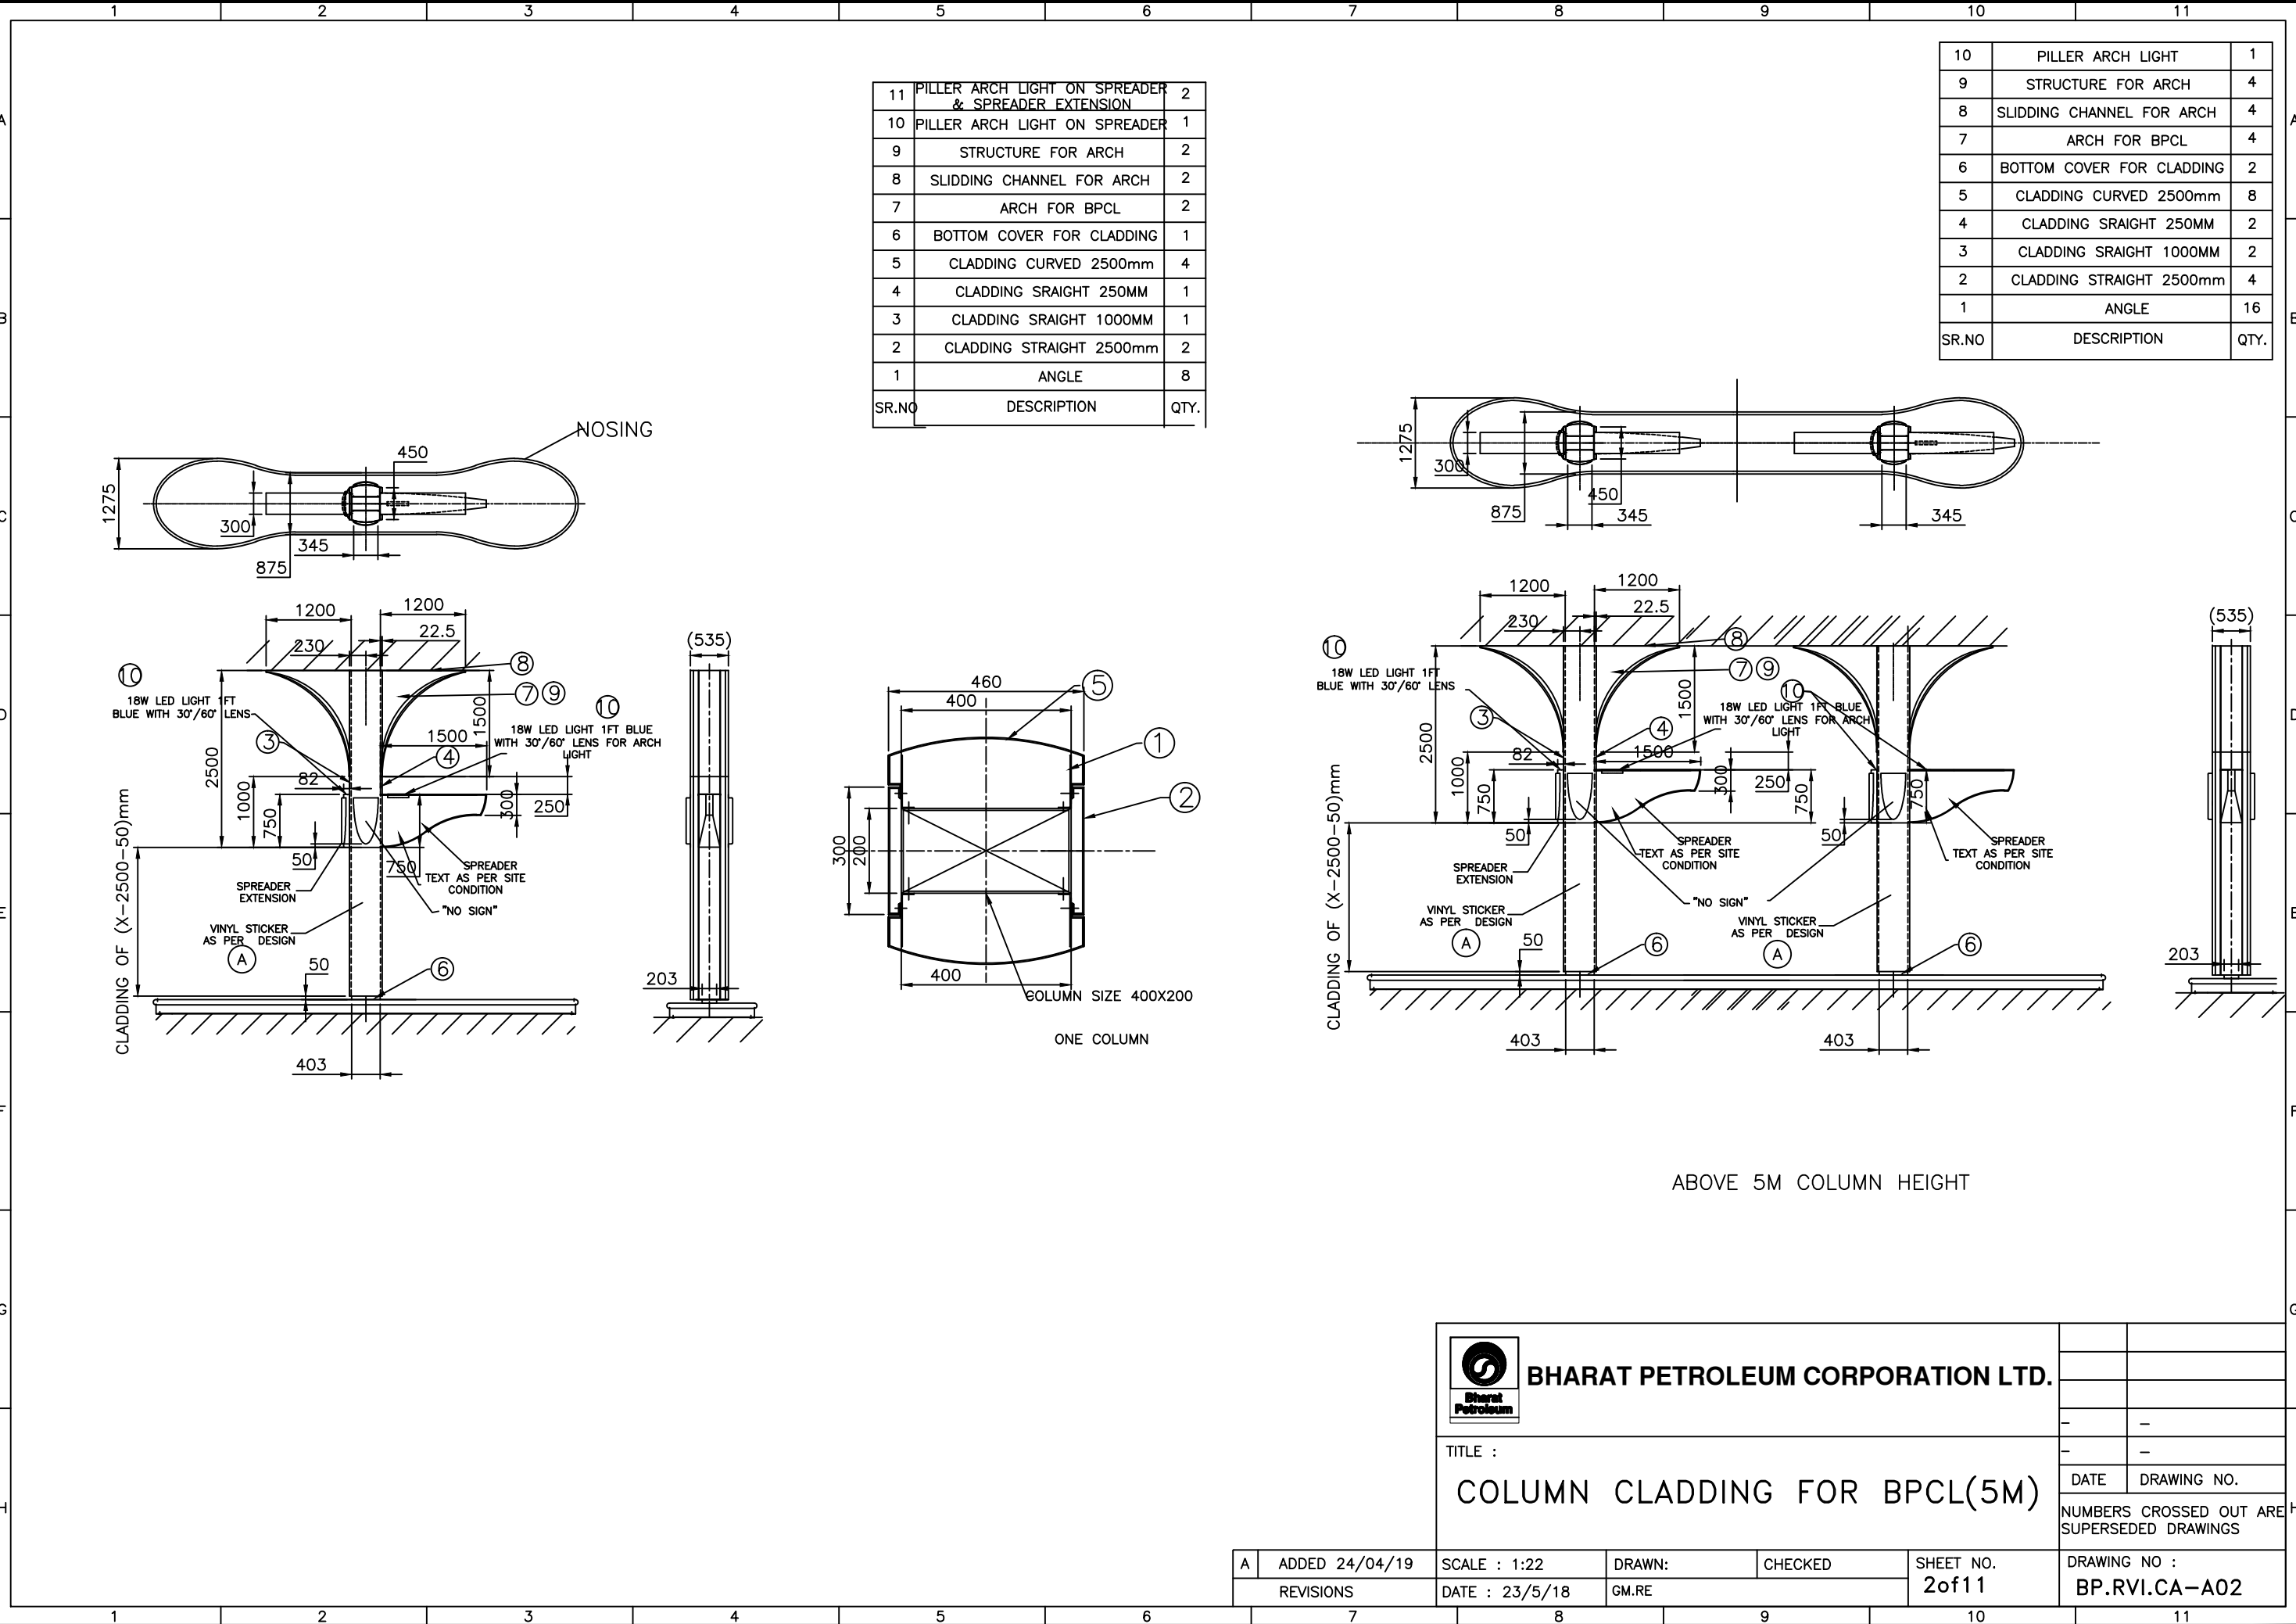



11	PILLER ARCH LIGHT ON SPREADER & SPREADER EXTENSION	2
10	PILLER ARCH LIGHT ON SPREADER	1
9	STRUCTURE FOR ARCH	2
8	SLIDGING CHANNEL FOR ARCH	2
7	ARCH FOR BPCL	2
6	BOTTOM COVER FOR CLADDING	1
5	CLADDING CURVED 2500mm	4
4	CLADDING SRAIGHT 250MM	1
3	CLADDING SRAIGHT 1000MM	1
2	CLADDING STRAIGHT 2500mm	2
1	ANGLE	8
SR.NO	DESCRIPTION	QTY.

10	PILLER ARCH LIGHT	1
9	STRUCTURE FOR ARCH	4
8	SLIDGING CHANNEL FOR ARCH	4
7	ARCH FOR BPCL	4
6	BOTTOM COVER FOR CLADDING	2
5	CLADDING CURVED 2500mm	8
4	CLADDING SRAIGHT 250MM	2
3	CLADDING SRAIGHT 1000MM	2
2	CLADDING STRAIGHT 2500mm	4
1	ANGLE	16
SR.NO	DESCRIPTION	QTY.

ABOVE 5M COLUMN HEIGHT

 BHARAT PETROLEUM CORPORATION LTD.			
TITLE : COLUMN CLADDING FOR BPCL(5M)		DATE	DRAWING NO.
		NUMBERS CROSSED OUT ARE SUPERSEDED DRAWINGS	
A		ADDED 24/04/19	SCALE : 1:22
		REVISIONS	DATE : 23/5/18
		DRAWN:	CHECKED
		GM.RE	SHEET NO. 2 of 11
		DRAWING NO : BP.RVI.CA-A02	

10	PILLER ARCH LIGHT	1
9	STRUCTURE FOR ARCH	4
8	SLIDDING CHANNEL FOR ARCH	4
7	ARCH FOR BPCL	4
6	BOTTOM COVER FOR CLADDING	2
5	REMAIN CLADDING CURVED (2500mm)	4
4	CLADDING CURVED 2500mm(CUTOUT FOR NO SIGN)	4
3	CLADDING STRAIGHT (2750MM)	2
2	CLADDING STRAIGHT (3500mm)	2
1	ANGLE	16
SR.NO	DESCRIPTION	QTY.

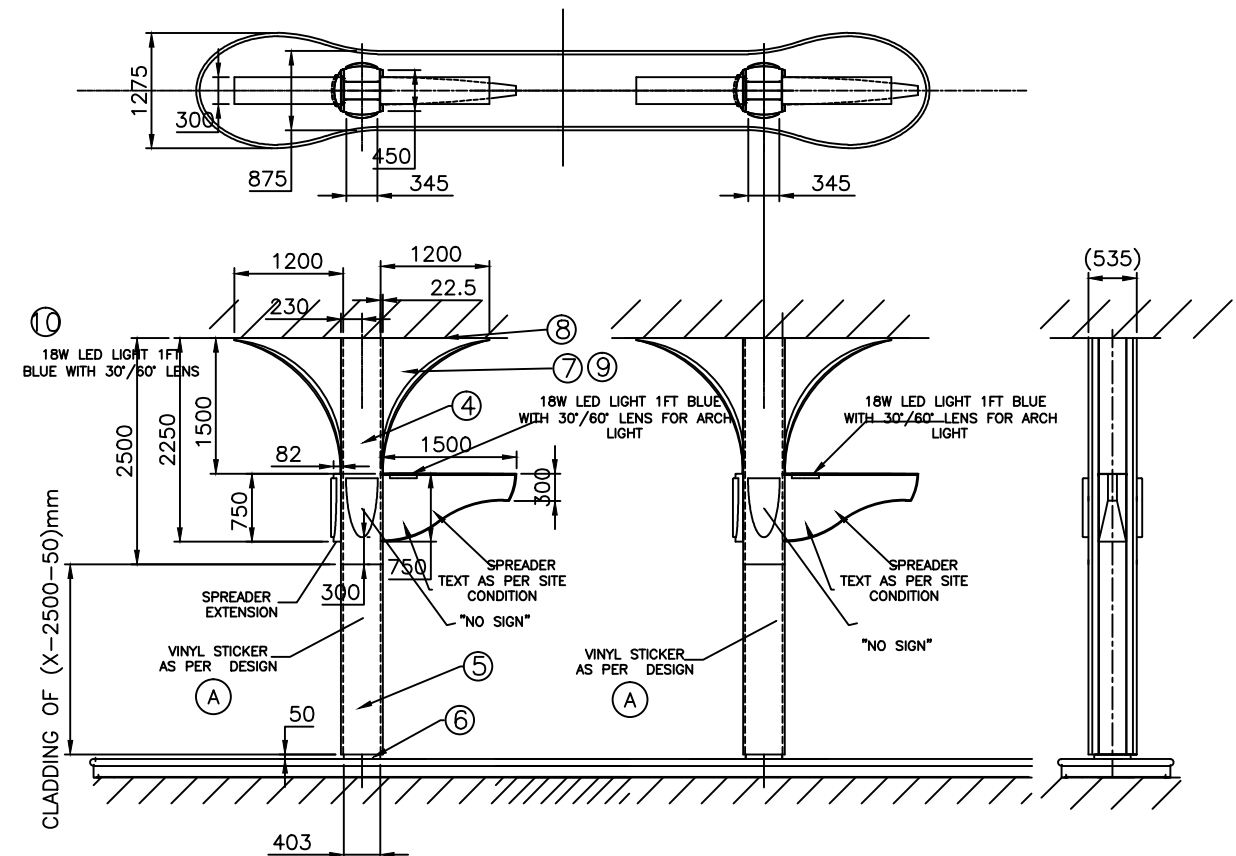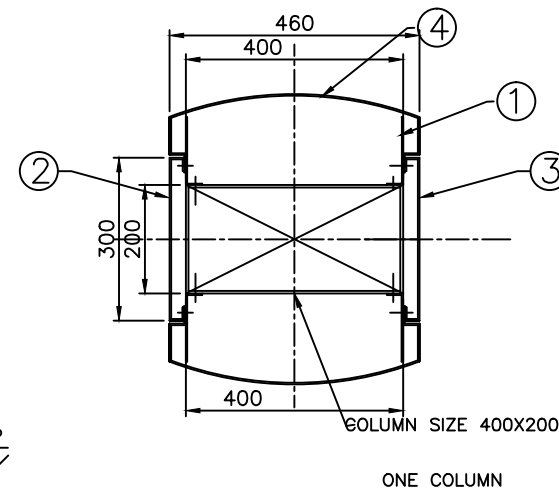

A	ADDED 24/04/19	SCALE : 1:22	DRAWN:	CHECKED	SHEET NO. 2 of 11	DRAWING NO : BP.RVI.CA-A02a
REVISIONS		DATE : 23/5/18	GM.RE			