

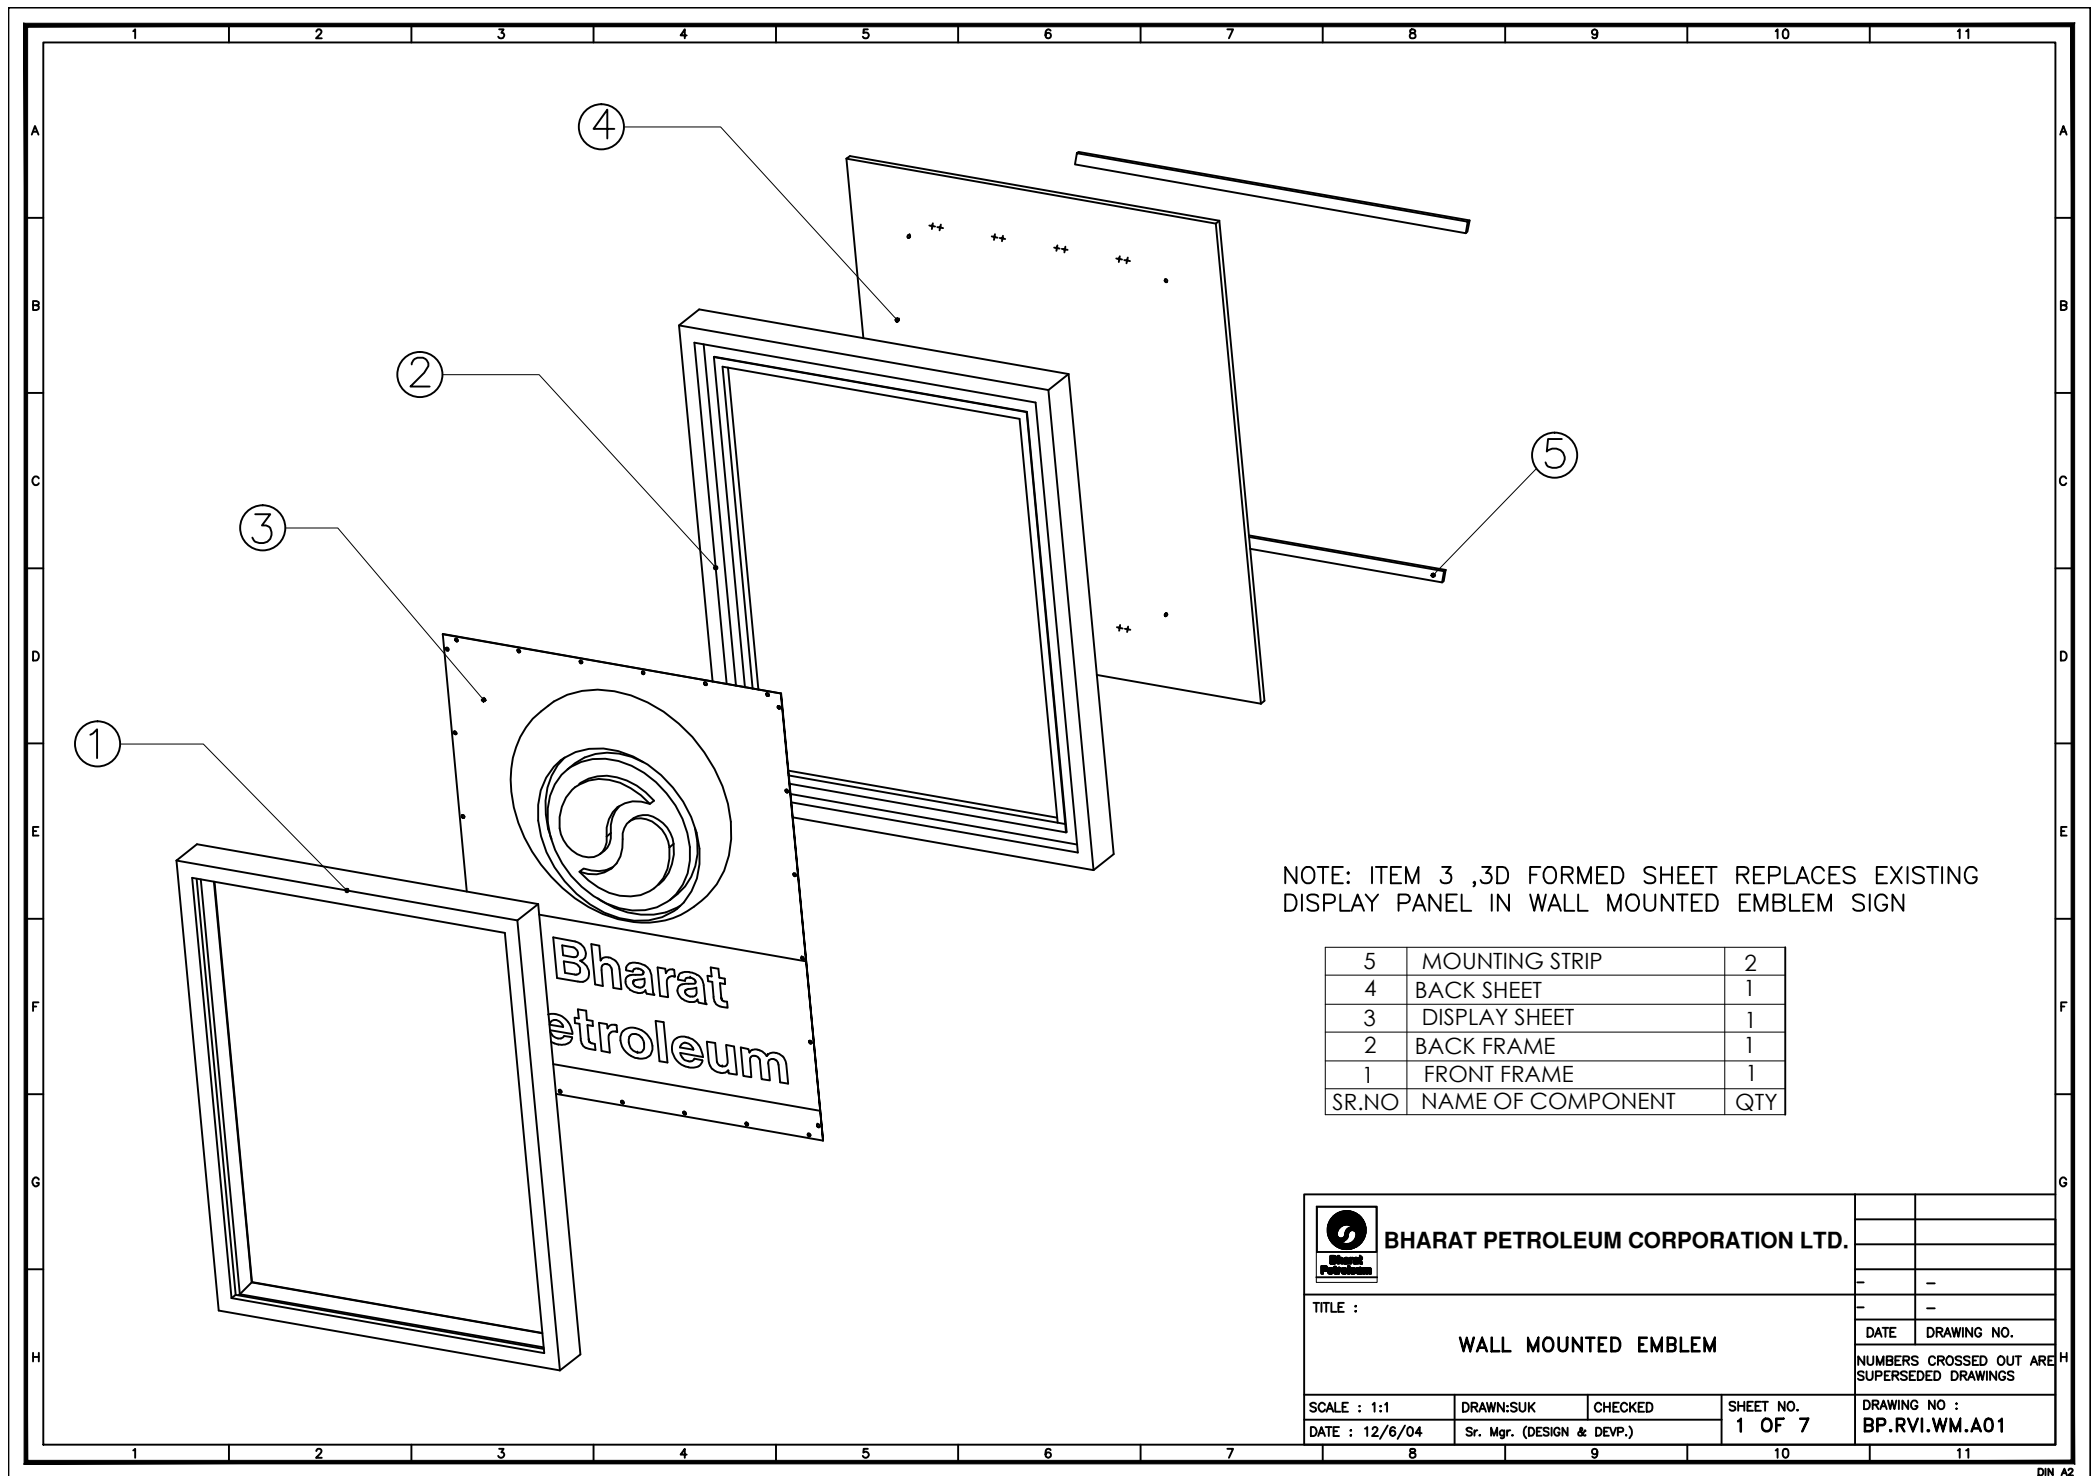
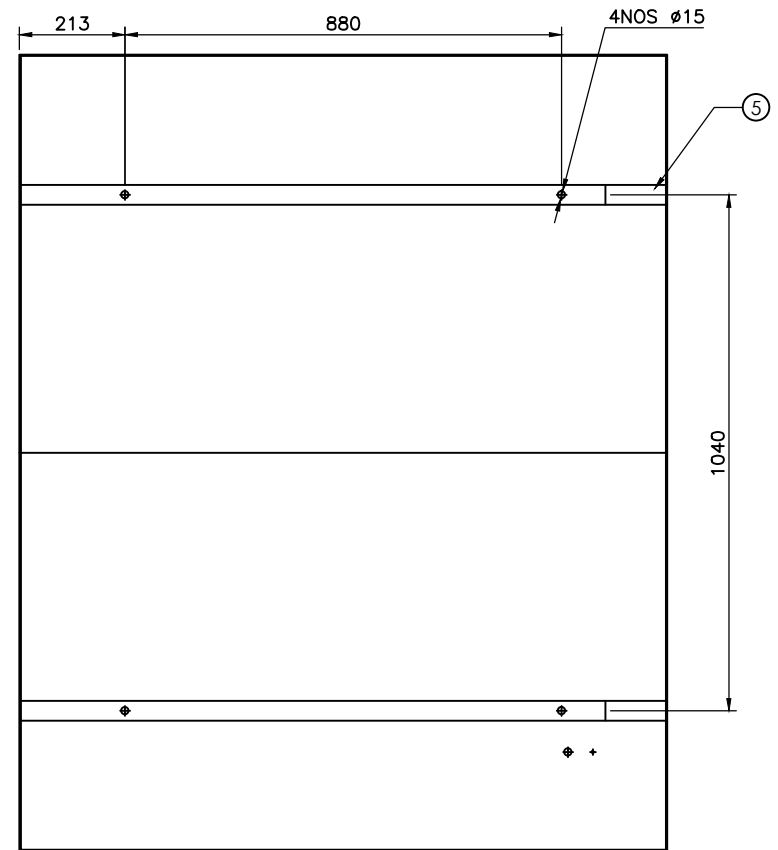


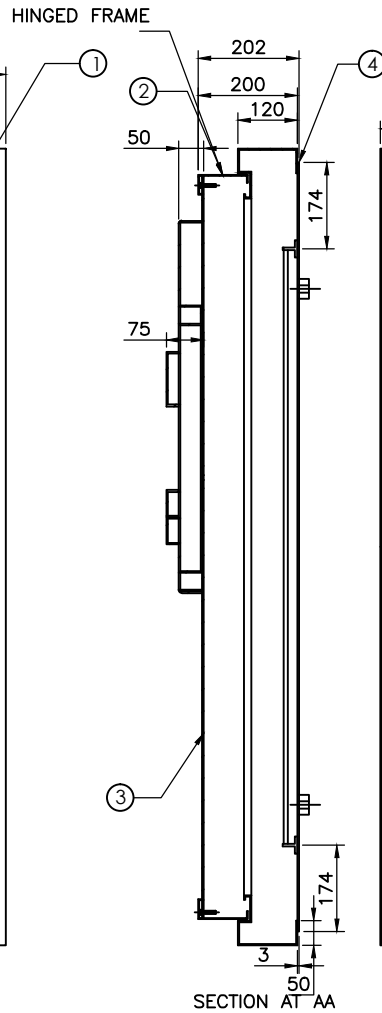

NOTE: ITEM 3 ,3D FORMED SHEET REPLACES EXISTING
DISPLAY PANEL IN WALL MOUNTED EMBLEM SIGN


5	MOUNTING STRIP	2
4	BACK SHEET	1
3	DISPLAY SHEET	1
2	BACK FRAME	1
1	FRONT FRAME	1
SR.NO	NAME OF COMPONENT	QTY



				BHARAT PETROLEUM CORPORATION LTD.			
TITLE :							
WALL MOUNTED EMBLEM							
SCALE : 1:1						DATE	DRAWING NO.
DATE : 12/6/04						NUMBERS CROSSED OUT ARE SUPERSEDED DRAWINGS	
DRAWN:SUK		CHECKED		SHEET NO.		DRAWING NO :	
Sr. Mgr. (DESIGN & DEVP.)				1 OF 7		BP.RVI.WM.A01	

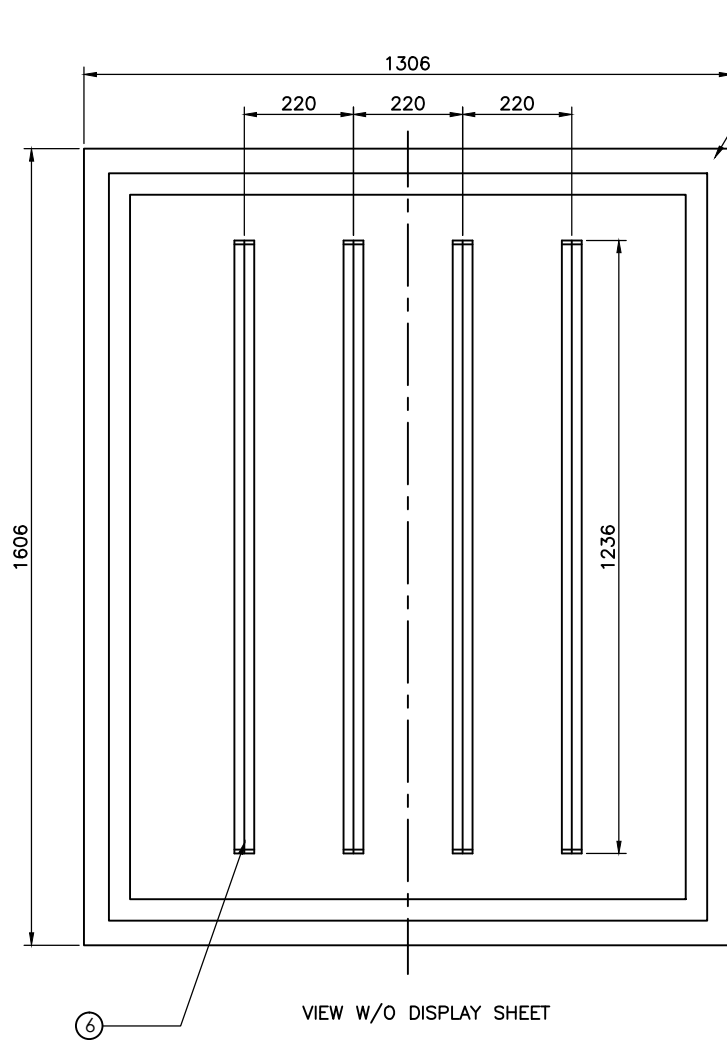

6	TUBE LIGHT ASSY.	4
5	MOUNTING STRIP	2
4	BACK SHEET	1
3	DISPLAY SHEET	1
2	BACK FRAME	1
1	FRONT FRAME	1
SR.NO	NAME OF COMPONENT	QTY

 BHARAT PETROLEUM CORPORATION LTD.					
TITLE :					
WALL MOUNTED EMBLEM ASSY				DATE	
				DRAWING NO.	
SCALE : 1:10 DATE : 12/6/04				DRAWING NO : BP.RVI.WM.A02	
DRAWN:SUK Sr. Mgr. (DESIGN & DEVP.)		CHECKED Sr. Mgr. (DESIGN & DEVP.)		SHEET NO. 2 OF 7	
NUMBERS CROSSED OUT ARE SUPERSEDED DRAWINGS					

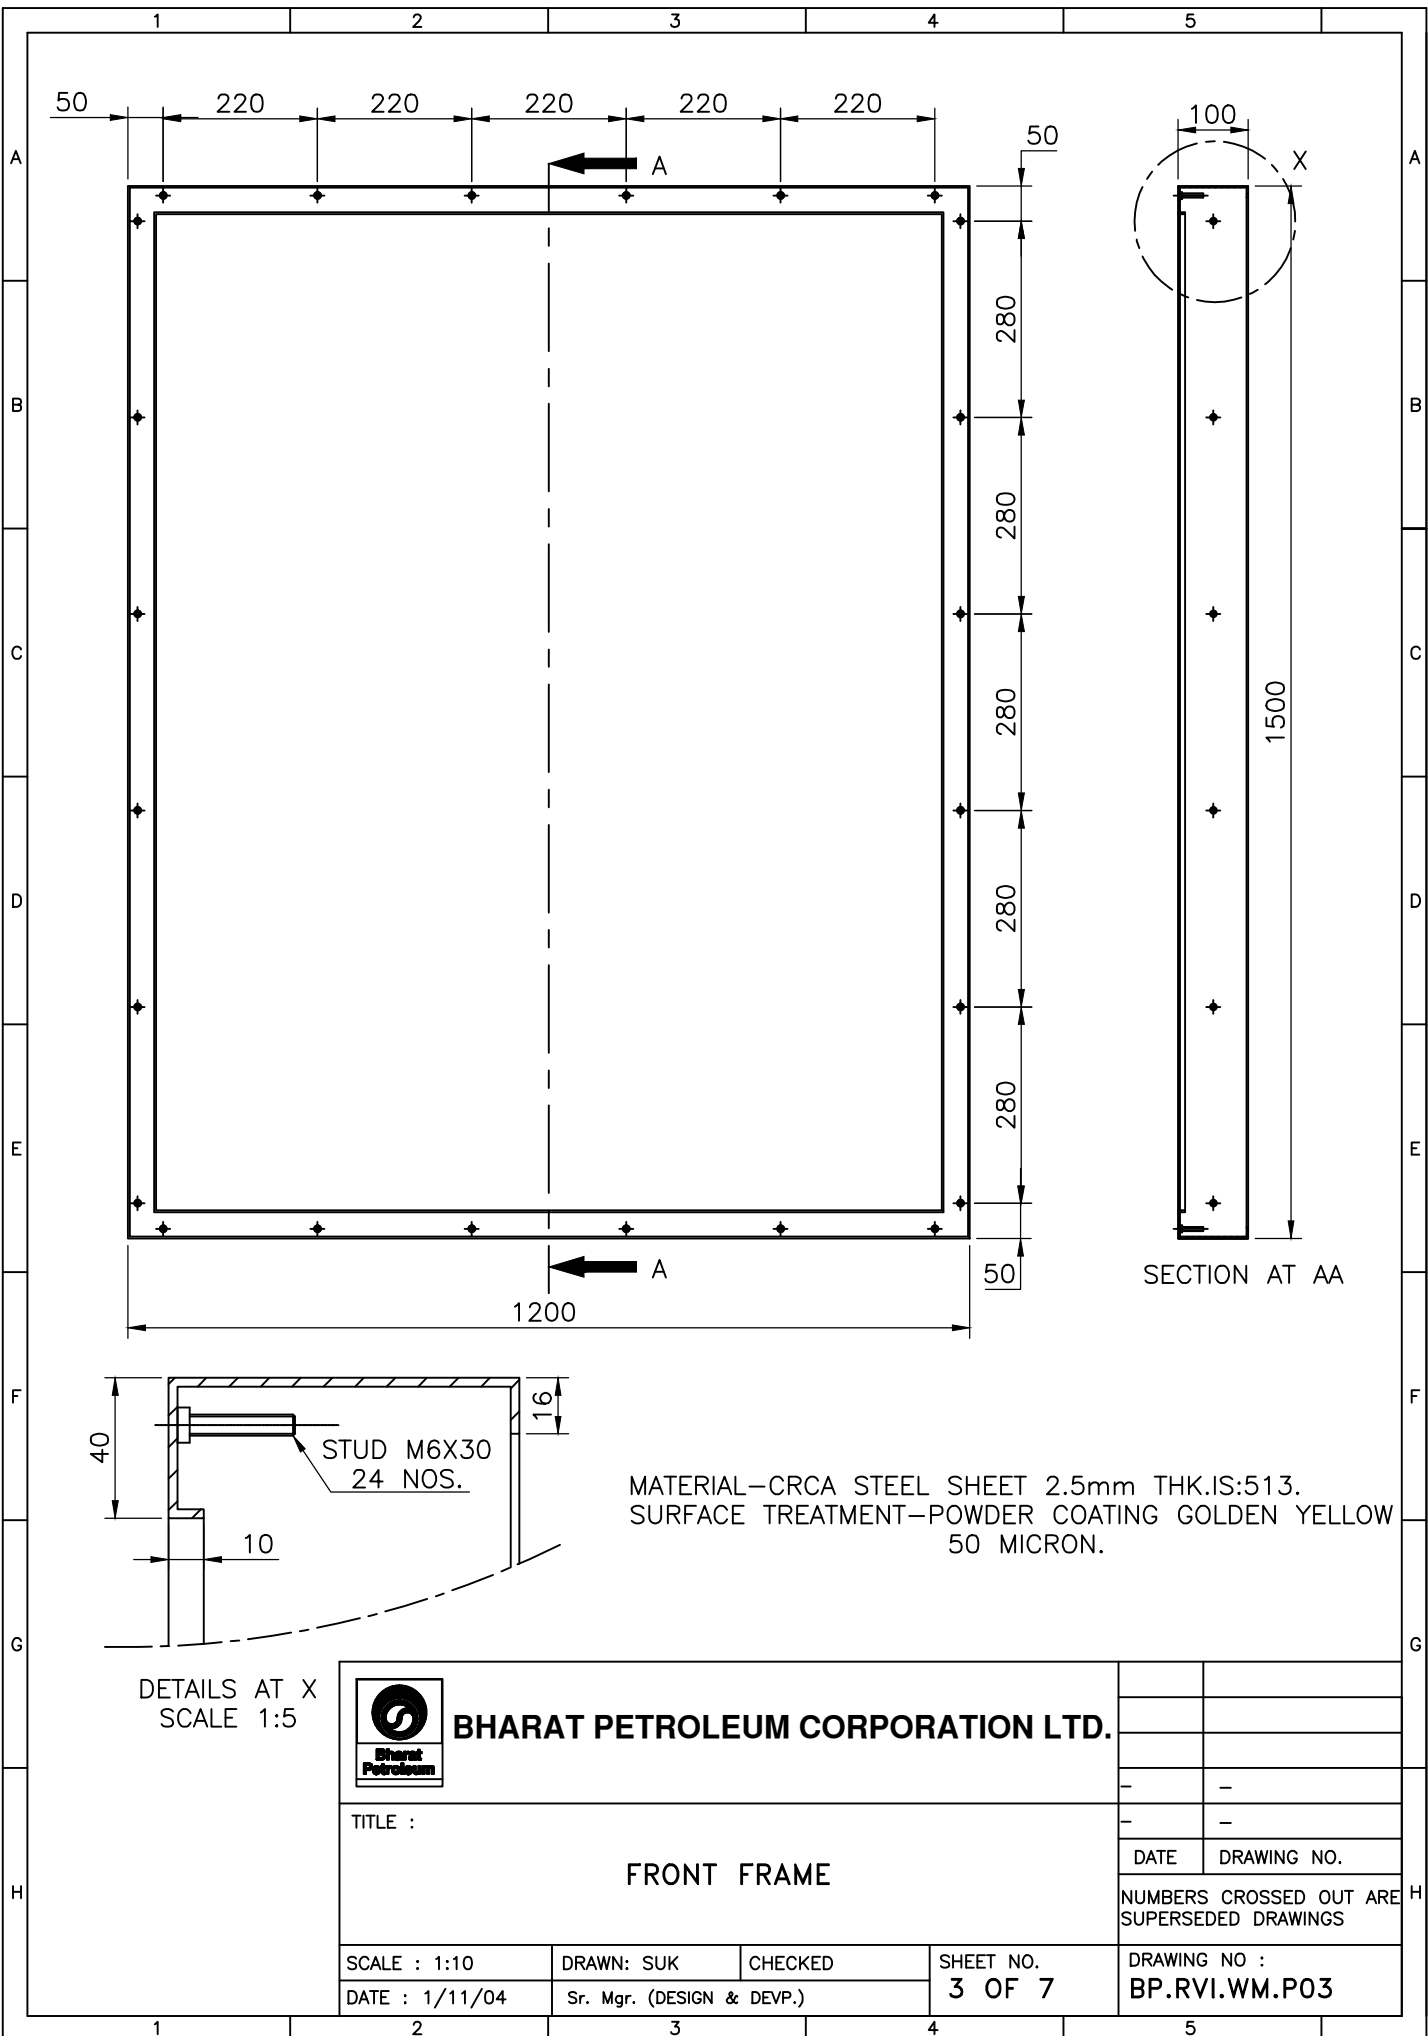

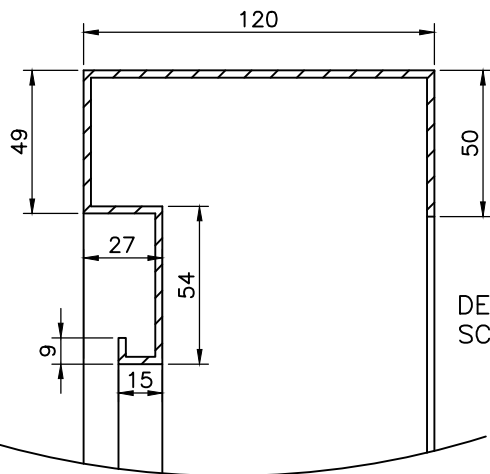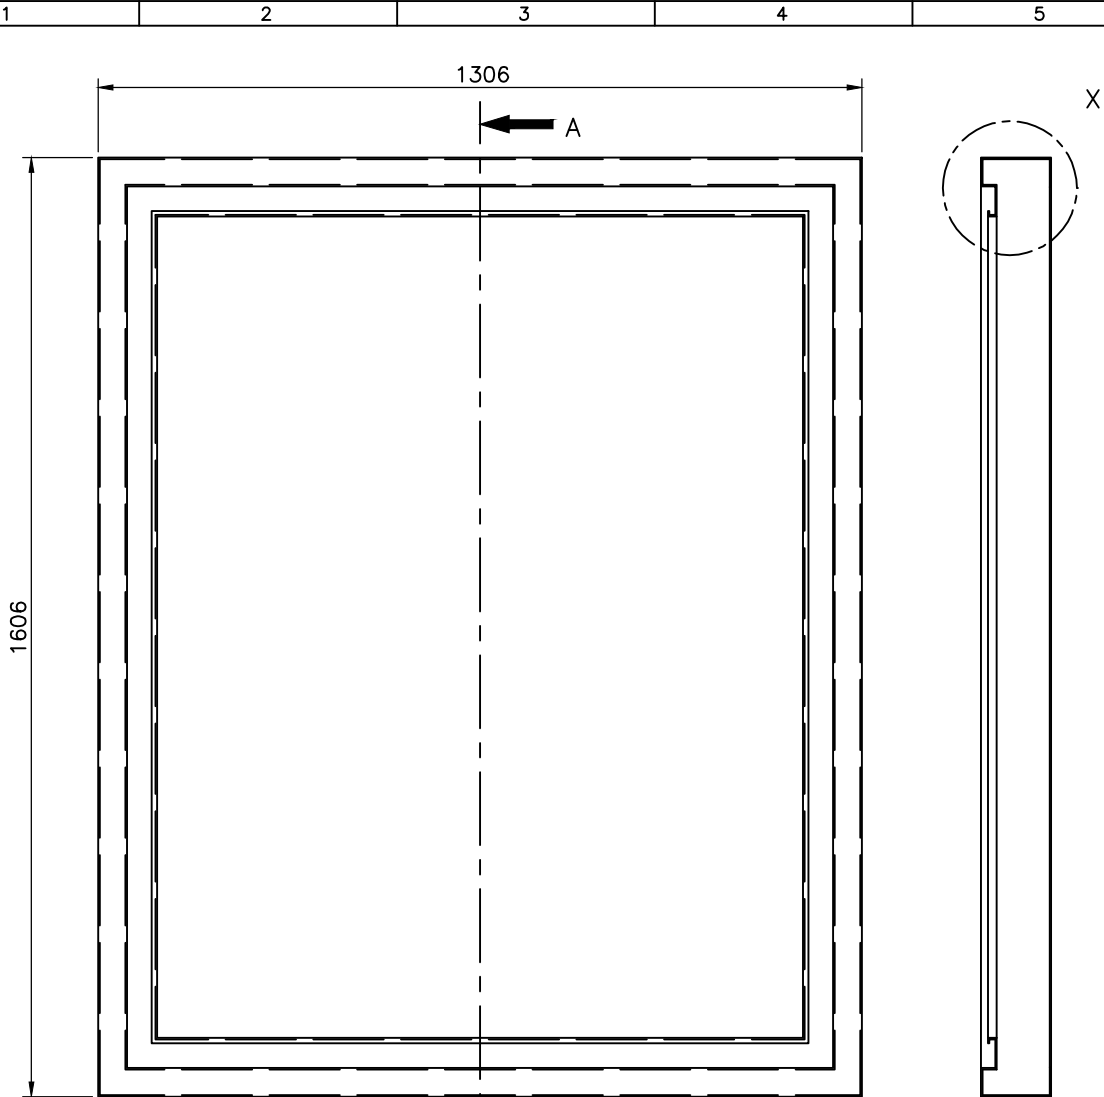

SECTION AT AA

DETAIL AT X
SCALE 1:5

MATERIAL—CRCA STEEL SHEET 2.5mm THK.IS:513.
SURFACE TREATMENT—POWDER COATING WHITE SEMI GLOSSY
50 MICRON.



BHARAT PETROLEUM CORPORATION LTD.

TITLE :

BACK FRAME

DATE DRAWING NO.

NUMBERS CROSSED OUT ARE
SUPERSEDED DRAWINGS

SCALE : 1:12

DRAWN: SUK

CHECKED

SHEET NO.


DRAWING NO :

DATE : 1/11/04

Sr. Mgr. (DESIGN & DEVP.)

4 OF 7

BP.RVI.WM.P04

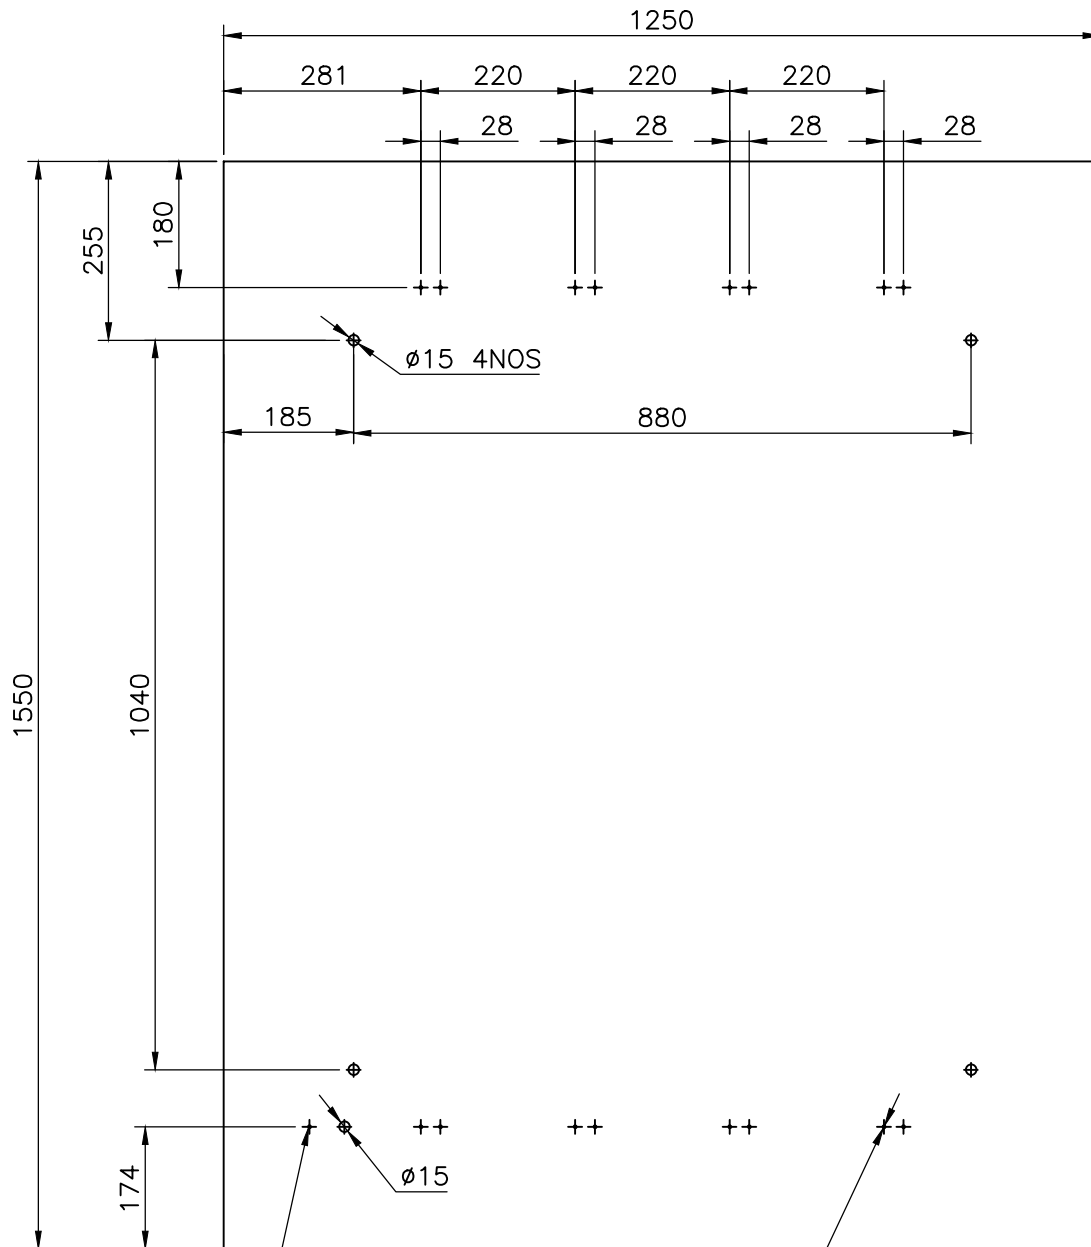

M4 BUSH $\phi 10 \times 10$ MM
HEIGHT TAG WELDED

M4 TAPPING 16 NOS

MATERIAL—CRCA STEEL SHEET 2mm THK.IS:513.
SURFACE TREATMENT—POWDER COATING WHITE SEMI GLOSSY 50
MICRON.



BHARAT PETROLEUM CORPORATION LTD.

TITLE :

BACK SHEET

SCALE : 1:10

DRAWN: SUK

CHECKED

SHEET NO.


DRAWING NO :

DATE : 1/11/04

Sr. Mgr. (DESIGN & DEVP.)


6 OF 7

BP.RVI.WM.PO6

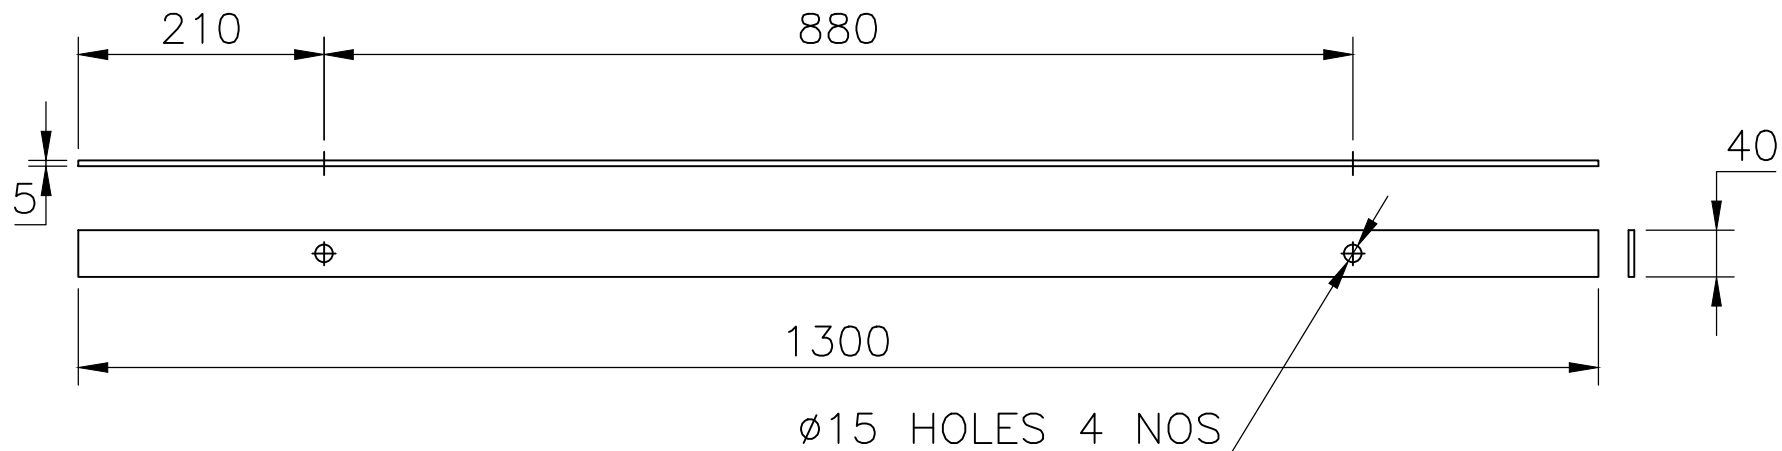



MATERIAL—MS FLAT 40X5mm THK.
SURFACE TREATMENT—POWDER COATING
WHITE SEMI GLOSSY 50MICRON.

 BHARAT PETROLEUM CORPORATION LTD.			
TITLE :			
MOUNTING STRIP		DATE	DRAWING NO.
		NUMBERS CROSSED OUT ARE SUPERSEDED DRAWINGS	
SCALE : 1:10	DRAWN:SUK	CHECKED	SHEET NO.
DATE : 01/07/1999	Sr. Mgr. (DESIGN & DEVP.)		7 OF 7
			DRAWING NO : BP.RVI.WM.P07

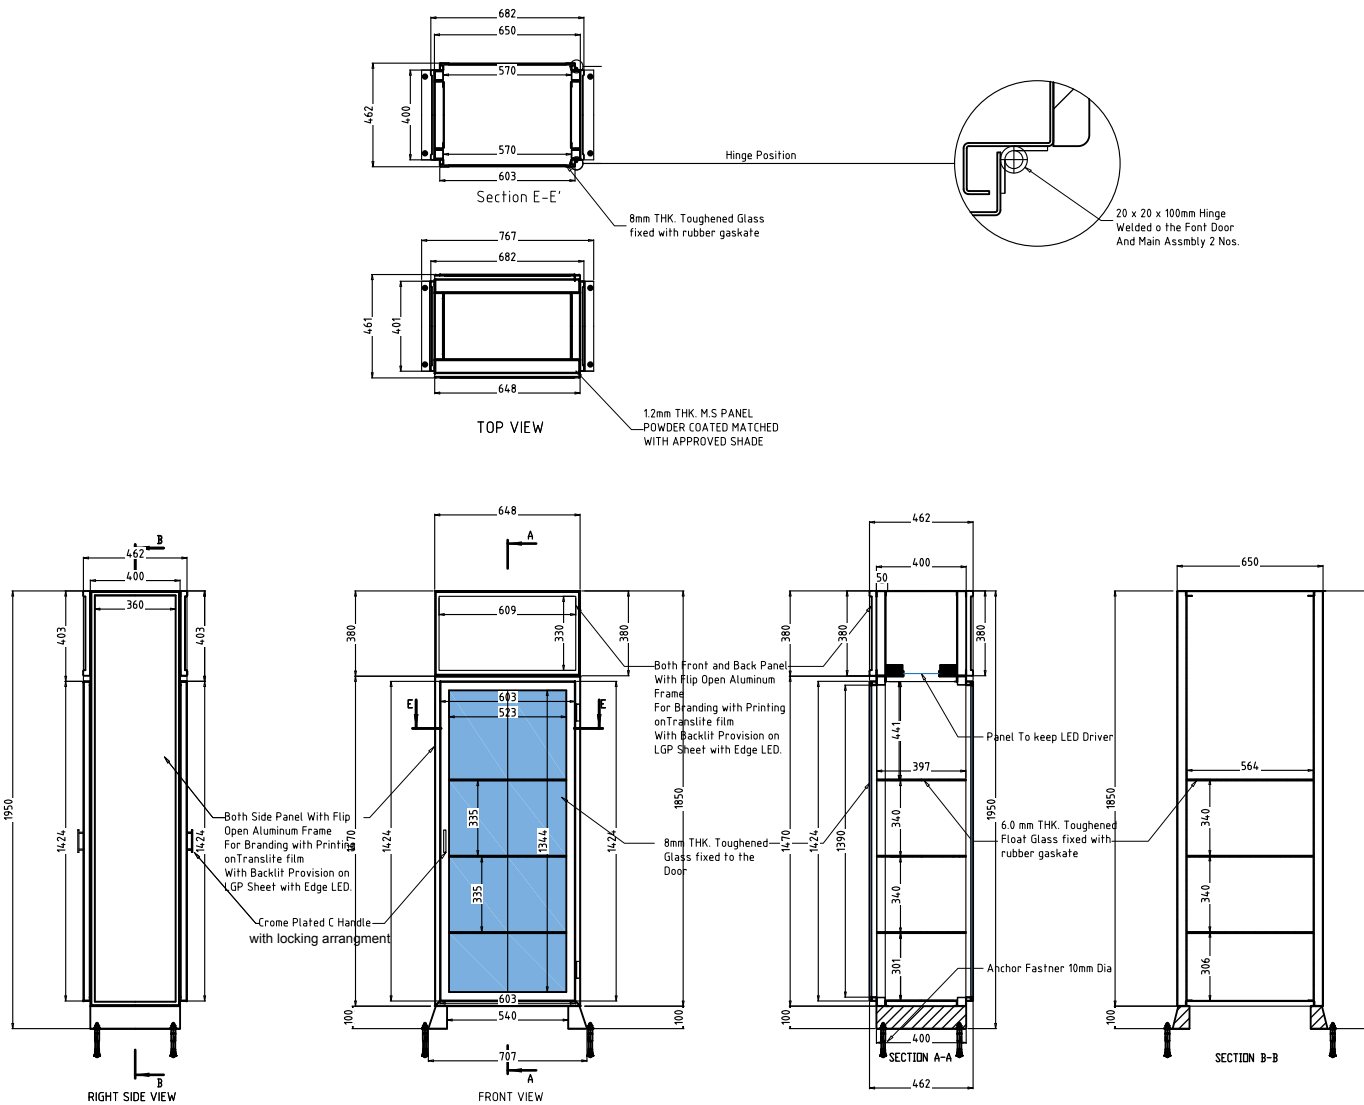





- NOTES:
1. ALL DIMENSIONS IN MILLIMETERS
 2. THE DRAWING OF THE LUBE MODULE UNIT IS AN INTENT DRAWING
 3. MS. CLADDING IN MS SHEET, 12mm THK.
 4. THE MS STRUCTURE MUST BE SPRAYED WITH TWO COATS OF PRIMER
 5. ONLY CRITICAL DIMENSIONS DETAILED HERE. QUERY IF ADDITIONAL INFORMATION IS NEEDED
 6. ADDITIONAL STIFFENERS ETC. TO BE PROVIDED BY VENDOR, AS PER REQUIREMENT
 7. PATTERN TO BE ROUTED AS PER FINAL ARTWORK

ALL DIMENSIONS IN MILLIMETERS THIS DRAWING IS NOT TO BE SCALED ASSUME TOLERANCES WHEREVER NECESSARY  THIRD ANGLE PROJECTION	DIRECTION	PROJECT: BPCL	
	DATE	TITLE LUBE DISPLAY MODULE - LIT TYPE	SCALE 1:1
	05-10-2020	DRAWING NO. LBM-001	SHEETS A3
		REV.	003

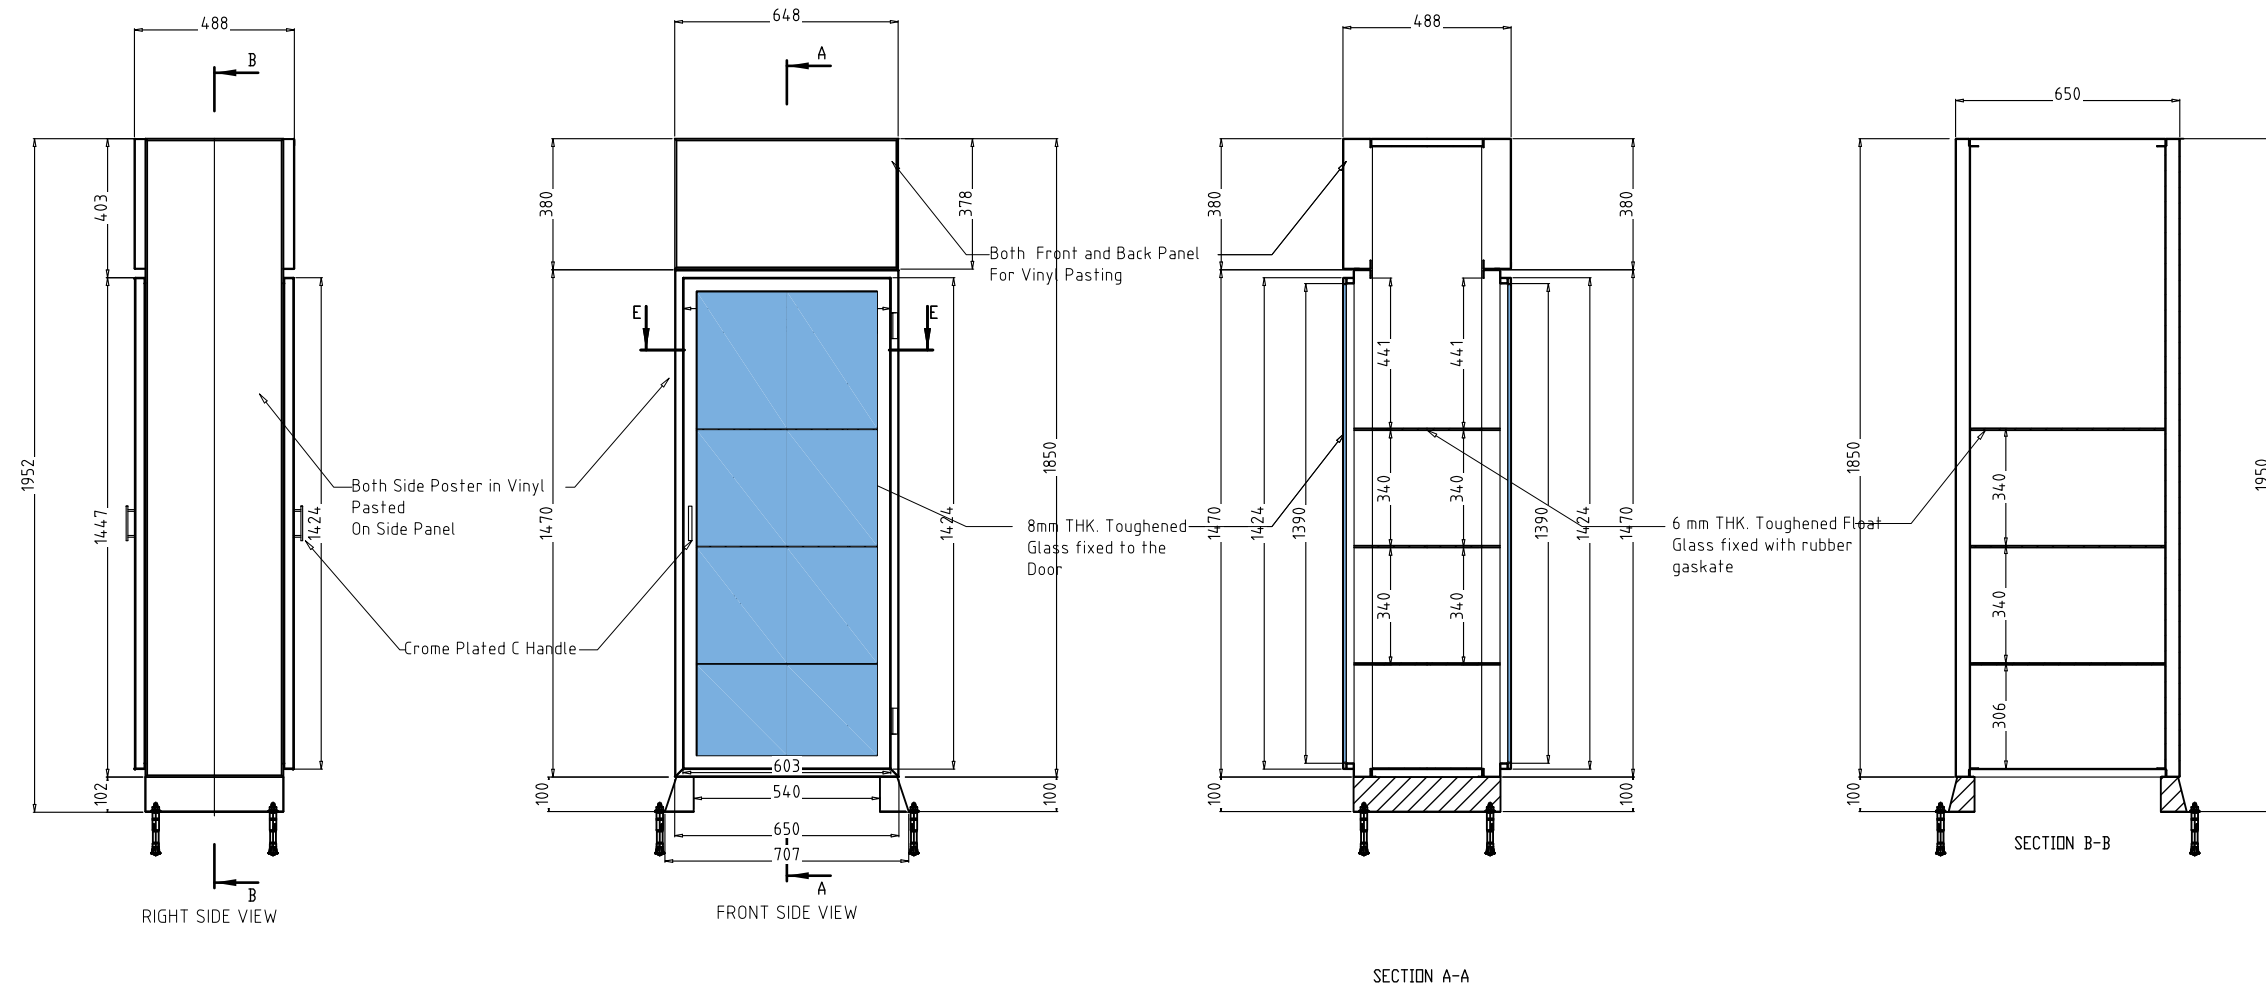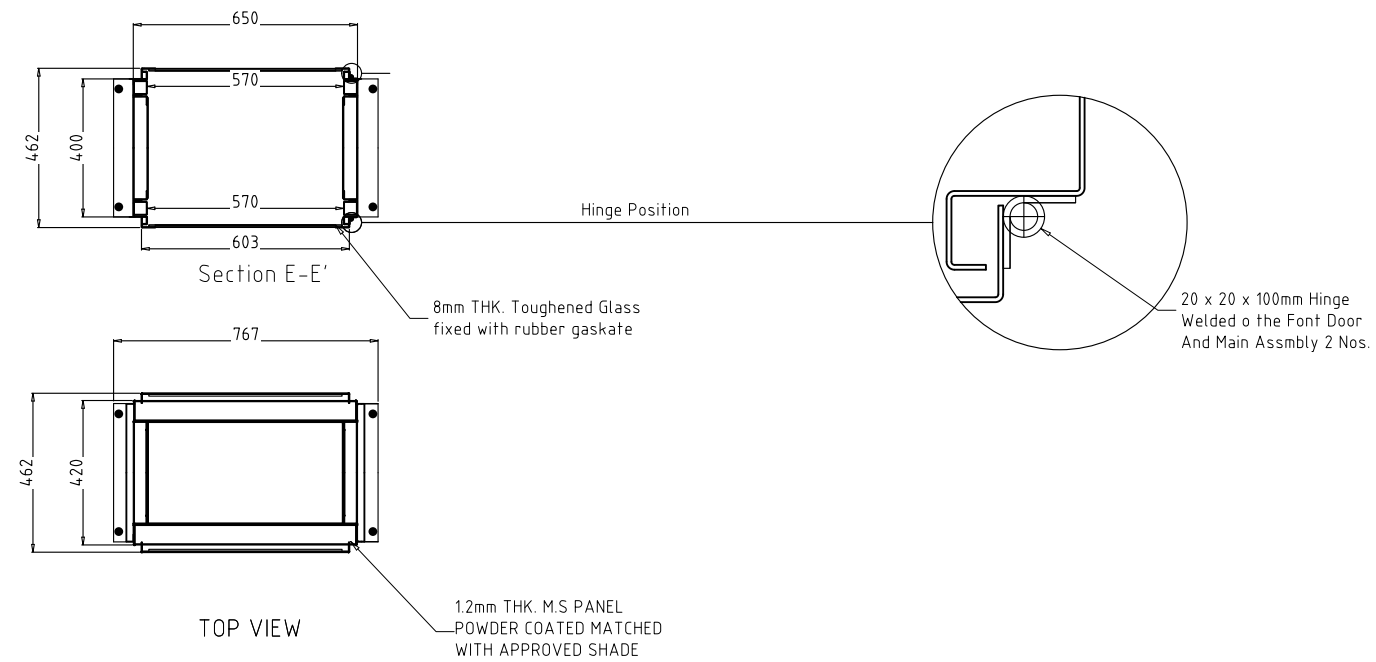


- NOTES:
1. ALL DIMENSIONS IN MILLIMETERS
 2. THE DRAWING OF THE LUBE MODULE UNIT IS AN INTENT DRAWING
 3. MS, CLADDING IN MS SHEET, 1.2mm THK.
 4. THE MS STRUCTURE MUST BE SPRAYED WITH TWO COATS OF PRIMER
 5. ONLY CRITICAL DIMENSIONS DETAILED HERE; QUERY IF ADDITIONAL INFORMATION IS NEEDED
 6. ADDITIONAL STIFFENERS ETC. TO BE PROVIDED BY VENDOR, AS PER REQUIREMENT
 7. PATTERN TO BE ROUTED AS PER FINAL ARTWORK

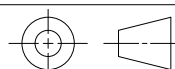
ALL DIMENSIONS IN MILLIMETERS THIS DRAWING IS NOT TO BE SCALED ASSUME TOLERANCES WHEREVER NECESSARY  THIRD ANGLE PROJECTION	DIRECTION	PROJECT: BPCL	
	DATE	TITLE LUBE DSPLAY MODULE - NON LIT	SCALE 1:1
	05-10-2020	DRAWING NO. LBM-002	SHEETS A3
			REV. 003


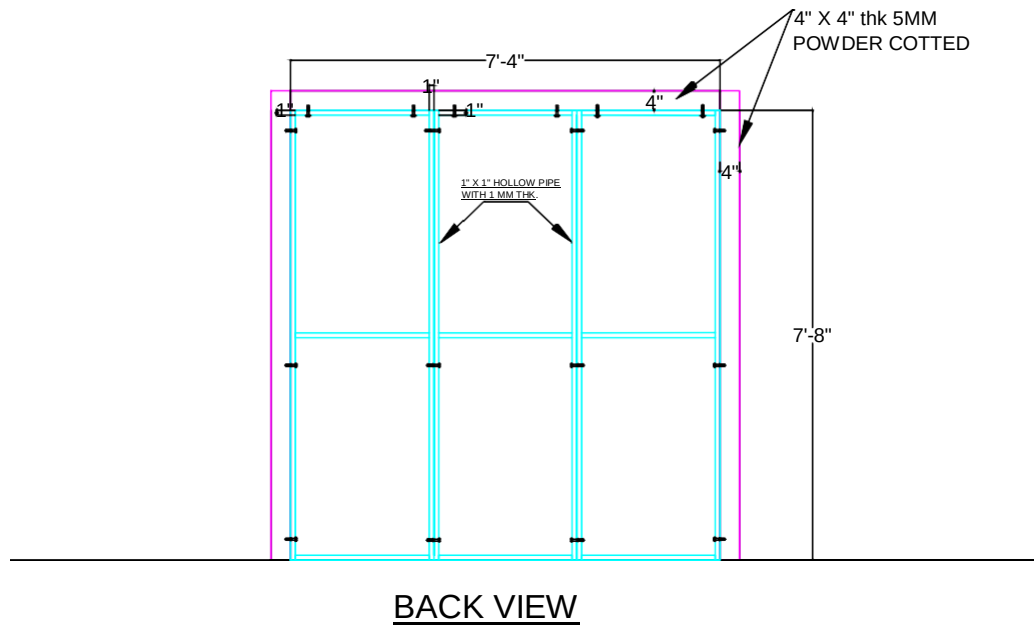
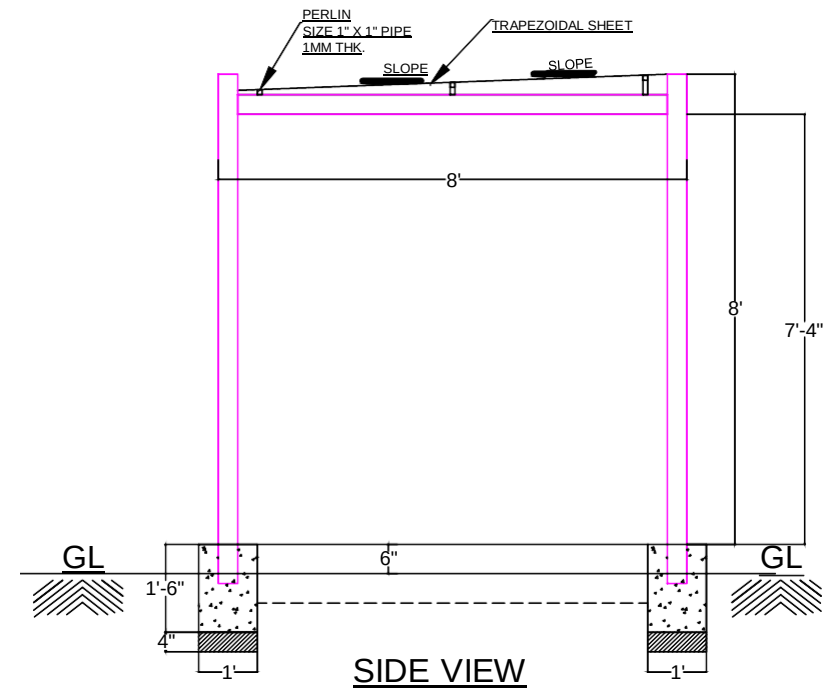
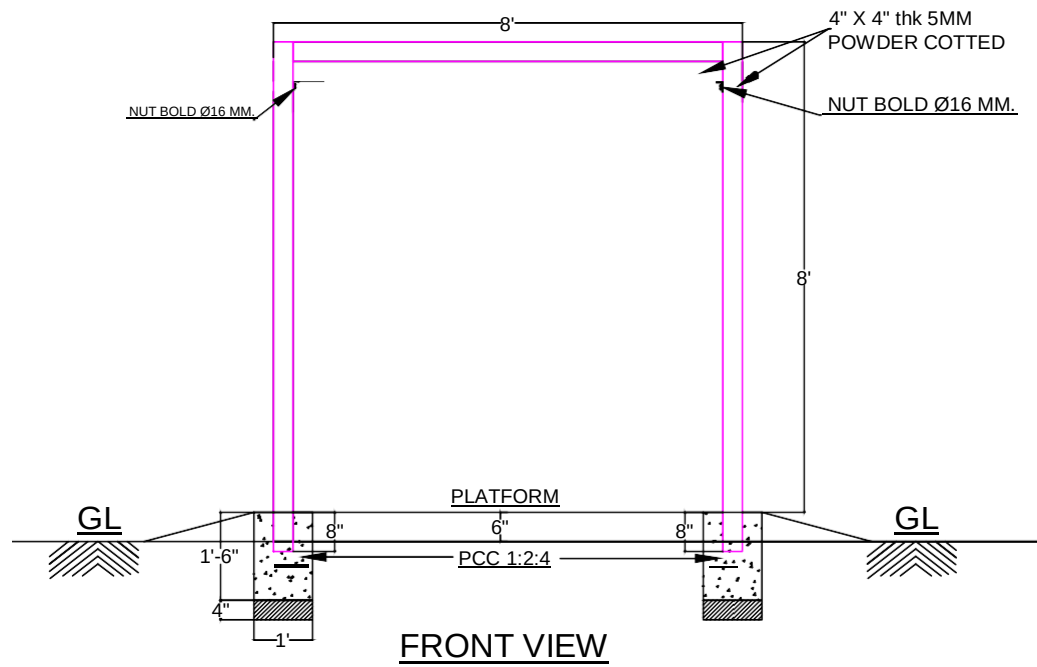


FRAME REAR SIDE
PUTTING 1.5 X 1.5 MM. GI
SHEET FOR ART WORK

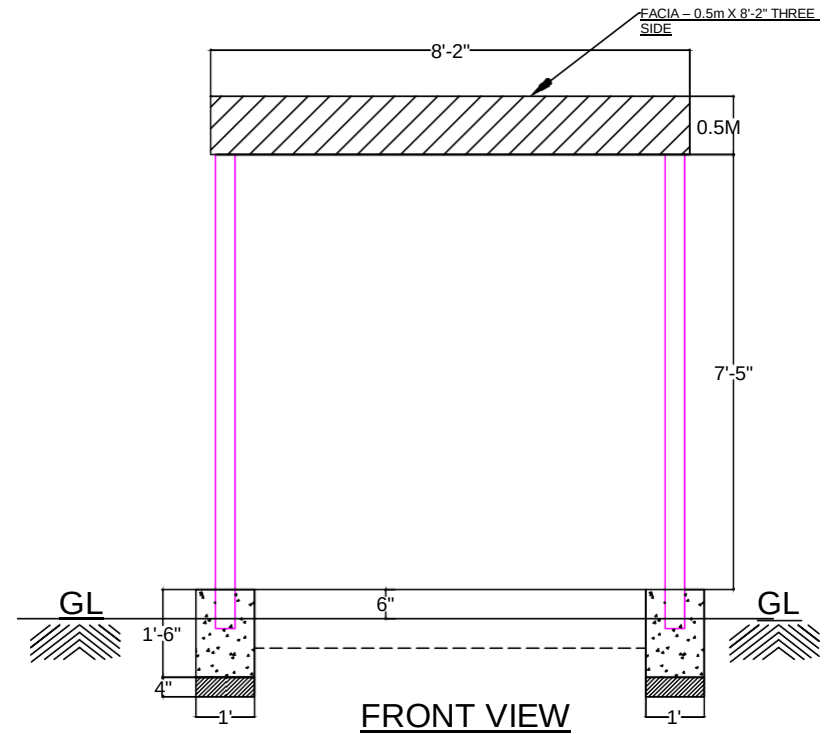

QOC Logo on Fascia: FRP Molded, with Graphic Pasted.

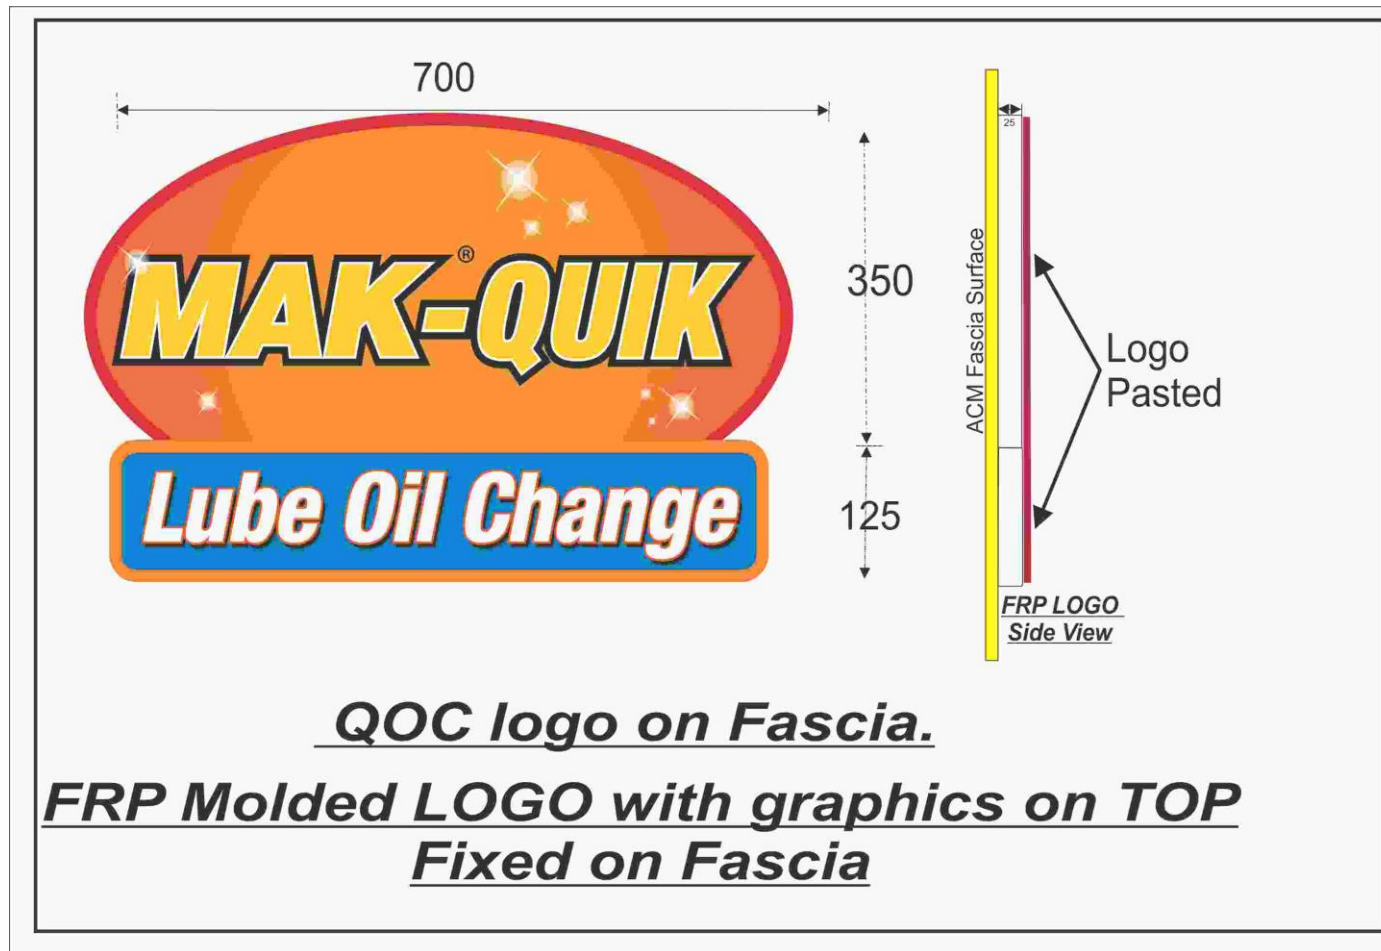


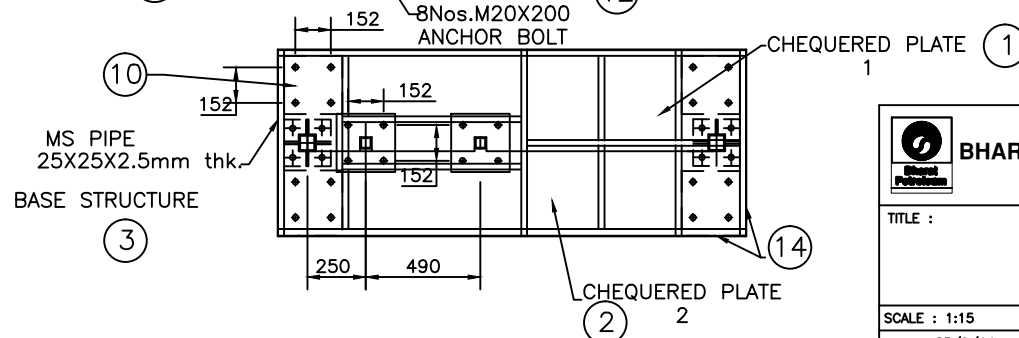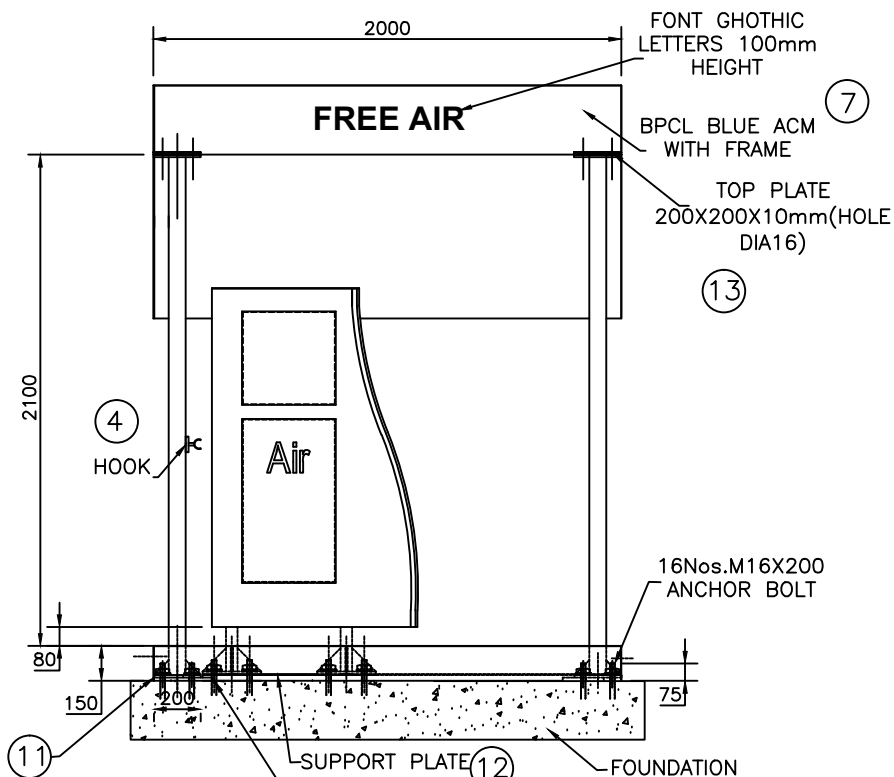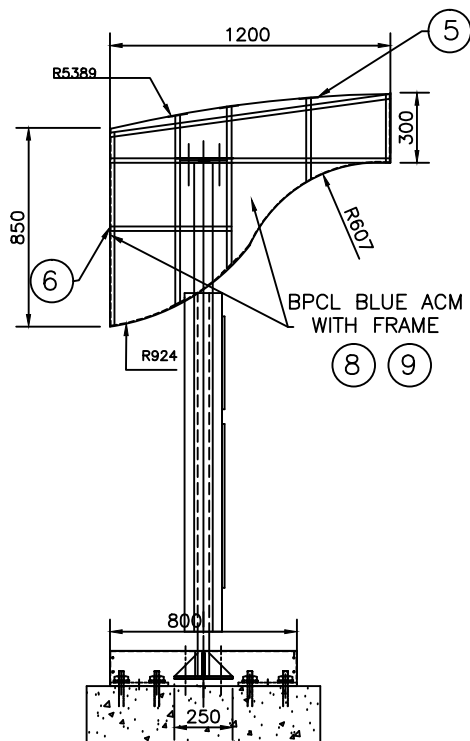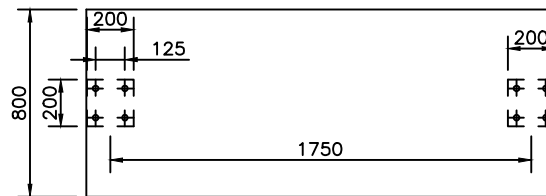

14	SIDE PLATE BASE STRUCTURE	4	MS	1.6mm thk. (2 TYPES)
13	TOP PLATE WELDED	2	MS	200X200X10mm thk.
12	SUPPORT PLATE	1	MS	2000X800X3mm thk.
11	POLE BASE PLATE	2	MS	200X200X10mm thk.
10	MOUNTING PLATE	4	MS	250X250X16mm thk.
9	TOP & SIDE STRUCTURE	1	MS PIPE	20X20X1.6mm thk.
8	SIDE ACM SHEET	2	BPCL BLUE ACM	3mm thk.
7	FRONT ACM SHEET	1	BPCL BLUE ACM	3mm thk.
6	BACK ACM SHEET	1	BPCL BLUE ACM	3mm thk.
5	ROOFING SHEET	1	GI CORRUGATED	1mm thk.
4	PIPE (WITH HOOK)	2	MS PIPE	72X72X5mm thk.
3	BASE STRUCTURE	1	MS PIPE	25X25X2.5mm thk.
2	CHEQUERED PLATE 2	1	ALUMINIUM	1.6MM THK.mm
1	CHEQUERED PLATE 1	1	ALUMINIUM	1.6MM THK.mm
Sr. NO.	DESCRIPTION	QTY.	MATERIAL	SIZE

ALL DIMENSIONS
ARE IN MM.

BHARAT PETROLEUM CORPORATION LTD.				
TITLE :				
AIR BOY CANOPY				
SCALE : 1:15	DRAWN	CHECKED	SHEET NO.	DRAWING NO :
25/9/14	GM.RE		1 of 8	BP.RVI.ASC-A01

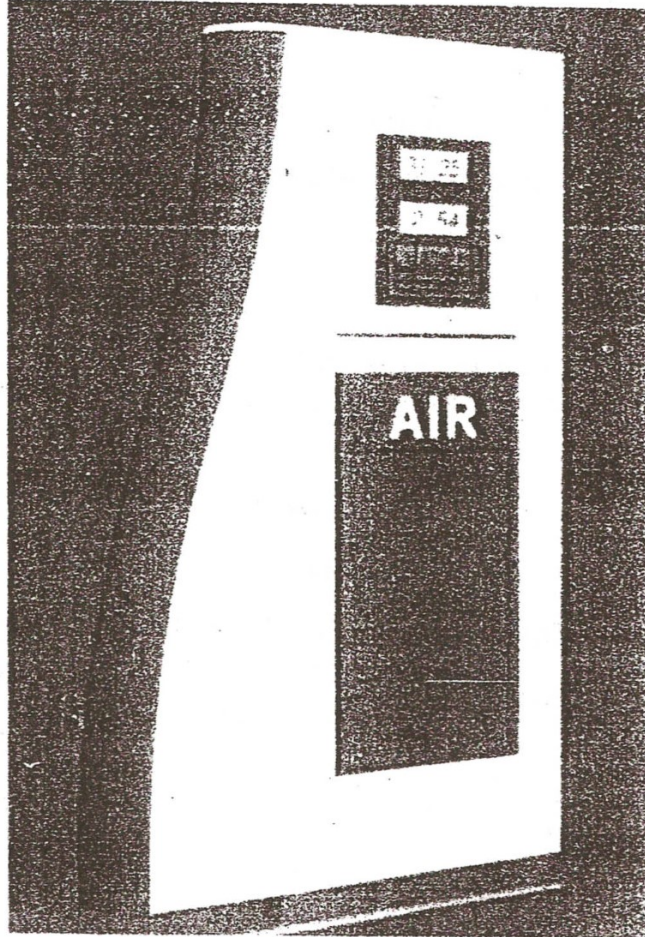


Air Sign

- Air Sign is to provide information to customers who wants to make use of the facility.
- Materials used are Aluminium 2mm thk. and FRP
- This sign is internally lit.
- Approximate dimensions are 900x160x1650(WxDxH).

DRAWING LIST FOR AIR SIGN

SL.NO	PART NAME	PART NO.
1	EXPLODED VIEW	BP-RVI-AS-A01
2	ASSY.DRG.AIR SIGN	BP-RVI-AS-A02
3	BODY FOR AIR LH	BP-RVI-AS-P03
4	BODY FOR AIR RH	BP-RVI-AS-P04
5	DISPLAY PANEL FOR AIR	BP-RVI-AS-P05
6	DISPLAY PANEL FOR AIR/SIGN METER	BP-RVI-AS-P06
7	SIDE COVER FOR AIR SIGN	BP-RVI-AS-P07
8	TUBE FRAME AIR SIGN	BP-RVI-AS-P08
9	TUBE FRAME AIR SIGN	BP-RVI-AS-P09
10	POLE FOR AIR SIGN	BP-RVI-AS-P10
11	STRUCTURE FOR AIR SIGN	BP-RVI-AS-P11
12	SUPPORT FRAME FOR AIR	BP-RVI-AS-P12
13	C CHANNEL FOR TUBE LIGHT FRAME	BP-RVI-AS-P13
14	TOP AND BOTTOM SHEET	BP-RVI-AS-P14

SR.NO	NAME OF COMPONENT	QTY
10	TOP & BOTTOM SHEET	2
9	TUBE LIGHT 2 FEET	2
8	SUPPORT FOR AIR SIGN	2
7	TUBE FRAME ASSLY	1
6	POLE ASSLY FOR AIR WATER	1
5	SIDE COVER	1
4	DISPALY PANEL FOR AIR METER	1
3	DISPALY PANEL FOR AIR WATER	2
2	BODY FOR AIR WATER SIGN RH	1
1	BODY FOR AIR WATER SIGN LH	1

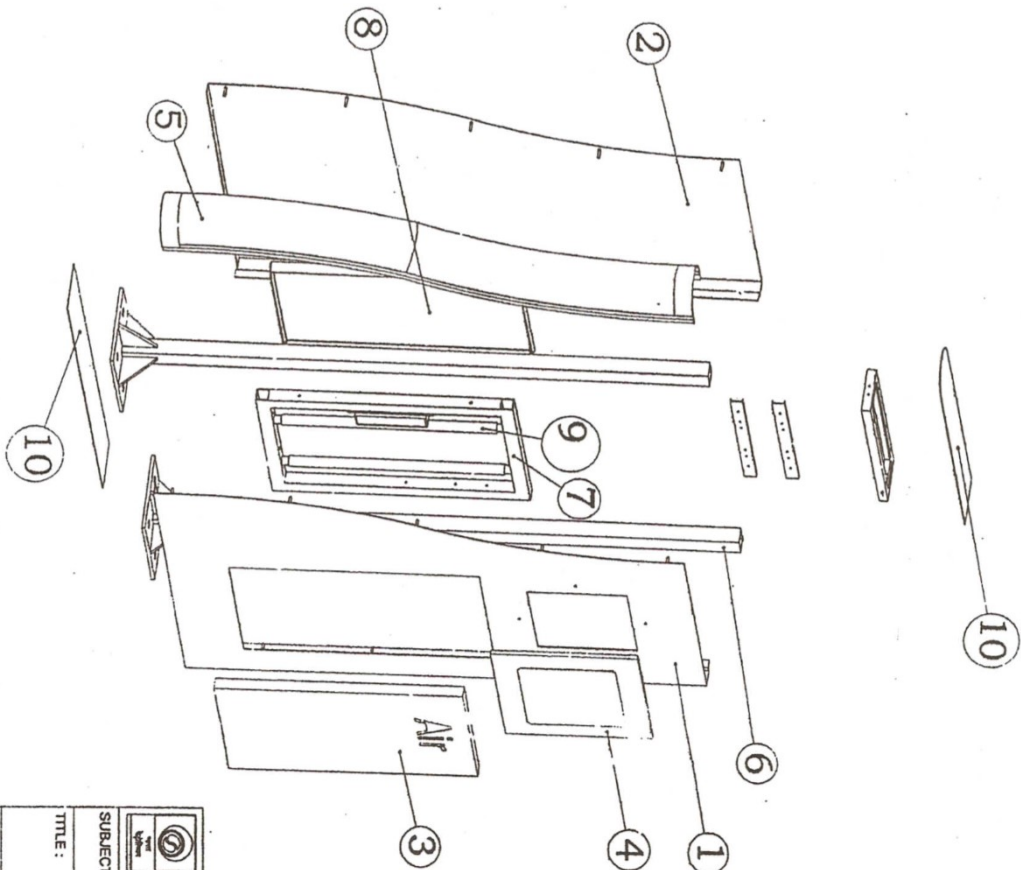


भारत पेट्रोलियम कॉर्पोरेशन लिमिटेड
BHARAT PETROLEUM CORPORATION LTD.




SUBJECT: R V M

TITLE:

AIR SIGN

SCALE: 1:12	DRAWN: -	THACED	CHECKED	SHEET NO: 1 OF 14	DRAWING NO. BP.RVI.AS-A01
DATE: 12/6/04	CHEF MGR. (REG) HQ				

DATE: _____
 DRAWING NO. _____
 NUMBER CROSS-OUT
 AND SUPERSEDED
 DRAWINGS

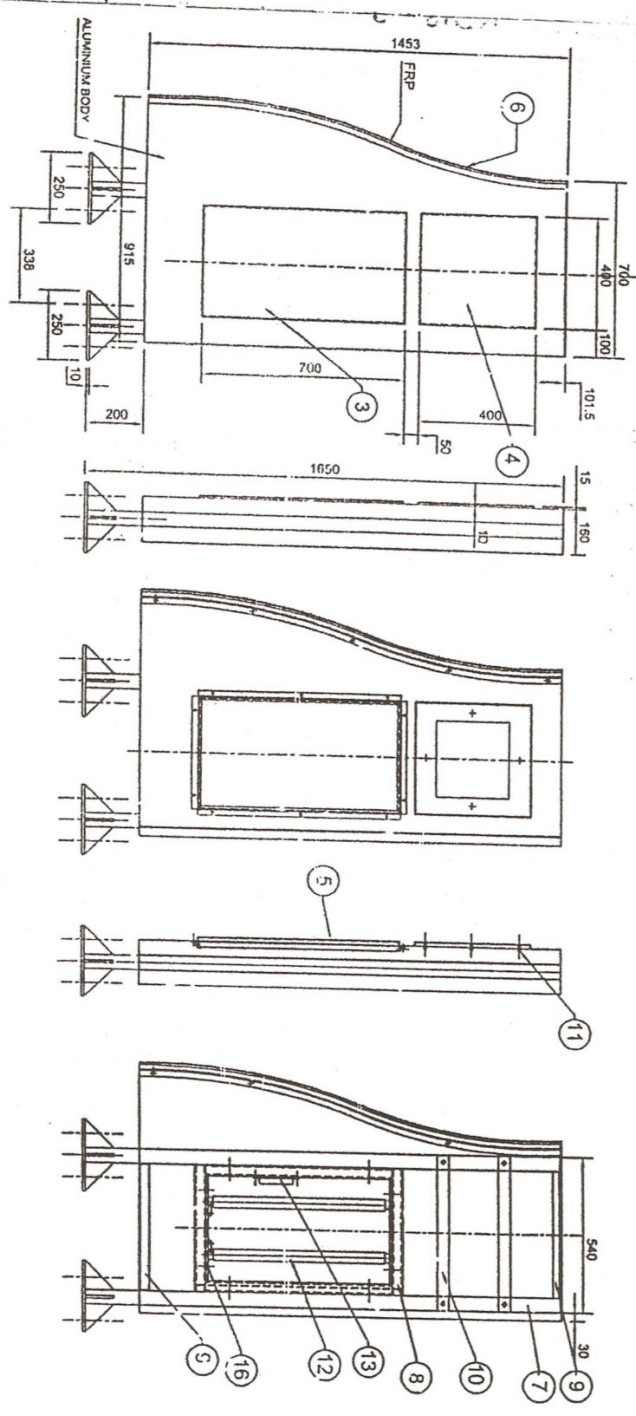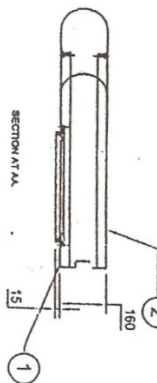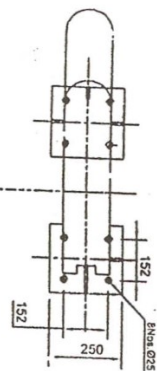

S.NO	DESCRIPTION	QTY
1	C CHANNEL	2
2	CONNECTOR	1
3	BALAST ELECTRONIC UNIT	1
4	PHILLIPS WAVE	1
5	TUBE LIGHT SHEET	2
6	MS STUD	20
7	MS PLAT 3X55mm	2
8	SUPPORT FOR AIR SIGN	2
9	TUBE FRAME ASSEMBLY	1
10	POLE ASSEMBLY FOR AIR SIGN	1
11	SIDE COVER (FRP)	1
12	Z CHANNEL FOR AIR SIGN	1
13	DISPLAY PANEL FOR AIR METER	1
14	DISPLAY PANEL FOR AIR METER	2
15	BODY FOR AIR METER SIGN (H)	1
16	BODY FOR AIR METER SIGN (L)	1

भारत पेट्रोलियम कॉर्पोरेशन लिमिटेड
BHARAT PETROLEUM CORPORATION LTD.


SUBJECT: R V M


TITLE:

AIR SIGN

SCALE:	DRAWN	TRACED	CHECKED
DATE: 12/6/04	CHIEF MGR. (RE) HQ		SHEET NO. 2 of 14

DATE	DRAWING NO.
	NUMBERS CROSSED OUT ARE SUPERSEDED DRAWINGS
	DRAWING NO. BP.RVI.AS-A02

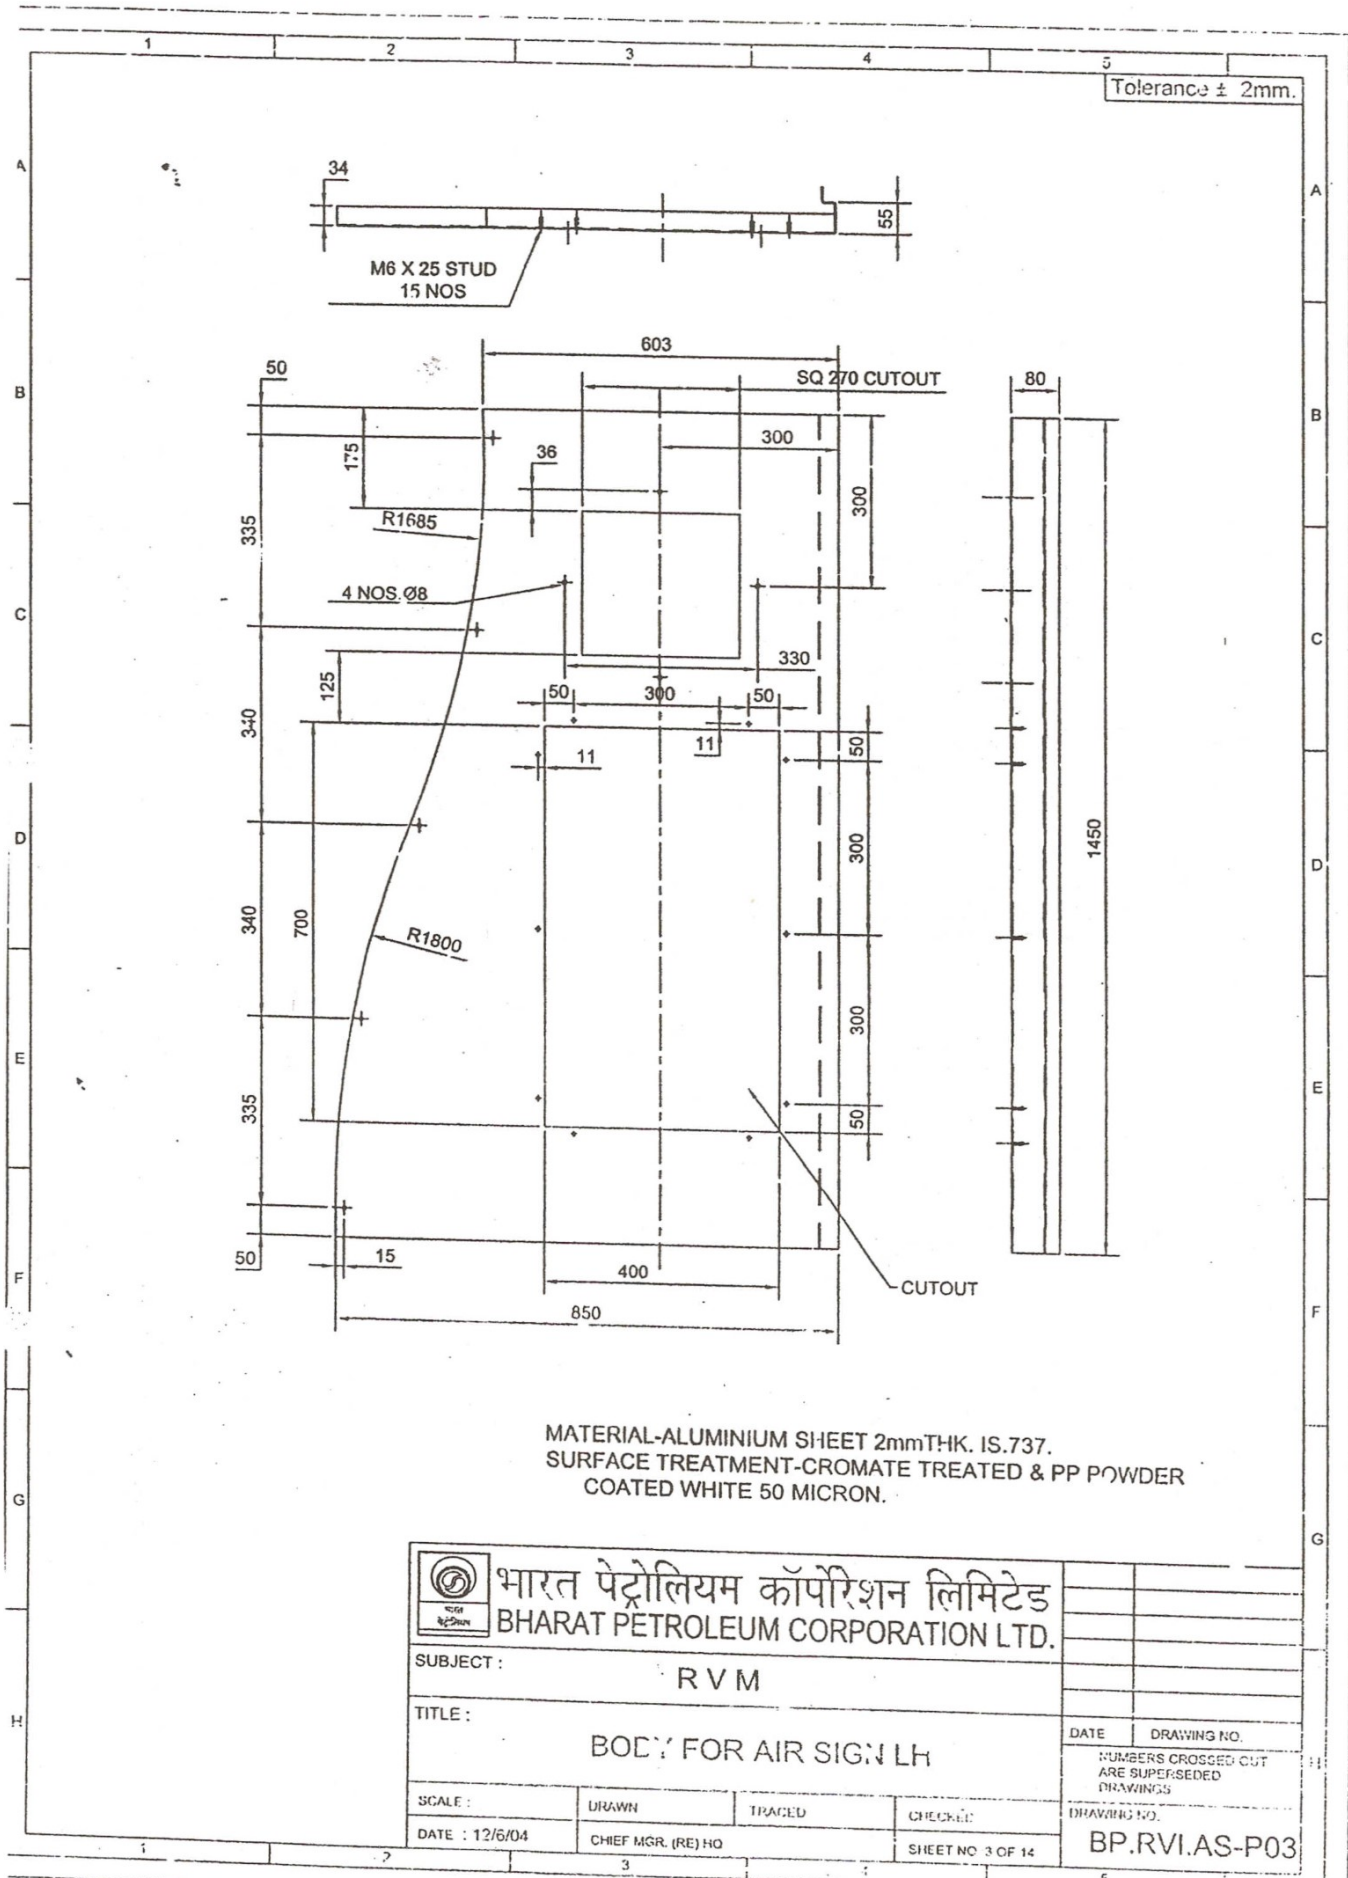

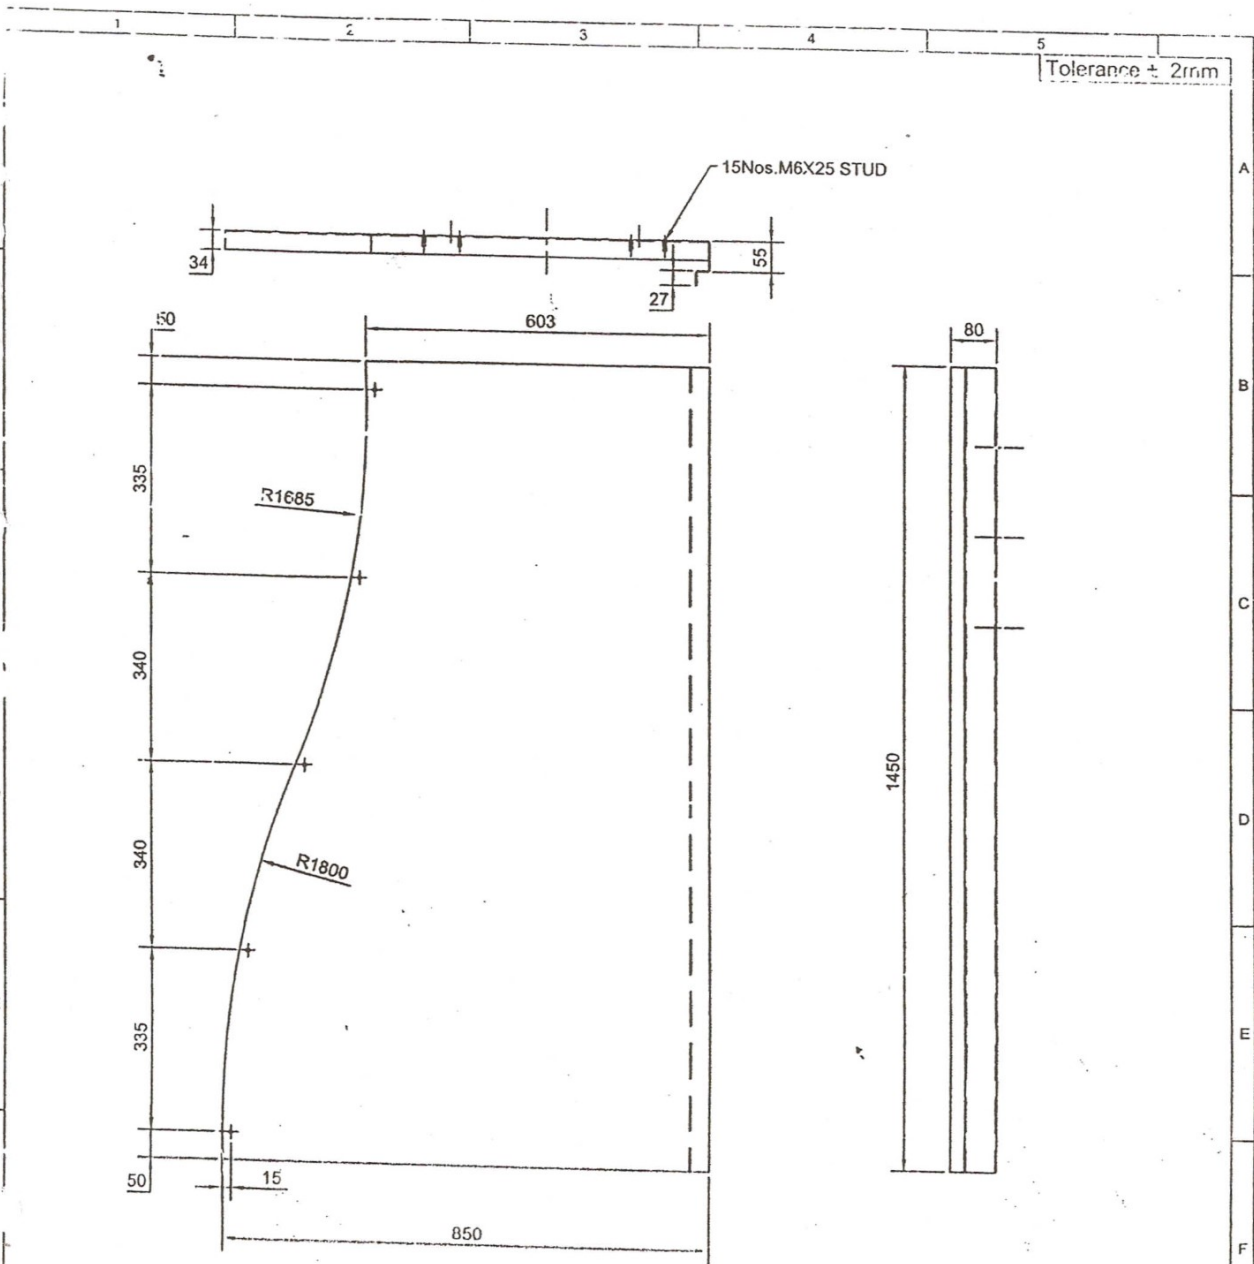


MATERIAL-ALUMINIUM SHEET 2mmTHK. IS:737.
SURFACE TREATMENT-CROMATE TREATED & PP POWDER
COATED WHITE 50 MICRON.

 भारत पेट्रोलियम कॉर्पोरेशन लिमिटेड BHARAT PETROLEUM CORPORATION LTD.			
SUBJECT : R V M			
TITLE : BODY FOR AIR SIGN RH			
SCALE :	DRAWN	TRACED	CHECKED
DATE : 12/6/04	CHIEF MGR. (RE) HQ	SHEET NO. 4 OF 14	
		DATE	DRAWING NO.
		NUMBERS CROSSED OUT ARE SUPERSEDED DRAWINGS	
		DRAWING NO. BP.RVI.AS-P04	

25

1		2		3		4		5		Tolerance: $\pm 2\text{mm}$	
TEXT FONT-ARIAL REGULAR BACKLIT WITH PET-G 3mm thk.OPAL.										35	
395										695	
100										130	
(184)										35	
TYRE PRESSURE CHART IN PRINTED VINYL STUCK HERE.										35	
MATERIAL:ALUMINIUM SHEET 2mm thk.IS:737. SURFACE TREATMENT-CROMATE TREATED &PAINTED IN PU BPCL BLUE.										35	
भारत पेट्रोलियम कॉर्पोरेशन लिमिटेड BHARAT PETROLEUM CORPORATION LTD.										35	
SUBJECT: RVM										35	
TITLE: DISPLAY PANEL FOR AIR (AL)										35	
SCALE:		DRAWN		TRACED		CHECKED		DATE		DRAWING NO.	
DATE : 12/6/04		CHIEF MGR. (RE) HQ		SHEET NO :5 OF 14		DRAWING NO.		NUMBERS CROSSED OUT ARE SUPERSEDED DRAWINGS		H	
BP.RVI.AS-P05										35	


25

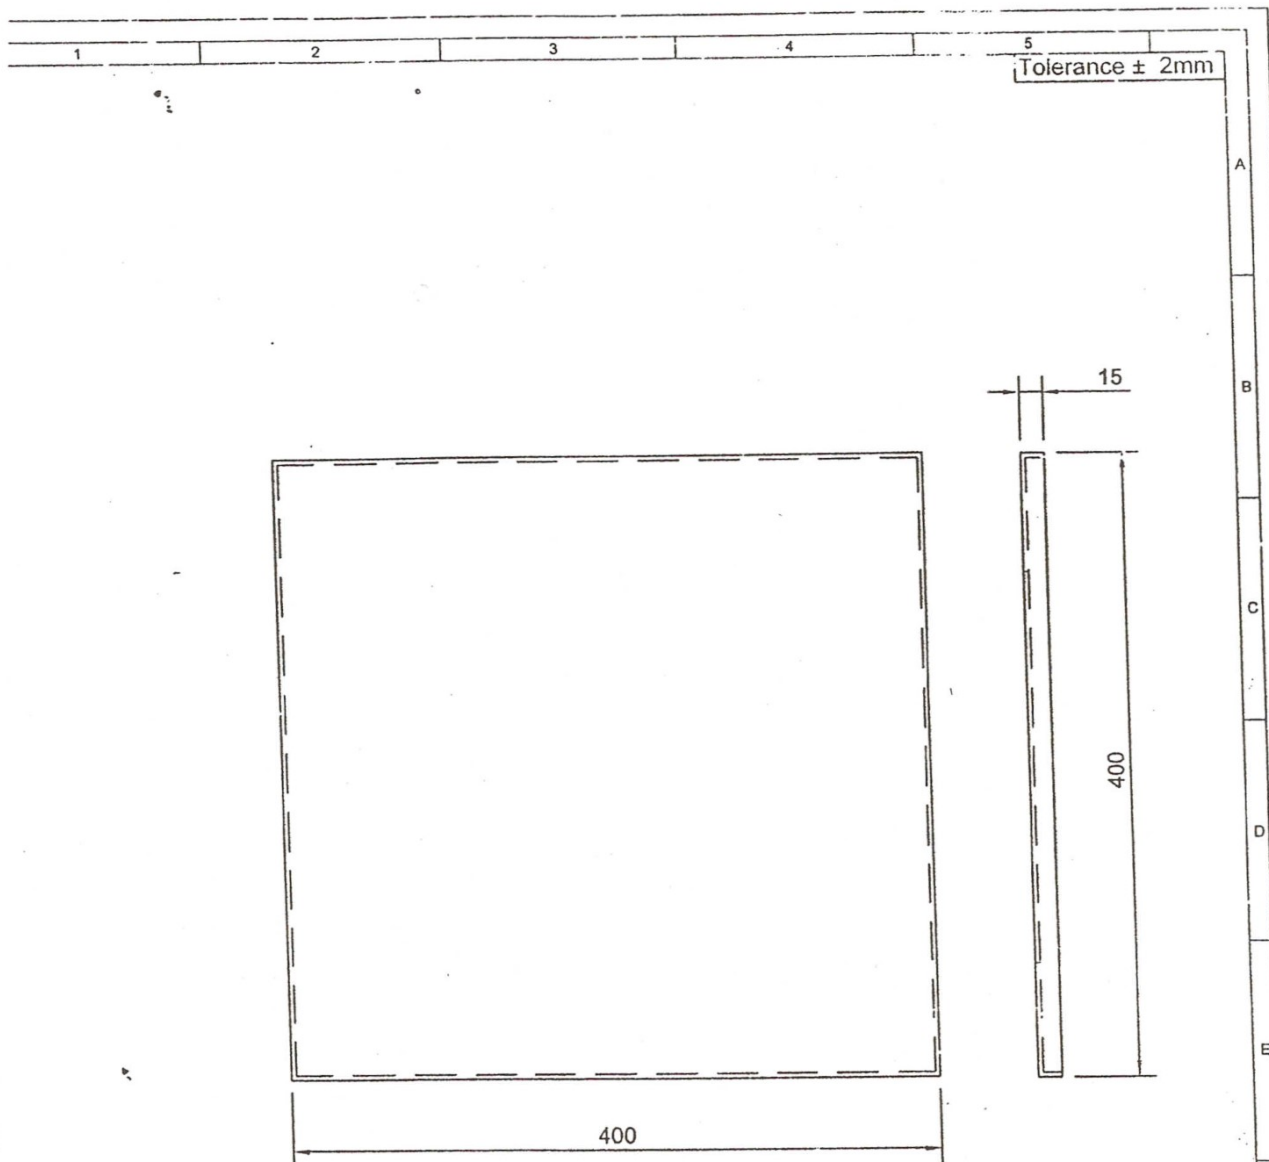

MATERIAL-ALUMINIUM SHEET 2mmTHK. IS:737.
SURFACE TREATMENT-CROMATE TREATED & PU PAINTED
IN BPCL BLUE.


 भारत पेट्रोलियम कॉर्पोरेशन लिमिटेड BHARAT PETROLEUM CORPORATION LTD.			
SUBJECT :		R V M	
TITLE :		DISPLAY PANEL FOR AIR SIGN METER	
SCALE :	DRAWN	TRACED	CHECKED
DATE : 12/6/04	CHIEF MGR. (RE) HQ	SHEET NO : 6 OF 14	
		DATE	DRAWING NO.
		MEMBERS CROSSED OUT ARE SUPERSEDED DRAWINGS	
		DRAWING NO. BP.RVI.AS-P06	

27

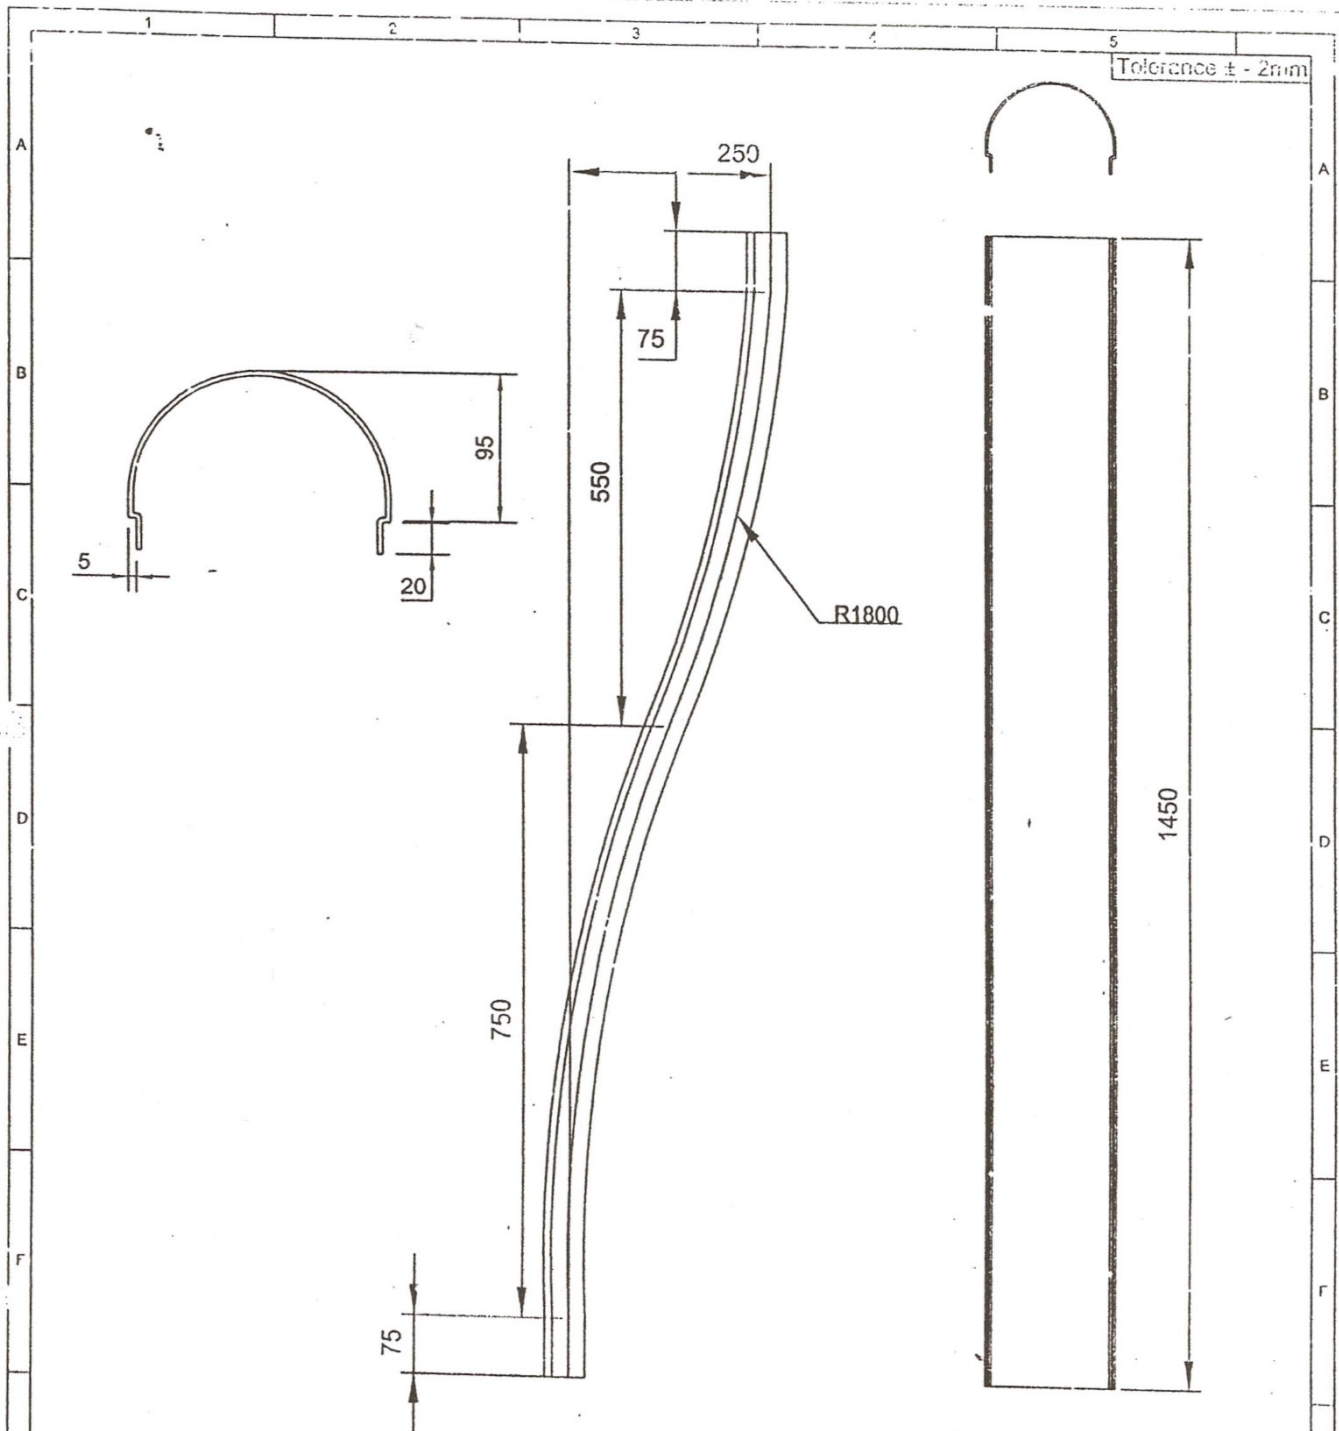


MATERIAL-FRP 3mmTHK.ADD RIBS AS REQD. TO MAINTAIN PROFILE
PAINT- PU. BPCL BLUE PAINTED 50 micron. OUTSIDE ONLY.


		भारत पेट्रोलियम कॉर्पोरेशन लिमिटेड BHARAT PETROLEUM CORPORATION LTD.			
SUBJECT : R V M					
TITLE : SIDE COVER FOR AIR SIGN				DATE _____ DRAWING NO. _____ NUMBERS CROSSED OUT ARE SUPERSEDED DRAWINGS	
SCALE :	DRAWN	TRACED	CHECKED	DRAWING NO.	
DATE : 12/6/04	CHIEF MGR. (RE) HQ		SHEET NO : 7 OF 14	BP.RVI.AS-P07	

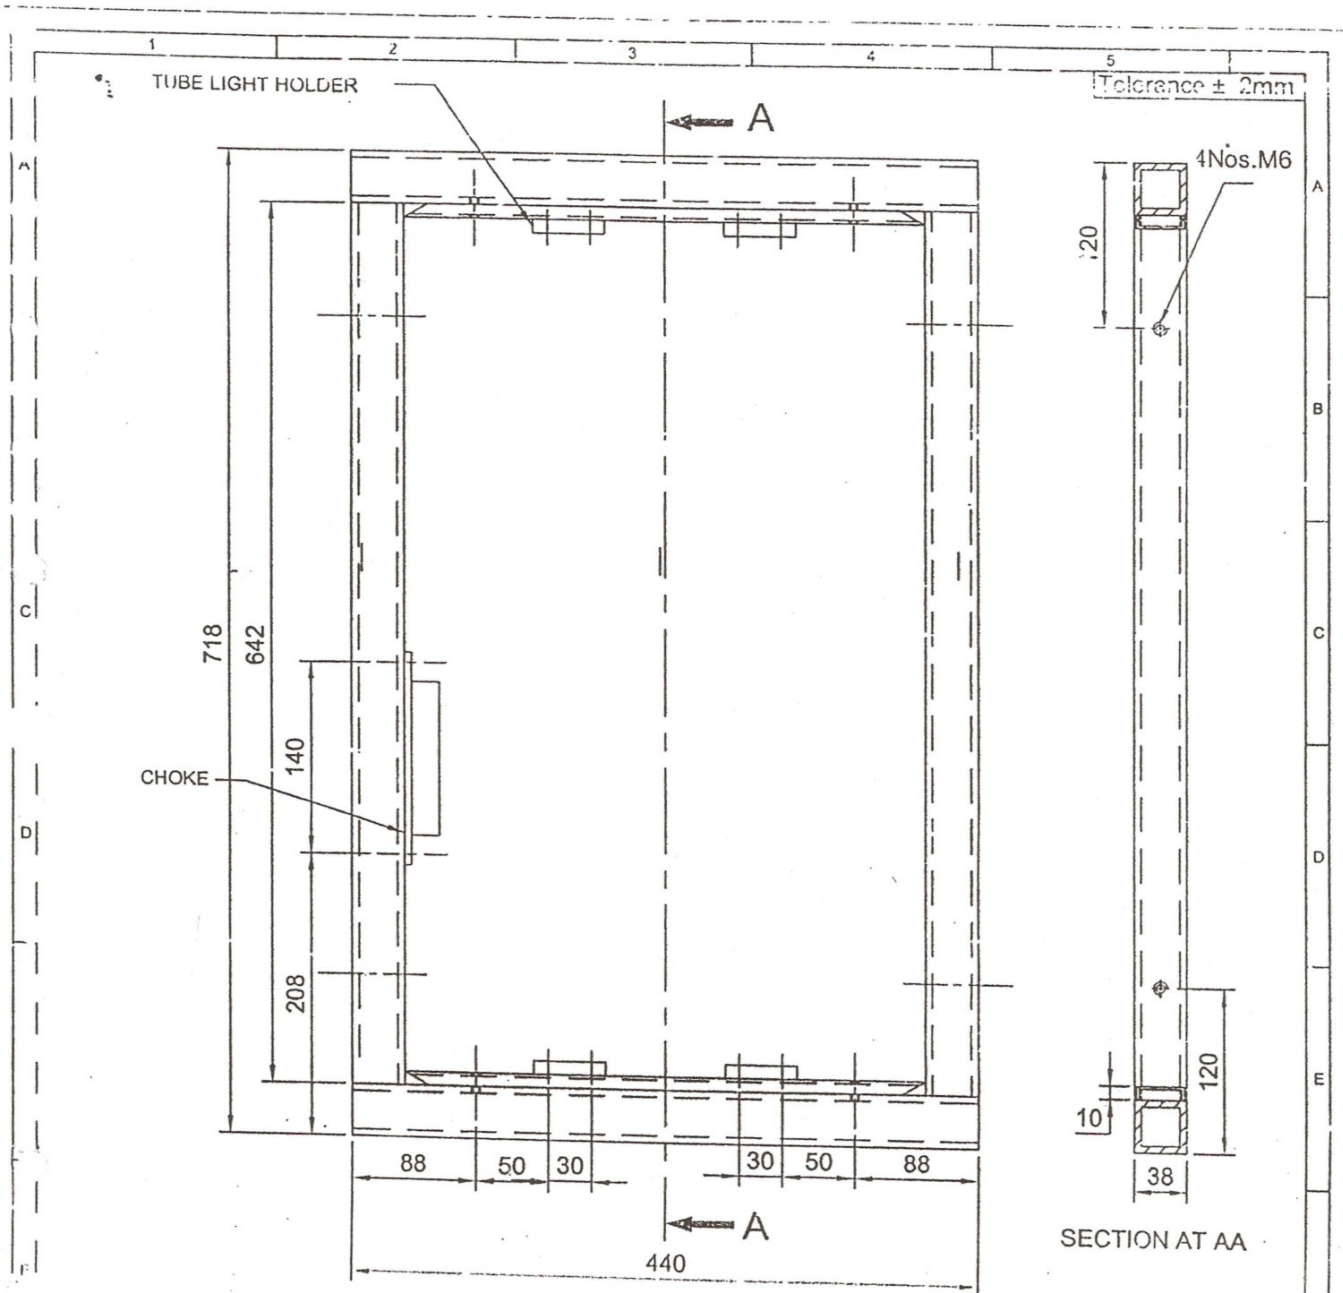

MATERIAL-ALUMINIUM SQ. 38X38X2.5 mm THK.
 ALUMINIUM C CHANNEL 35X10X1.5mm THK.
 SQ.38X38X2.5= LENGTH 440 QTY 2
 LENGTH 622 QTY 2
 'C' CHANNEL=LENGTH 366mm QTY 2


 भारत पेट्रोलियम कॉर्पोरेशन लिमिटेड BHARAT PETROLEUM CORPORATION LTD.			
SUBJECT:		R V M	
TITLE:		TUBE FRAME ASSY AIR SIGN	
SCALE:	DRAWN	TRACED	CHECKED
DATE : 12/6/04	CHIEF MGR. (PS) HQ		SHEET NO. 10 OF 14
		DATE	DRAWING NO.
		NUMBERS CROSSED OUT ARE SUPERSEDED DRAWINGS	
		DRAWING NO. BP.RVI.AS-P08	

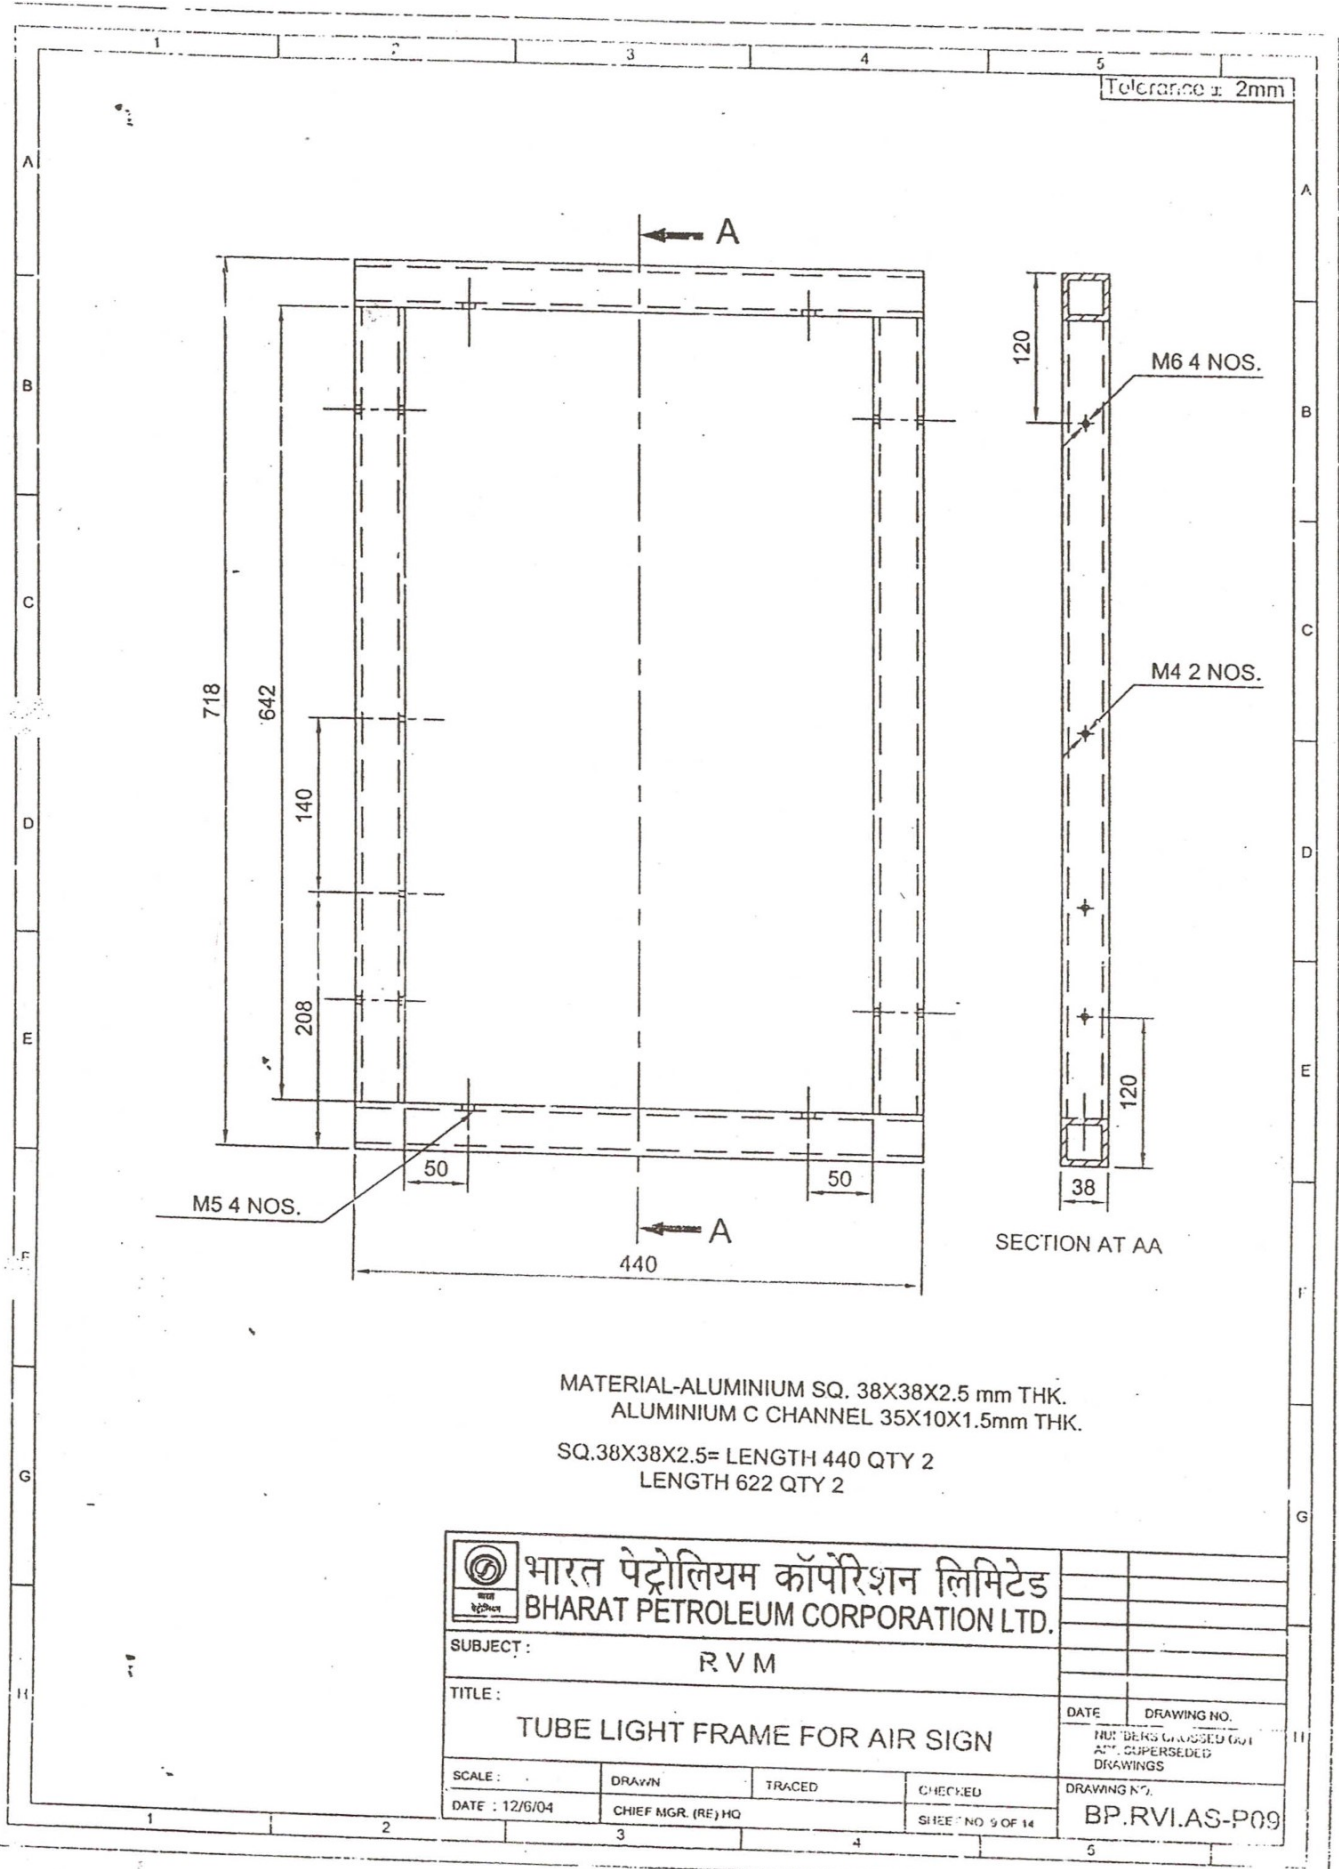

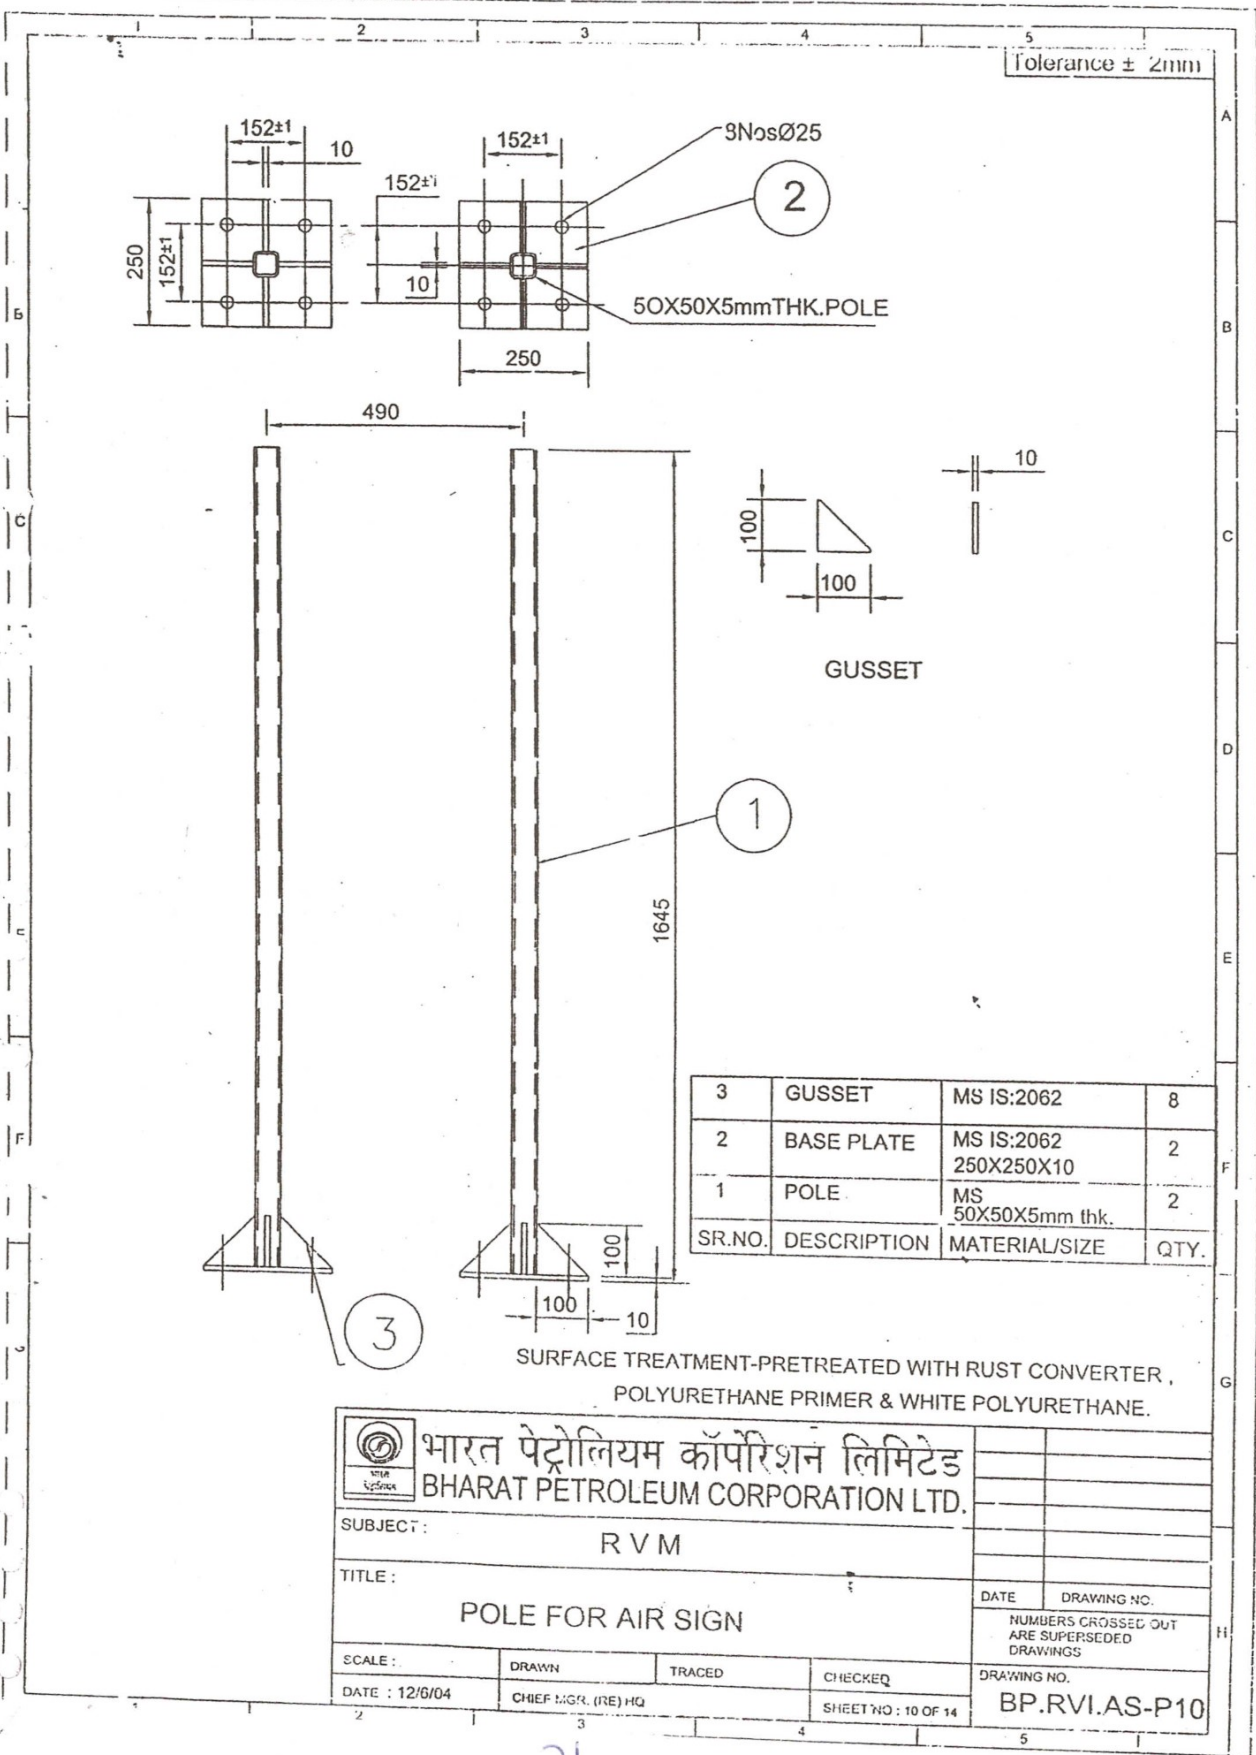



 भारत पेट्रोलियम कॉर्पोरेशन लिमिटेड BHARAT PETROLEUM CORPORATION LTD.			
SUBJECT: R V M			
TITLE: STRUCTURE FOR AIR SIGN			
SCALE:	DRAWN	THICKED	CHECKED
DATE: 11.12.2004	CHIEF MGR. (P&M)		SHEET NO. 11 of 14
DRAWING NO. BP.RV.I.A.S. 01		DATE: DRAWN BY: NO. 1 AMT. SUPERSEDED DRAWING: 3	


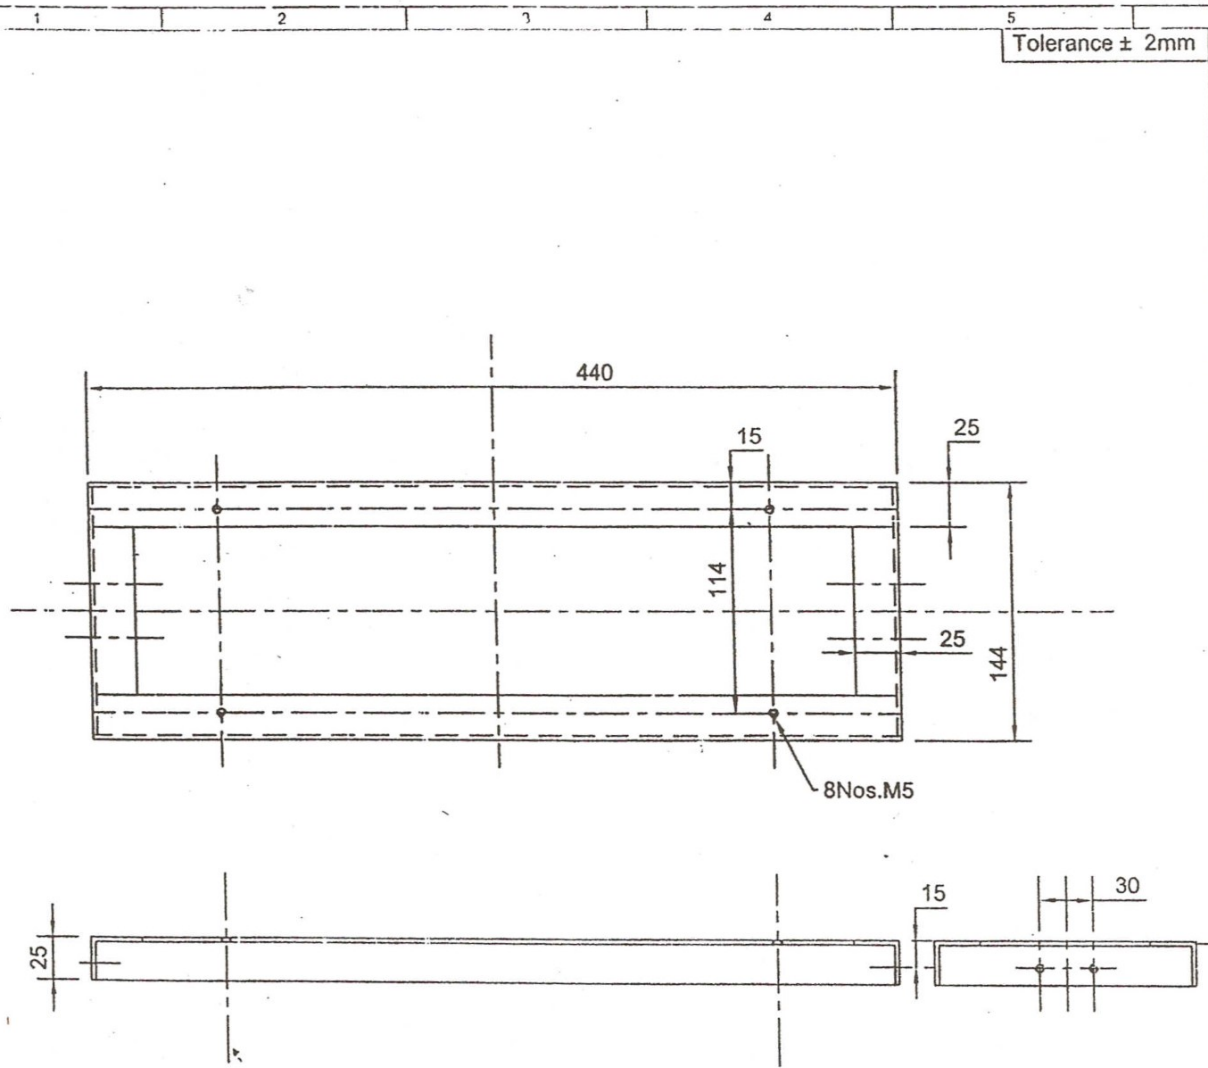


MATERIAL-HRCA STEEL 25X25X5mm thk.

SURFACE TREATMENT-PRETREATED & PU WHITE PAINTED.40 MICRON.

 भारत पेट्रोलियम कॉर्पोरेशन लिमिटेड BHARAT PETROLEUM CORPORATION LTD.					
SUBJECT: R V M					
TITLE: SUPPORT FRAME FOR AIR SIGN				DATE	DRAWING NO.
				NUMBERS CROSSED OUT ARE SUPPRESSED DRAWINGS	
SCALE:	DRAWN	TRACED	CHECKED	DRAWING NO.	
DATE : 12/6/04	CHIEF MGR. (RE) HQ			BP.RVI.AS-P12	
SHEET NO : 12 OF 14					

Tolerance $\pm 2\text{mm}$

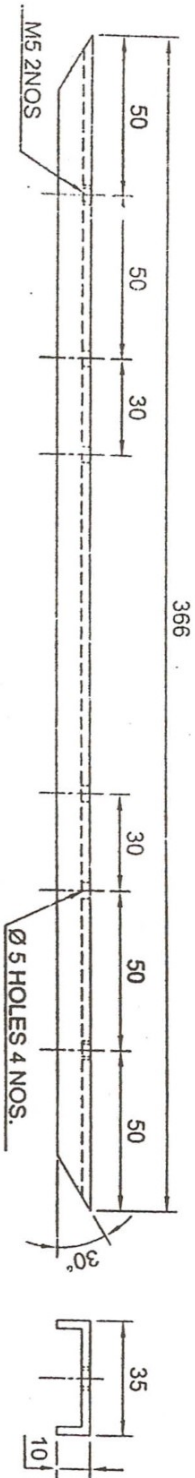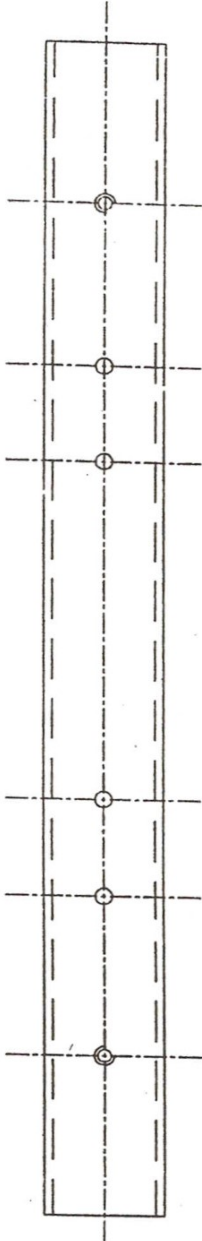

MATERIAL-ALUMINIUM 1.2mm THK.IS:737.
SURFACE TREATMENT - CHROMATE TREATED.
QTY.-2 NOS.



भारत पेट्रोलियम कॉर्पोरेशन लिमिटेड
BHARAT PETROLEUM CORPORATION LTD.

R V M


SUBJECT: R V M
TITLE: C CHANNEL FOR TUBE LIGHT FRAME (AIR)

SCALE:	DATE:	CHKD. NO.	TRACED	CHECKED	SHEET NO.	DRAWING NO.
1:12/04	12/04	13			13 of 14	BP.RVI.AS-P13

Tolerance $\pm$ 2mm

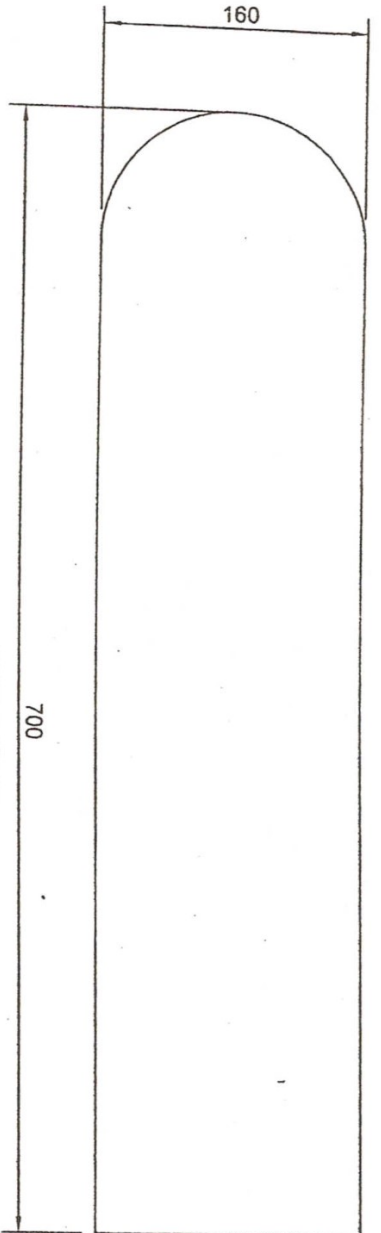


TOP SHEET

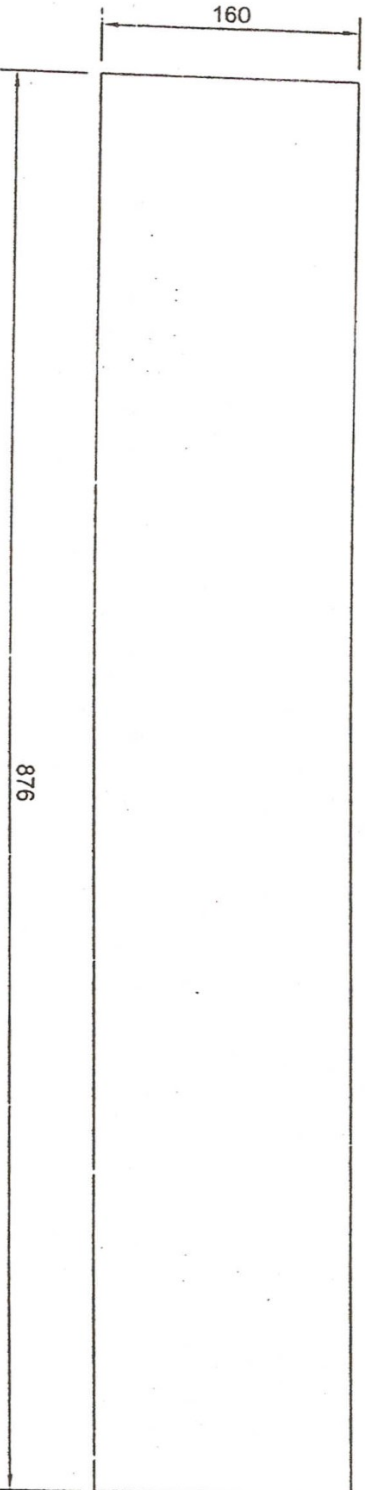

BOTTOM SHEET

MATERIAL-ALUMINIUM SHEET 2mm THK.IS:737.
SURFACE TREATMENT-CHROMATE TREATED & PU
WHITE PAINTED.40 micron.

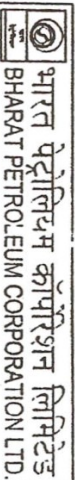

भारत पेट्रोलियम कॉर्पोरेशन लिमिटेड
BHARAT PETROLEUM CORPORATION LTD.

SUBJECT:

R V M

TITLE:

TOP & BOTTOM SHEET

SCALE:

DATE: 12/5/24

DRAWN: CHE MGR. (FEN) 3

TRACED

CHECKED: SHEET NO. 14 OF 14

DRAWING NO. BP.RV.AS-P1

DATE: 12/5/24
DRAWING NO. BP.RV.AS-P1
NUMBERS CHECKED 3/5
ARE SUBMITTED

Product Data sheet for Air sign

- 1) Pole as per drg. No. BP-RVI-AS-P10 is provided for mounting the sign. They are PU painted white. Support as per drg. No. BP-RVI-AS-P11 is provided.
- 2) Body as per drg. No. BP-RVI-AS-P03, P04 are screwed to the pole on one side. Other side of body (curved end) is stud welded & FRP cladding painted in BPCL Blue is fixed to that.
- 3) Top cut out in front side is done at site as per requirement for fixing meter. MS flat of 38*5mm (2 nos.) are provided for meter fixing as shown in drawing BP-RVI-AS-A02.
- 4) Display panel as per drawing no. BP-RVI-AS-P05 is screwed to 4 nos. angles which are stud welded & fixed in bottom cutout of main body. This display panel has engraved letters. An opal PET-G sheet of 3mm is fixed with VHB tape from back side.
- 5) A tube light frame as per drawing no. BP-RVI-AS-P08, P09 is screwed to pole directly as shown in drawing no. BP-RVI-AS-A02.
- 6) A top cover & bottom cover is provided.

Material Data sheet for Air sign :

Description	Material
1) Body LH/RH	Aluminium 2mm thk. Precoated with white paint/powder coated with PP powder.
2) Display panel fixed & hinged	Al. 2mm thk BPCL blue powder coated
3) Display panel for meter	Al. 2mm thk BPCL blue powder coated
4) Z channel	Aluminium sheet 1.2mm thk. as per IS : 737. PU white painted
5) Side cover	FRP 3mm thk. Painted in BPCL Blue
6) Pole assy.	50*50*5mm thk. MS PU white painted
7) Tube frame assy.	Aluminium extrusion 38*38*2.5 mm thk.
8) Electronic ballast	36/40w
9) Tube light	20w
10) VHB tape	1.1mm thk

Check points:

- 1) No damage/dent.
- 2) No light leakage.




Packing:

- Each unit is wrapped in polythene & packed in wooden crate.

DRAWING LIST FOR NO SIGN

SL.NO	PART NAME	PART NO.
1	NO SIGN	BP-RVI-NS-A01
2	DISPLAY PANEL	BP-RVI-NS-P02

DETAIL AT X

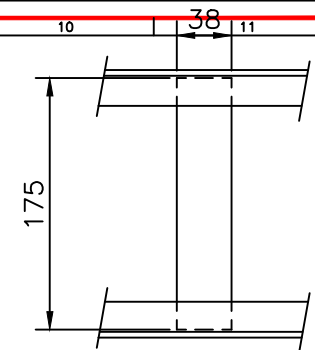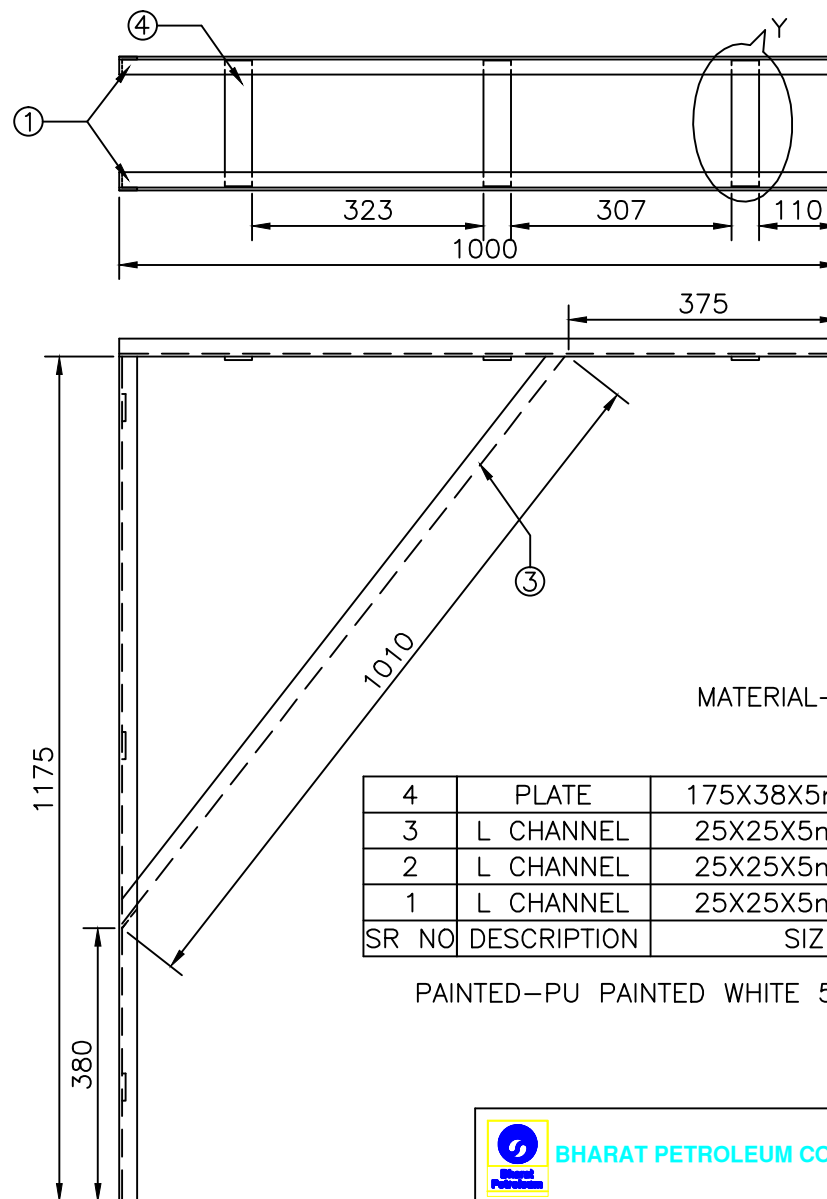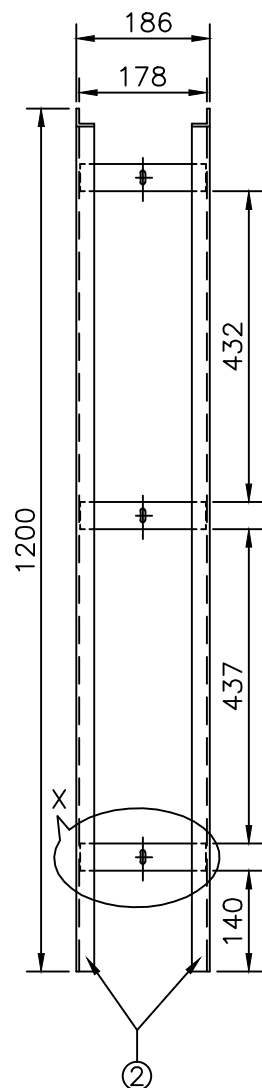

DETAIL AT Y

MATERIAL—HR
SIZE AS GIVEN TABLE.

4	PLATE	175X38X5mm thk.		6
3	L CHANNEL	25X25X5mm thk.	1010	2
2	L CHANNEL	25X25X5mm thk.	1175	2
1	L CHANNEL	25X25X5mm thk.	1000	2
SR NO	DESCRIPTION	SIZE	LENGTH	QTY.

PAINTED—PU PAINTED WHITE 50 micron.



BHARAT PETROLEUM CORPORATION LTD.

TITLE :

STRUCTURE FOR ARCH

DATE	DRAWING NO.
------	-------------

SCALE :

DATE : 23/5/18

DRAWN:

	GM.RE
--	-------

	CHECKED
--	---------

SHEET NO.
3 of 11

DRAWING NO :	
--------------	--

BP.RVI.CA-P03

REVISIONS

Product Description	13W LED linear Profile Light with top cover of PC diffuser, Constant Current , 1 Mtr Long with 120 LEDs per RM Linear Profile Light of Dimension 1000mm by 16.0mm by 16.0mm – IP65, LM-79 & LM-80, Operating Voltage -12V
Fixture Dimension	1000mm X 16mm X 16mm
Fixture Body	Aluminium Extrusion fabricated Housing
Viewing Angle	120
Colour Temp	10000K
CRI	>70K
Working Temperature	-35 to 80deg C
Fixture Efficacy	>75lm/watt
Life Span	50,000 hrs, On Site Warranty Five Year
LED Driver	BIS Approved Fully Potted IP67 LED Driver (Non-Integral. Single Driver to be used for 2 Linear Fixtures) with below specification: (a) Over Voltage Cut Off & Restart (220V & 100V) (b) Under Voltage Cut off & Restart(220V & 100V) (c) 440V Protection – 8 Hours (d) THD <10% (e) Power Factor >0.9 (f) Surge Protection: 4KV
LED Chip Make	CREE/ NICHIA/ OSRAM/ SAMSUNG/ CITIZEN/ PHILIPS (Lumileds)/SEOUL/ Bridgelux
External Surge Protection for one side fascia	10KA/10KV, IP67 SPD to be used (Non Integral)




- ✓ Certification from CPRI/Intertek / UL /TUV lab for LED fittings and Driver required.
- ✓ Light fittings to be provided with all necessary internal wiring (Copper 3/20).
- ✓ Drivers should comply with BIS specifications.
- ✓ All products should be to embossed or screen printed (No sticker or skin allowed) with Name of supplier, Batch No & Year.
- ✓ Warranty for lights will be given for lot by suppliers. RVI vendor to provide warranty to BPCL linking this batch no with sites. Overall responsibilities of warranty lies with RVI Vendor.

ajay
kumar

Digitally signed
by ajay kumar
Date: 2022.01.10
21:12:05 +05'30'

Technical Specs:Annex1

BPCL RVI-Additional Element- Front Lit Fascia

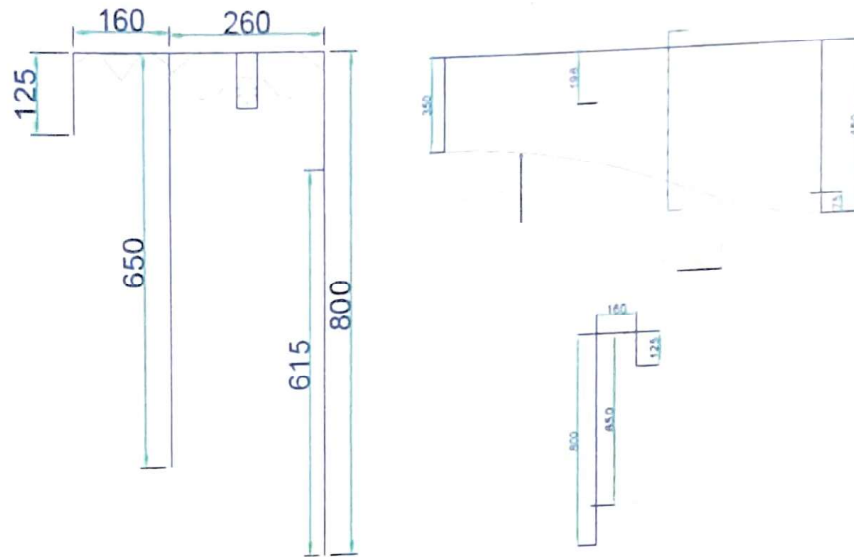

Supply and installation of an additional **Blue ACM (BPCL Approved Make)** at an offset of 160mm over the existing Blue fascia wave. The additional blue ACM fascia is rectangular in shape of 125 mm depth measured from the top of the existing fascia in the groove formed between 125mm depth and 160mm offset of the Blue Fascia, the LED tube-lights of 'White' Color of 13 Watts with a viewing angle of 120 degrees.




Blue Fascia lighting Tech Specs :

Front Lit light for Blue wave of 1-meter-long LED linera light with aluminum profile and Driver fitted on the outer edge of the Pelmet touching the front and upper sides. The LED Strips are placed in the profile at 45-degree angle from horizontal (or vertical) to lighten towards the canopy fascia.

ajay
kumar

Digitally signed
by ajay kumar
Date:
2022.01.10
21:11:38 +05'30'

5	FLEX	1
4	SPRING	4
3	BOTTOM ROD	1
2	FRAME	1
1	BASE	1
SR NO	SIZE	QTY.

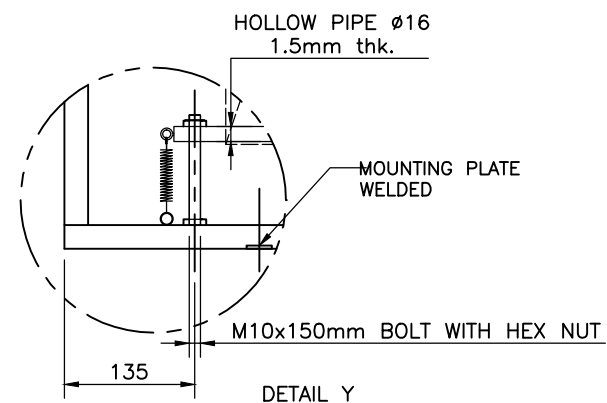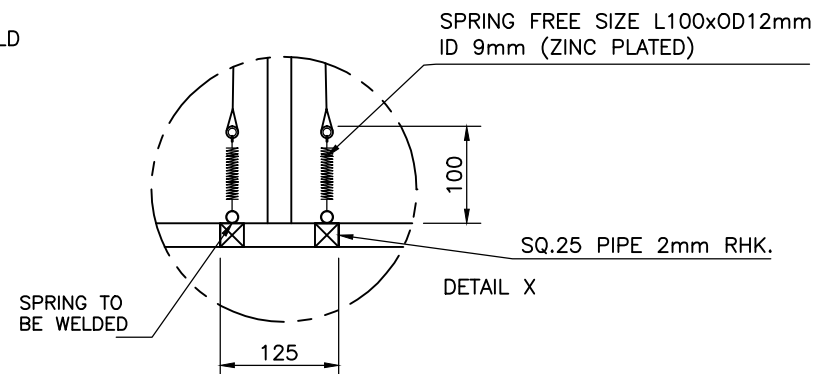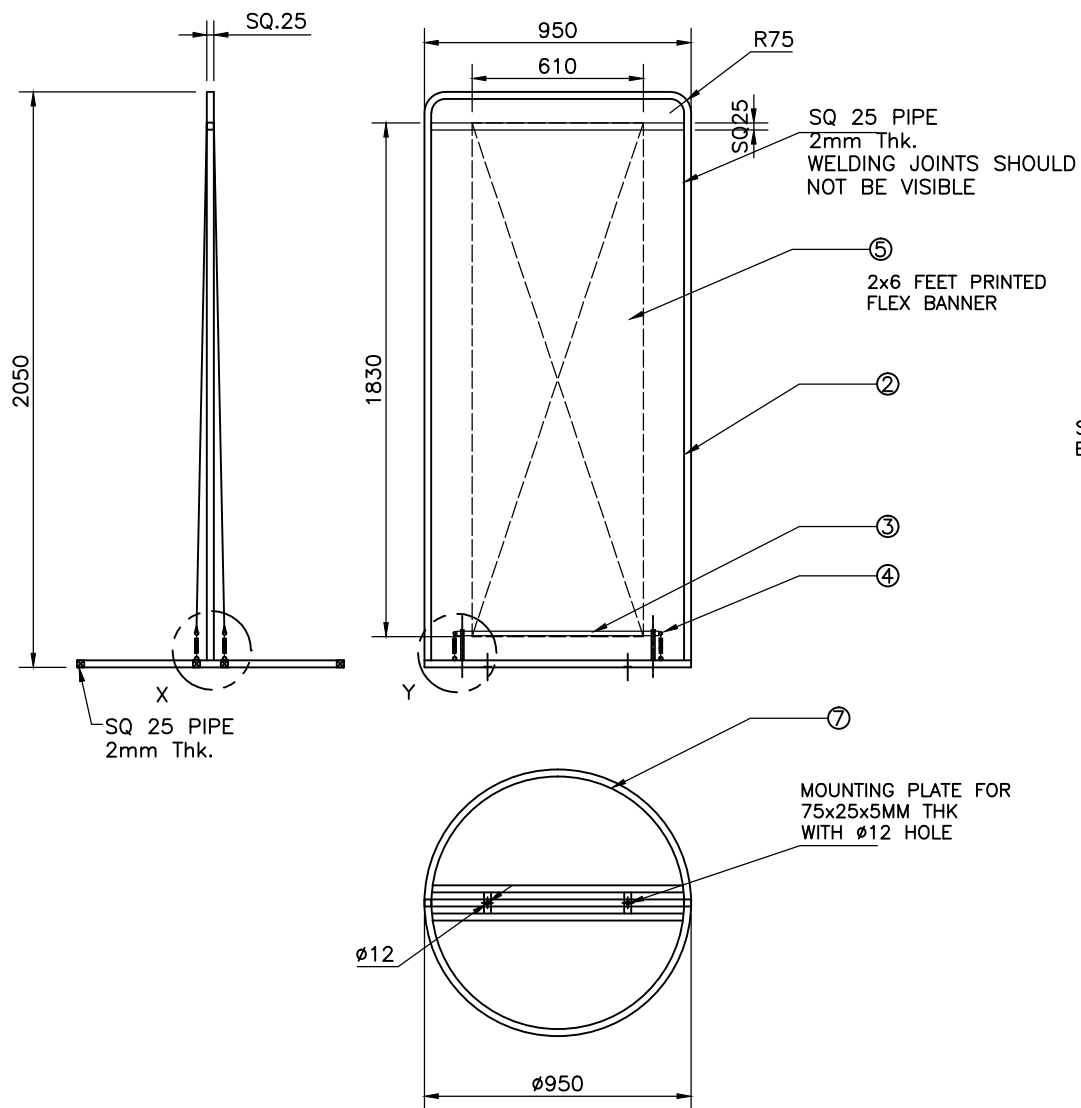

SURFACE TREATMENT-ZINC PHOSPHATE TREATED &
POWDER COATED PURE POLYESTER WHITE 50 MICRON.




BHARAT PETROLEUM CORPORATION LTD.

TITLE :

BANNER STAND FLOOR MOUNTED

REVISED 18/1/19	SCALE :	DRAWN:	CHECKED	SHEET NO. 1 of 1	DRAWING NO : BP.RVI.BF-A01
REVISION	DATE : 24/05/18	GM.RE			
7	8	9	10	11	

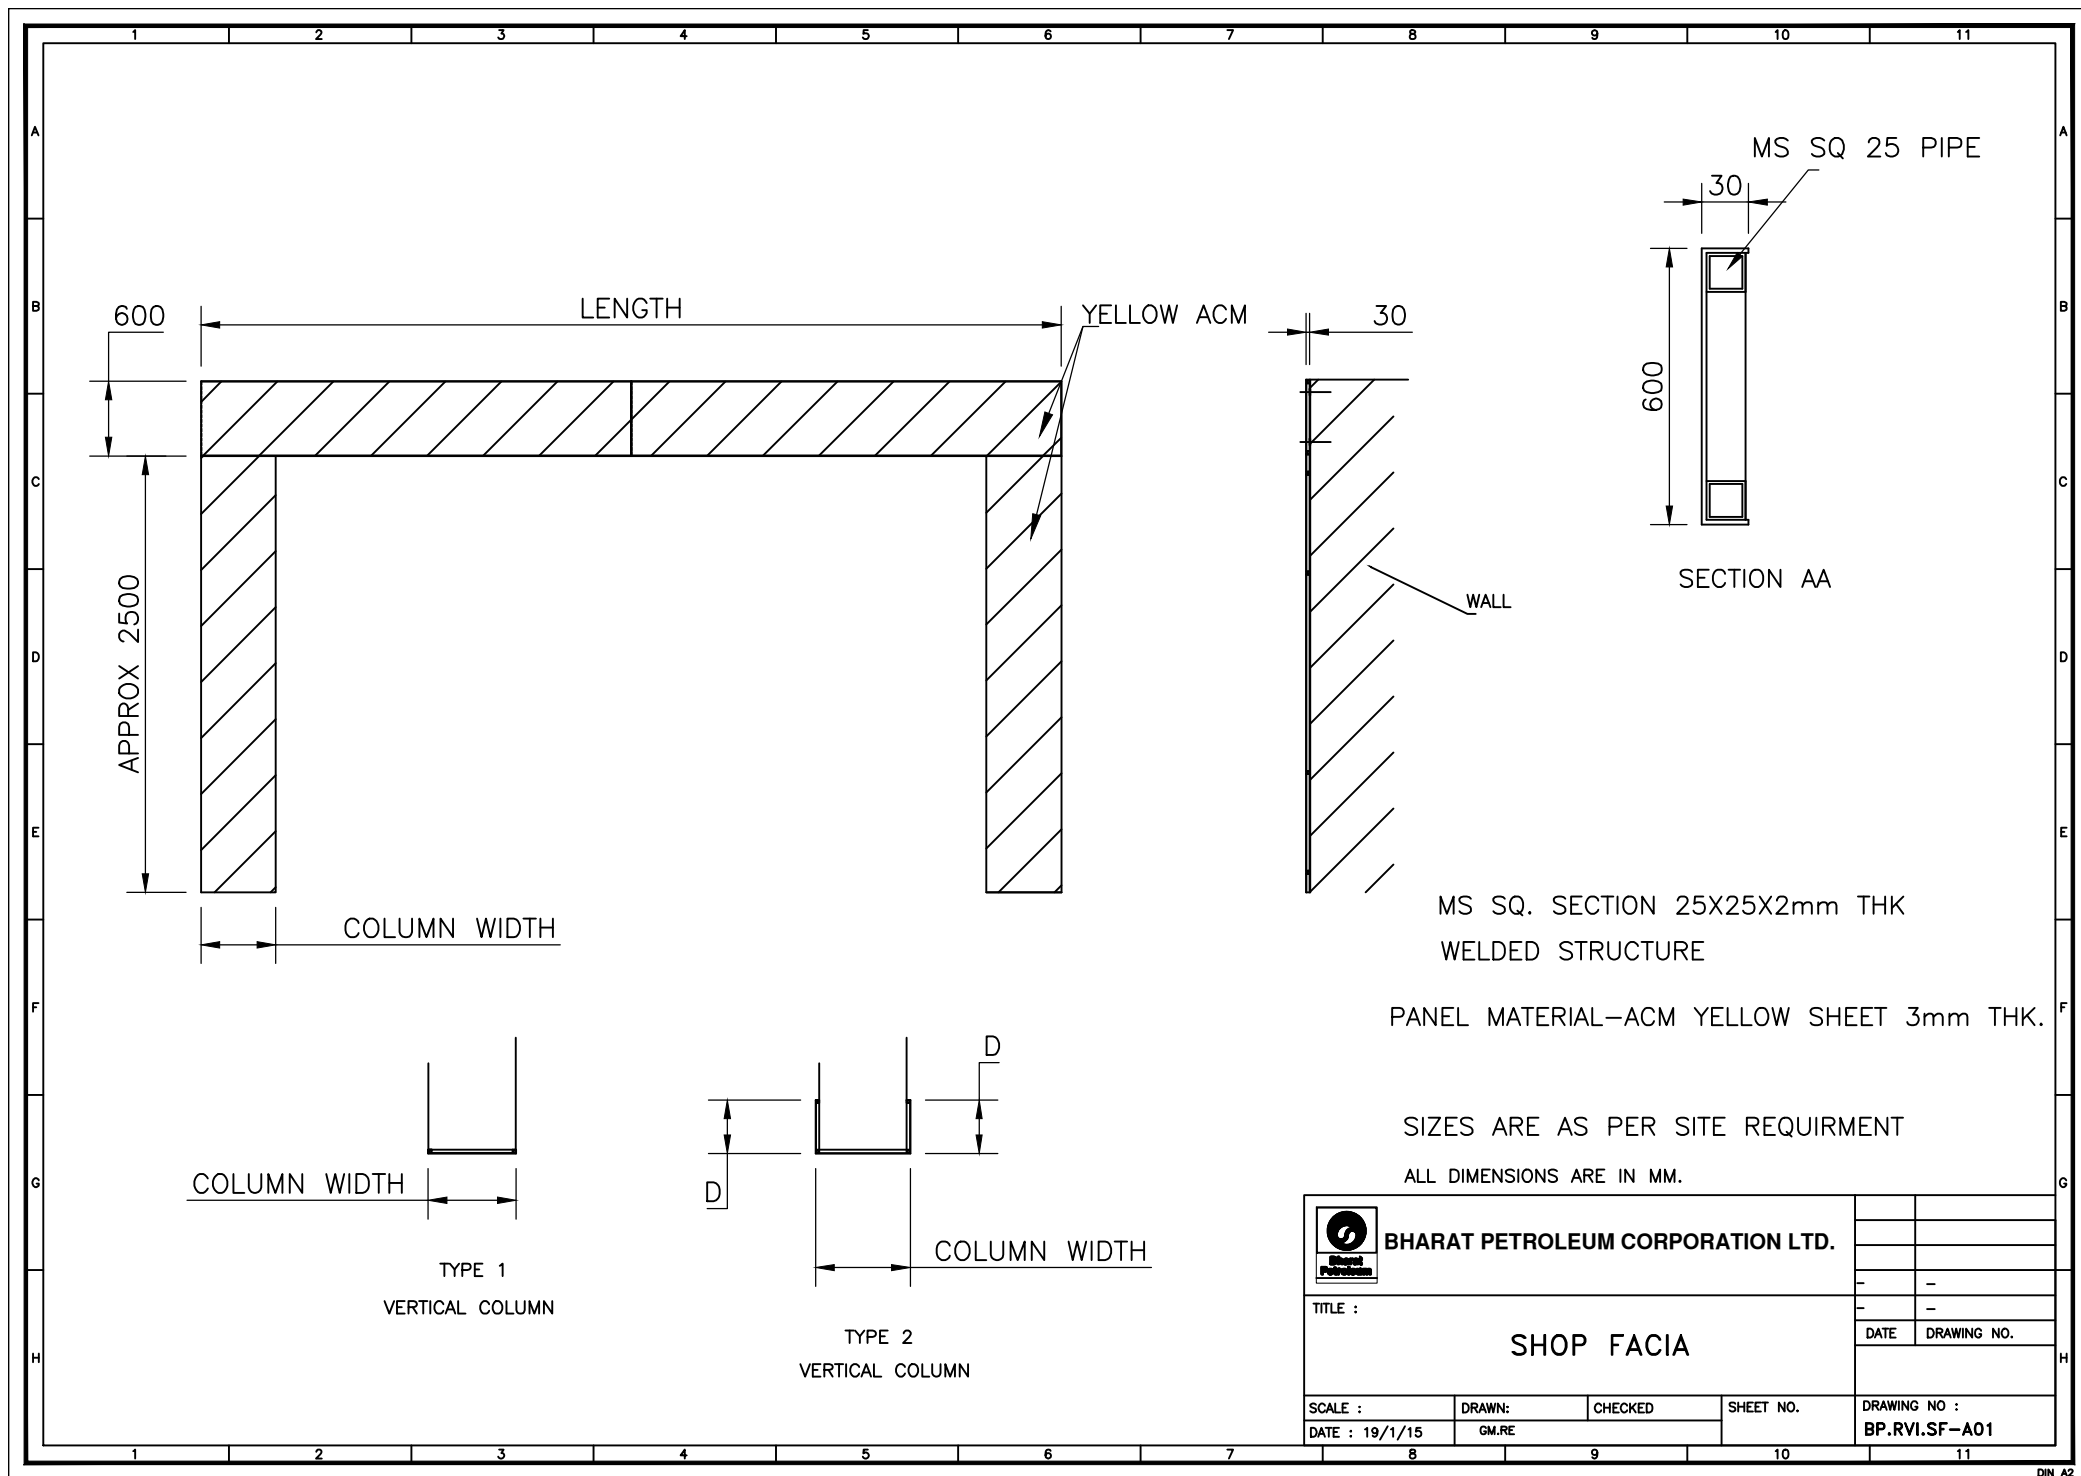

BHARAT PETROLEUM CORPORATION LTD.

TITLE :

SHOP FACIA

SCALE :

DATE : 19/1/15

DRAWN:


GM.RE

CHECKED


SHEET NO.

DRAWING NO :


BP.RVI.SF-A01

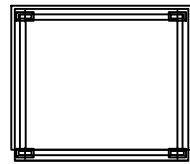


TOP VIEW

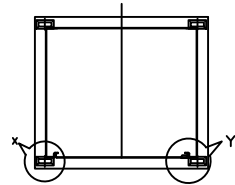


FRONT VIEW
WITHOUT DOOR

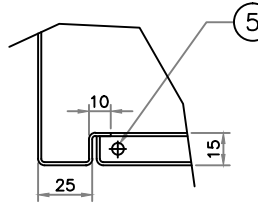


DETAIL X

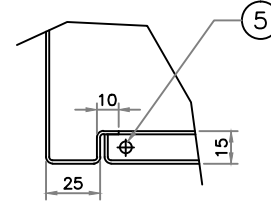


DETAIL X

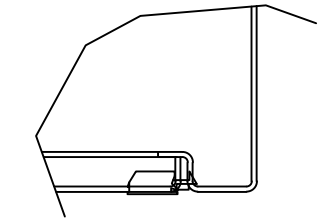


DETAIL Y
LOCKING ARRANGEMENT

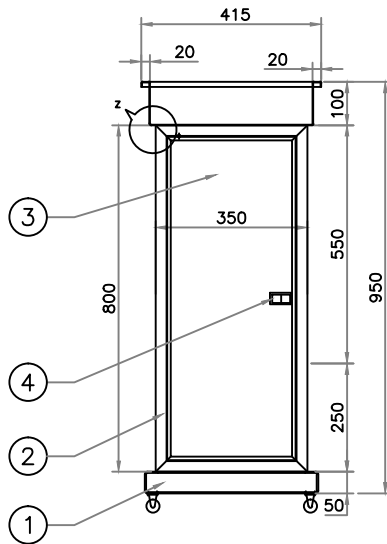


BACK VIEW
(OPERATOR SIDE)

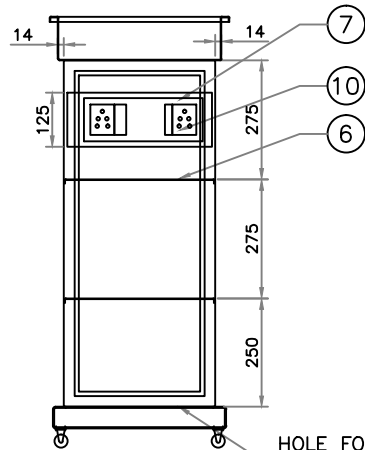

HOLE FOR
WIRE ENTRY

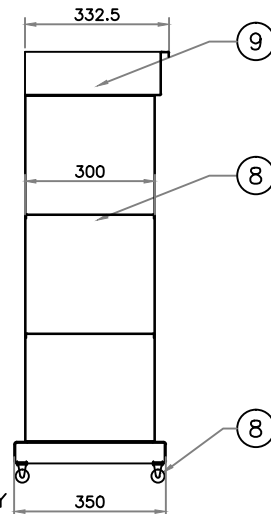


SIDE VIEW

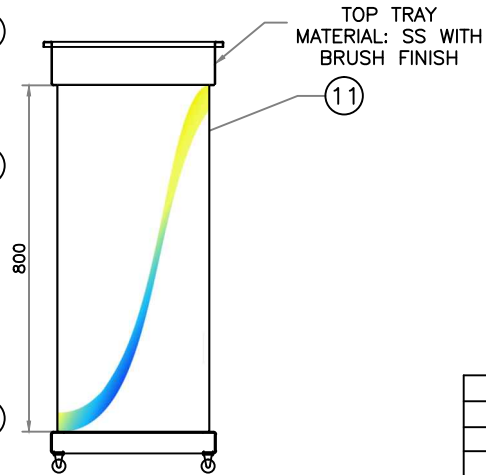

FRONT VIEW
(CUSTOMER SIDE)

11	SIGNATURE GRAPHICS	1
10	PLUG & SWITCH	2
9	TOP TRAY	1
8	WHEEL	4
7	MOUNTING PLATE FOR SWITCH BOARD	1
6	TRAY	2
5	HINGES	2
4	SLIDE LOCK	2
3	DOOR	2
2	MAIN STRUCTURE	1
1	BASE (2 mm thk)	1
SR NO	DESCRIPTION	QTY

MATERIAL—CRCA STEEL SHEET 1.5mm THK
SURFACE TREATMENT : WHITE POWDER COATING

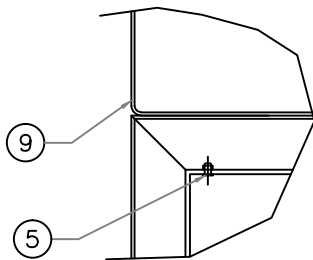

DETAIL Z



BHARAT PETROLEUM CORPORATION LTD.

TITLE :

ISLAND COUNTER UNIT

SCALE :

DATE : 26/2/19

DRAWN:

GM.RE

CHECKED




SHEET NO.

of

DRAWING NO :

BP.RVI.IRCU-A01

REVISION

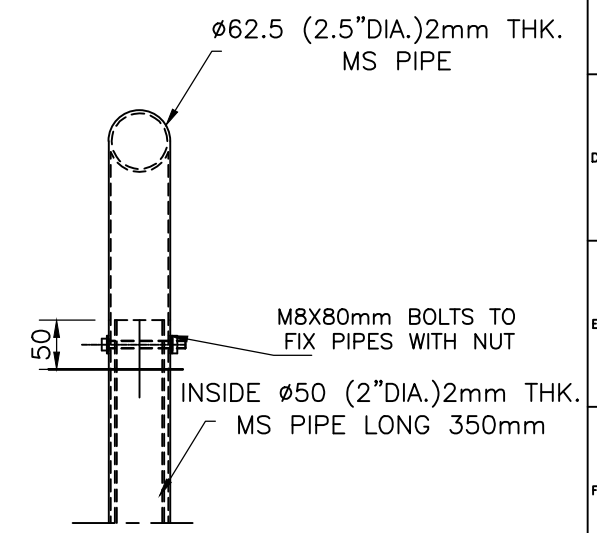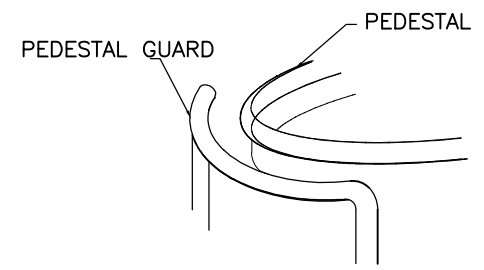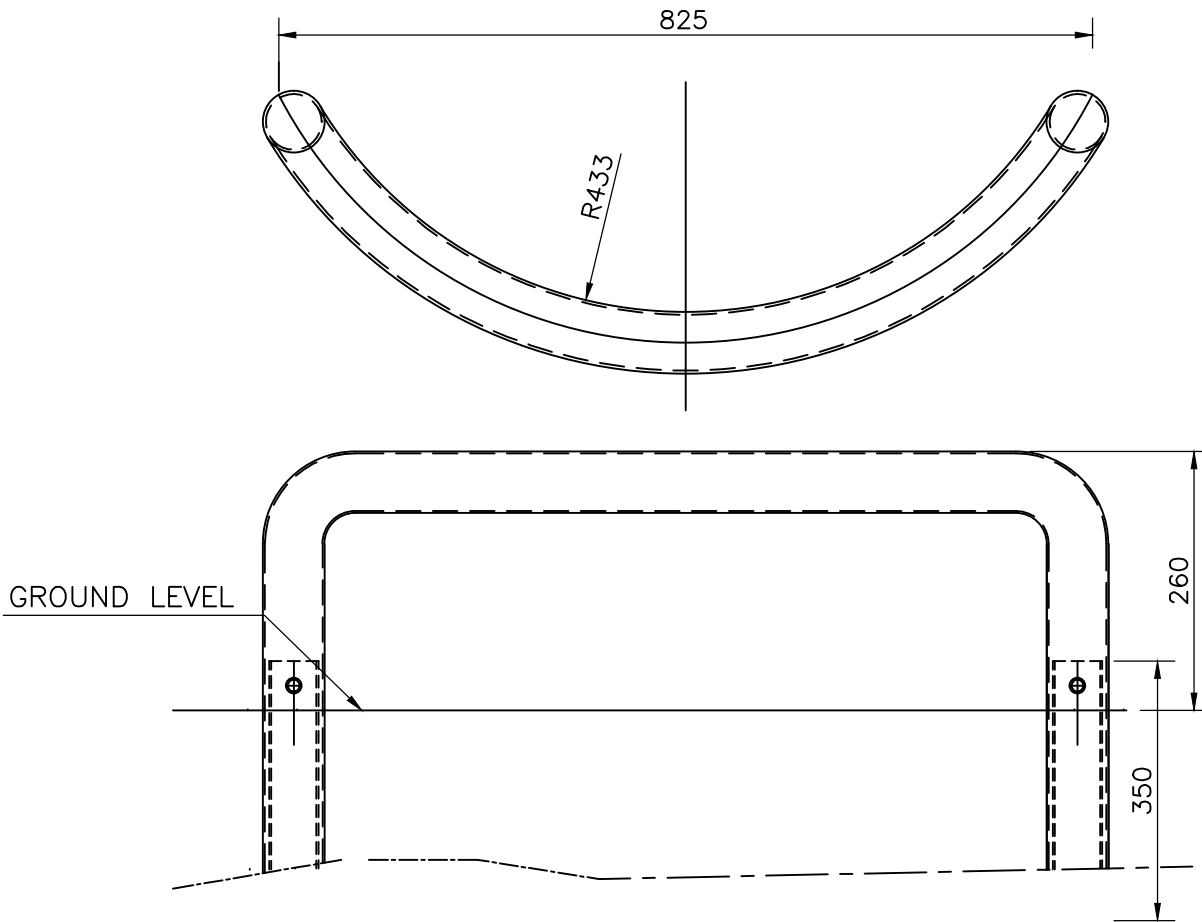

FINISH – BLUE PAINTED
ALL DIMS ARE IN mm.

NOTES – 1) TOP LEVEL OF PIPE TO MATCH
THE FINISHED LEVEL OF PEDESTAL
2) MS PIPE SECTION AS SOCKET GROUTED BELOW
THE PAVEMENT TO FIT AND HOLD
PEDESTAL GUARD

A	REVISED 11/10/18
REVISION	

 BHARAT PETROLEUM CORPORATION LTD.			
TITLE :			
ASSLY FOR PEDESTAL GUARD			
SCALE :	DRAWN:	CHECKED	SHEET NO.
DATE : 29/5/18	GM.RE.		1 of 1
		DRAWING NO. :	
		BP.RVI.PG-A01	