


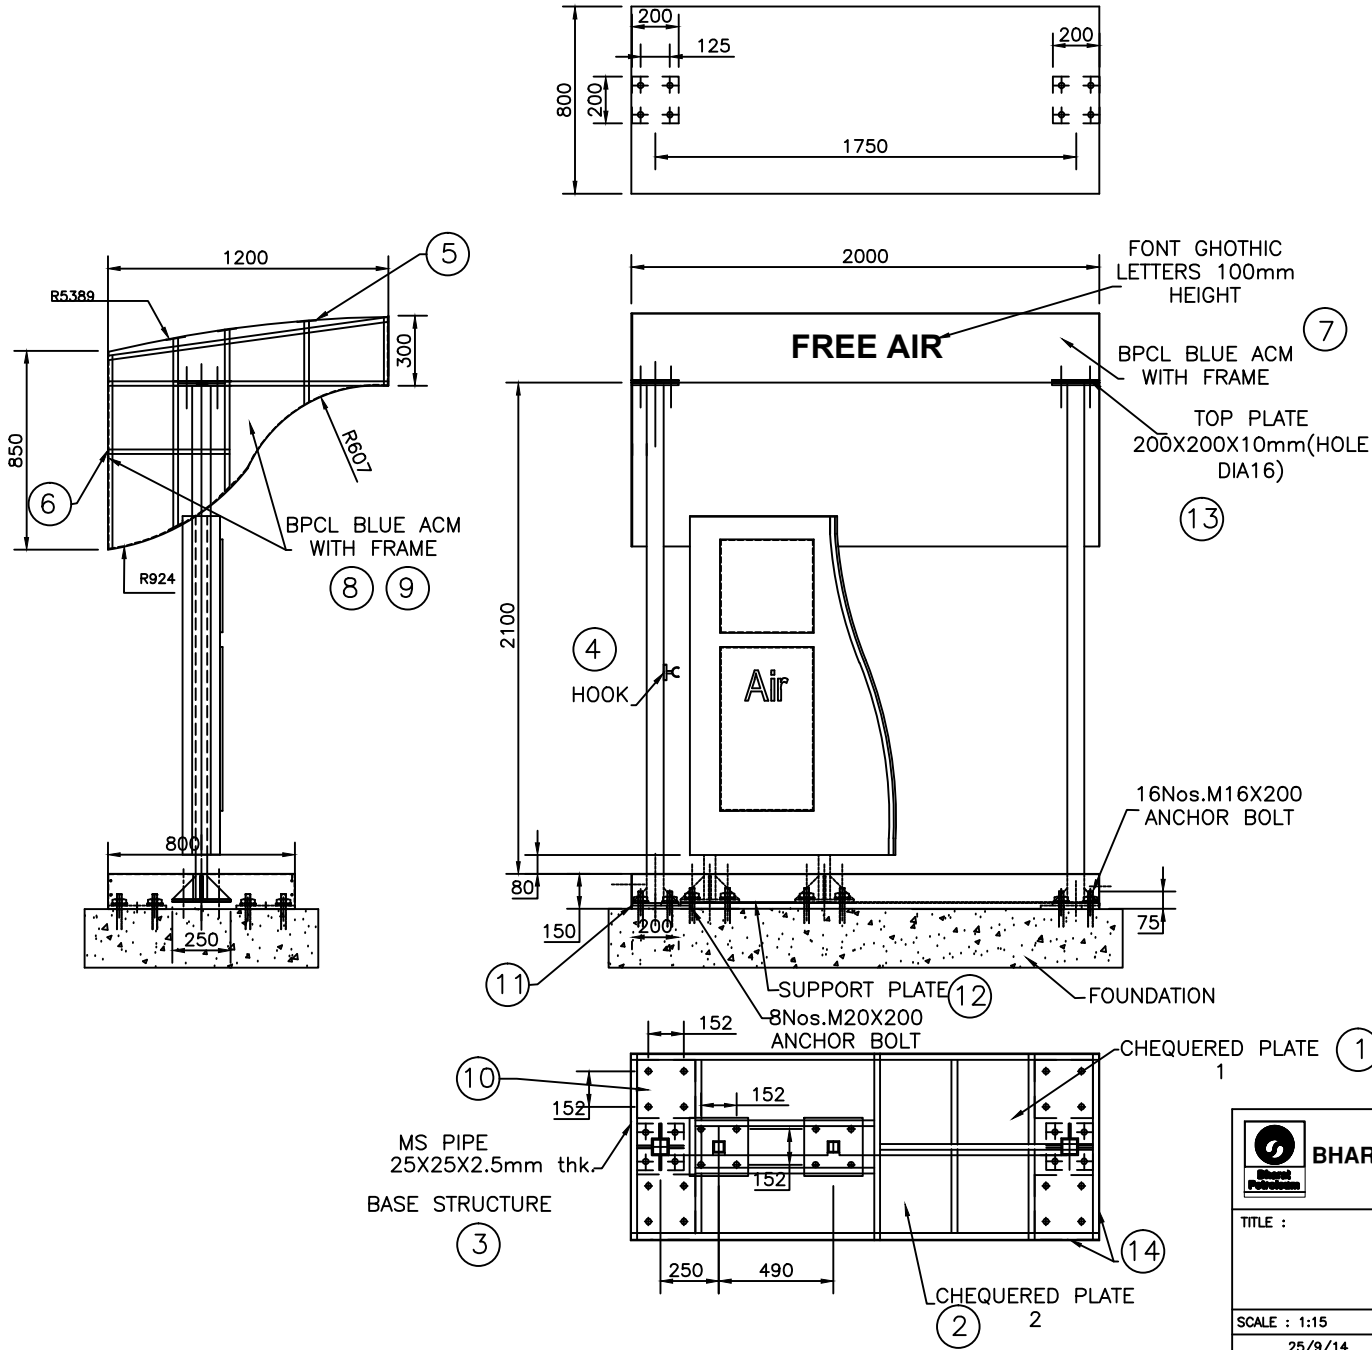

14	SIDE PLATE BASE STRUCTURE	4	MS	1.6mm thk. (2 TYPES)
13	TOP PLATE WELDED	2	MS	200X200X10mm thk.
12	SUPPORT PLATE	1	MS	2000X800X3mm thk.
11	POLE BASE PLATE	2	MS	200X200X10mm thk.
10	MOUNTING PLATE	4	MS	250X250X16mm thk.
9	TOP & SIDE STRUCTURE	1	MS PIPE	20X20X1.6mm thk.
8	SIDE ACM SHEET	2	BPCL BLUE ACM	3mm thk.
7	FRONT ACM SHEET	1	BPCL BLUE ACM	3mm thk.
6	BACK ACM SHEET	1	BPCL BLUE ACM	3mm thk.
5	ROOFING SHEET	1	GI CORRUGATED	1mm thk.
4	PIPE (WITH HOOK)	2	MS PIPE	72X72X5mm thk.
3	BASE STRUCTURE	1	MS PIPE	25X25X2.5mm thk.
2	CHEQUERED PLATE 2	1	ALUMINIUM	1.6MM THK.mm
1	CHEQUERED PLATE 1	1	ALUMINIUM	1.6MM THK.mm
Sr. No.	DESCRIPTION	QTY.	MATERIAL	SIZE

ALL DIMENSIONS
ARE IN MM.


BHARAT PETROLEUM CORPORATION LTD.

TITLE :
AIR BOY CANOPY

SCALE : 1:15	DRAWN	CHECKED	SHEET NO.	DRAWING NO :
25/9/14	GM.RE		1 of 8	BP.RVI.ASC-A01

DATE	DRAWING NO.

NUMBERS CROSSED OUT ARE
SUPERSEDED DRAWINGS