


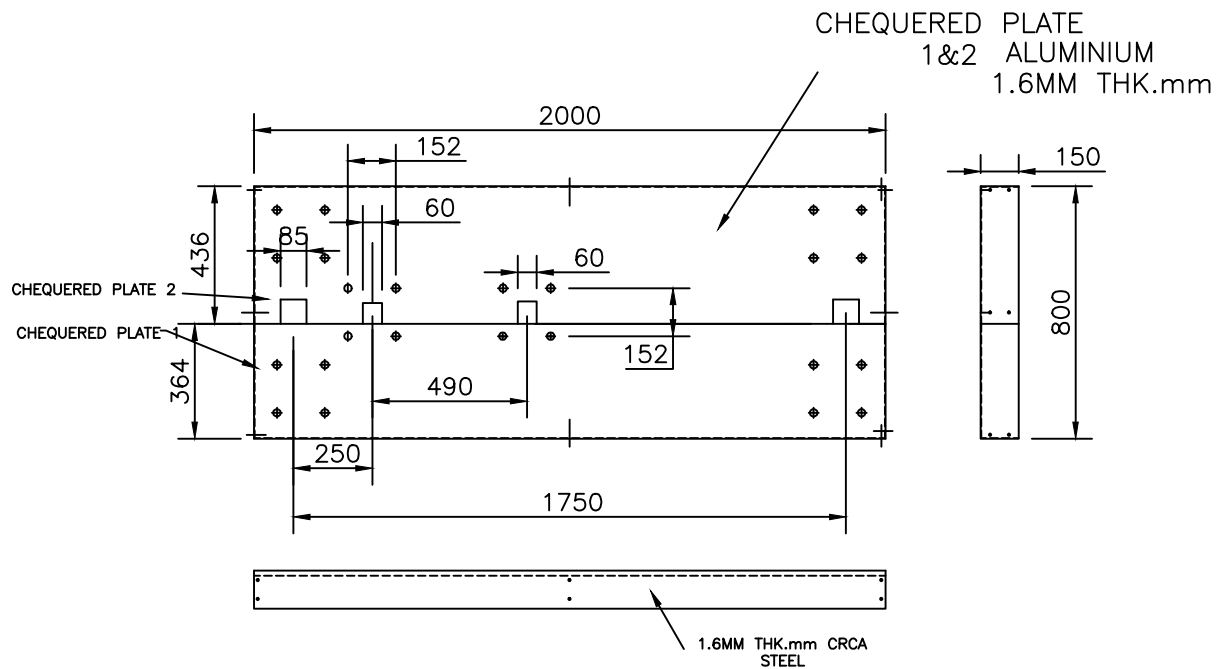

SURFACE TREATMENT—PRETREATED
& PP POWDER COATED WHITE 50
MICRON.

SIDE PLATE
BASE STRUCTURE

 BHARAT PETROLEUM CORPORATION LTD.					
TITLE :					
CHEQUERED PLATE				DATE	DRAWING NO.
				NUMBERS CROSSED OUT ARE SUPERSEDED DRAWINGS	
SCALE : 1:15	DRAWN	CHECKED	SHEET NO.	DRAWING NO :	
25/9/14	GM.RE		7 of 8	BP.RVI.ASC-P07	