

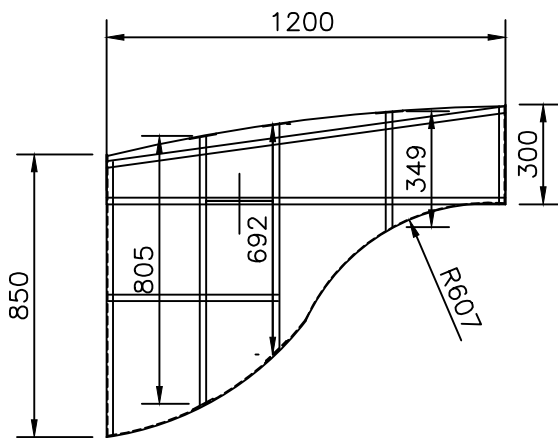


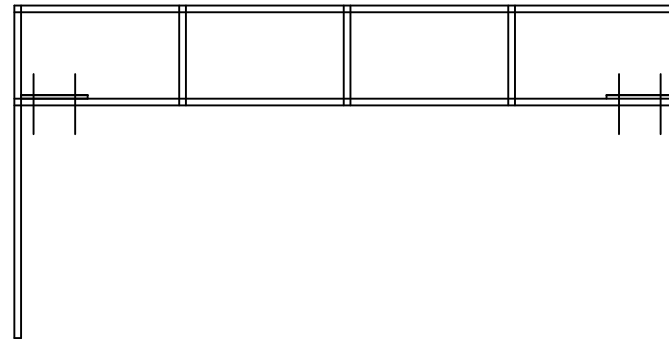

SURFACE TREATMENT—PRETREATED & PP
POWDER COATED WHITE 50 MICRON.

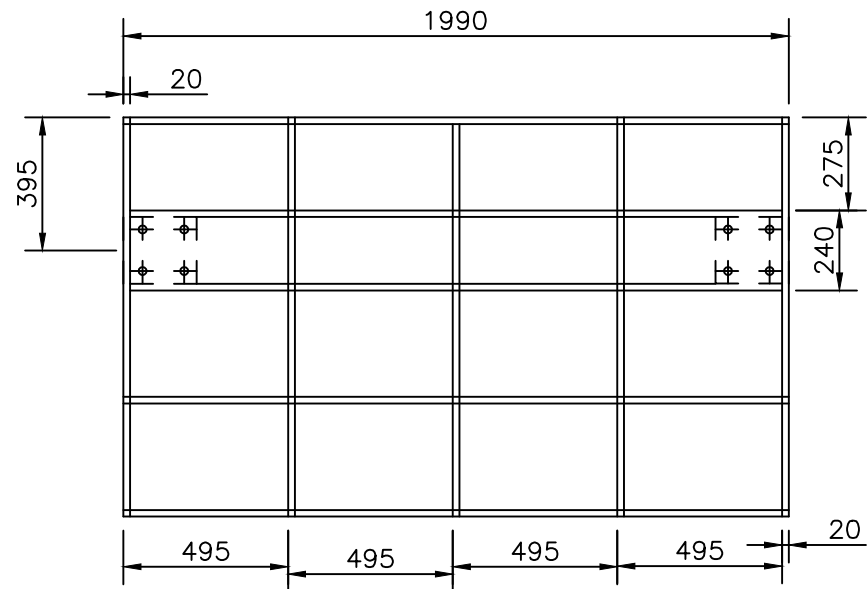

 BHARAT PETROLEUM CORPORATION LTD.			
TITLE :		DATE	
TOP & SIDE STRUCTURE AIR CANOPY		DRAWING NO.	
SCALE : 1:15		NUMBERS CROSSED OUT ARE SUPERSEDED DRAWINGS	
DRAWN		DRAWING NO :	
25/9/14		BP.RVI.ASC-P08	
CHECKED		SHEET NO.	
GM.RE		8 of 8	