


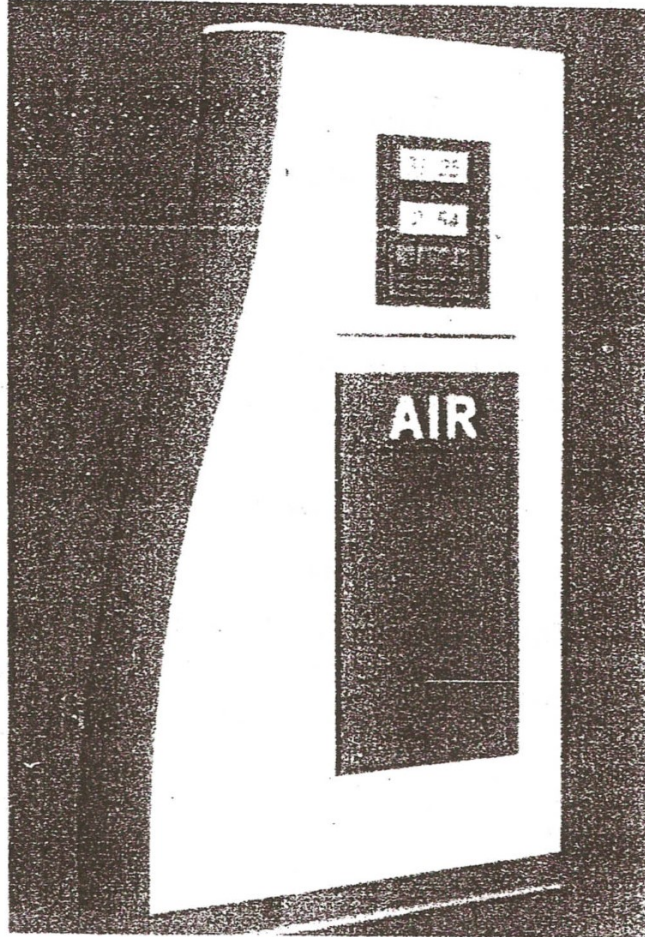


Air Sign

- Air Sign is to provide information to customers who wants to make use of the facility.
- Materials used are Aluminium 2mm thk. and FRP
- This sign is internally lit.
- Approximate dimensions are 900x160x1650(WxDxH).

DRAWING LIST FOR AIR SIGN

SL.NO	PART NAME	PART NO.
1	EXPLODED VIEW	BP-RVI-AS-A01
2	ASSY.DRG.AIR SIGN	BP-RVI-AS-A02
3	BODY FOR AIR LH	BP-RVI-AS-P03
4	BODY FOR AIR RH	BP-RVI-AS-P04
5	DISPLAY PANEL FOR AIR	BP-RVI-AS-P05
6	DISPLAY PANEL FOR AIR/SIGN METER	BP-RVI-AS-P06
7	SIDE COVER FOR AIR SIGN	BP-RVI-AS-P07
8	TUBE FRAME AIR SIGN	BP-RVI-AS-P08
9	TUBE FRAME AIR SIGN	BP-RVI-AS-P09
10	POLE FOR AIR SIGN	BP-RVI-AS-P10
11	STRUCTURE FOR AIR SIGN	BP-RVI-AS-P11
12	SUPPORT FRAME FOR AIR	BP-RVI-AS-P12
13	C CHANNEL FOR TUBE LIGHT FRAME	BP-RVI-AS-P13
14	TOP AND BOTTOM SHEET	BP-RVI-AS-P14

SR.NO	NAME OF COMPONENT	QTY
10	TOP & BOTTOM SHEET	2
9	TUBE LIGHT 2 FEET	2
8	SUPPORT FOR AIR SIGN	2
7	TUBE FRAME ASSLY	1
6	POLE ASSLY FOR AIR WATER	1
5	SIDE COVER	1
4	DISPALY PANEL FOR AIR METER	1
3	DISPALY PANEL FOR AIR WATER	2
2	BODY FOR AIR WATER SIGN RH	1
1	BODY FOR AIR WATER SIGN LH	1

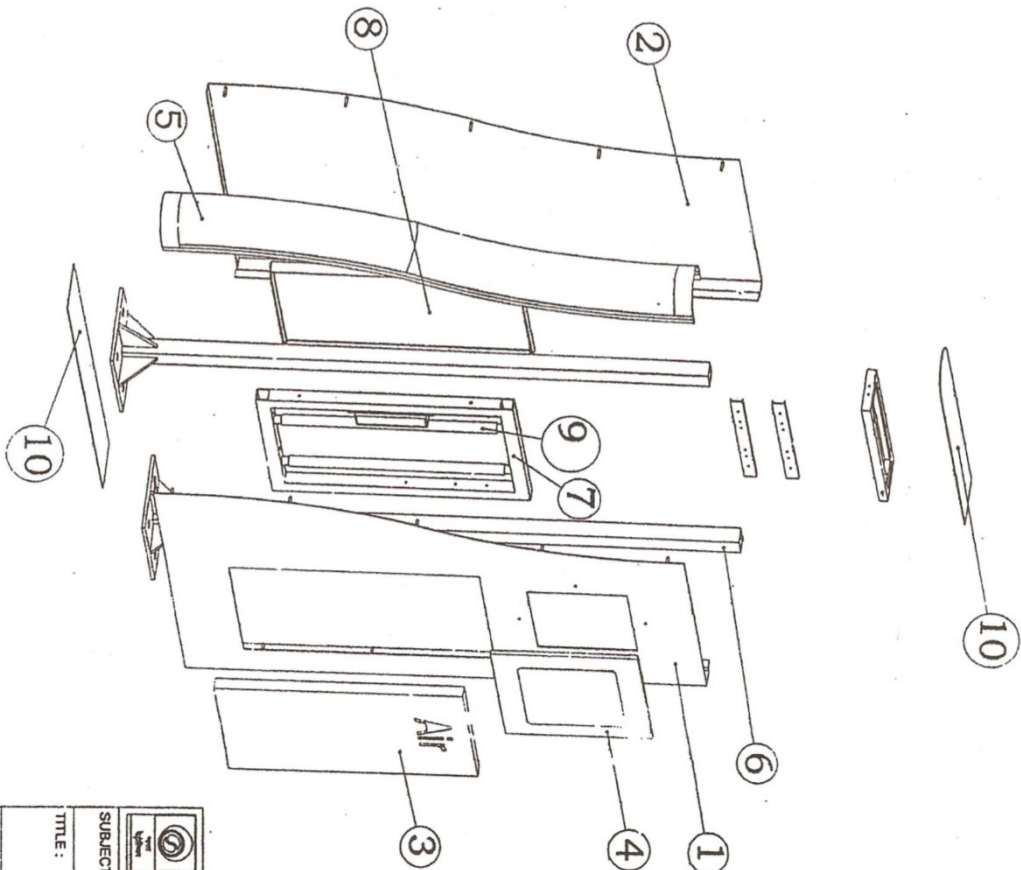


भारत पेट्रोलियम कॉर्पोरेशन लिमिटेड
BHARAT PETROLEUM CORPORATION LTD.






SUBJECT: R V M

TITLE:

AIR SIGN

SCALE: 1 : 12	DRAWN: -	THACED	CHECKED	SHEET NO: 1 OF 14	DRAWING NO. BP.RVL/AS-A01
DATE: 12/6/04	CHEF MGR. (REG) HQ				

DATE: _____
 DRAWING NO. _____
 NUMBER CROSS OUT
 AND SUPERSEDED
 DRAWINGS

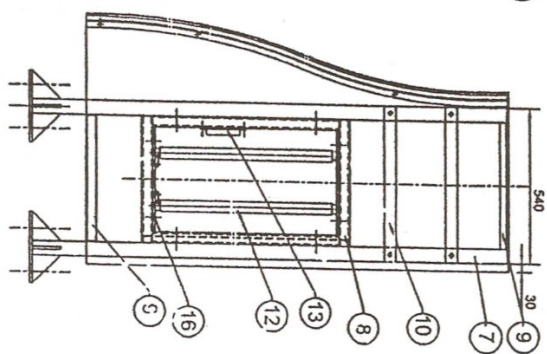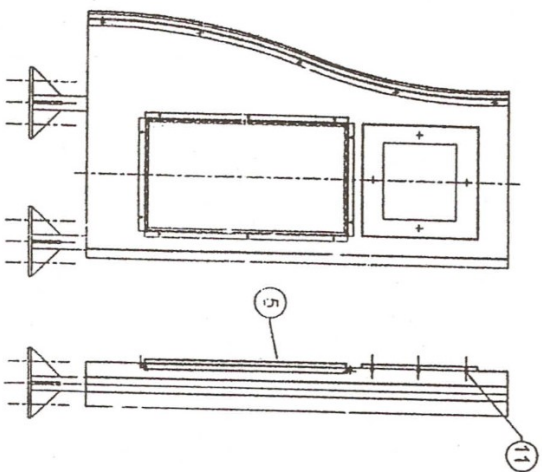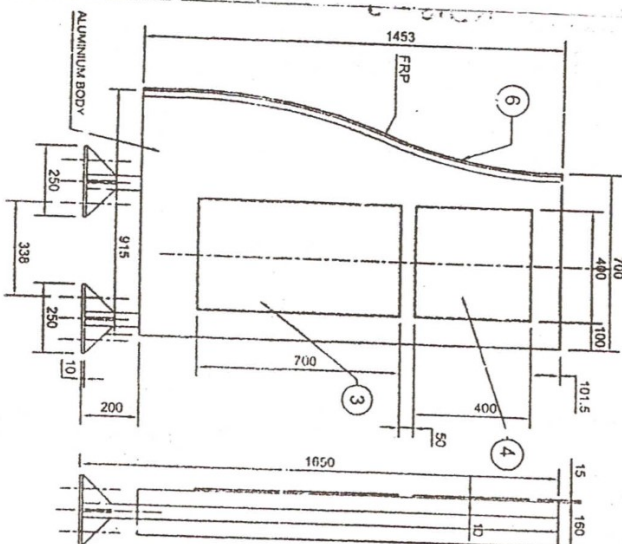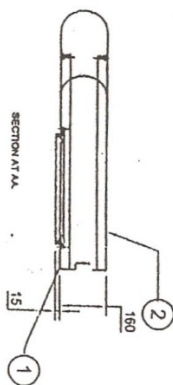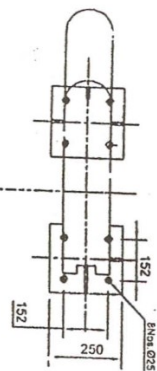

S.NO	DESCRIPTION	QTY
1	C CHANNEL	2
2	CONNECTOR	1
3	BALAST ELECTRONIC UNIT	1
4	PHILLIPS WAVE	1
5	TUBE LIGHT SHEET	2
6	MS STUD	20
7	MS PLAT 3X55mm	2
8	SUPPORT FOR AIR SIGN	2
9	TUBE FRAME ASSEMBLY	1
10	POLE ASSEMBLY FOR AIR SIGN	1
11	SIDE COVER (FRP)	1
12	Z CHANNEL FOR AIR SIGN	1
13	DISPLAY PANEL FOR AIR METER	1
14	DISPLAY PANEL FOR AIR METER	2
15	BODY FOR AIR METER SIGN IN	1
16	BODY FOR AIR METER SIGN IN	1

भारत पेट्रोलियम कॉर्पोरेशन लिमिटेड
BHARAT PETROLEUM CORPORATION LTD.


SUBJECT: R V M


TITLE:

AIR SIGN

SCALE:	DRAWN	TRACED	CHECKED
DATE: 12/6/04	CHIEF MGR. (RE) HQ		SHEET NO. 2 of 14

DATE	DRAWING NO.
	NUMBERS CROSSED OUT ARE SUPERSEDED DRAWINGS
	DRAWING NO.
	BP.RVI.AS-A02

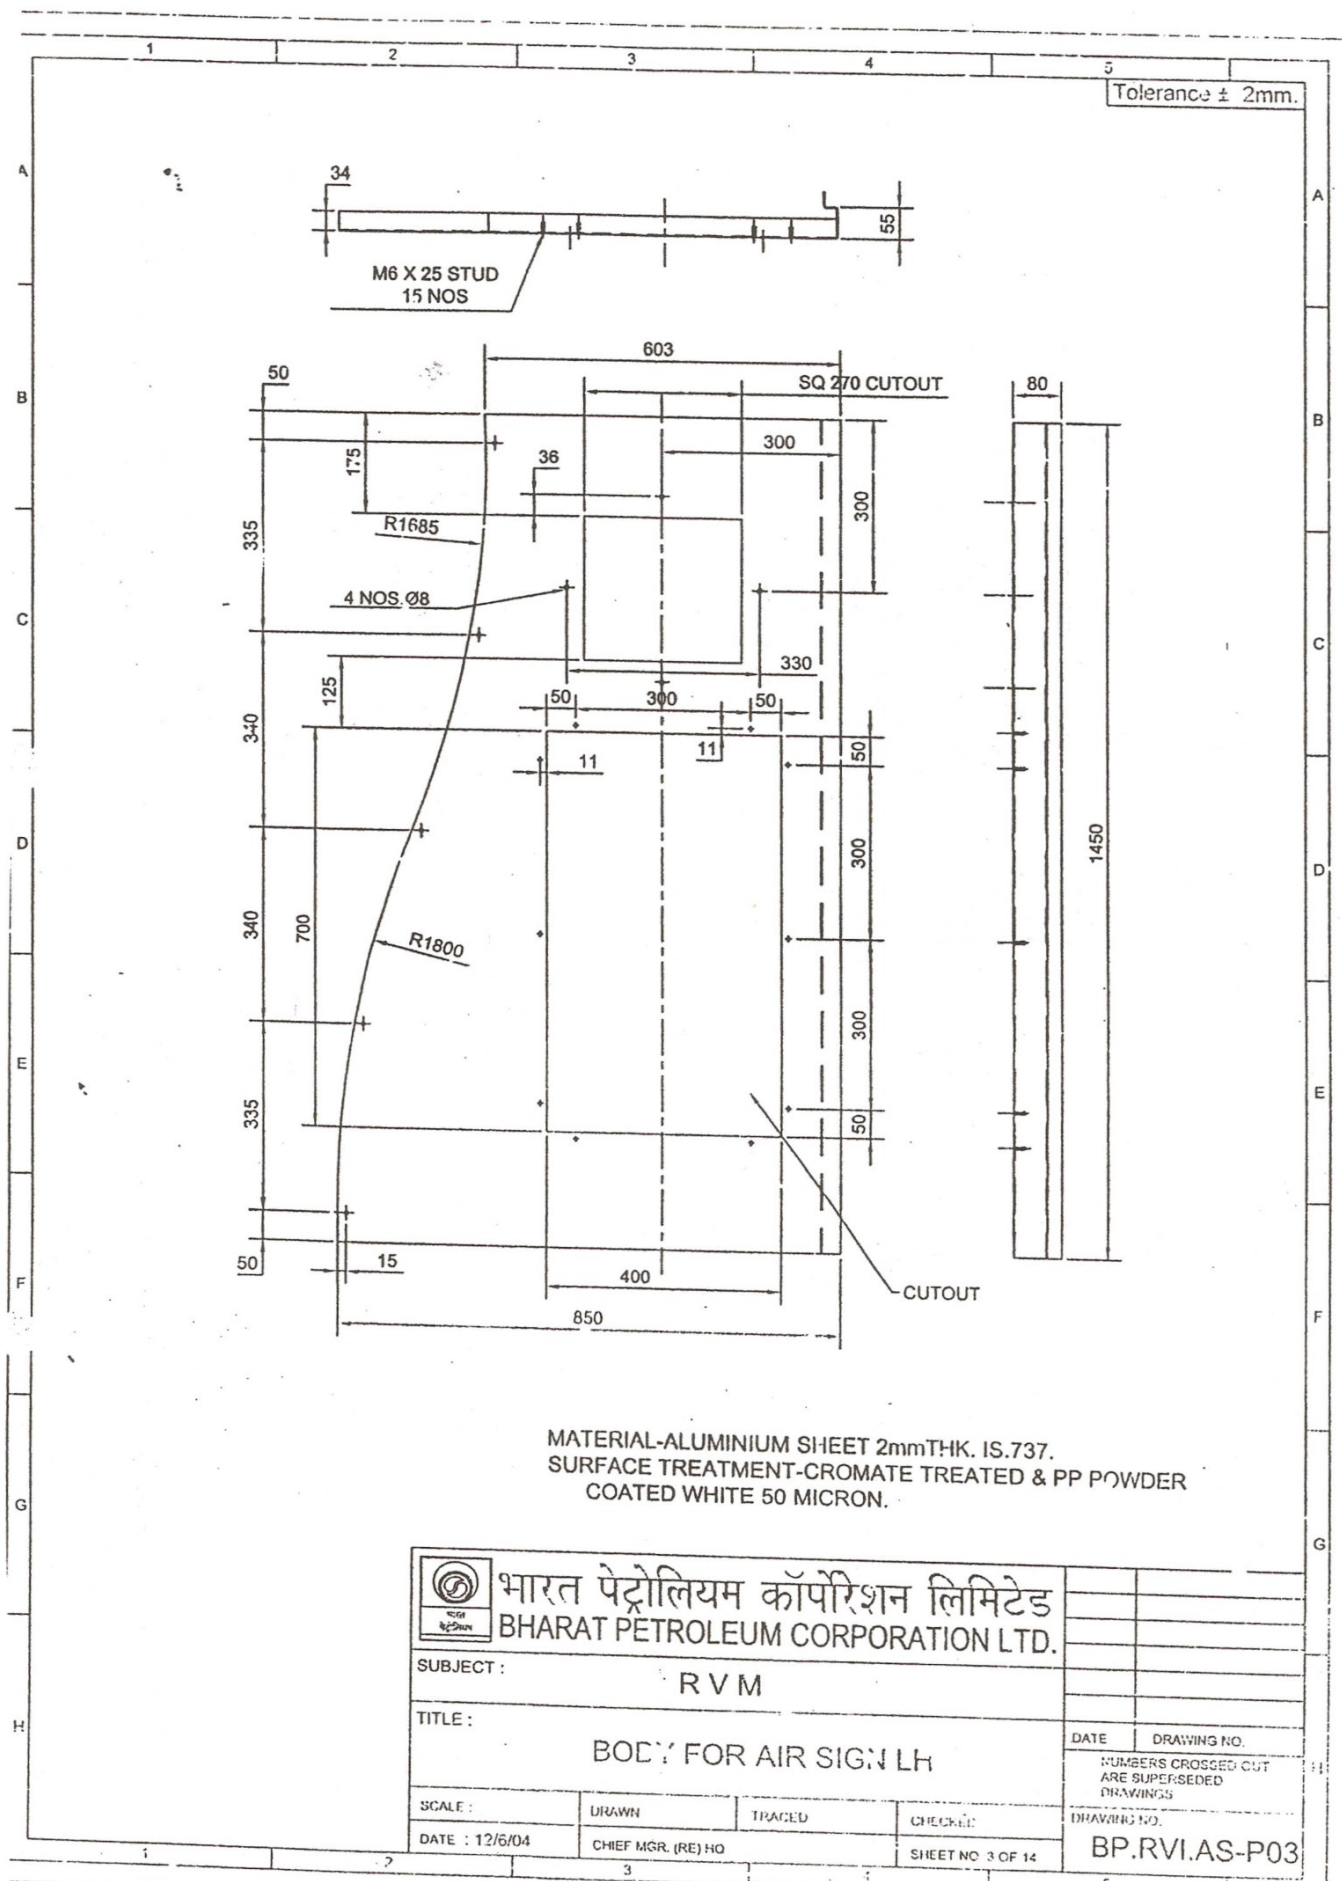

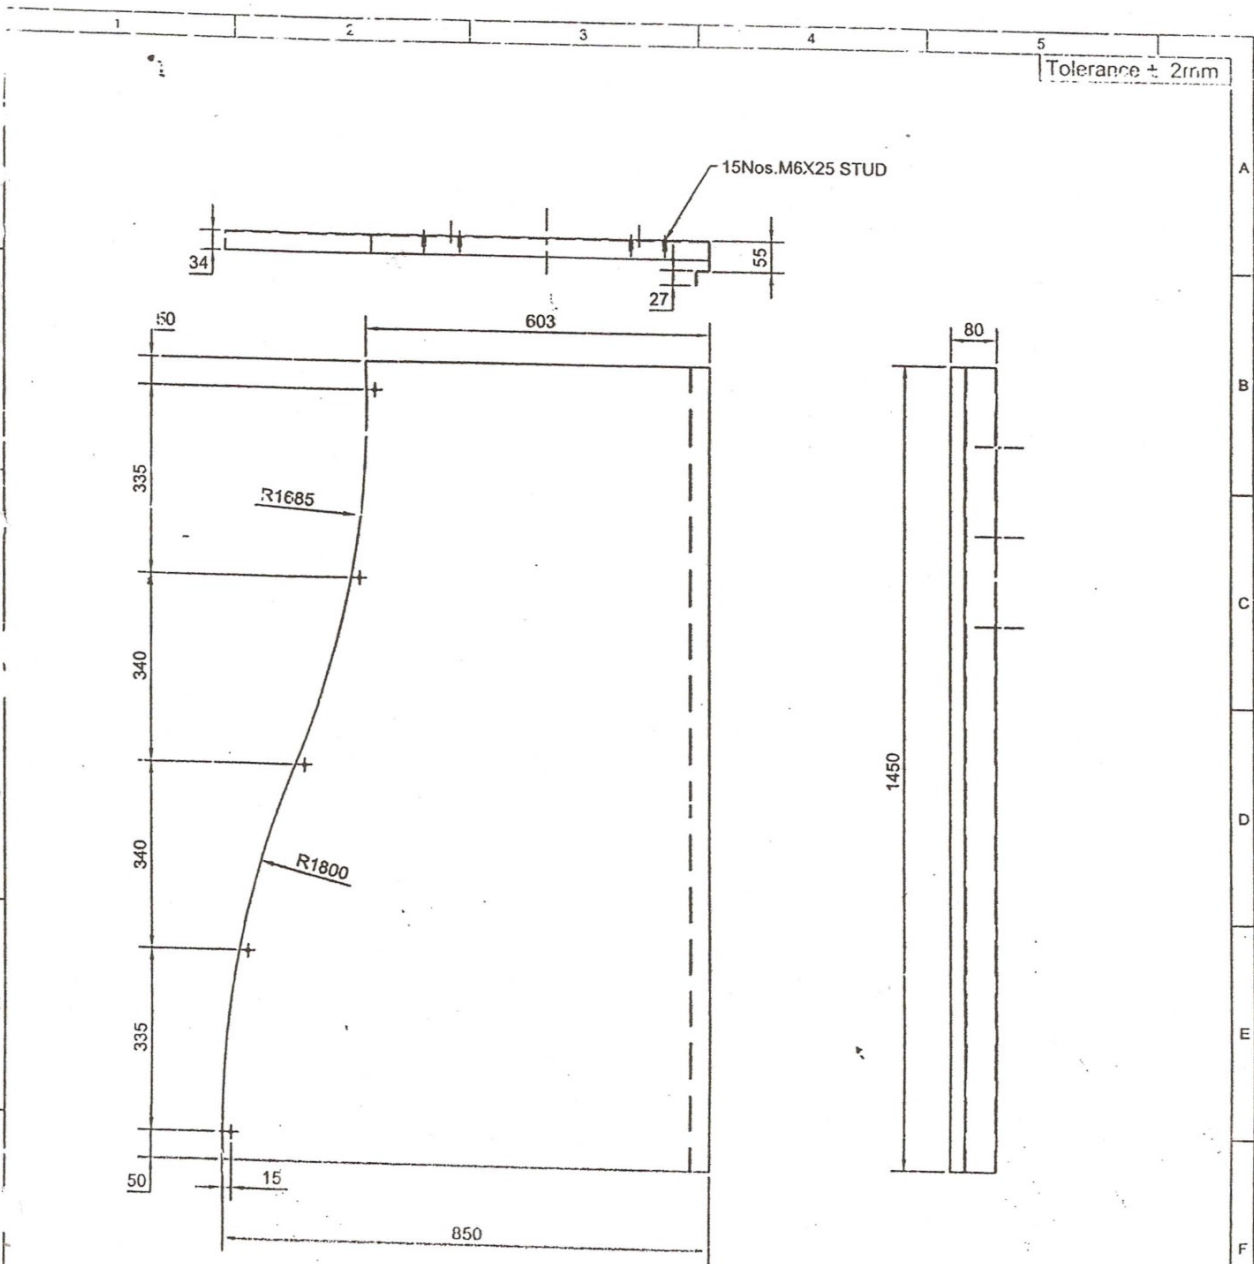


MATERIAL-ALUMINIUM SHEET 2mmTHK. IS:737.
SURFACE TREATMENT-CROMATE TREATED & PP POWDER
COATED WHITE 50 MICRON.

 भारत पेट्रोलियम कॉर्पोरेशन लिमिटेड BHARAT PETROLEUM CORPORATION LTD.			
SUBJECT : R V M			
TITLE : BODY FOR AIR SIGN RH			
SCALE :	DRAWN	TRACED	CHECKED
DATE : 12/6/04	CHIEF MGR. (RE) HQ	SHEET NO. 4 OF 14	
		DRAWING NO. BP.RVI.AS-P04	

25

1 2 3 4 5					Tolerance: $\pm 2\text{mm}$	
Air (184) TYRE PRESSURE CHART IN PRINTED VINYL STUCK HERE. TEXT FONT-ARIAL REGULAR BACKLIT WITH PET-G 3mm thk.OPAL.					35	
MATERIAL:ALUMINIUM SHEET 2mm thk.IS:737. SURFACE TREATMENT-CROMATE TREATED &PAINTED IN PU BPCL BLUE.						
भारत पेट्रोलियम कॉर्पोरेशन लिमिटेड BHARAT PETROLEUM CORPORATION LTD.						
SUBJECT : R V M						
TITLE : DISPLAY PANEL FOR AIR (AL)					DATE DRAWING NO.	
SCALE : DRAWN TRACED CHECKED					NUMBERS CROSSED OUT ARE SUPERSEDED DRAWINGS	
DATE : 12/6/04		CHIEF MGR. (RE) HQ		SHEET NO :5 OF 14		
					DRAWING NO. BP.RVI.AS-P05	


25

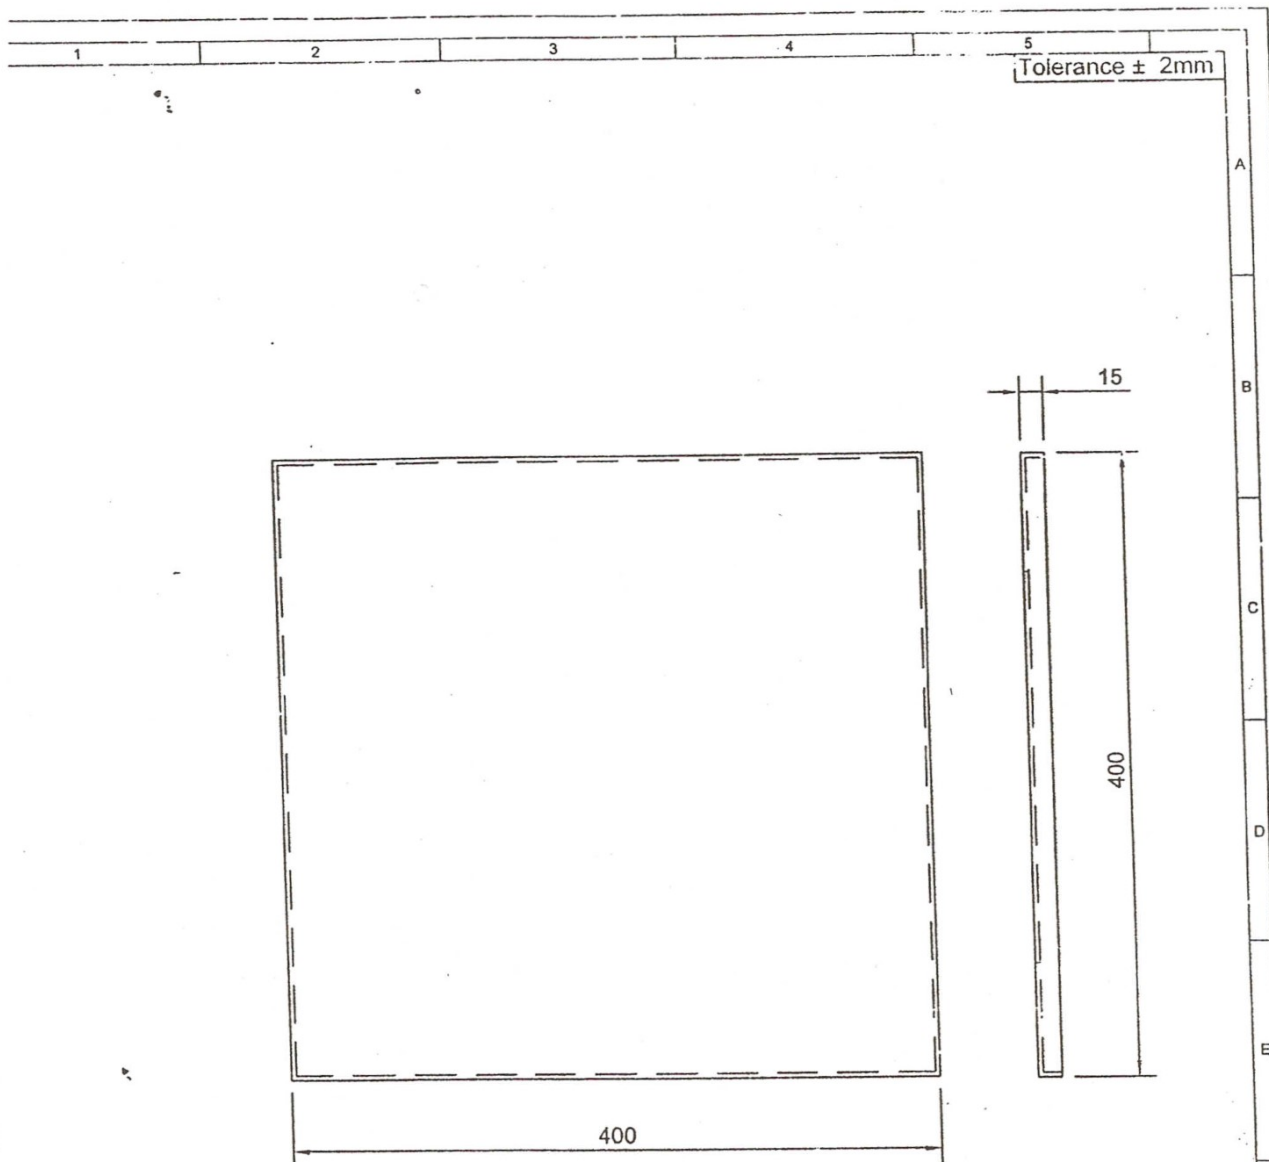

MATERIAL-ALUMINIUM SHEET 2mmTHK. IS:737.
SURFACE TREATMENT-CROMATE TREATED & PU PAINTED
IN BPCL BLUE.


 भारत पेट्रोलियम कॉर्पोरेशन लिमिटेड BHARAT PETROLEUM CORPORATION LTD.			
SUBJECT :		R V M	
TITLE :		DISPLAY PANEL FOR AIR SIGN METER	
SCALE :	DRAWN	TRACED	CHECKED
DATE : 12/6/04	CHIEF MGR. (RE) HQ	SHEET NO : 6 OF 14	
		DATE	DRAWING NO.
		MEMBERS CROSSED OUT ARE SUPERSEDED DRAWINGS	
		DRAWING NO. BP.RVI.AS-P06	

27

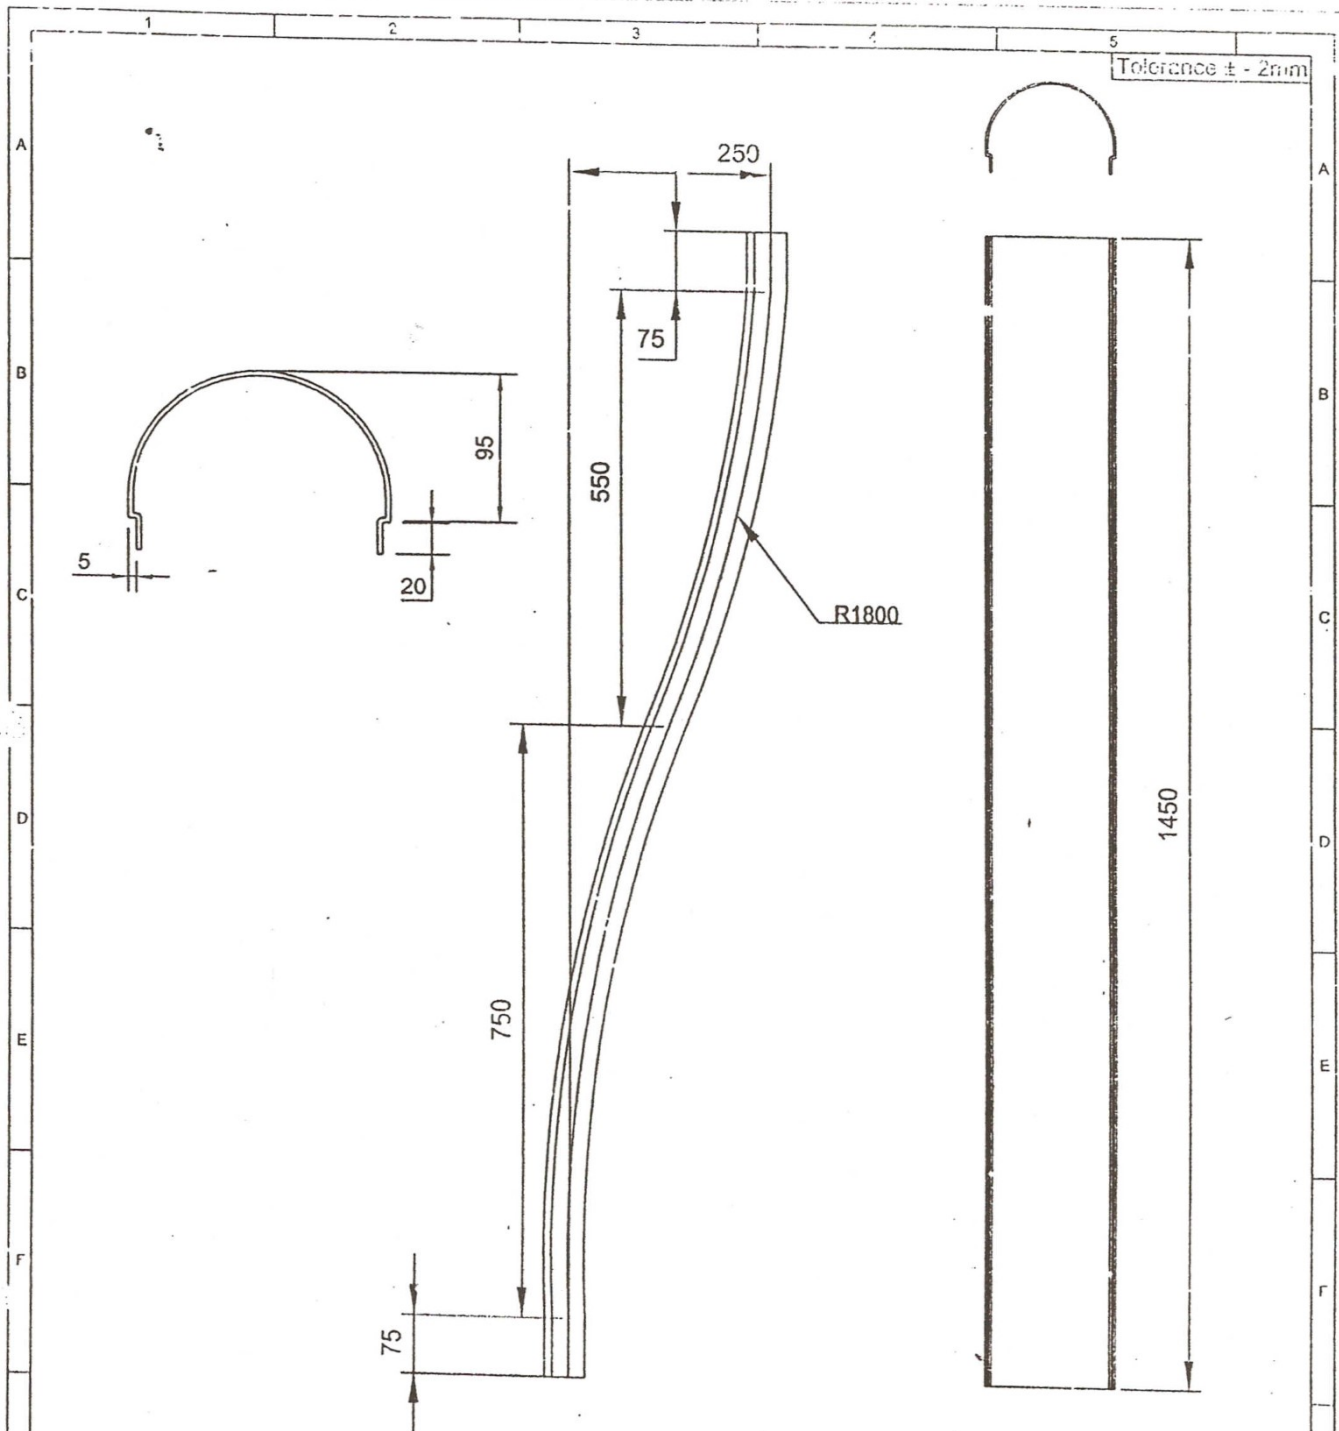


MATERIAL-FRP 3mmTHK.ADD RIBS AS REQD. TO MAINTAIN PROFILE
PAINT- PU. BPCL BLUE PAINTED 50 micron. OUTSIDE ONLY.


		भारत पेट्रोलियम कॉर्पोरेशन लिमिटेड BHARAT PETROLEUM CORPORATION LTD.			
SUBJECT : R V M					
TITLE : SIDE COVER FOR AIR SIGN				DATE _____ DRAWING NO. _____	
				NUMBERS CROSSED OUT ARE SUPERSEDED DRAWINGS	
SCALE :	DRAWN	TRACED	CHECKED	DRAWING NO.	
DATE : 12/6/04	CHIEF MGR. (RE) HQ		SHEET NO : 7 OF 14	BP.RVI.AS-P07	


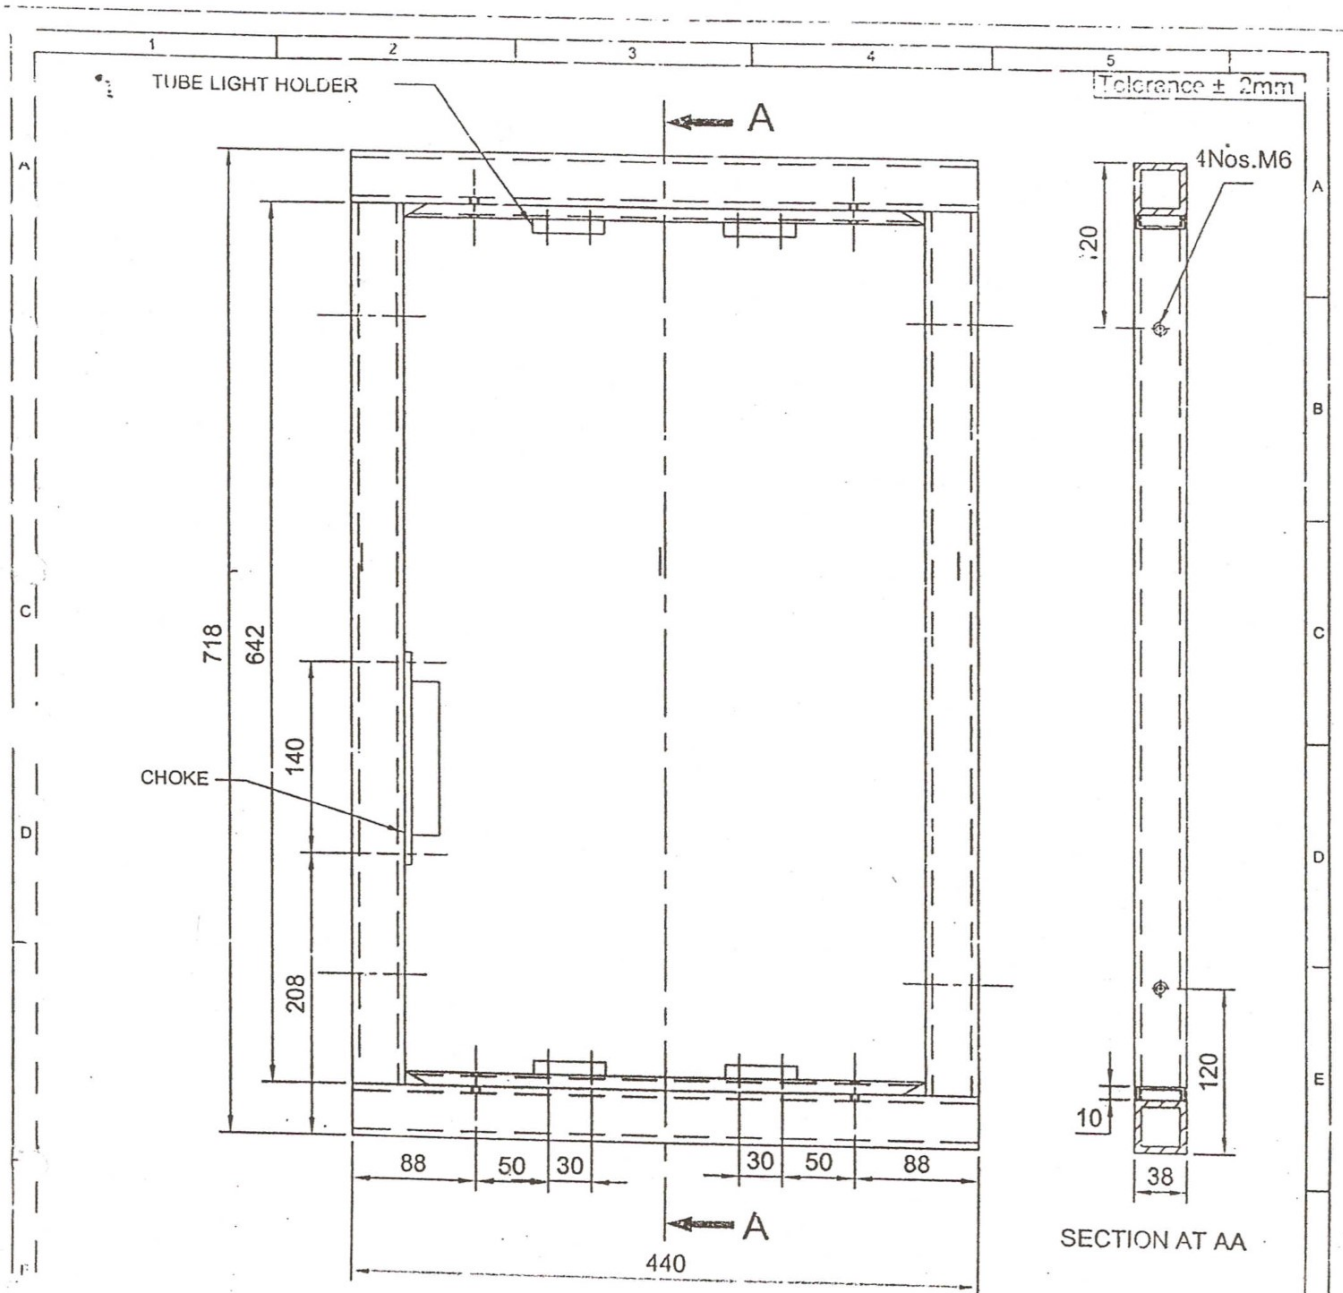


MATERIAL-ALUMINIUM SQ. 38X38X2.5 mm THK.
 ALUMINIUM C CHANNEL 35X10X1.5mm THK.
 SQ.38X38X2.5= LENGTH 440 QTY 2
 LENGTH 622 QTY 2
 'C' CHANNEL=LENGTH 366mm QTY 2

 भारत पेट्रोलियम कॉर्पोरेशन लिमिटेड BHARAT PETROLEUM CORPORATION LTD.			
SUBJECT:		R V M	
TITLE:		TUBE FRAME ASSY AIR SIGN	
SCALE:	DRAWN	TRACED	CHECKED
DATE : 12/6/04	CHIEF MGR. (PS) HQ		SHEET NO. 10 OF 14
		DATE	DRAWING NO.
		NUMBERS CROSSED OUT ARE SUPERSEDED DRAWINGS	
		DRAWING NO. BP.RVI.AS-P08	

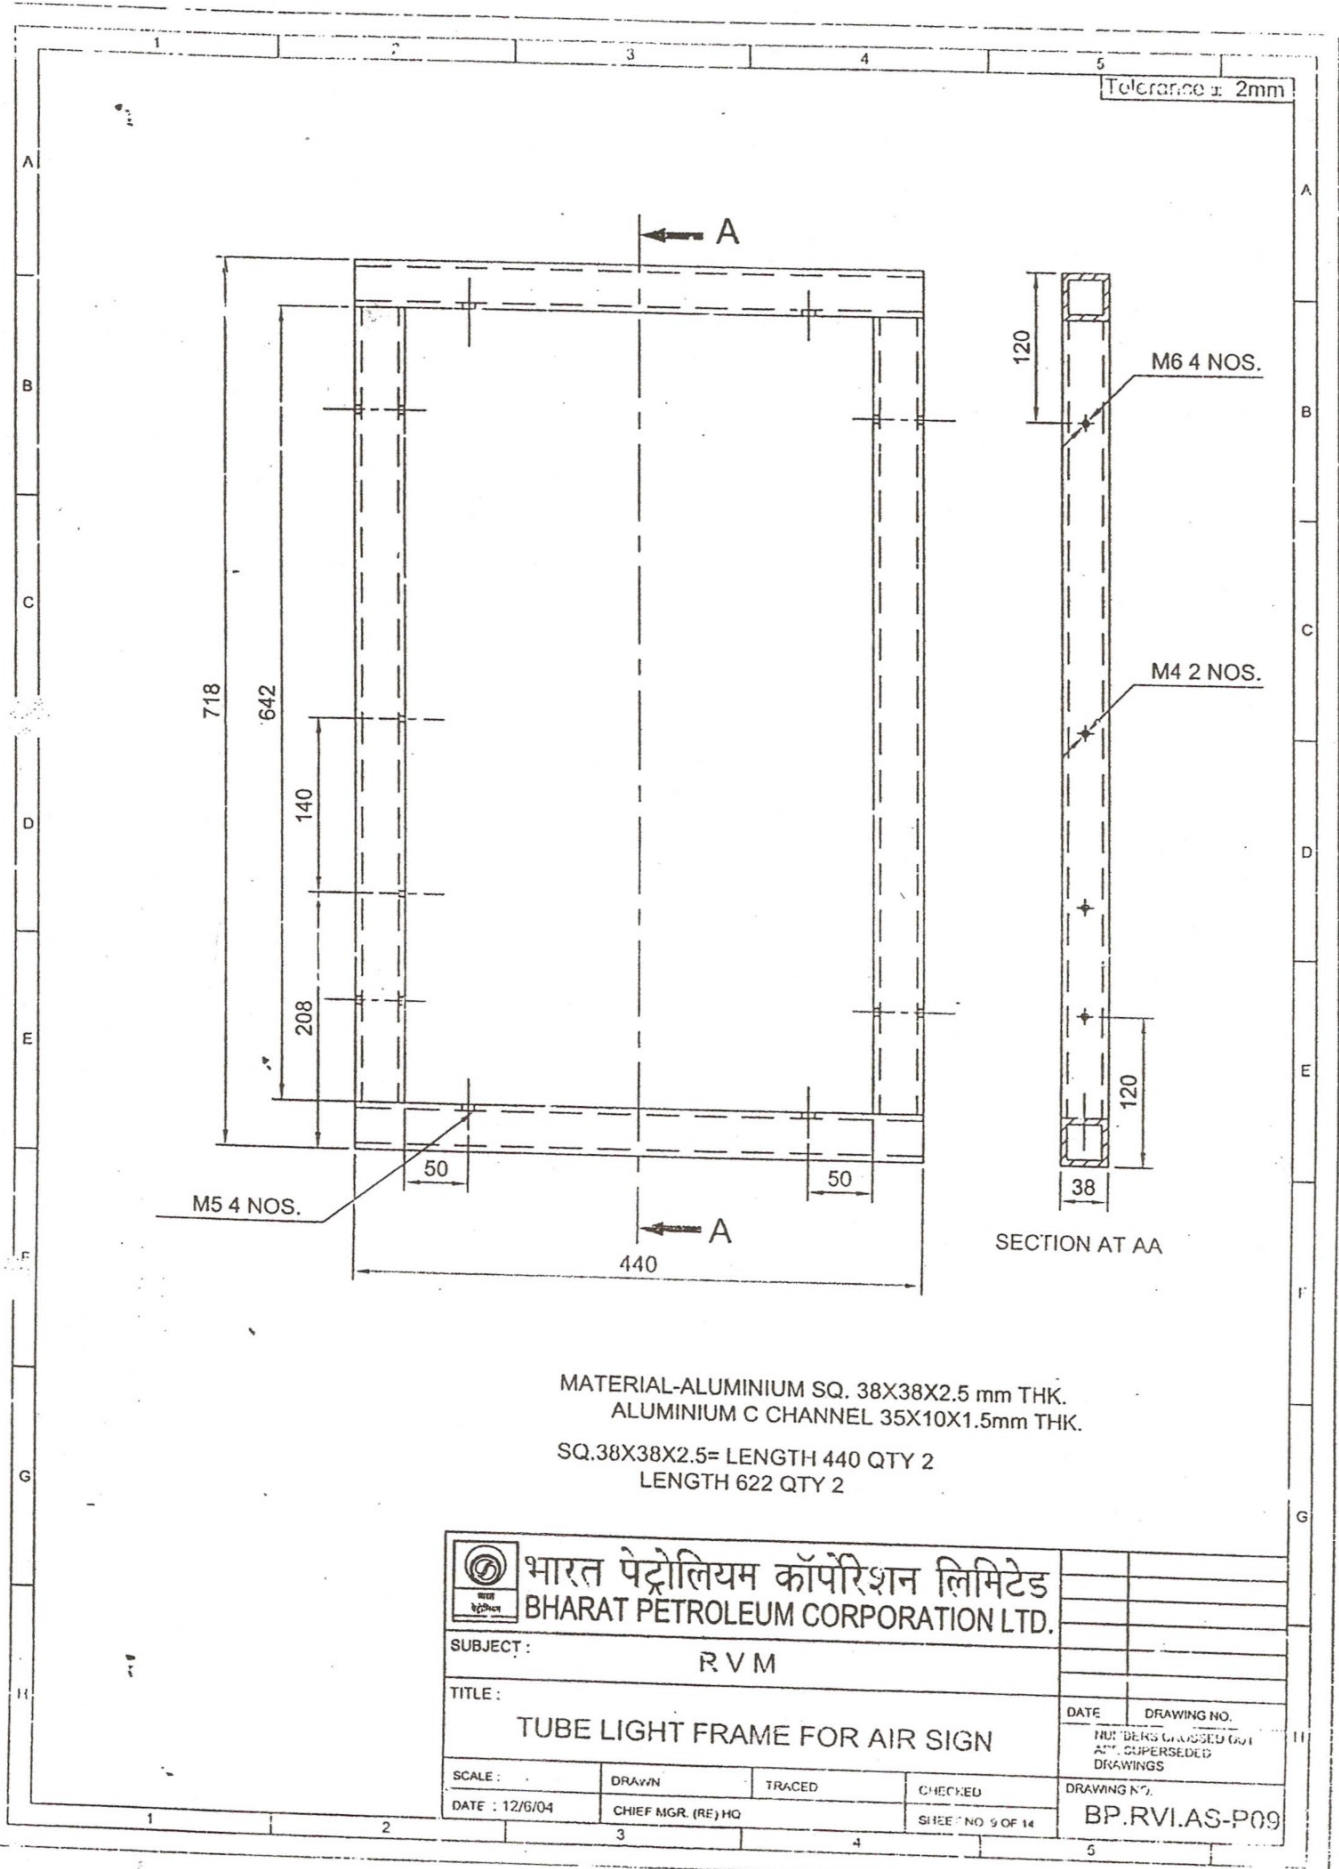

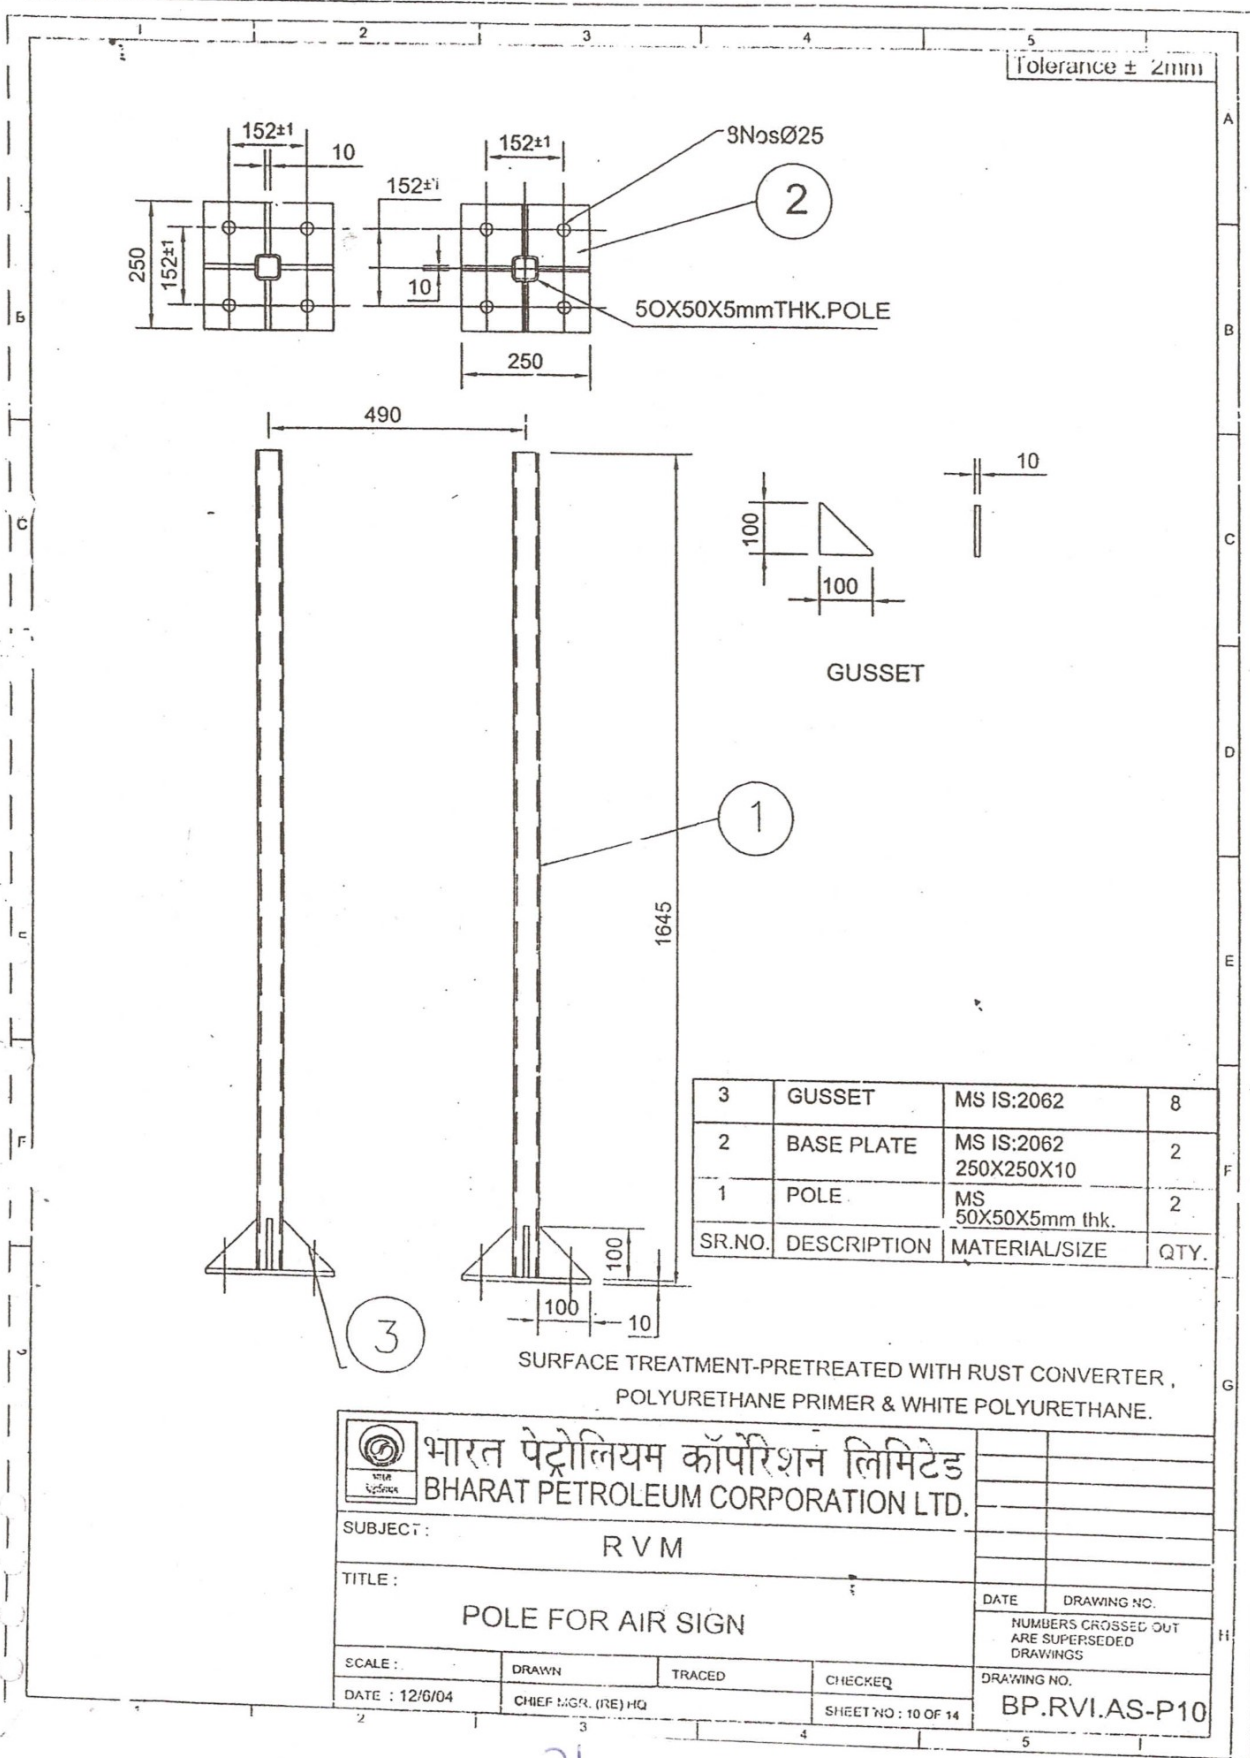


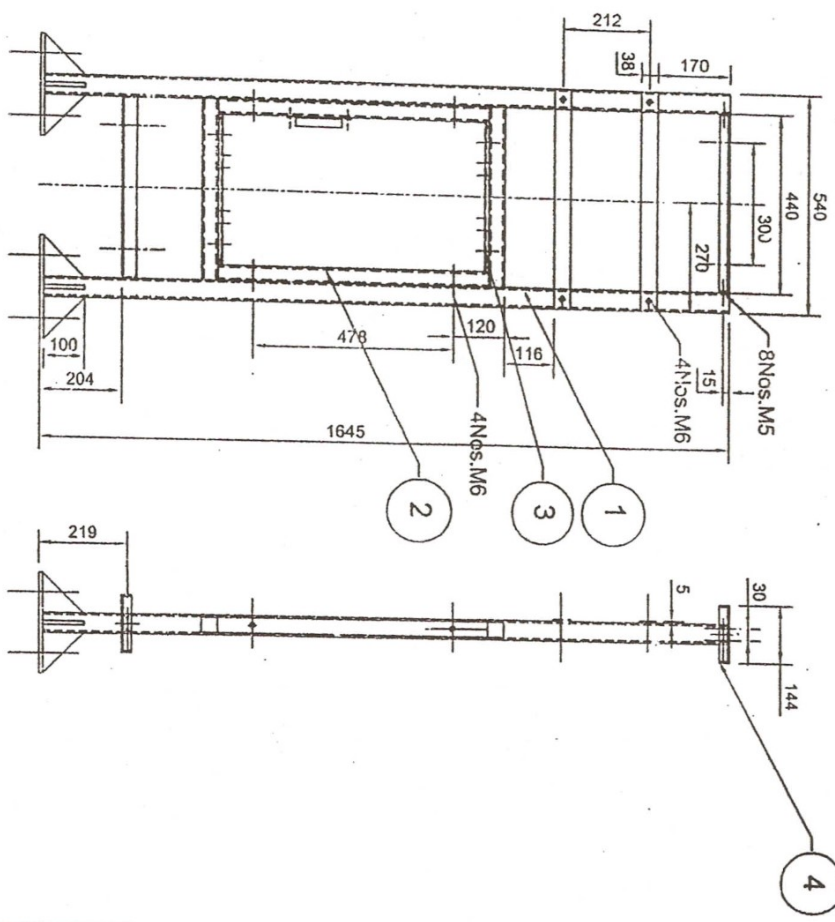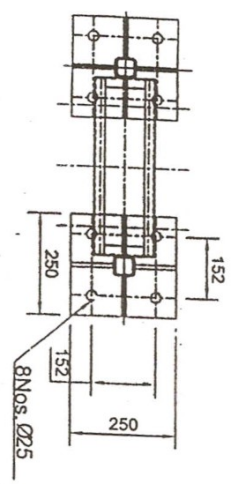

SR NO	DESCRIPTION	QTY.
4	SUPPORT FRAME	2
3	C CHANNEL	2
2	TUBE LIGHT FRAME	1
1	POLE ASSY	1

भारत पेट्रोलियम कॉर्पोरेशन लिमिटेड BHARAT PETROLEUM CORPORATION LTD.			
SUBJECT: R V M			
TITLE: STRUCTURE FOR AIR SIGN			
SCALE: 1:2500	DRAWN: CHIEF MGR. (P) NO	TRACED	CHECKED
DATE: 23/04	SHEET NO: 11 of 14	DRAWING NO: BP.RVI.AS-P.11	
D/P/E		DRAWN 3 NO.	
NUMBERS CROSS TO G.O.		DRAWING 1	

Tolerance $\pm 2\text{mm}$


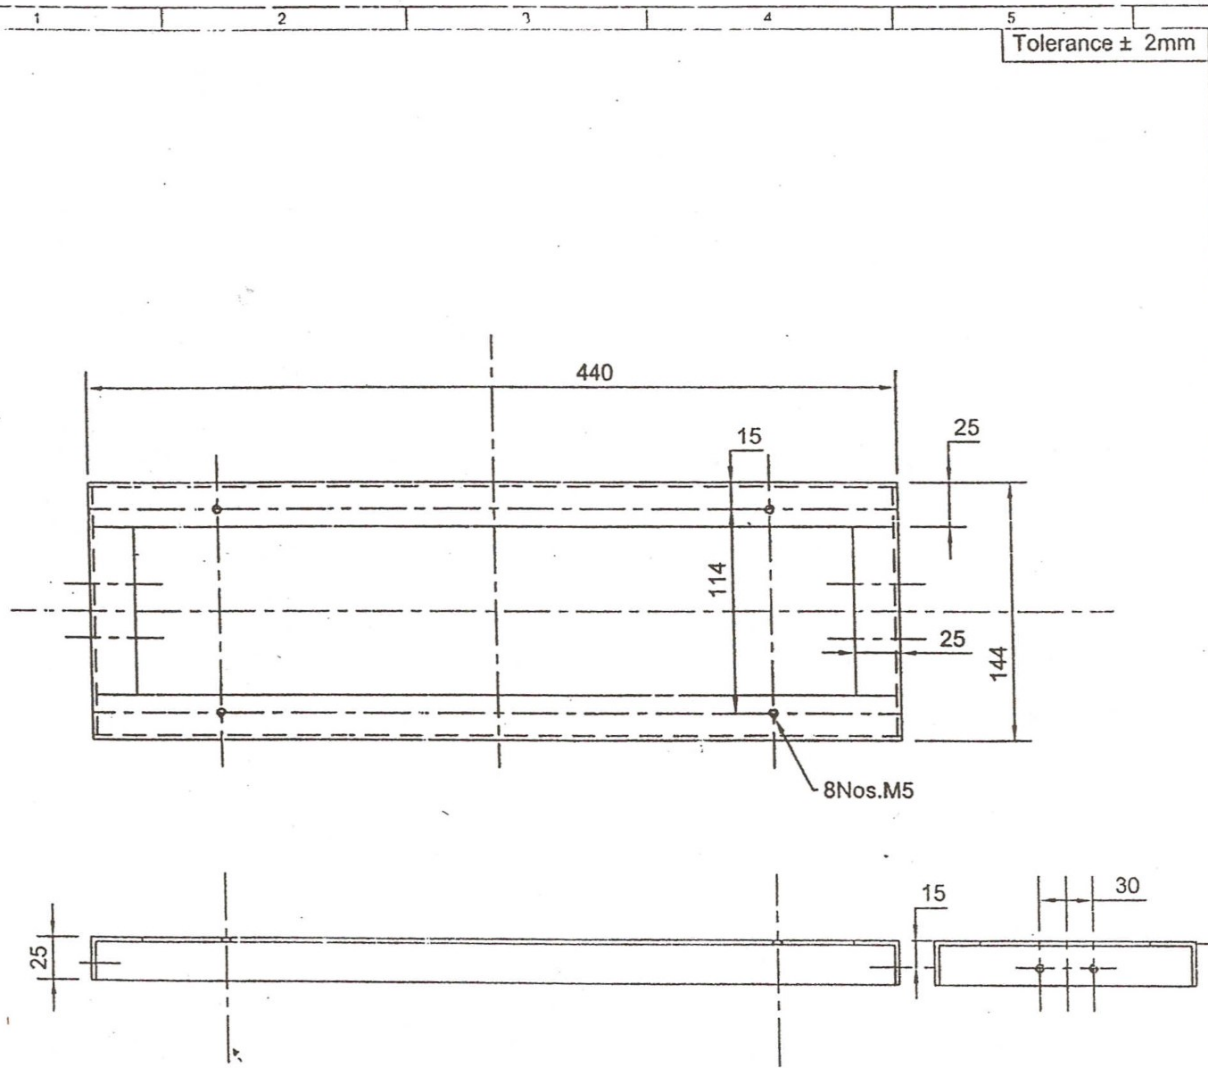


MATERIAL-HRCA STEEL 25X25X5mm thk.

SURFACE TREATMENT-PRETTREATED & PU WHITE PAINTED.40 MICRON.

 भारत पेट्रोलियम कॉर्पोरेशन लिमिटेड BHARAT PETROLEUM CORPORATION LTD.					
SUBJECT: R V M					
TITLE: SUPPORT FRAME FOR AIR SIGN				DATE	DRAWING NO.
				NUMBERS CROSSED OUT ARE SUPPRESSED DRAWINGS	
SCALE:	DRAWN	TRACED	CHECKED	DRAWING NO.	
DATE : 12/6/04	CHIEF MGR. (RE) HQ		SHEET NO : 12 OF 14	BP.RVI.AS-P12	

Tolerance $\pm$ 2mm

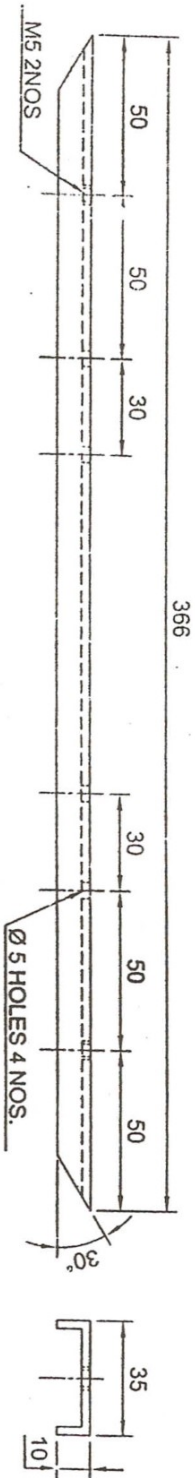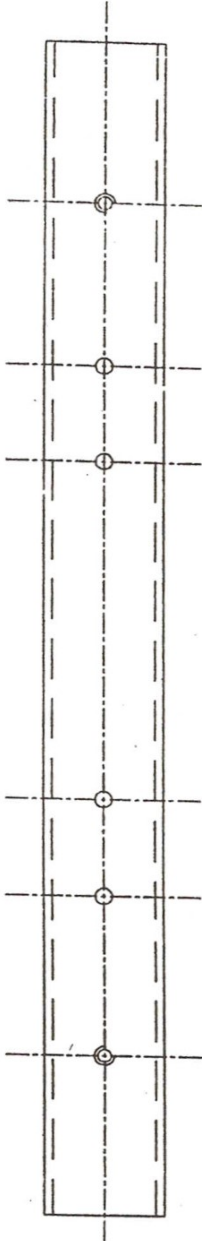

MATERIAL-ALUMINIUM 1.2mm THK.IS:737.
SURFACE TREATMENT - CHROMATE TREATED.
QTY.-2 NOS.

भारत पेट्रोलियम कॉर्पोरेशन लिमिटेड
BHARAT PETROLEUM CORPORATION LTD.


R V M

TITLE : C CHANNEL FOR TUBE LIGHT FRAME
(AIR)


SCALE : 1:2/04
DATE : 12/04
CHIEF MGR. (RE) NO
TRACED
CHECKED
SHEET NO : 13 of 14

DATE :
DRAWING NO.
NUMBERS CROSSED OUT
ARE SUPERSEDED
DRAWINGS
BP.RVI.AS-P13

Tolerance $\pm$ 2mm

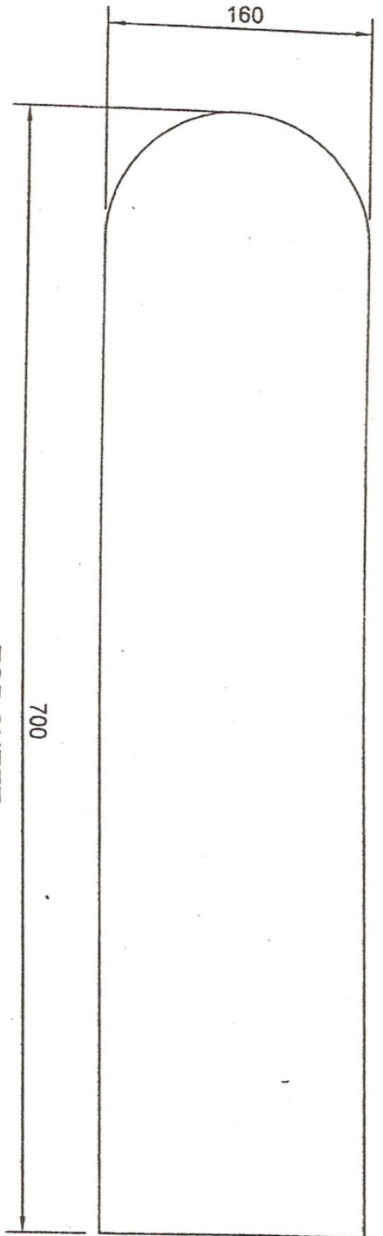


TOP SHEET

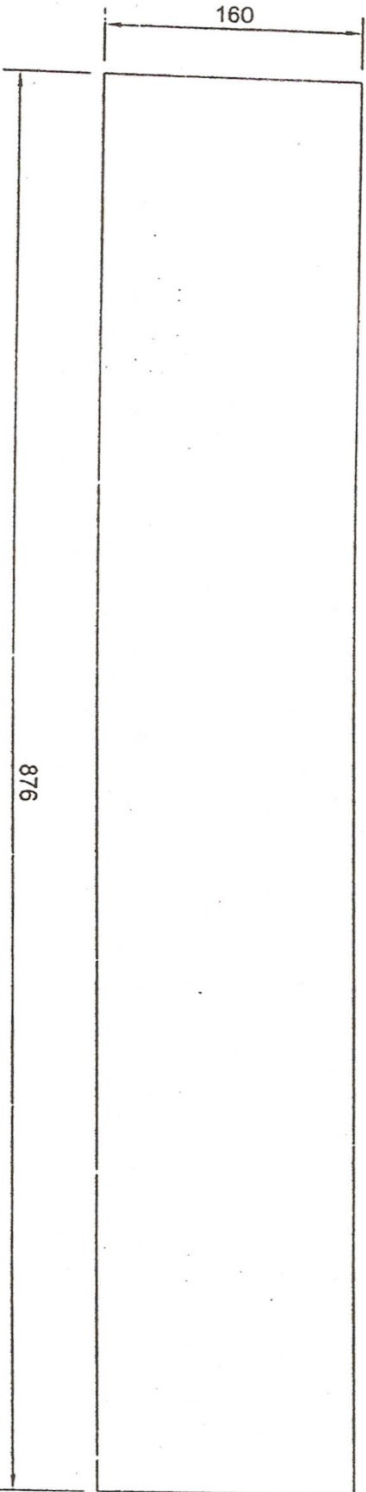

BOTTOM SHEET

MATERIAL-ALUMINIUM SHEET 2mm THK.IS:737.
SURFACE TREATMENT-CHROMATE TREATED & PU
WHITE PAINTED.40 micron.

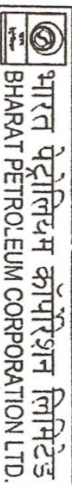

भारत पेट्रोलियम कॉर्पोरेशन लिमिटेड
BHARAT PETROLEUM CORPORATION LTD.

SUBJECT:

R V M

TITLE:

TOP & BOTTOM SHEET

SCALE:	DRAWN	TRACED	CHECKED
DATE: 12/5/24	CHEK MGR. (P/EN) 3		SHEET NO. 14 OF 14

DRAWING NO.
BP.RV.AS-P14

DATE
NUMBERS CHECKED
ARE SUBMITTED
D.V.M.V.S

Product Data sheet for Air sign

- 1) Pole as per drg. No. BP-RVI-AS-P10 is provided for mounting the sign. They are PU painted white. Support as per drg. No. BP-RVI-AS-P11 is provided.
- 2) Body as per drg. No. BP-RVI-AS-P03, P04 are screwed to the pole on one side. Other side of body (curved end) is stud welded & FRP cladding painted in BPCL Blue is fixed to that.
- 3) Top cut out in front side is done at site as per requirement for fixing meter. MS flat of 38*5mm (2 nos.) are provided for meter fixing as shown in drawing BP-RVI-AS-A02.
- 4) Display panel as per drawing no. BP-RVI-AS-P05 is screwed to 4 nos. angles which are stud welded & fixed in bottom cutout of main body. This display panel has engraved letters. An opal PET-G sheet of 3mm is fixed with VHB tape from back side.
- 5) A tube light frame as per drawing no. BP-RVI-AS-P08, P09 is screwed to pole directly as shown in drawing no. BP-RVI-AS-A02.
- 6) A top cover & bottom cover is provided.

Material Data sheet for Air sign :

Description	Material
1) Body LH/RH	Aluminium 2mm thk. Precoated with white paint/powder coated with PP powder.
2) Display panel fixed & hinged	Al. 2mm thk BPCL blue powder coated
3) Display panel for meter	Al. 2mm thk BPCL blue powder coated
4) Z channel	Aluminium sheet 1.2mm thk. as per IS : 737. PU white painted
5) Side cover	FRP 3mm thk. Painted in BPCL Blue
6) Pole assy.	50*50*5mm thk. MS PU white painted
7) Tube frame assy.	Aluminium extrusion 38*38*2.5 mm thk.
8) Electronic ballast	36/40w
9) Tube light	20w
10) VHB tape	1.1mm thk

Check points:

- 1) No damage/dent.
- 2) No light leakage.

Packing:

- Each unit is wrapped in polythene & packed in wooden crate.

DRAWING LIST FOR NO SIGN

SL.NO	PART NAME	PART NO.
1	NO SIGN	BP-RVI-NS-A01
2	DISPLAY PANEL	BP-RVI-NS-P02