



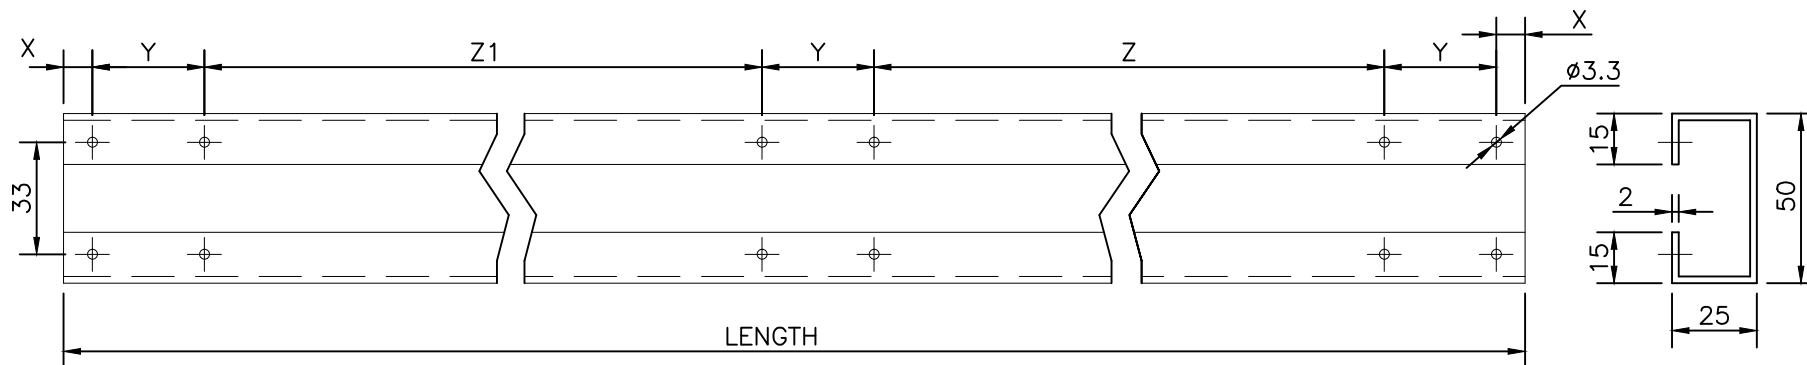

C CHANNEL CROSS SECTION

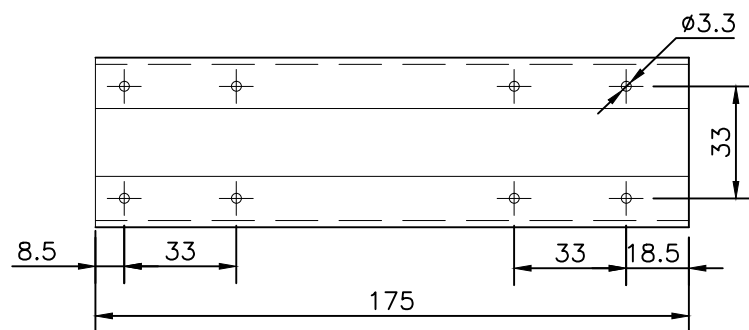

C CHANNEL LENGTH 175

MATERIAL—G.I. SHEET 2mm thk.IS:277.

L -1)FRAME LENGTH IS 1440mm for 6m MODULE.

L -1)FRAME LENGTH IS 1690mm for 7m MODULE.

L -2)FRAME LENGTH IS 1940mm for 8m MODULE.

7	575	18.5	33	---	---
6	525	18.5	33	---	---
5	425	18.5	33	---	---
4	315	18.5	33	---	---
3	275	18.5	33	---	---
2	700	8.5	33	617	---
1	(L)1690	8.5	33	787	787
SR NO	CHANNEL LENGTH	X	Y	Z	Z1



BHARAT PETROLEUM CORPORATION LTD.

TITLE :

CHANNELS FOR FASCIA STRUCTURE

A RETRO 24/5/18
REVISIONS

SCALE :
DATE : 12/6/04

DRAWN:
GM.RE

CHECKED

SHEET NO.
17 OF 19

DRAWING NO :
BP.RVI.CF-P17