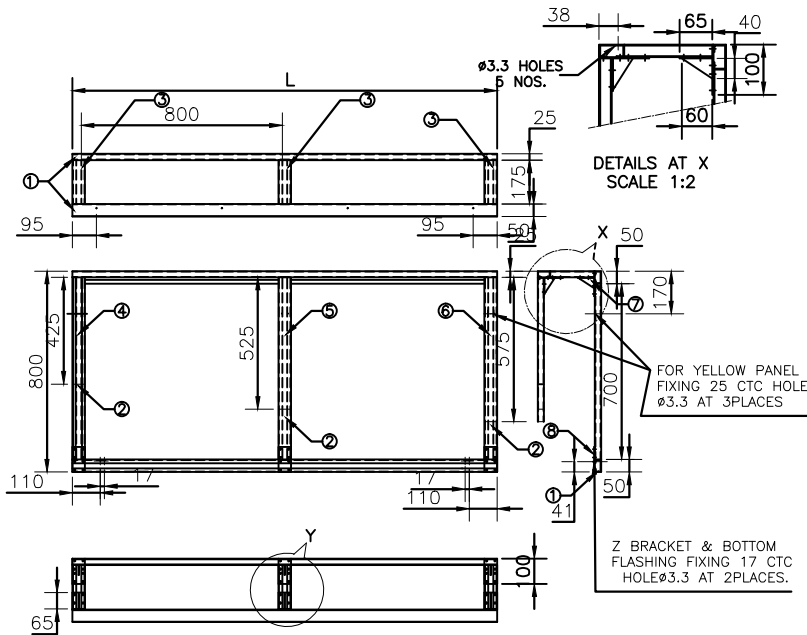




8	SUPPORT PLATE	3
7	GUSSET	6
6	C CHANNEL 575lg.	1
5	C CHANNEL 525lg.	1
4	C CHANNEL 425lg.	1
3	C CHANNEL 175lg.	3
2	C CHANNEL 700lg.	3
1	C CHANNEL 1690lg.	3
1	C CHANNEL 1690lg.(7m MODULE)	3
SR NO	DESCRIPTION	QTY

FRAME LH1

NOTE:- RIVETED & CO2 WELDED AT ALL JOINTS

L-FRAME LENGTH IS 1440mm for 6m MODULE.
VERTICAL CHANNEL IS SAME.

L -2)FRAME LENGTH IS 1940mm for 8m MODULE.

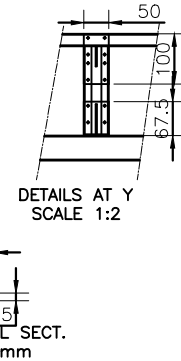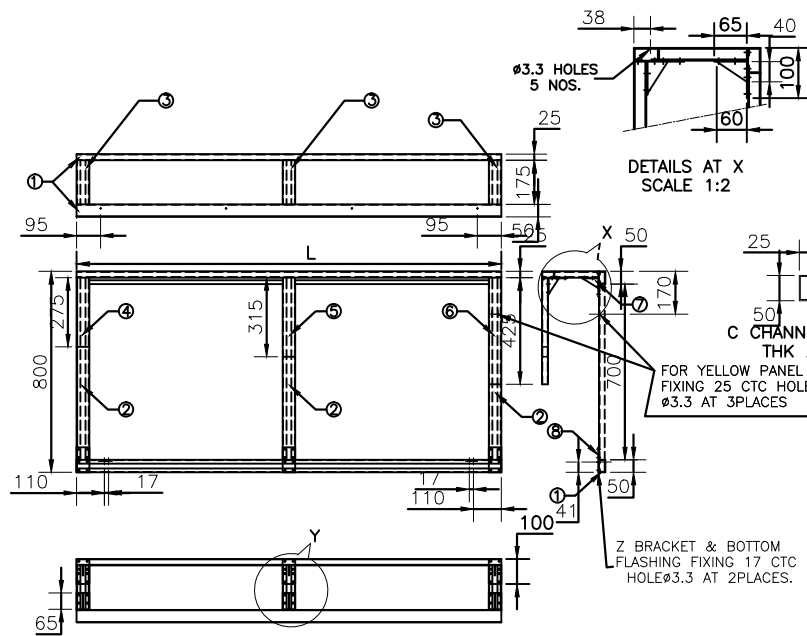

8	SUPPORT PLATE	3
7	GUSSET	6
6	C CHANNEL 425lg.	1
5	C CHANNEL 315lg.	1
4	C CHANNEL 275lg.	1
3	C CHANNEL 175lg.	3
2	C CHANNEL 700lg.	3
1	C CHANNEL 1690lg.(7m MODULE)	3
SR NO	DESCRIPTION	QTY

FRAME LH2

MS SQ.25X2MM Thk. PIPE
WELDED STRUCTURE
OR MS C CHANNEL
WELDED STRUCTURE



BHARAT PETROLEUM CORPORATION LTD.

TITLE :

FRAME LH

DATE DRAWING NO.

NUMBERS CROSSED OUT ARE
SUPERSEDED DRAWINGS

DRAWING NO :
BP.RVI.CF-P03

A	RETRO 24/5/18
REVISIONS	
7	

SCALE : 1:15
DATE : 12/6/04

DRAWN:
GM.RE

CHECKED

SHEET NO.
3 of 19