


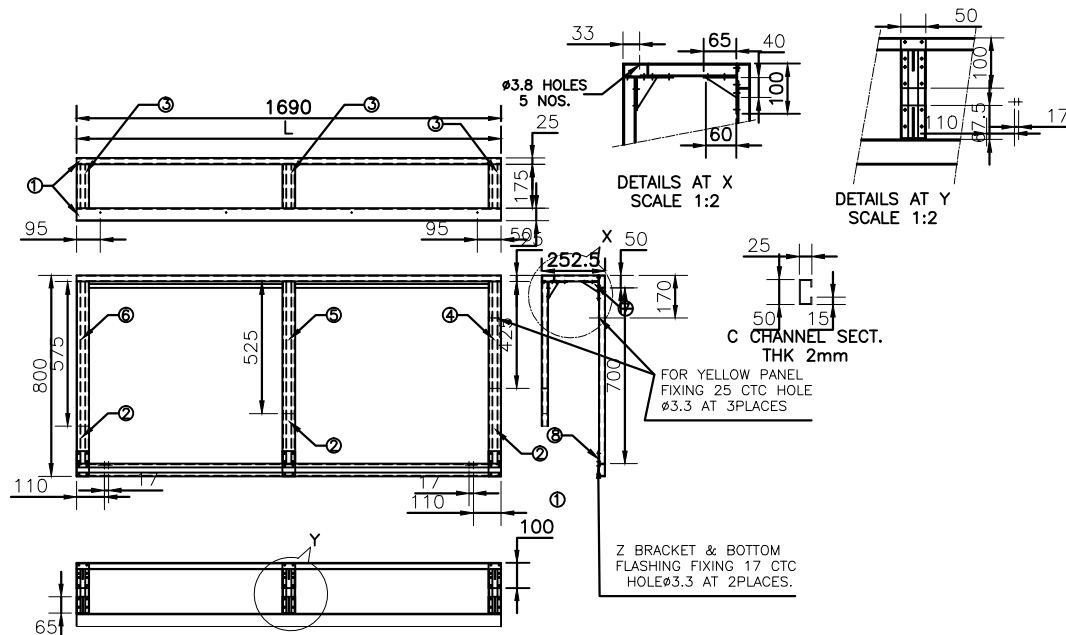


8	SUPPORT PLATE	3
7	GUSSET	6
6	C CHANNEL 575lg.	1
5	C CHANNEL 525lg.	1
4	C CHANNEL 425lg.	1
3	C CHANNEL 175lg.	3
2	C CHANNEL 700lg.	3
1	C CHANNEL 1690lg.(7m MODULE)	3
SR NO	DESCRIPTION	QTY

FRAME RH1

NOTE:- RIVETED & CO2 WELDED AT ALL JOINTS

L -1)FRAME LENGTH IS 1440mm for 6m MODULE.
VERTICAL CHANNEL IS SAME.

L -2)FRAME LENGTH IS 1940mm for 8m MODULE.

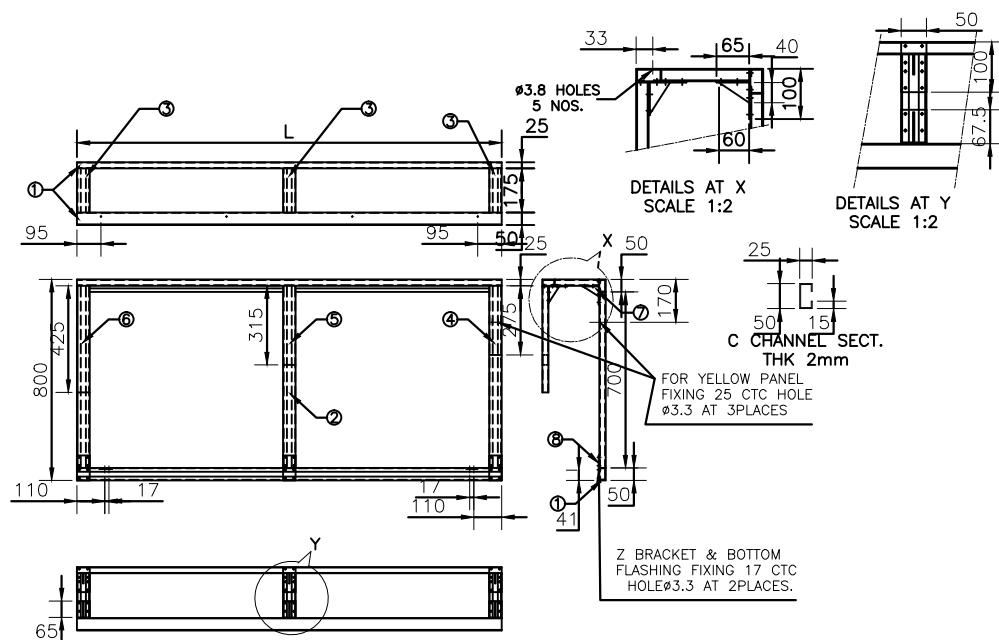

8	SUPPORT PLATE	3
7	GUSSET	6
6	C CHANNEL 425lg.	1
5	C CHANNEL 315lg.	1
4	C CHANNEL 275lg.	1
3	C CHANNEL 175lg.	3
2	C CHANNEL 700lg.	3
1	C CHANNEL 1690lg.(7m MODULE)	3
SR NO	DESCRIPTION	QTY

FRAME RH2

MS SQ.25X2MM Thk. PIPE
WELDED STRUCTURE
OR MS C CHANNEL
WELDED STRUCTURE

 BHARAT PETROLEUM CORPORATION LTD.					
TITLE : FRAME RH		DATE	DRAWING NO.		
		NUMBERS CROSSED OUT ARE SUPERSEDED DRAWINGS			
REVISIONS <table border="1"> <tr> <td>A</td> <td>RETRO 24/5/18</td> </tr> </table>	A	RETRO 24/5/18	SCALE : 1:15 DATE : 12/6/04	DRAWN: GM.RE	CHECKED
A	RETRO 24/5/18				
SHEET NO. 4 of 19		DRAWING NO : BP.RVI.CF-P04			