


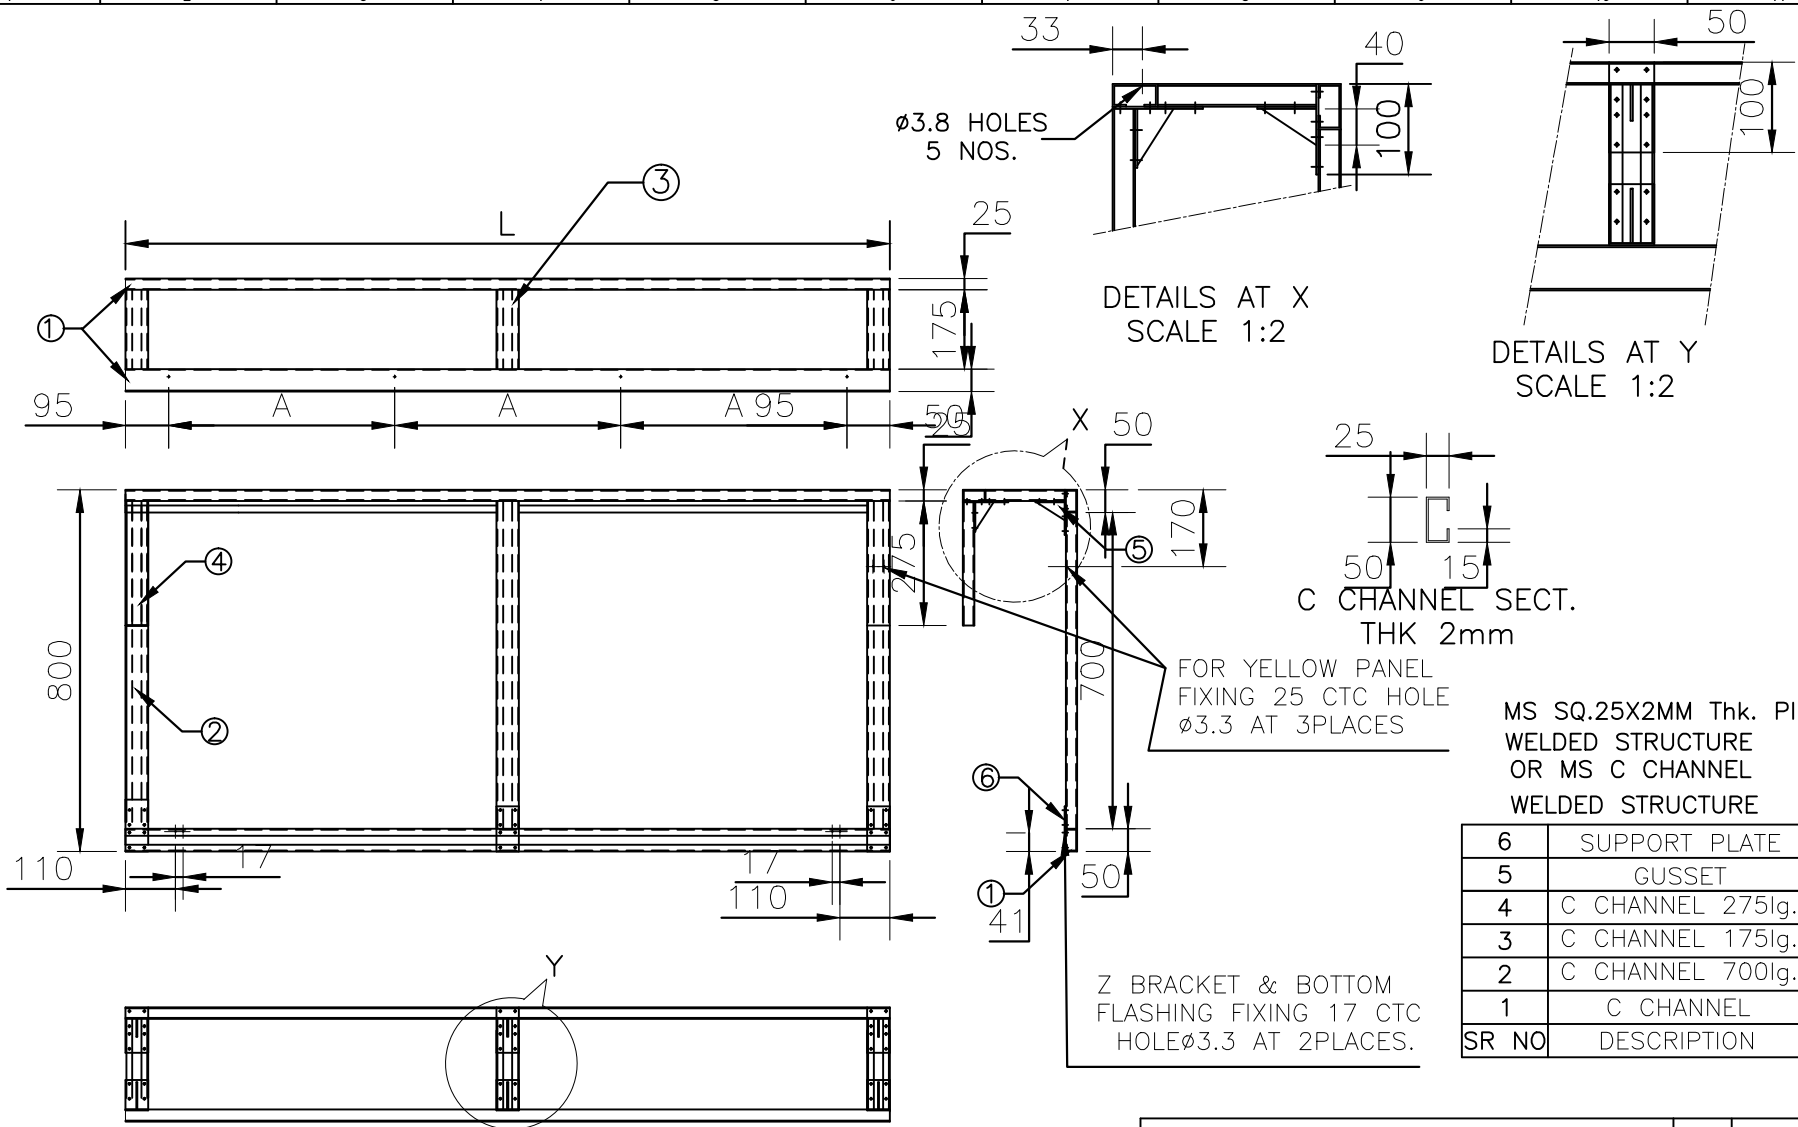

L=LENGTH TO SUIT SITE CONDITION.
A=TO SUIT ACM FIXING

NOTE:- RIVETED & CO2 WELDED AT ALL JOINTS

MS SQ.25X2MM Thk. PIPE
WELDED STRUCTURE
OR MS C CHANNEL
WELDED STRUCTURE

6	SUPPORT PLATE	3
5	GUSSET	6
4	C CHANNEL 275lg.	3
3	C CHANNEL 175lg.	3
2	C CHANNEL 700lg.	3
1	C CHANNEL	3
SR NO	DESCRIPTION	QTY



BHARAT PETROLEUM CORPORATION LTD.

TITLE :

FRAME STRAIGHT CORNER PIECE

A RETRO 24/5/18	SCALE :	DRAWN:	CHECKED	SHEET NO.
REVISIONS	DATE : 12/6/04	GM.RE		7 of 19

DRAWING NO :
BP.RVI.CF-P07